

ARAPAHOE COUNTY DETENTION FACILITY
ADDITION AND REMODEL
7375 S. POTOMAC ST.
CENTENNIAL, CO 80112

SHEET NUMBER	DESCRIPTION
SE000	COVER SHEET
SE001	SYMBOLS LEGEND
SE100	SECURITY SITE PLAN
SE101	SECURITY FLOOR PLAN - KITCHEN, LAUNDRY
SE102	SECURITY FLOOR PLAN - MENTAL HEALTH
SE201	FUNCTIONAL DIAGRAM - FIBER RISER
SE202	FUNCTIONAL DIAGRAM - NETWORK RISER
SE203	FUNCTIONAL DIAGRAM - PLC, HMI, INTERCOM, CCTV
SE301	WIRING DETAILS - INTERCOM AND PAGING, CCTV
SE302	WIRING DETAILS - LOCKS, UTILITY
SE303	WIRING DETAILS - MISCELLANEOUS DEVICES
SE401	RACK LAYOUTS - KITCHEN, LAUNDRY (RM. M102)
SE402	RACK LAYOUTS - MENTAL HEALTH (RM. 175)

REVISION	DATE	DESCRIPTION	REVISION	DATE	DESCRIPTION	REVISION	DATE	DESCRIPTION
0	10 / 25 / 2023	SUBMITTAL	7	12 / 17 / 2024	ADDED LOCAL KEYSWITCHES: SLIDERS 100,138,140,150,122A,122B, 150A AND KICK RELEASE DOORS 106-112,115-119,123,125,130-131	X	XX / XX / XXXX	XXXXXX
1	12 / 05 / 2023	RESUBMITTAL	8	01 / 17 / 2025	RFI #297 (CARD READER 175S DELETED)			
2	05 / 14 / 2024	ASI #08 UPDATES	9	04 / 04 / 2025	RFI #316 (ADDED DOOR 174 CONTROL & INTERCOM)			
3	06 / 12 / 2024	RFI #202 UPDATES	10	06 / 15 / 2025	ADDED CAMERAS N166 AND N167			
4	07 / 02 / 2024	ASI #08-R1 UPDATES	11	08 / 25 / 2025	DESIGN CHANGES PER RFI 367			
5	08 / 26 / 2024	ASI #08-R2 UPDATES						
6	11 / 04 / 2024	RFI #259 UPDATES						

[redacted]

PROJECT
ARAPAHOE COUNTY DETENTION CENTER
ADDITION AND REMODEL
7375 S. POTOMAC ST.
CENTENNIAL, CO 80112

SHEET NAME
COVER SHEET

SHEET NUMBER
SE000

REVISION
11

SECURITY ELECTRONICS SYSTEM - SYMBOLS LEGEND

SYMBOL	DESCRIPTION	BACK BOX	MOUNTING HEIGHT	CABLE TYPE
	ELECTRICALLY CONTROLLED AND MONITORED DOOR (G) = GATE CONTROL (OPEN, STOP, CLOSE) (S) = FULL FUNCTION SLIDER (OPEN, STOP, CLOSE) (KS) = KEYSWITCH 7	N/A	AS REQUIRED	B (ALL DOOR/GATES) + D (W/KEYSWITCH) 7
	MONITORED ONLY DOOR	N/A	AS REQUIRED	C
S	PAGING SPEAKER	CUSTOM	CEILING	E (1 HOMERUN PER ZONE - SEE PLAN)
H	PAGING HORN	SINGLE GANG	12' 0" AFF	E (1 HOMERUN PER ZONE - SEE PLAN)
IC	INTERCOM STATION (P)=PEDESTAL MOUNTED - DUAL HEIGHT 5 (F)=FRAME MOUNTED	DOUBLE GANG	48" TO CENTER	D
	FIXED CAMERA (P)=PEDESTAL MOUNTED - DUAL HEIGHT	REFER TO SCHEDULE (TYPICALLY SINGLE GANG)	REFER TO SCHEDULE	A (ALL CAMERAS) H + B (PEDESTAL CAM VIDEO, AND CAM/ CONVERTER PWR) 6
P	PANIC PUSHBUTTON	SINGLE GANG	48" TO CENTER	C
IL	DOOR INTERLOCK GROUP	N/A	N/A	N/A
CR	CARD READER (BY OTHERS)	N/A- (BY OTHERS)	N/A- (BY OTHERS)	N/A- (BY OTHERS)
	REQUEST-TO-EXIT (REX) PUSHBUTTON	SINGLE GANG	48" TO CENTER	C
REX	REQUEST-TO-EXIT (REX) OVERHEAD MOTION DEVICE (BY OTHERS) *IF DOOR HARDWARE ALLOWS, CONNECT TO REX OUTPUT FROM HARDWARE IN LIEU OF OVERHEAD MOTION DEVICE	N/A	ABOVE DOOR	G

SYMBOL	DESCRIPTION	BACK BOX	MOUNTING HEIGHT	CABLE TYPE
R	RECEPTACLE CONTROL (CONTROL/INDICATION WIRES TO DIV. 26 CONTACTOR PANEL)	N/A	N/A	G (FOR EACH CONTACTOR)

SECURITY ELECTRONICS SYSTEM - GENERAL NOTES

1. INSTALL ALL SYSTEMS IN ACCORDANCE WITH THE DESIGN DRAWINGS, SPECIFICATIONS, OR OTHER CONTRACT DOCUMENTS.
2. COORDINATE THE INSTALLATION OF SECURITY SYSTEMS WITH ALL OTHER BUILDING SYSTEMS AND TRADES, IF NEEDED.
3. DEVICE AND CONDUIT LAYOUT IS DIAGRAMMATIC. REFER TO ARCHITECTURAL PLANS FOR EXACT BUILDING DIMENSIONS AND CONFIGURATION.
4. SEPARATE CONDUITS SHALL BE PROVIDED FOR EACH SYSTEM TYPE. CLASS 1 AND 2 WIRING CIRCUITS SHALL BE KEPT SEPARATE.

SECURITY ELECTRONICS CABLE AND CONDUIT FILL SCHEDULE (WET LOCATION)



SECURITY ELECTRONICS CABLE AND CONDUIT FILL SCHEDULE (RISER)



REVISION	DATE	DESCRIPTION
0	10 / 25 / 2023	SUBMITTAL
1	12 / 05 / 2023	RESUBMITTAL
2	05 / 14 / 2024	ASI #08 UPDATES
3	06 / 12 / 2024	RFI #202 UPDATES
4	07 / 02 / 2024	ASI #08-R1 UPDATES
5	08 / 26 / 2024	ASI #08-R2 UPDATES
6	11 / 04 / 2024	RFI #259 UPDATES

REVISION	DATE	DESCRIPTION
7	12 / 17 / 2024	ADDED LOCAL KEYSWITCHES: SLIDERS 100,138,140,150,122A,122B, 150A AND KICK RELEASE DOORS 106-112,115-119,123,125,130-131
8	01 / 17 / 2025	RFI #297 (CARD READER 175S DELETED)
9	04 / 04 / 2025	RFI #316 (ADDED DOOR 174 CONTROL & INTERCOM)
10	06 / 15 / 2025	ADDED CAMERAS N166 AND N167
11	08 / 25 / 2025	DESIGN CHANGES PER RFI 367


REVISION	DATE	DESCRIPTION
X	XX / XX / XXXX	XXXXXX

PROJECT
ARAPAHOE COUNTY DETENTION CENTER
ADDITION AND REMODEL
7375 S. POTOMAC ST.
CENTENNIAL, CO 80112

SHEET NAME
SYMBOLS LEGEND

SHEET NUMBER
SE001

REVISION
11

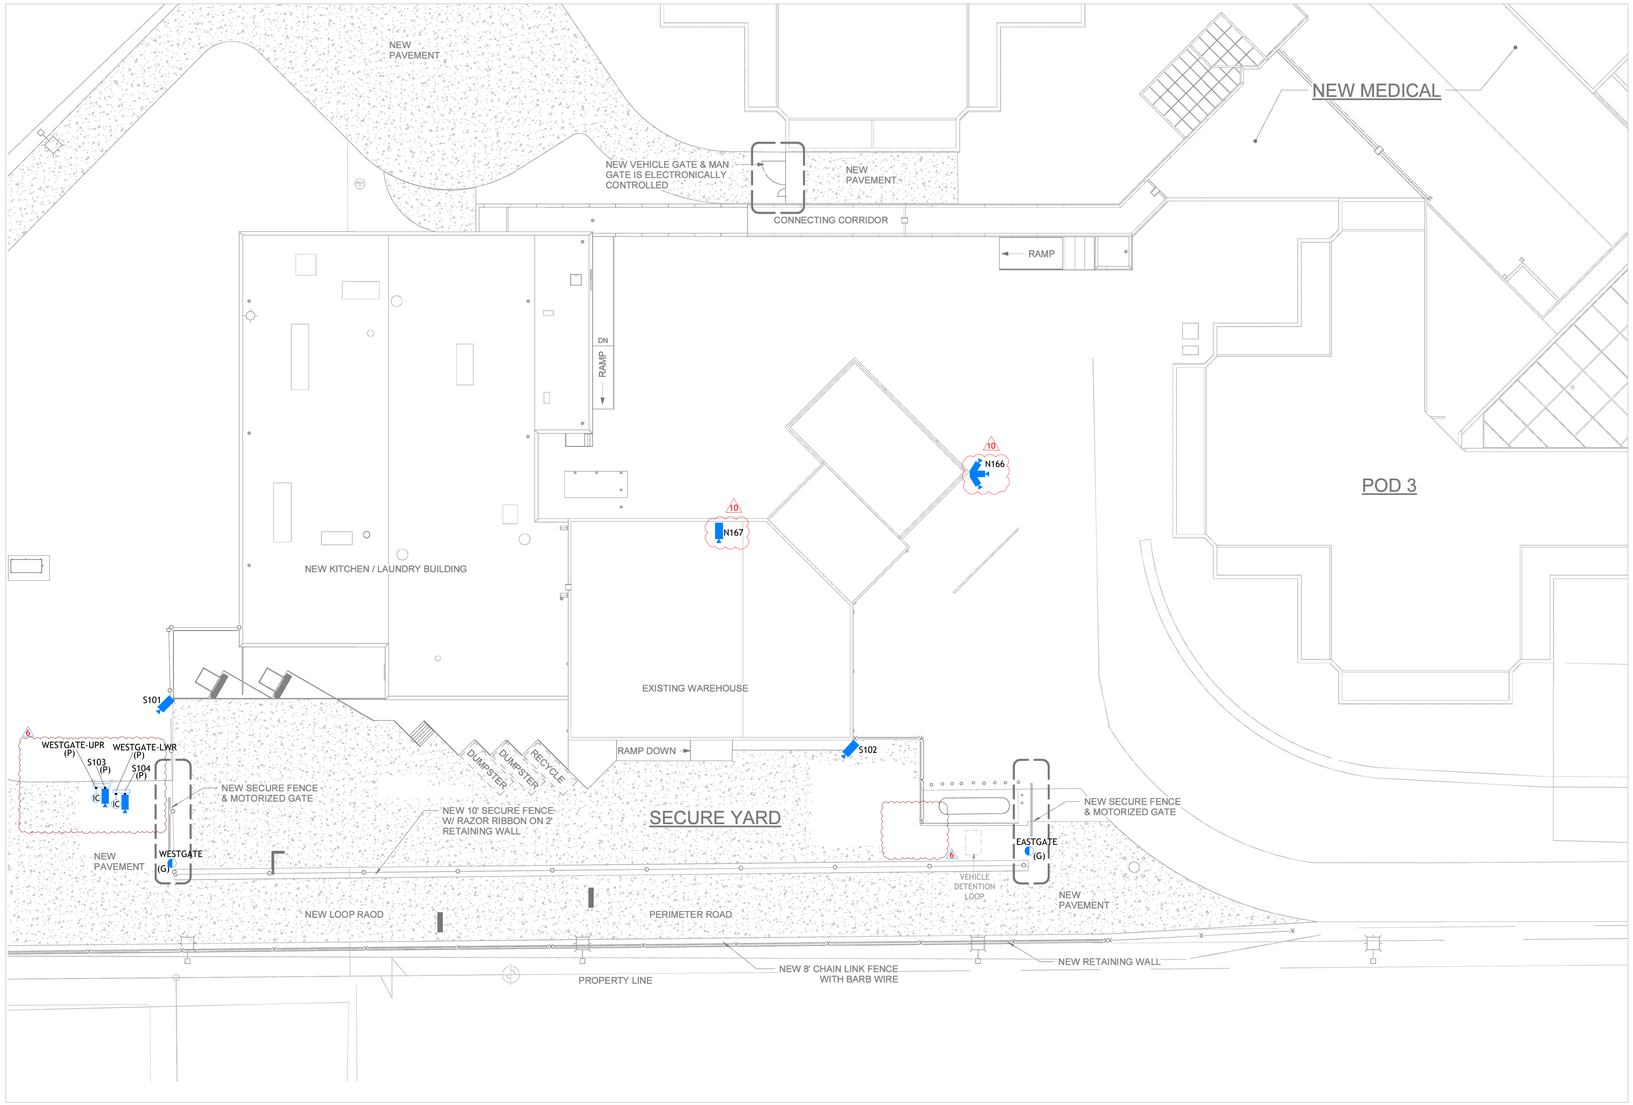

N

1 SECURITY SITE PLAN - GATE 1 / GATE 2

SCALE: 1/16" = 1'-0"

REVISION	DATE	DESCRIPTION	REVISION	DATE	DESCRIPTION	REVISION	DATE	DESCRIPTION
0	10 / 25 / 2023	SUBMITTAL	7	12 / 17 / 2024	ADDED LOCAL KEYSWITCHES: SLIDERS 100,138,140,150,122A,122B, 150A AND KICK RELEASE DOORS 106-112,115-119,123,125,130-131	X	XX / XX / XXXX	XXXXXX
1	12 / 05 / 2023	RESUBMITTAL	8	01 / 17 / 2025	RFI #297 (CARD READER 175S DELETED)			
2	05 / 14 / 2024	ASI #08 UPDATES	9	04 / 04 / 2025	RFI #316 (ADDED DOOR 174 CONTROL & INTERCOM)			
3	06 / 12 / 2024	RFI #202 UPDATES	10	06 / 15 / 2025	ADDED CAMERAS N166 AND N167			
4	07 / 02 / 2024	ASI #08-R1 UPDATES	11	08 / 25 / 2025	DESIGN CHANGES PER RFI 367			
5	08 / 26 / 2024	ASI #08-R2 UPDATES						
6	11 / 04 / 2024	RFI #259 UPDATES						

[redacted]

PROJECT

ARAPAHOE COUNTY DETENTION CENTER
ADDITION AND REMODEL
7375 S. POTOMAC ST.
CENTENNIAL, CO 80112

SHEET NAME


SECURITY SITE PLAN

SHEET NUMBER


SE100

REVISION


11

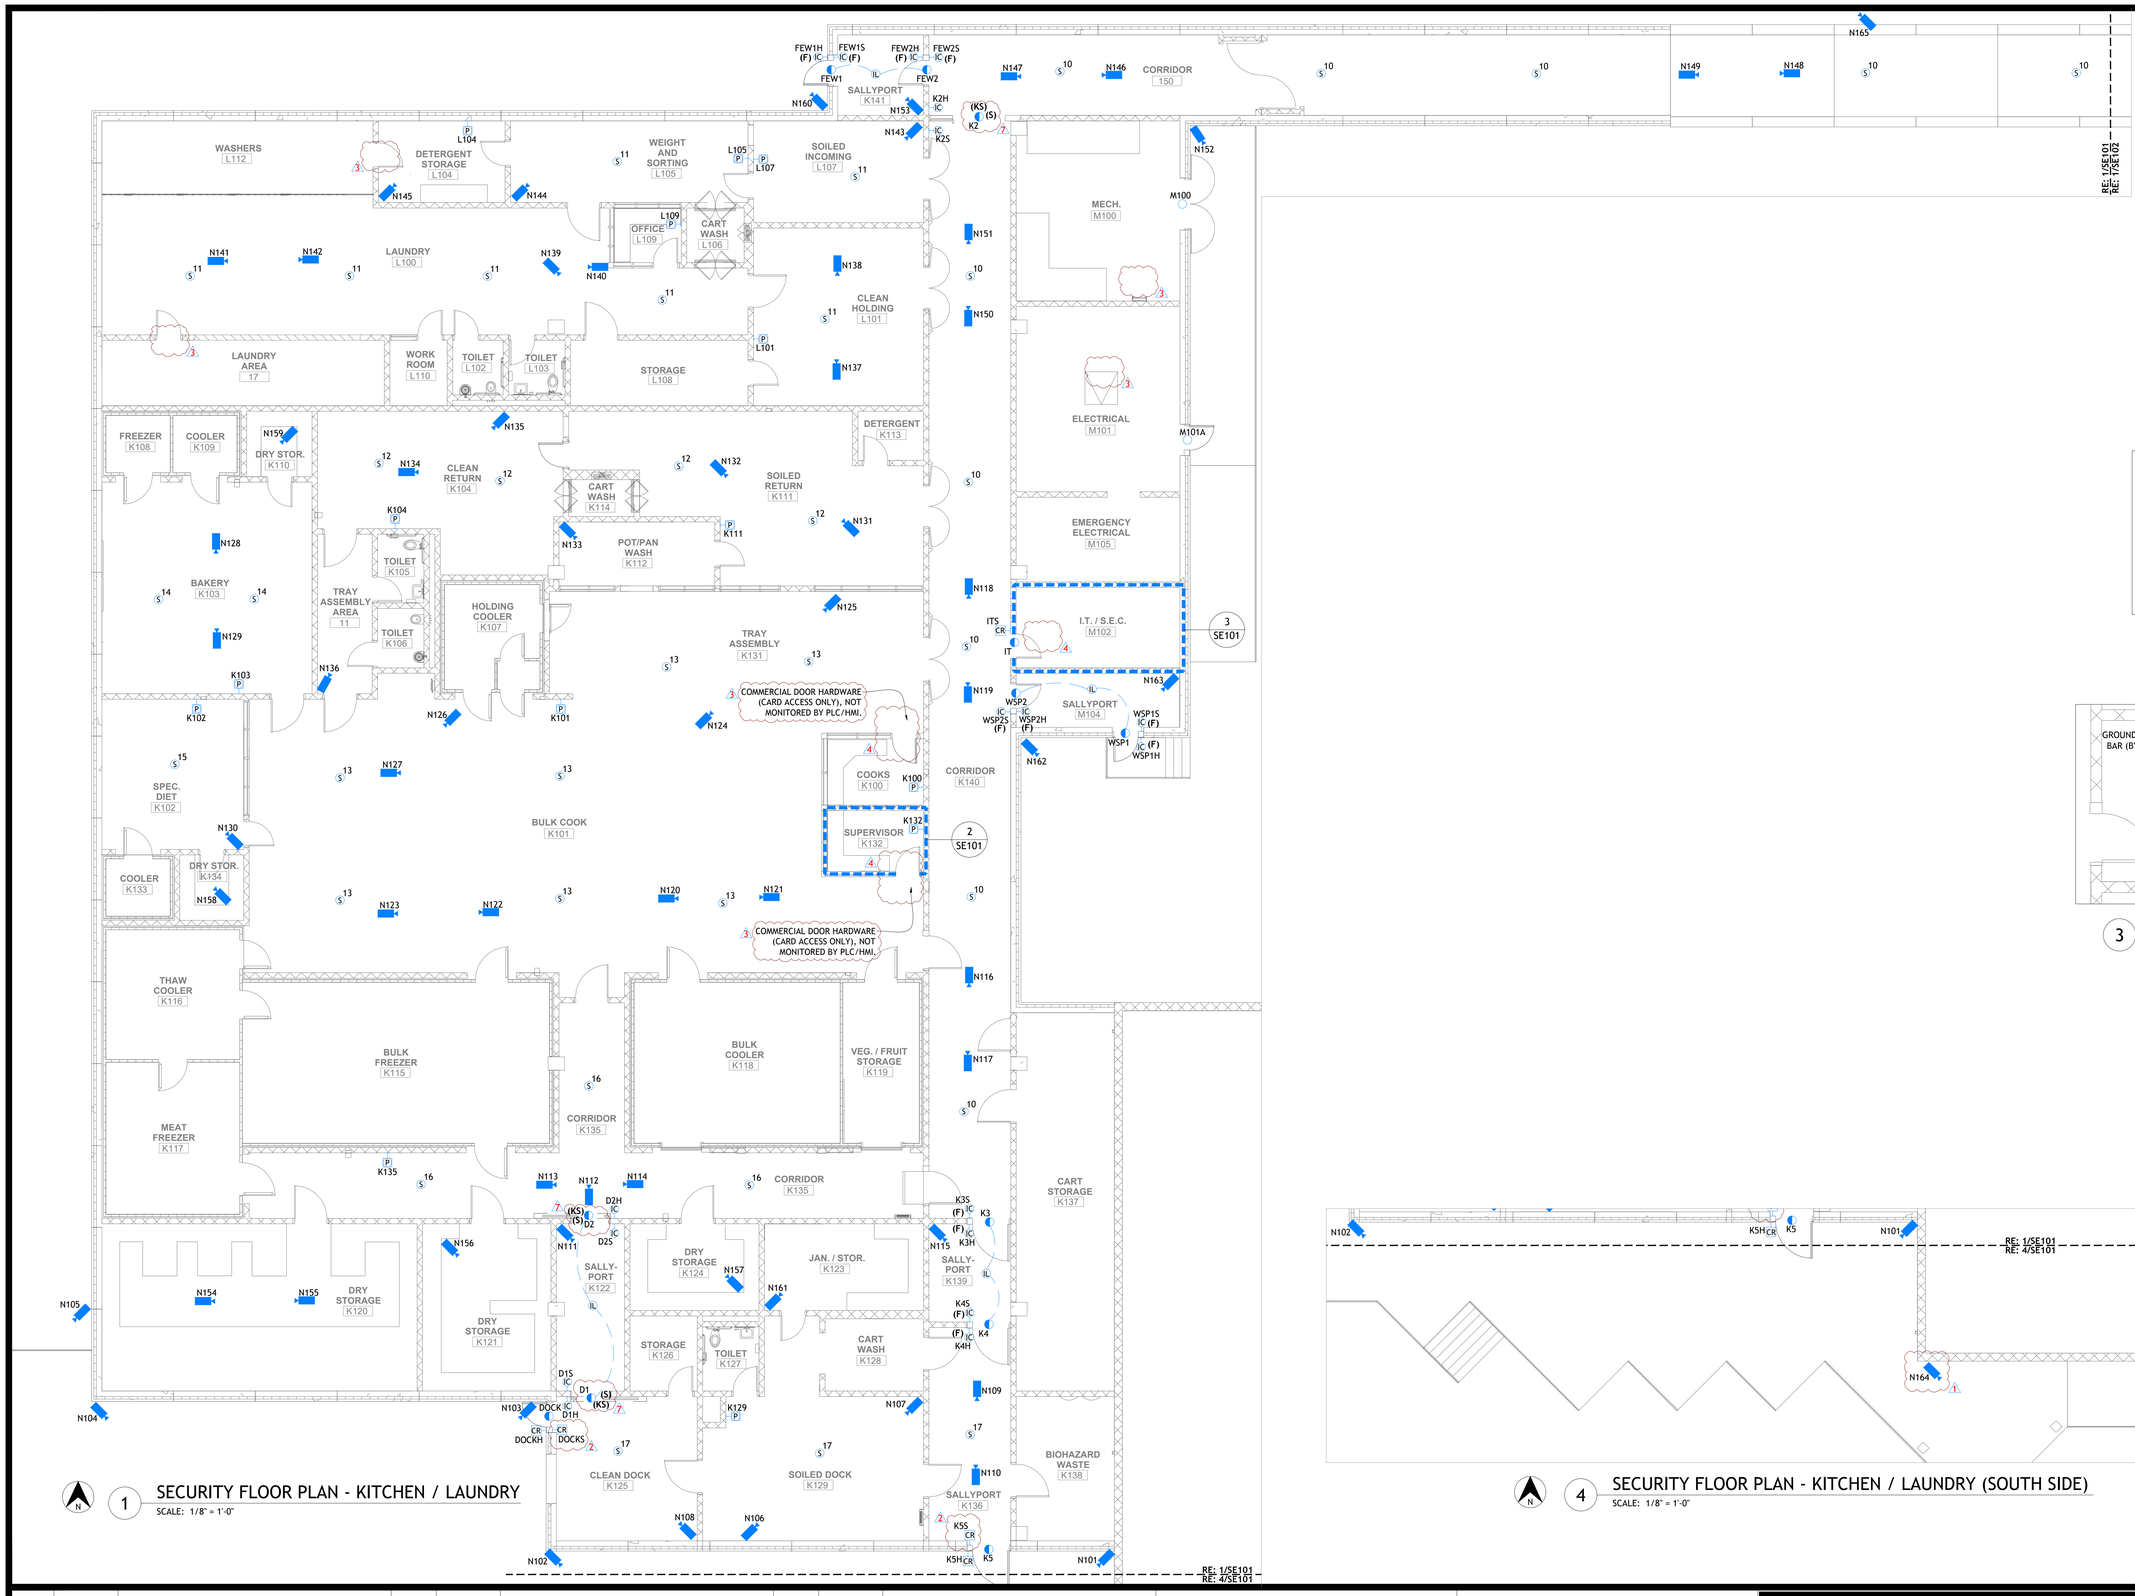


1 SECURITY FLOOR PLAN - KITCHEN / LAUNDRY
SCALE: 1/8" = 1'-0"

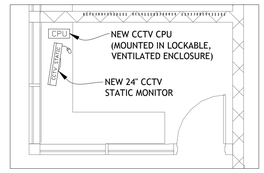

2 SUPERVISOR - RM. K132
SCALE: 1/4" = 1'-0"

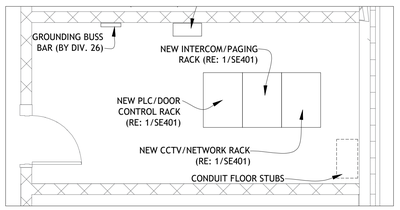

3 I.T. / S.E.C. EQUIPMENT - RM. M102
SCALE: 1/4" = 1'-0"

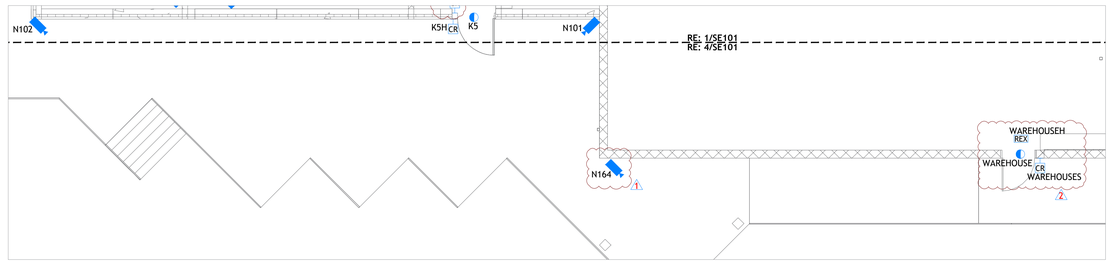

4 SECURITY FLOOR PLAN - KITCHEN / LAUNDRY (SOUTH SIDE)
SCALE: 1/8" = 1'-0"

REVISION	DATE	DESCRIPTION
0	10 / 25 / 2023	SUBMITTAL
1	12 / 05 / 2023	RESUBMITTAL
2	05 / 14 / 2024	ASI #08 UPDATES
3	06 / 12 / 2024	RFI #202 UPDATES
4	07 / 02 / 2024	ASI #08-R1 UPDATES
5	08 / 26 / 2024	ASI #08-R2 UPDATES
6	11 / 04 / 2024	RFI #259 UPDATES
7	12 / 17 / 2024	ADDED LOCAL KEYSWITCHES: SLIDERS 100,138,140,150,122A,122B, 150A AND KICK RELEASE DOORS 106-112,115-119,123,125,130-131
8	01 / 17 / 2025	RFI #297 (CARD READER 175S DELETED)
9	04 / 04 / 2025	RFI #316 (ADDED DOOR 174 CONTROL & INTERCOM)
10	06 / 15 / 2025	ADDED CAMERAS N166 AND N167
11	08 / 25 / 2025	DESIGN CHANGES PER RFI 367
X	XX / XX / XXXX	XXXXXX


[redacted]

PROJECT
ARAPAHOE COUNTY DETENTION CENTER
ADDITION AND REMODEL
7375 S. POTOMAC ST.
CENTENNIAL, CO 80112


SHEET NAME
SECURITY FLOOR PLAN - KITCHEN / LAUNDRY

SHEET NUMBER
SE101


REVISION
11

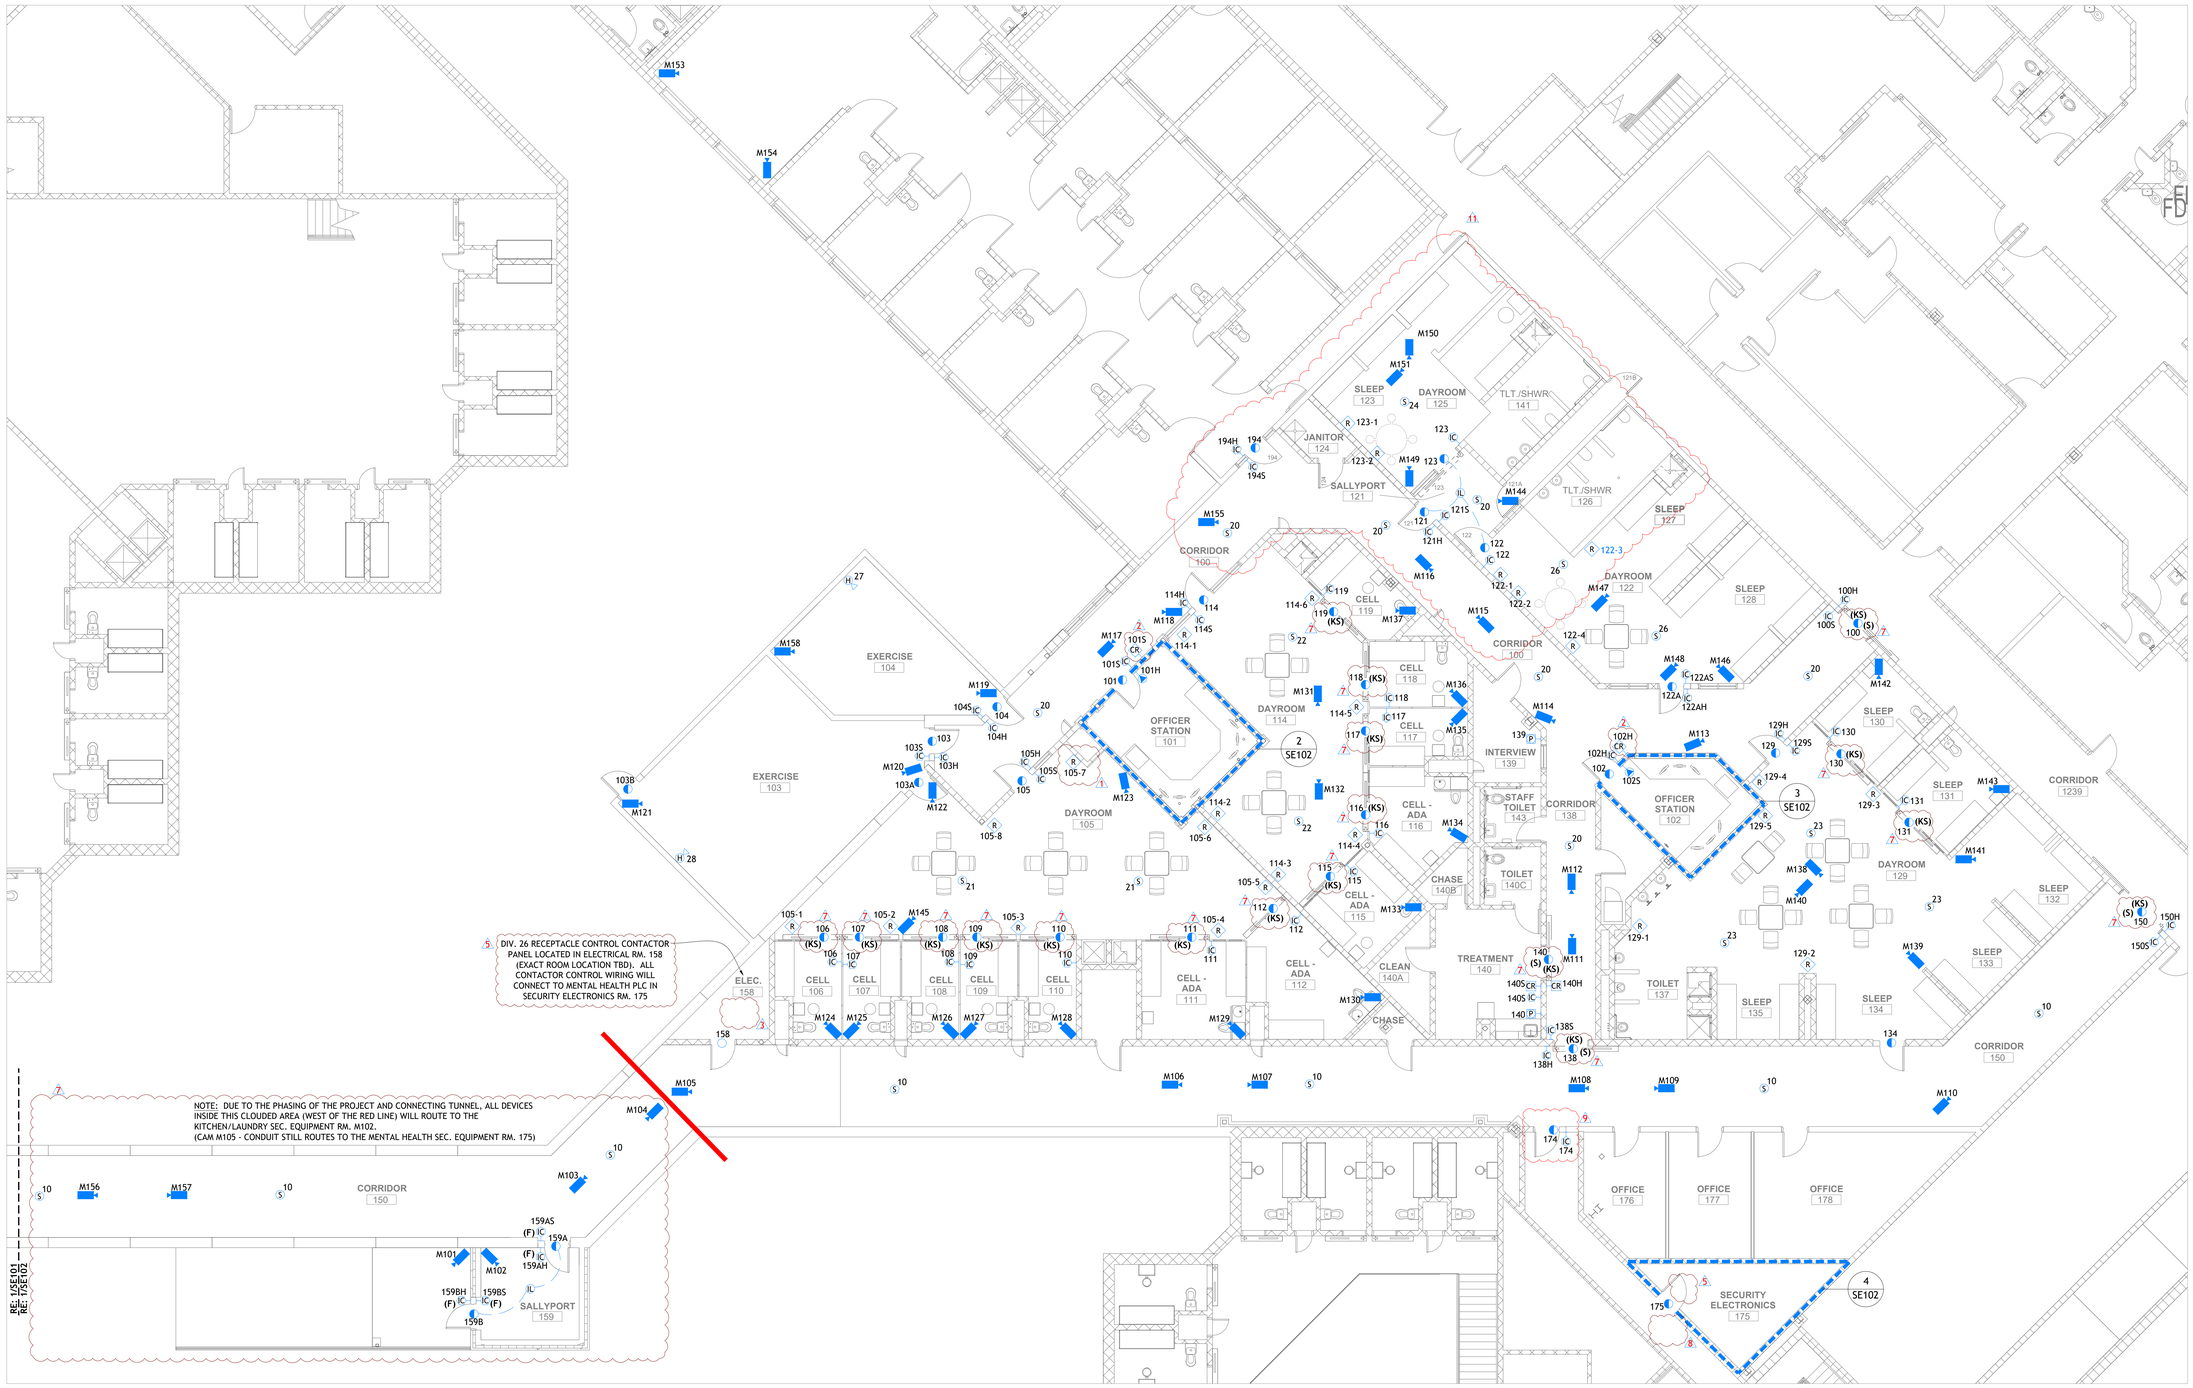


1 SECURITY FLOOR PLAN - MENTAL HEALTH
SCALE: 1/8" = 1'-0"

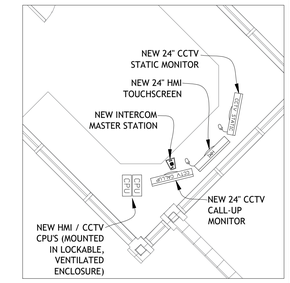

2 OFFICER STATION - RM. 101
SCALE: 1/4" = 1'-0"

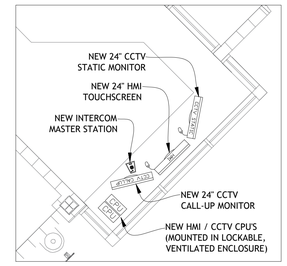

3 OFFICER STATION - RM. 102
SCALE: 1/4" = 1'-0"

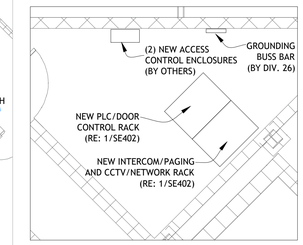

4 S.E.C. EQUIPMENT - RM. 175
SCALE: 1/4" = 1'-0"

REVISION	DATE	DESCRIPTION	REVISION	DATE	DESCRIPTION	REVISION	DATE	DESCRIPTION
0	10 / 25 / 2023	SUBMITTAL	7	12 / 17 / 2024	ADDED LOCAL KEYSWITCHES; SLIDERS 100,138,140,150,122A,122B, 150A AND KICK RELEASE DOORS 106-112,115-119,123,125,130-131	X	XX / XX / XXXX	XXXXXX
1	12 / 05 / 2023	RESUBMITTAL	8	01 / 17 / 2025	RFI #297 (CARD READER 175S DELETED)			
2	05 / 14 / 2024	ASI #08 UPDATES	9	04 / 04 / 2025	RFI #316 (ADDED DOOR 174 CONTROL & INTERCOM)			
3	06 / 12 / 2024	RFI #202 UPDATES	10	06 / 15 / 2025	ADDED CAMERAS N166 AND N167			
4	07 / 02 / 2024	ASI #08-R1 UPDATES	11	08 / 25 / 2025	DESIGN CHANGES PER RFI 367			
5	08 / 26 / 2024	ASI #08-R2 UPDATES						
6	11 / 04 / 2024	RFI #259 UPDATES						


[redacted]

PROJECT
ARAPAHOE COUNTY DETENTION CENTER
ADDITION AND REMODEL
7375 S. POTOMAC ST.
CENTENNIAL, CO 80112

SHEET NAME
SECURITY FLOOR PLAN - MENTAL HEALTH

SHEET NUMBER
SE102

REVISION
11

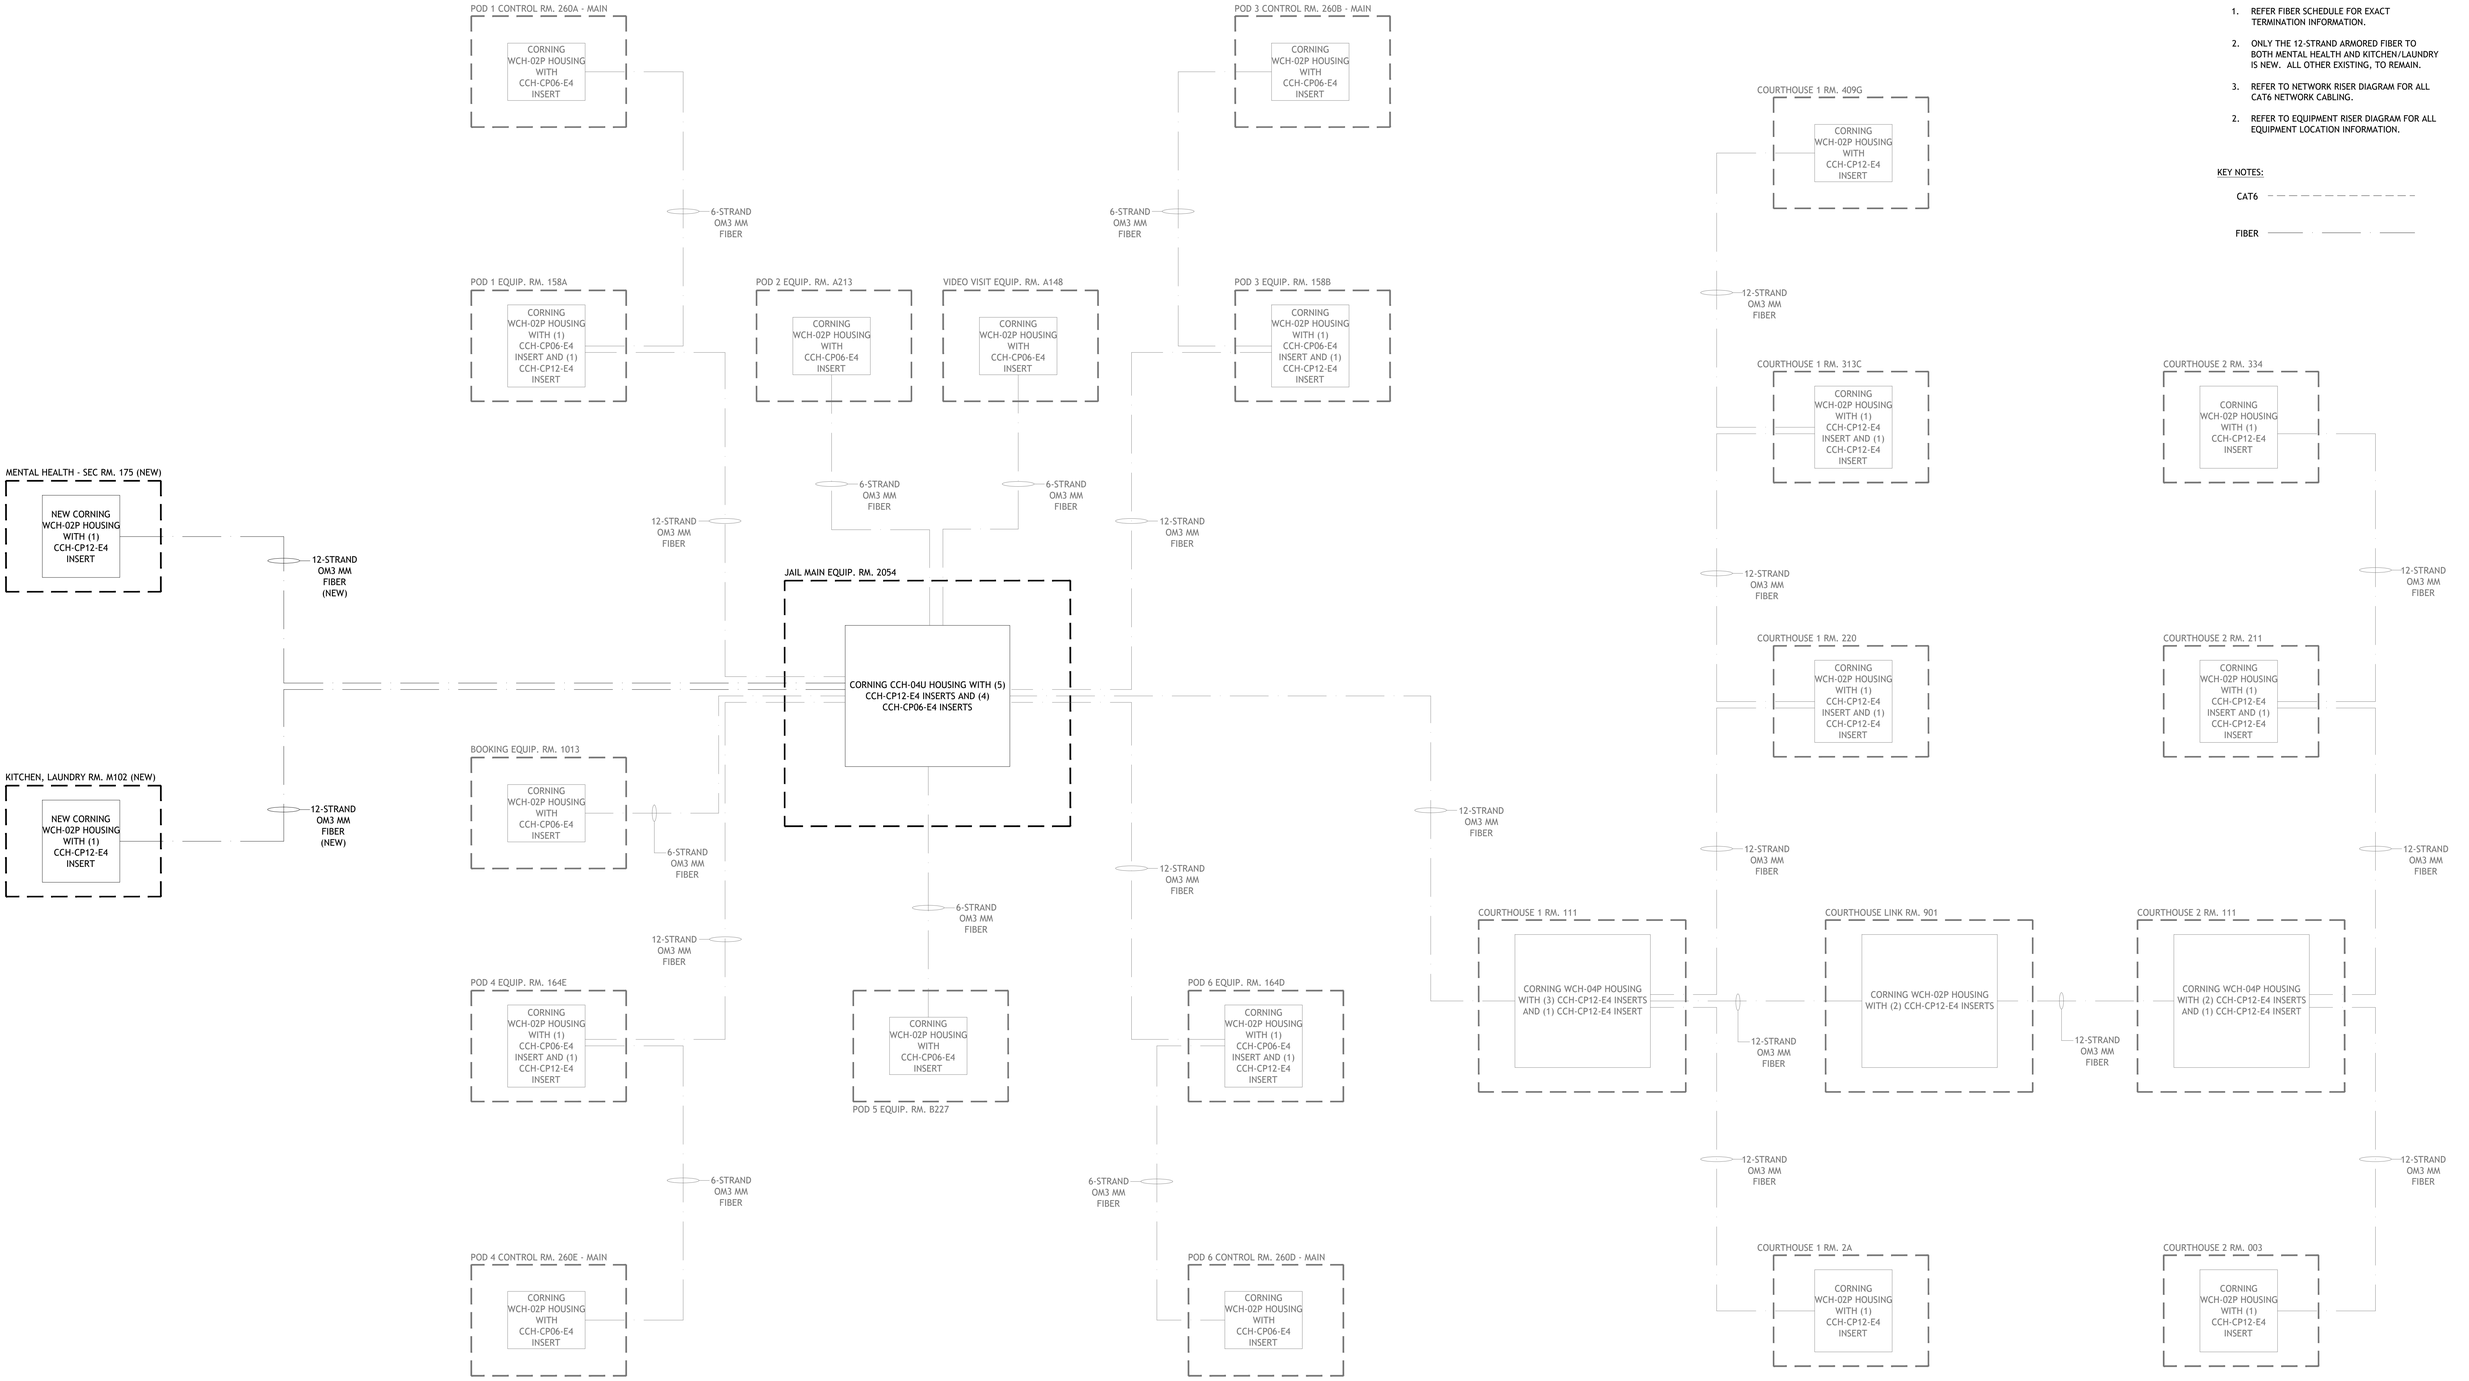

GENERAL NOTES:

1. REFER FIBER SCHEDULE FOR EXACT TERMINATION INFORMATION.
2. ONLY THE 12-STRAND ARMORED FIBER TO BOTH MENTAL HEALTH AND KITCHEN/LAUNDRY IS NEW. ALL OTHER EXISTING, TO REMAIN.
3. REFER TO NETWORK RISER DIAGRAM FOR ALL CAT6 NETWORK CABLING.
2. REFER TO EQUIPMENT RISER DIAGRAM FOR ALL EQUIPMENT LOCATION INFORMATION.

KEY NOTES:

CAT6 - - - - - - - - - - - - - - - -

FIBER ——— ——— ———

1 FUNCTIONAL DIAGRAM - FIBER RISER

SCALE: N.T.S.

REVISION	DATE	DESCRIPTION	REVISION	DATE	DESCRIPTION	REVISION	DATE	DESCRIPTION
0	10 / 25 / 2023	SUBMITTAL	7	12 / 17 / 2024	ADDED LOCAL KEYSWITCHES: SLIDERS 100,138,140,150,122A,122B, 150A AND KICK RELEASE DOORS 106-112,115-119,123,125,130-131	X	XX / XX / XXXX	XXXXXX
1	12 / 05 / 2023	RESUBMITTAL	8	01 / 17 / 2025	RFI #297 (CARD READER 175S DELETED)			
2	05 / 14 / 2024	ASI #08 UPDATES	9	04 / 04 / 2025	RFI #316 (ADDED DOOR 174 CONTROL & INTERCOM)			
3	06 / 12 / 2024	RFI #202 UPDATES	10	06 / 15 / 2025	ADDED CAMERAS N166 AND N167			
4	07 / 02 / 2024	ASI #08-R1 UPDATES	11	08 / 25 / 2025	DESIGN CHANGES PER RFI 367			
5	08 / 26 / 2024	ASI #08-R2 UPDATES						
6	11 / 04 / 2024	RFI #259 UPDATES						

[redacted]

PROJECT

ARAPAHOE COUNTY DETENTION CENTER
ADDITION AND REMODEL
7375 S. POTOMAC ST.
CENTENNIAL, CO 80112

SHEET NAME

FUNCTIONAL DIAGRAM - FIBER RISER

SHEET NUMBER

SE201

REVISION

11


GENERAL NOTES:

1. REFER IP DEVICE SCHEDULE FOR EXACT TERMINATION INFORMATION.
2. ONLY THE CAT6 TO MENTAL HEALTH AND KITCHEN/LAUNDRY IS NEW UNLESS NOTED OTHERWISE.
3. REFER TO FIBER RISER DIAGRAM FOR ALL FIBER NETWORK CABLING.
4. REFER TO EQUIPMENT RISER DIAGRAM FOR ALL EQUIPMENT LOCATION INFORMATION.

KEY NOTES:

CAT6 - - - - - - - - - - - - - - - -

FIBER ——— · ——— · ———

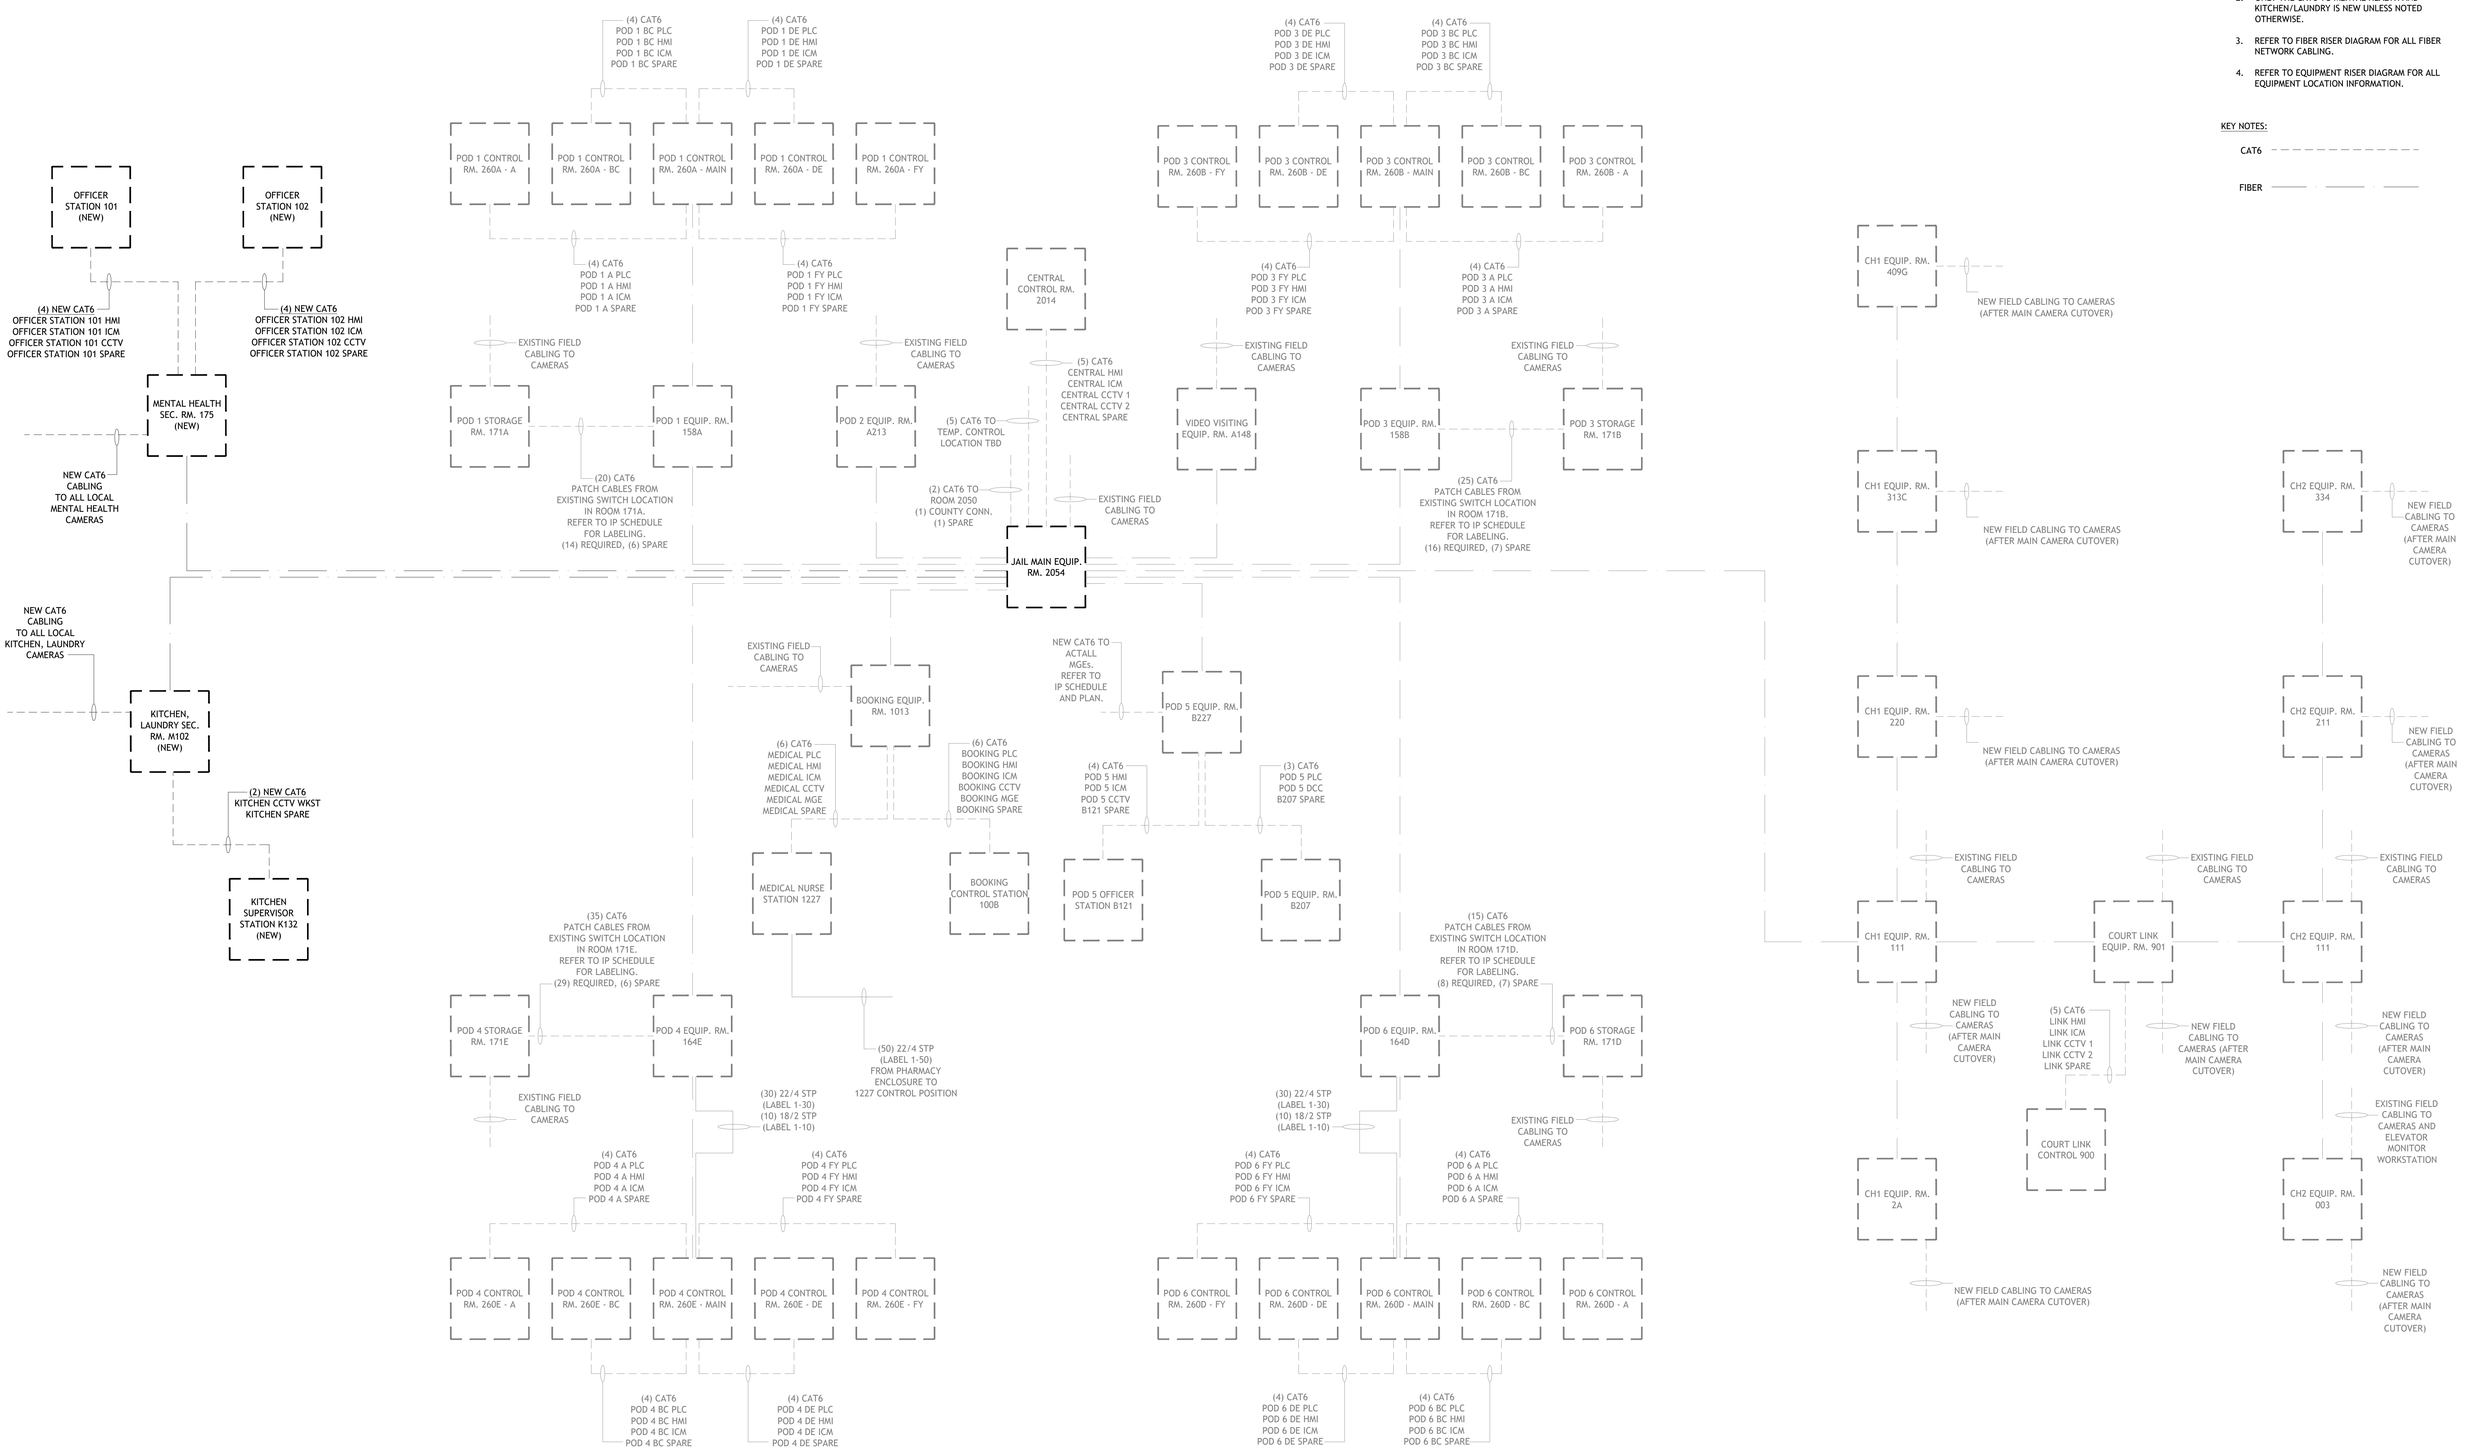

1 FUNCTIONAL DIAGRAM - NETWORK RISER

SCALE: N.T.S.

REVISION	DATE	DESCRIPTION	REVISION	DATE	DESCRIPTION	REVISION	DATE	DESCRIPTION
0	10 / 25 / 2023	SUBMITTAL	7	12 / 17 / 2024	ADDED LOCAL KEYSWITCHES: SLIDERS 100,138,140,150,122A,122B, 150A AND KICK RELEASE DOORS 106-112,115-119,123,125,130-131	X	XX / XX / XXXX	XXXXXX
1	12 / 05 / 2023	RESUBMITTAL	8	01 / 17 / 2025	RFI #297 (CARD READER 175S DELETED)			
2	05 / 14 / 2024	ASI #08 UPDATES	9	04 / 04 / 2025	RFI #316 (ADDED DOOR 174 CONTROL & INTERCOM)			
3	06 / 12 / 2024	RFI #202 UPDATES	10	06 / 15 / 2025	ADDED CAMERAS N166 AND N167			
4	07 / 02 / 2024	ASI #08-R1 UPDATES	11	08 / 25 / 2025	DESIGN CHANGES PER RFI 367			
5	08 / 26 / 2024	ASI #08-R2 UPDATES						
6	11 / 04 / 2024	RFI #259 UPDATES						

PROJECT

ARAPAHOE COUNTY DETENTION CENTER
ADDITION AND REMODEL
7375 S. POTOMAC ST.
CENTENNIAL, CO 80112

SHEET NAME

FUNCTIONAL DIAGRAM - NETWORK RISER

SHEET NUMBER


SE202

REVISION

11

GENERAL NOTES:

1. REFER TO PLC I/O LIST, CCTV-IP SCHEDULE, AND INTERCOM/PAGING SCHEDULE FOR ALL EXACT TERMINATIONS. FOR EXACT WIRING METHODS, REFER TO WIRING DETAIL DRAWINGS:
   RE: SE301 FOR INTERCOM/PAGING AND CCTV WIRING
   RE: SE302 FOR LOCK AND UTILITY CONTROL WIRING
   RE: SE303 FOR MISCELLANEOUS DEVICES (DPS, REX, PANICS, ACCESS TRIGGERS)
2. ONLY THE MENTAL HEALTH AND KITCHEN/LAUNDRY EXPANSION AREAS ARE SHOWN ON THIS DIAGRAM FOR CLARITY.
3. TVSS WILL BE PROVIDED ON ANY COPPER CONNECTOR BETWEEN EXTERIOR DEVICES/CAMERAS AND EQUIPMENT.

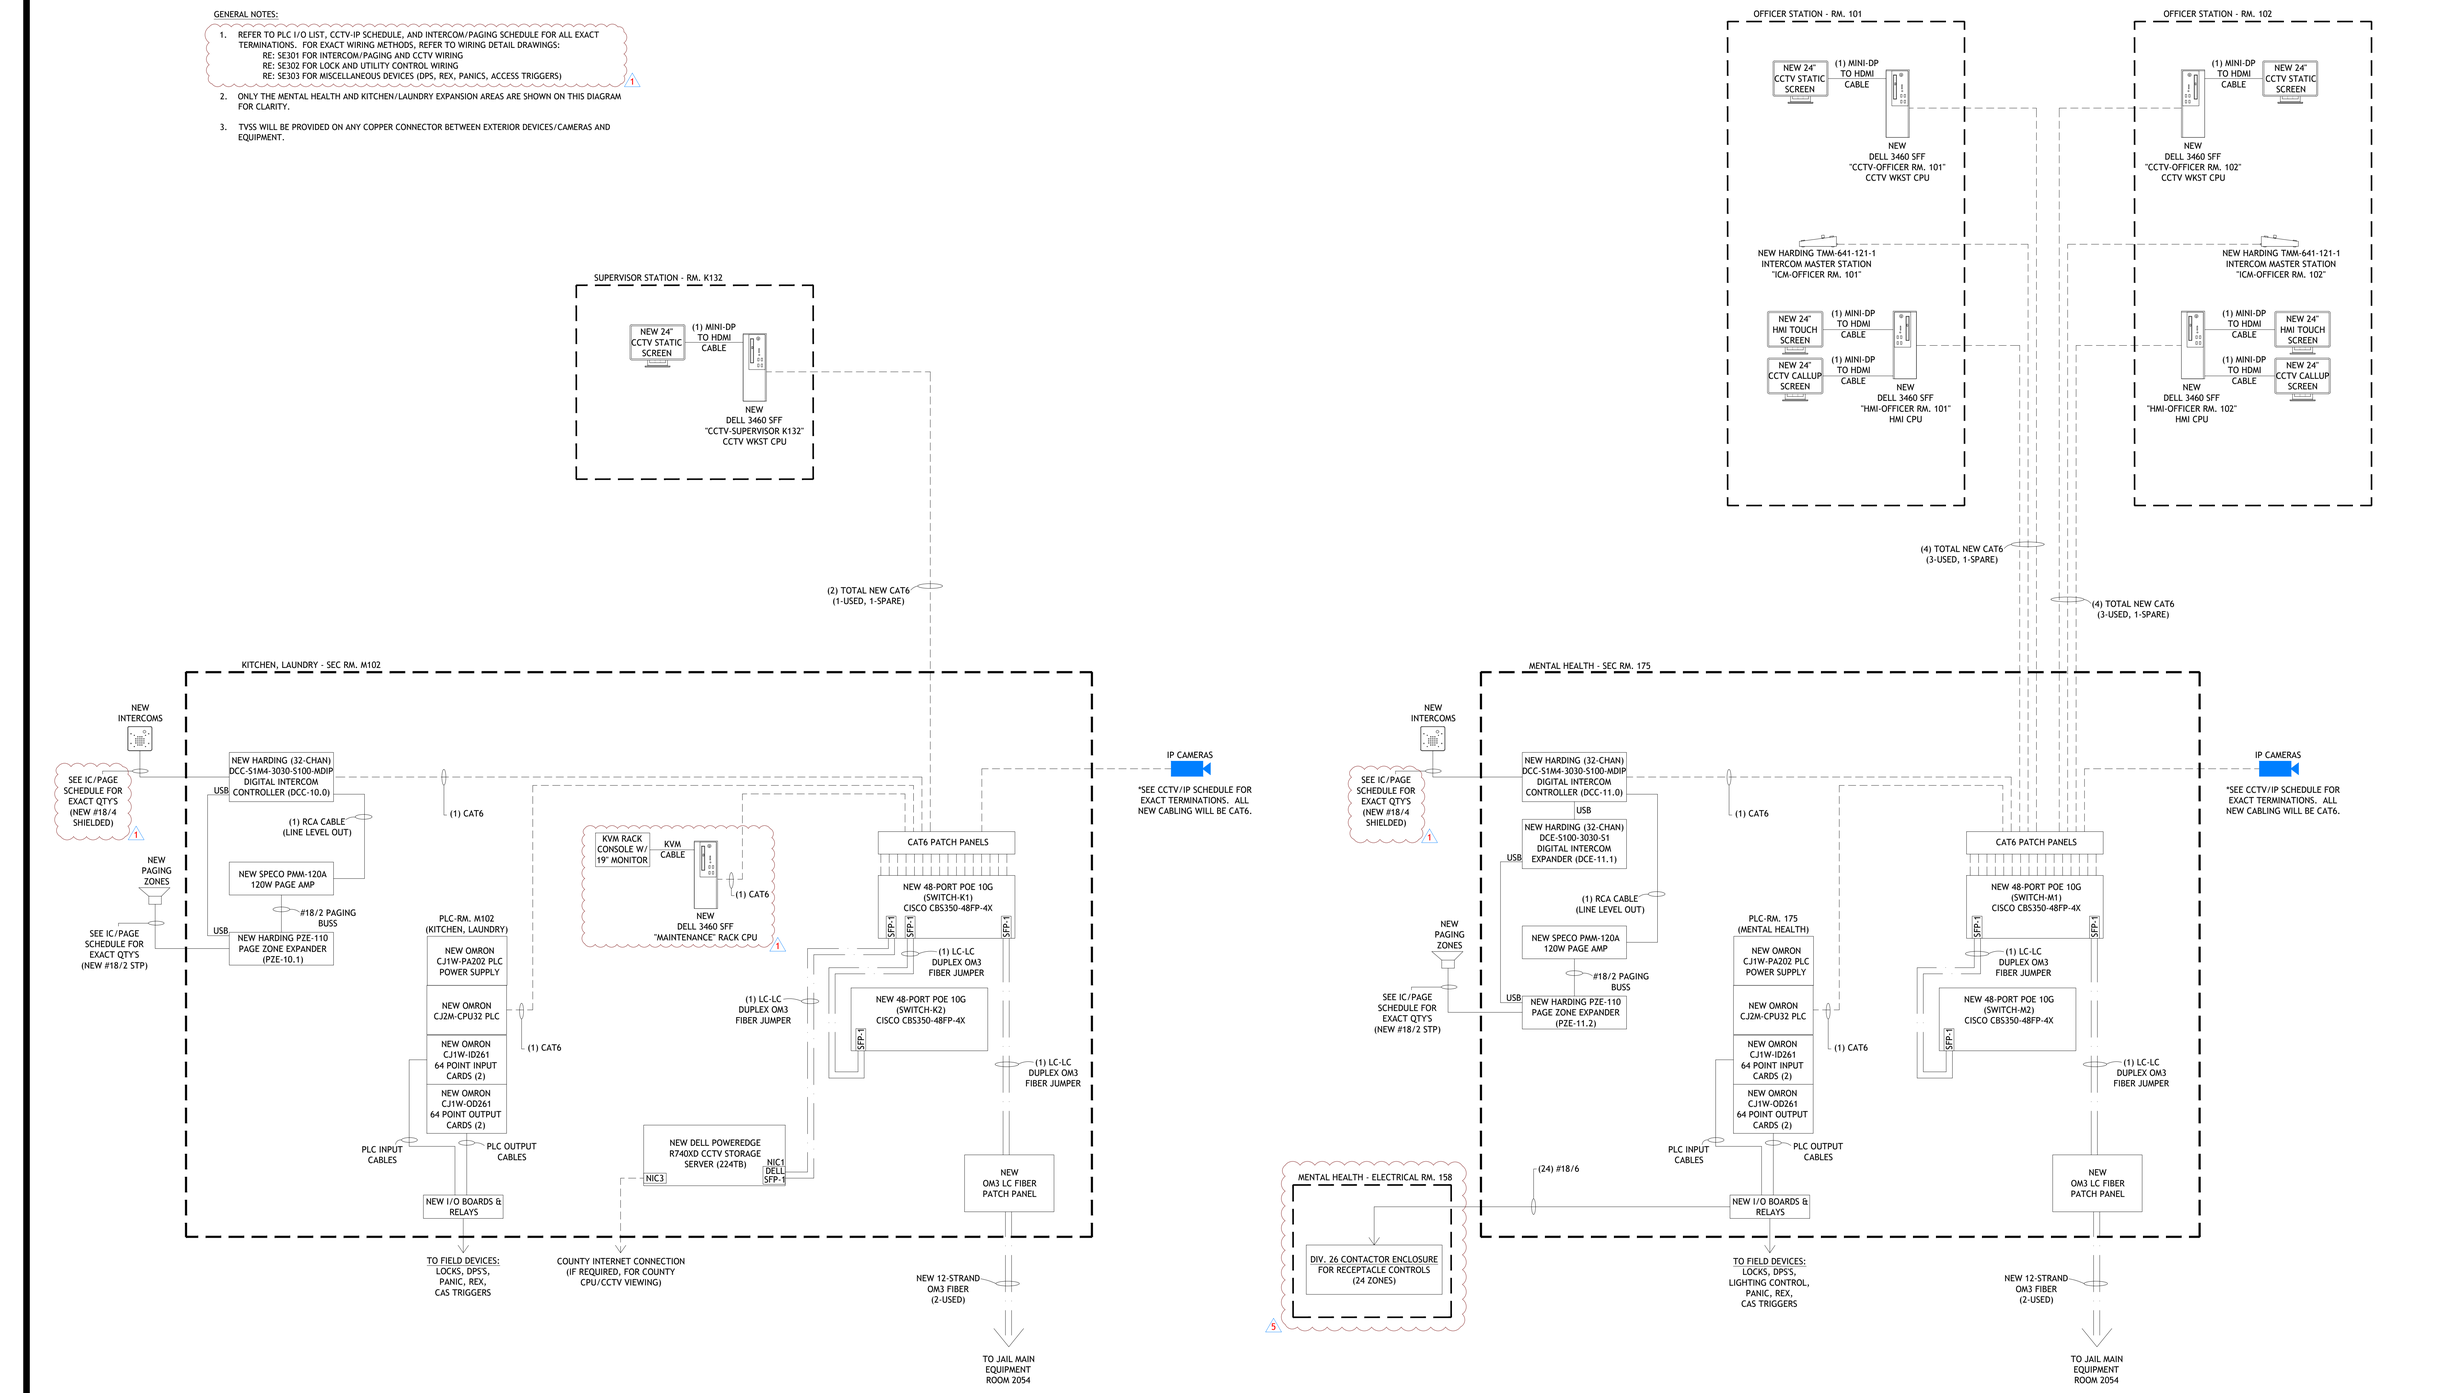

1 FUNCTIONAL DIAGRAM - PLC, HMI, INTERCOM, CCTV
SCALE: N.T.S.

REVISION	DATE	DESCRIPTION	REVISION	DATE	DESCRIPTION	REVISION	DATE	DESCRIPTION
0	10 / 25 / 2023	SUBMITTAL	7	12 / 17 / 2024	ADDED LOCAL KEYSWITCHES: SLIDERS 100,138,140,150,122A,122B, 150A AND KICK RELEASE DOORS 106-112,115-119,123,125,130-131	X	XX / XX / XXXX	XXXXXX
1	12 / 05 / 2023	RESUBMITTAL	8	01 / 17 / 2025	RFI #297 (CARD READER 1755 DELETED)			
2	05 / 14 / 2024	ASI #08 UPDATES	9	04 / 04 / 2025	RFI #316 (ADDED DOOR 174 CONTROL & INTERCOM)			
3	06 / 12 / 2024	RFI #202 UPDATES	10	06 / 15 / 2025	ADDED CAMERAS N166 AND N167			
4	07 / 02 / 2024	ASI #08-R1 UPDATES	11	08 / 25 / 2025	DESIGN CHANGES PER RFI 367			
5	08 / 26 / 2024	ASI #08-R2 UPDATES						
6	11 / 04 / 2024	RFI #259 UPDATES						


[redacted]

PROJECT
ARAPAHOE COUNTY DETENTION CENTER
ADDITION AND REMODEL
7375 S. POTOMAC ST.
CENTENNIAL, CO 80112

SHEET NAME
FUNCTIONAL DIAGRAM - PLC, HMI, INTERCOM, CCTV


SHEET NUMBER
SE203

REVISION
11

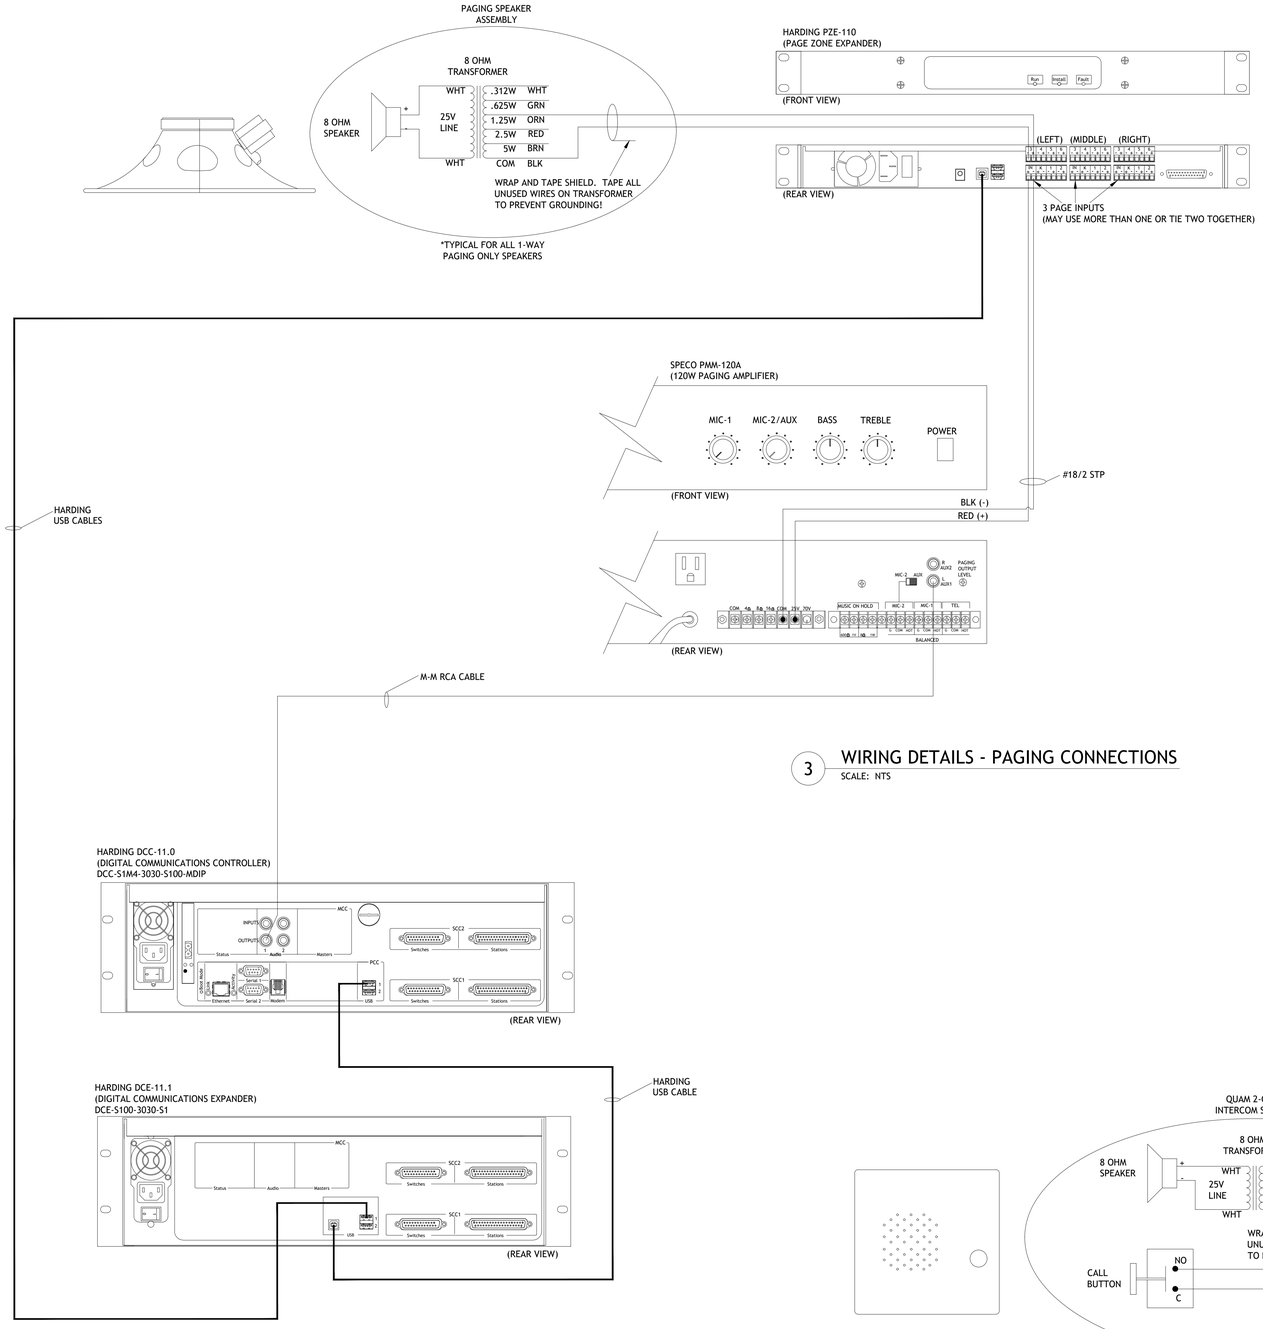


3 WIRING DETAILS - PAGING CONNECTIONS

SCALE: NTS

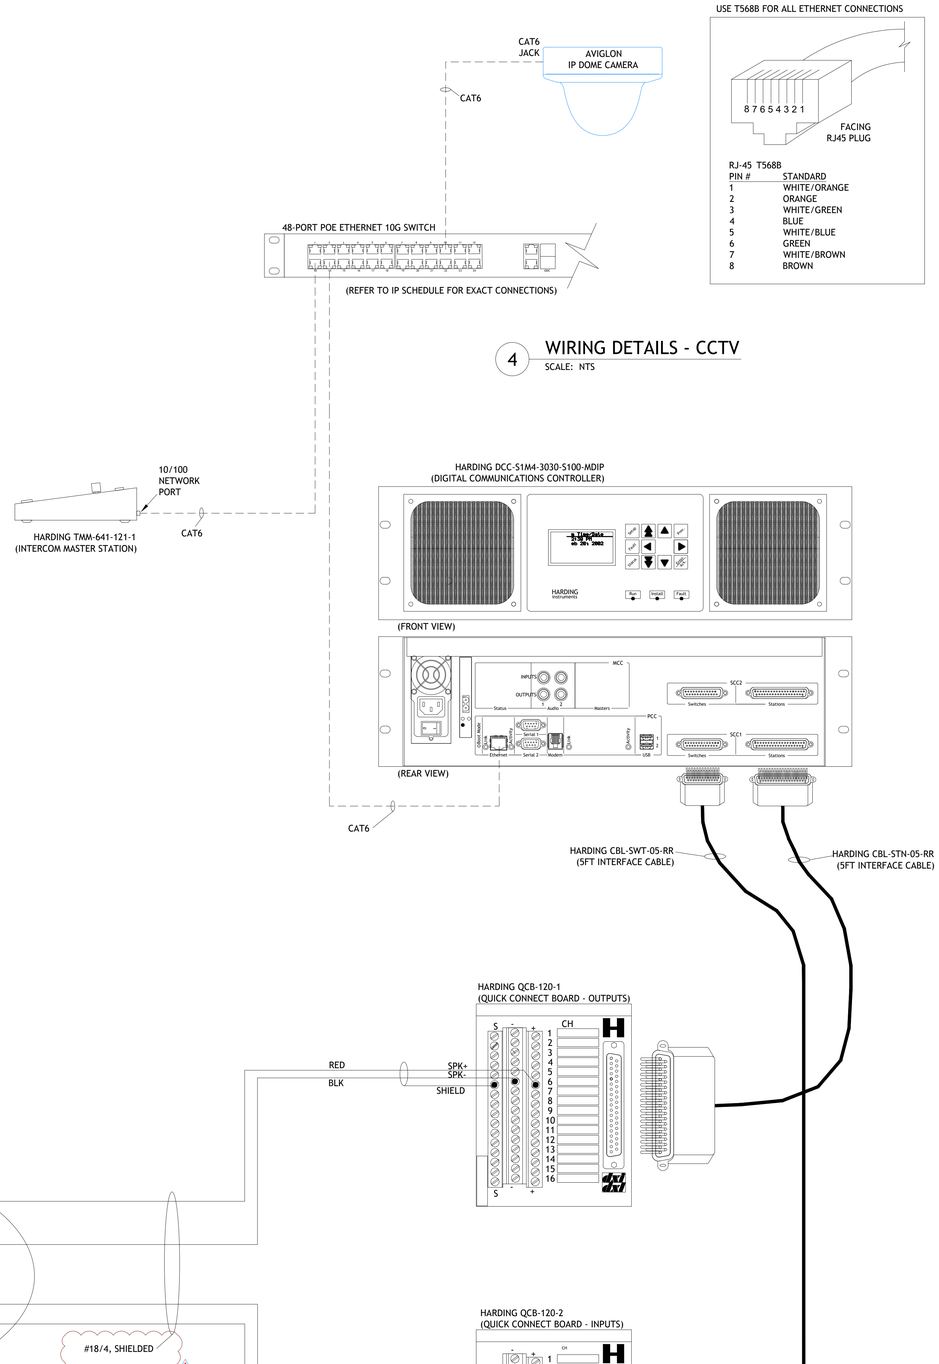

4 WIRING DETAILS - CCTV

SCALE: NTS

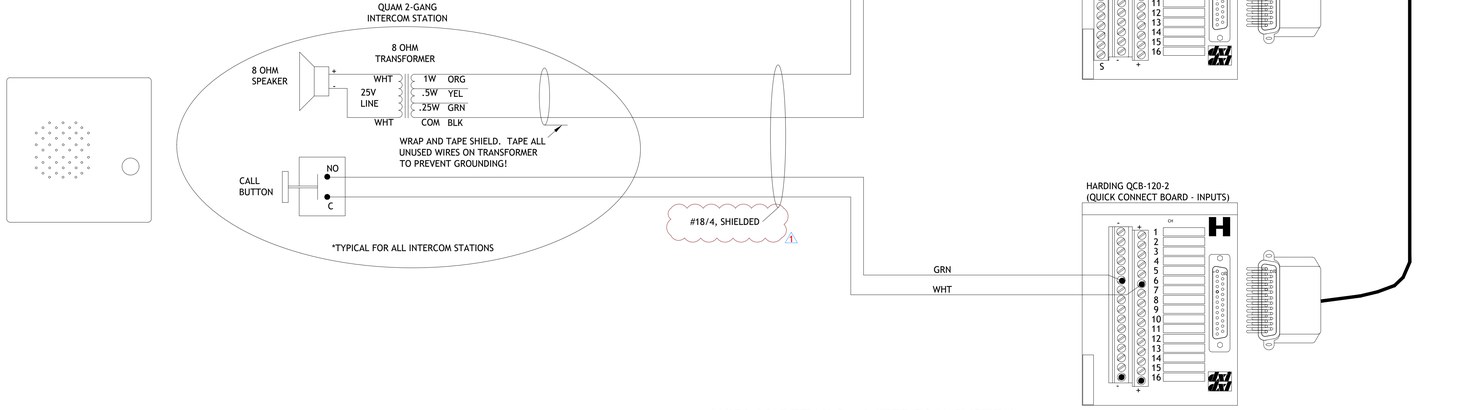

1 WIRING DETAILS - INTERCOM SYSTEM

SCALE: NTS

2 WIRING DETAILS - HARDING USB CONNECTIONS

SCALE: NTS


REVISION	DATE	DESCRIPTION	REVISION	DATE	DESCRIPTION	REVISION	DATE	DESCRIPTION
0	10 / 25 / 2023	SUBMITTAL	7	12 / 17 / 2024	ADDED LOCAL KEYSWITCHES: SLIDERS 100,138,140,150,122A,122B, 150A AND KICK RELEASE DOORS 106-112,115-119,123,125,130-131	X	XX / XX / XXXX	XXXXXX
1	12 / 05 / 2023	RESUBMITTAL	8	01 / 17 / 2025	RFI #297 (CARD READER 175S DELETED)			
2	05 / 14 / 2024	ASI #08 UPDATES	9	04 / 04 / 2025	RFI #316 (ADDED DOOR 174 CONTROL & INTERCOM)			
3	06 / 12 / 2024	RFI #202 UPDATES	10	06 / 15 / 2025	ADDED CAMERAS N166 AND N167			
4	07 / 02 / 2024	ASI #08-R1 UPDATES	11	08 / 25 / 2025	DESIGN CHANGES PER RFI 367			
5	08 / 26 / 2024	ASI #08-R2 UPDATES						
6	11 / 04 / 2024	RFI #259 UPDATES						

PROJECT
ARAPAHOE COUNTY DETENTION CENTER
ADDITION AND REMODEL
7375 S. POTOMAC ST.
CENTENNIAL, CO 80112


SHEET NAME
WIRING DETAILS -
INTERCOM AND PAGING, CCTV

SHEET NUMBER
SE301


REVISION
11

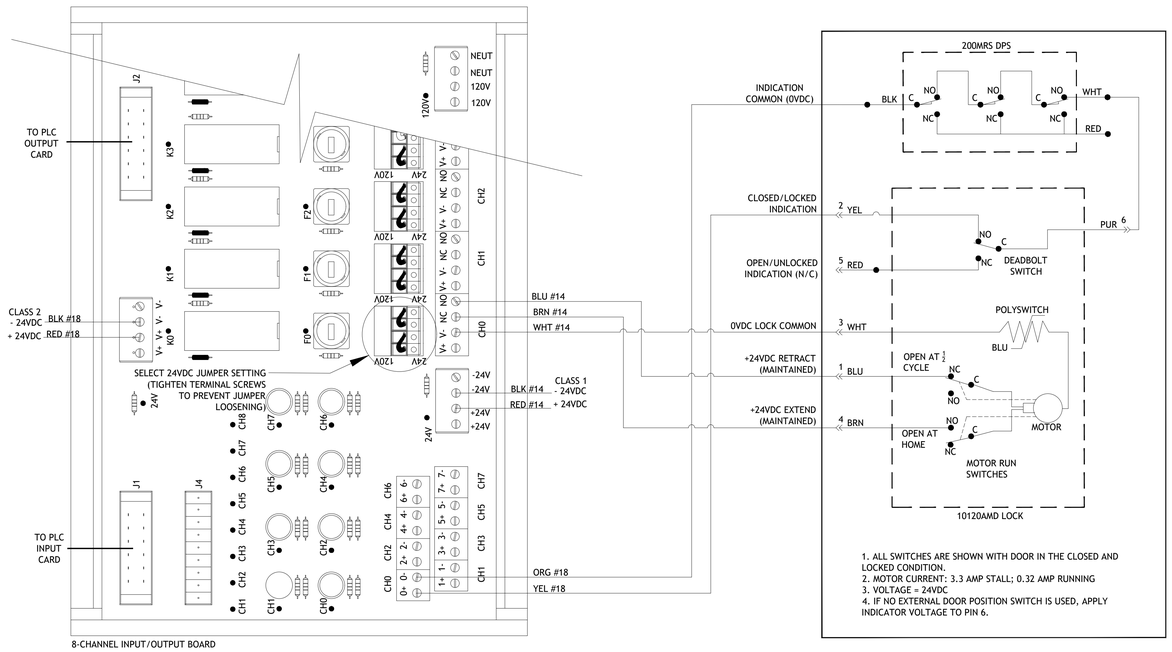


1 SOUTHERN STEEL - 10120AMD (24VDC MOTOR) LOCK W/ 200MRS D.P.S.
SCALE: NTS

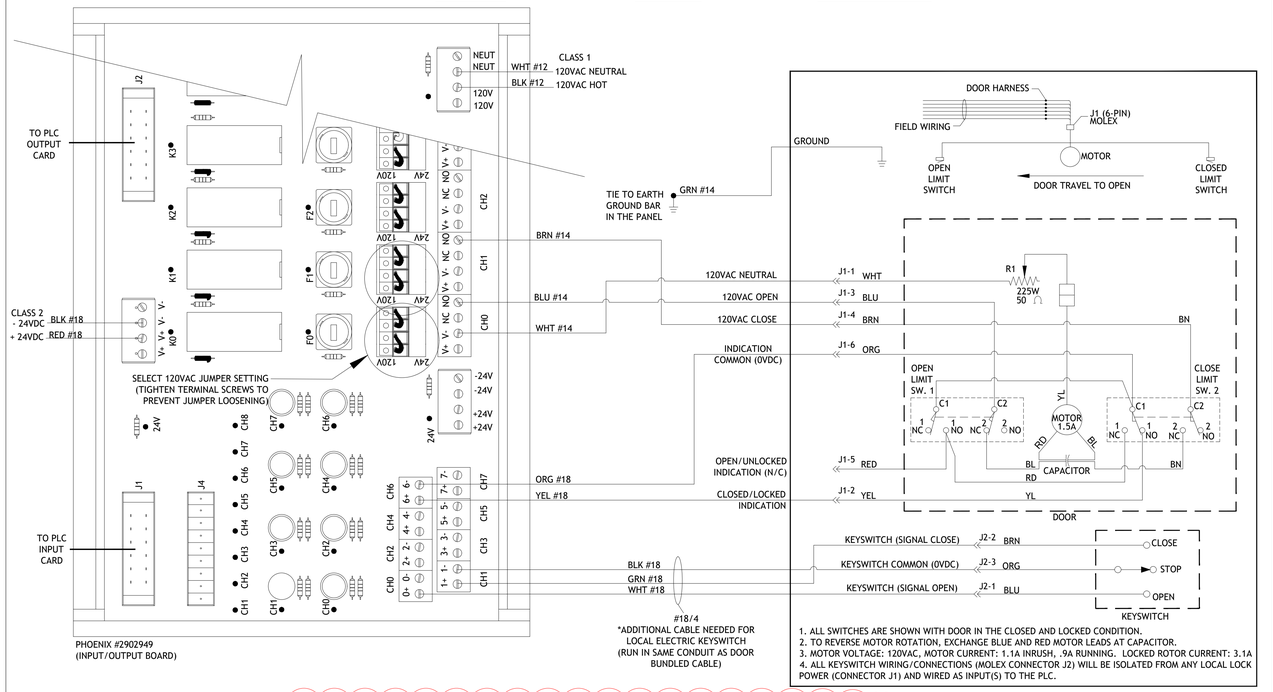

2 SOUTHERN STEEL - 3165LX.bPK (120VAC) SLIDER W/ KEYSWITCH
SCALE: NTS

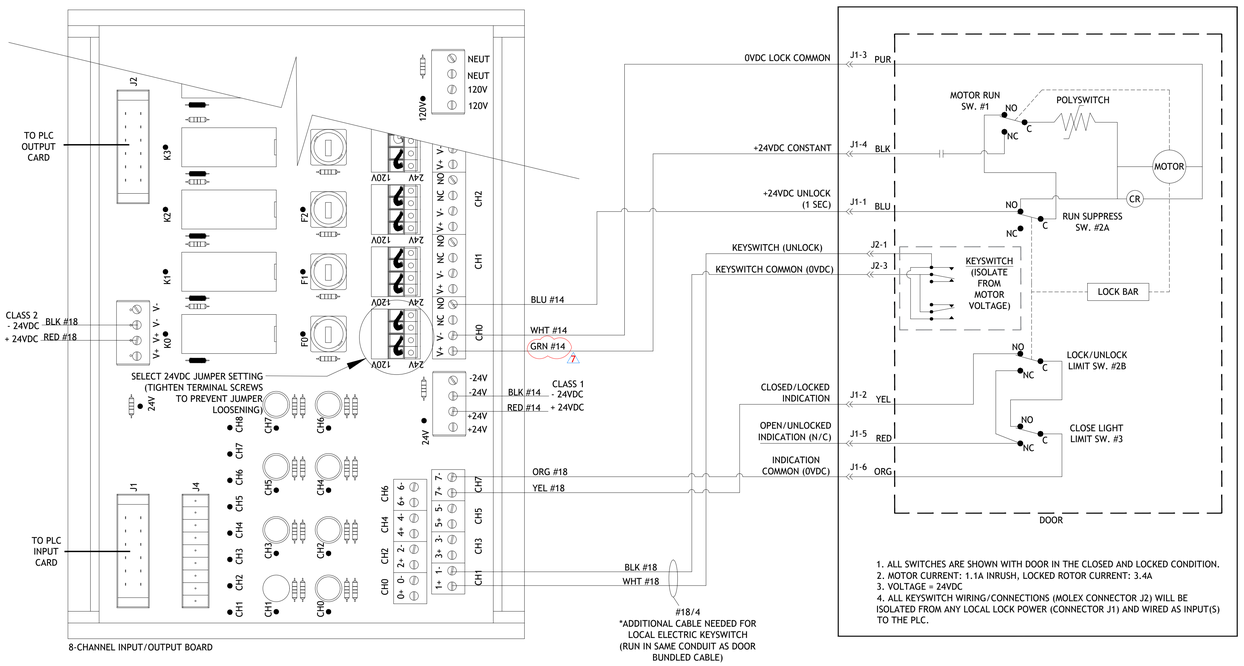

3 SOUTHERN STEEL - 4110LPKM (24VDC KICK RELEASE) LOCK - HALF CYCLE ELEMENTARY W/ KEYSWITCH
SCALE: NTS

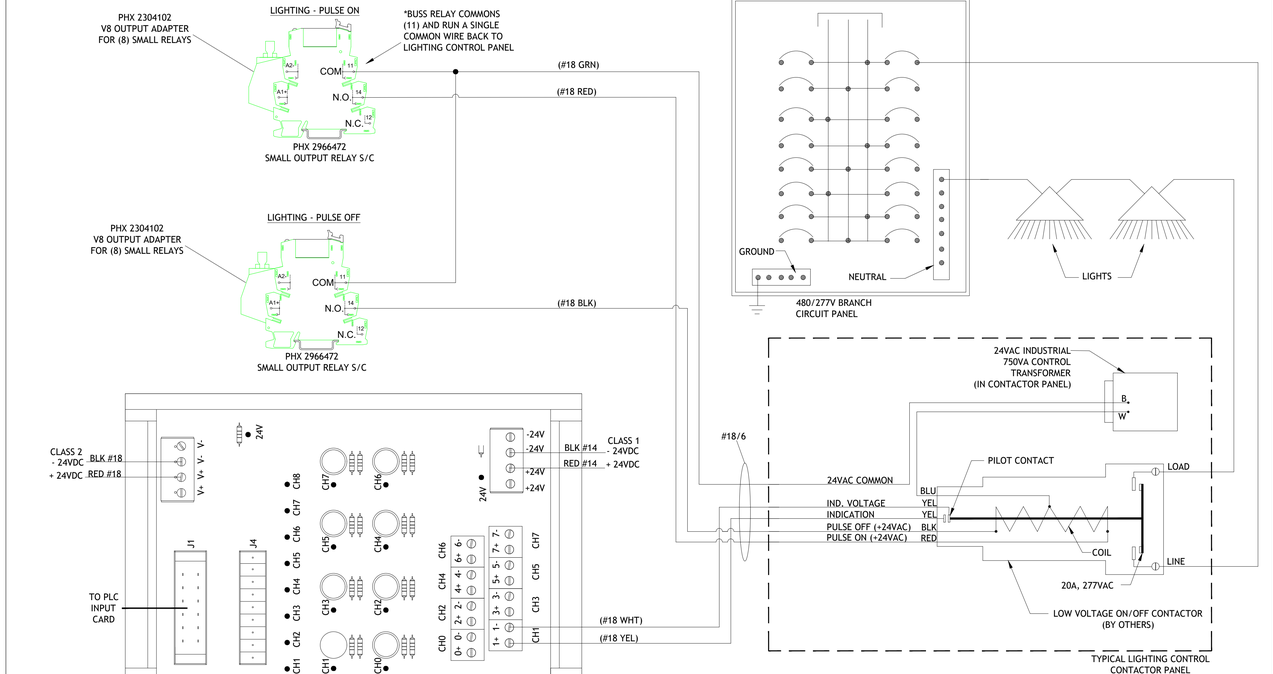

4 LIGHTING/RECEPTACLE (UTILITY) CONTROL WIRING
SCALE: NTS

REVISION	DATE	DESCRIPTION	REVISION	DATE	DESCRIPTION	REVISION	DATE	DESCRIPTION
0	10 / 25 / 2023	SUBMITTAL	7	12 / 17 / 2024	ADDED LOCAL KEYSWITCHES: SLIDERS 100,138,140,150,122A,122B, 150A AND KICK RELEASE DOORS 106-112,115-119,123,125,130-131	X	XX / XX / XXXX	XXXXXX
1	12 / 05 / 2023	RESUBMITTAL	8	01 / 17 / 2025	RFI #297 (CARD READER 175S DELETED)			
2	05 / 14 / 2024	ASI #08 UPDATES	9	04 / 04 / 2025	RFI #316 (ADDED DOOR 174 CONTROL & INTERCOM)			
3	06 / 12 / 2024	RFI #202 UPDATES	10	06 / 15 / 2025	ADDED CAMERAS N166 AND N167			
4	07 / 02 / 2024	ASI #08-R1 UPDATES	11	08 / 25 / 2025	DESIGN CHANGES PER RFI 367			
5	08 / 26 / 2024	ASI #08-R2 UPDATES						
6	11 / 04 / 2024	RFI #259 UPDATES						


[redacted]

PROJECT
ARAPAHOE COUNTY DETENTION CENTER
ADDITION AND REMODEL
7375 S. POTOMAC ST.
CENTENNIAL, CO 80112


SHEET NAME
WIRING DETAILS - LOCKS, UTILITY

SHEET NUMBER
SE302


REVISION
11

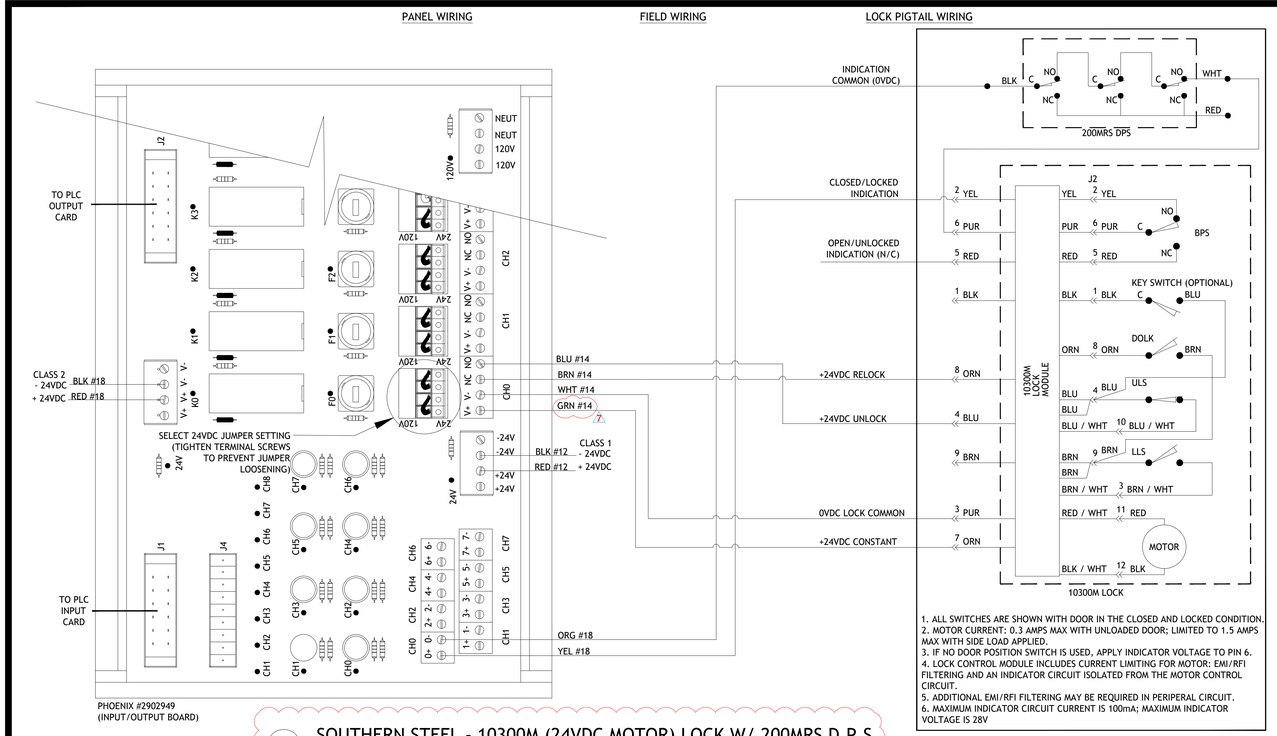

1 SOUTHERN STEEL - 10300M (24VDC MOTOR) LOCK W/ 200MRS D.P.S.
SCALE: NTS

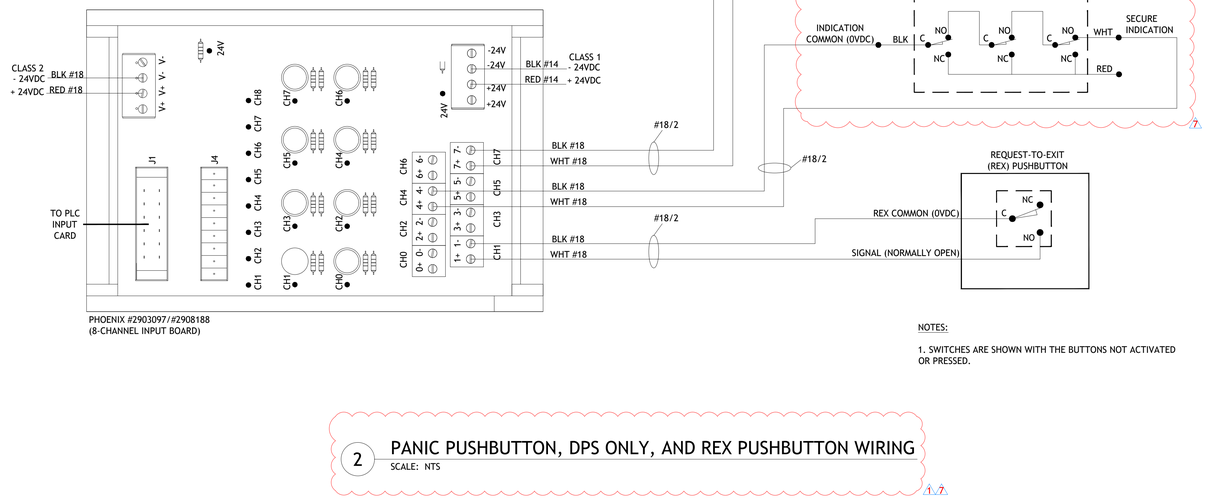

2 PANIC PUSHBUTTON, DPS ONLY, AND REX PUSHBUTTON WIRING
SCALE: NTS

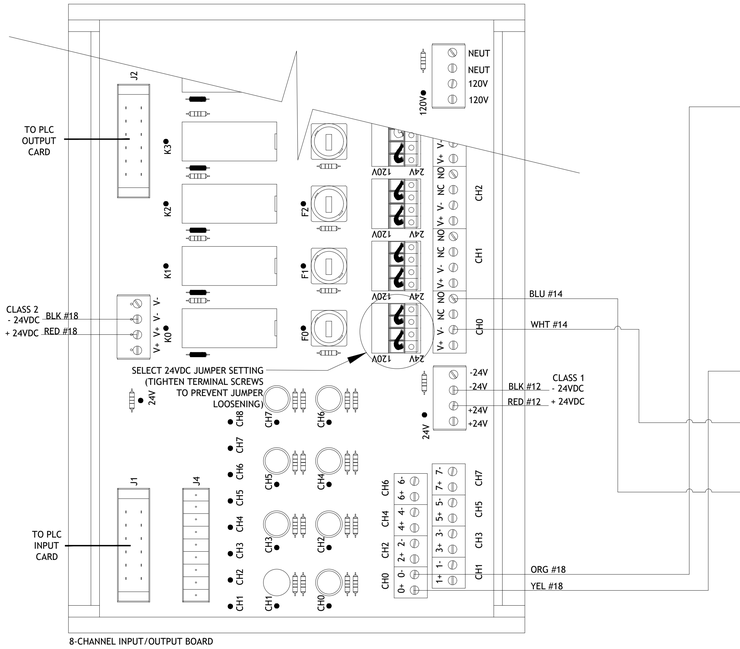

3 OVERHEAD MOTION DETECTOR (REX) AND ACCESS CONTROL TRIGGER WIRING
SCALE: NTS

4 SOUTHERN STEEL - 10600E (24VDC SOLENOID) LOCK W/ D.P.S.
SCALE: NTS

REVISION	DATE	DESCRIPTION	REVISION	DATE	DESCRIPTION	REVISION	DATE	DESCRIPTION
0	10 / 25 / 2023	SUBMITTAL	7	12 / 17 / 2024	ADDED LOCAL KEYSWITCHES: SLIDERS 100,138,140,150,122A,122B, 150A AND KICK RELEASE DOORS 106-112,115-119,123,125,130-131	X	XX / XX / XXXX	XXXXXX
1	12 / 05 / 2023	RESUBMITTAL	8	01 / 17 / 2025	RFI #297 (CARD READER 1755 DELETED)			
2	05 / 14 / 2024	ASI #08 UPDATES	9	04 / 04 / 2025	RFI #316 (ADDED DOOR 174 CONTROL & INTERCOM)			
3	06 / 12 / 2024	RFI #202 UPDATES	10	06 / 15 / 2025	ADDED CAMERAS N166 AND N167			
4	07 / 02 / 2024	ASI #08-R1 UPDATES	11	08 / 25 / 2025	DESIGN CHANGES PER RFI 367			
5	08 / 26 / 2024	ASI #08-R2 UPDATES						
6	11 / 04 / 2024	RFI #259 UPDATES						

[redacted]

PROJECT
ARAPAHOE COUNTY DETENTION CENTER
ADDITION AND REMODEL
7375 S. POTOMAC ST.
CENTENNIAL, CO 80112

SHEET NAME
WIRING DETAILS - MISCELLANEOUS DEVICES

SHEET NUMBER
SE303


REVISION
11

MAIN UPS FEEDER CIRCUITS	SECONDARY CIRCUIT(S)	FUSE AMPERAGES	DESCRIPTION	POWERED DEVICES
UPS-L1	UPS-F1	INPUT: 4A (LG F.B.) OUTPUT: 3A (SM F.B.)	CLASS 2, 3.8A, 24VDC PS-1	24VDC PLC I/O CARD POWER VIA (I/O BOARDS 1-4) *CLASS 2 SIDE ONLY
	UPS-F2	INPUT: 4A (LG F.B.) OUTPUT: 3A (SM F.B.)	CLASS 2, 3.8A, 24VDC PS-2	24VDC PLC I/O CARD POWER VIA (I/O BOARDS 5-8) *CLASS 2 SIDE ONLY
	UPS-F3	INPUT: 4A (LG F.B.) OUTPUT: 6A (SM F.B.)	CLASS 1, 10A, 24VDC PS-3	24VDC LOCK POWER (I/O BOARDS 1-2) *CLASS 1 SIDE ONLY
	UPS-F4	INPUT: 4A (LG F.B.) OUTPUT: 6A (SM F.B.)	CLASS 1, 10A, 24VDC PS-4	24VDC LOCK POWER (I/O BOARDS 4-8) *CLASS 1 SIDE ONLY
	UPS-F5	800mA (LG F.B.)	PLC-RM. M102 (KITCHEN, LAUNDRY)	OMRON CJ1W-PA202
	UPS-F6	SPARE: 6A (LG F.B.)	120VAC SLIDER POWER	120VAC SLIDER POWER (I/O BOARD 3) *CLASS 1 SIDE ONLY
	UPS-F7	SPARE: 4A (LG F.B.)	SPARE	


FUSE SCHEDULE

ITEM #	MANUFACTURER	PART_NUMBER	DESCRIPTION	QTY
1	OMRON	CJ1W-ID261	CJ1 PLC INPUT CARD, 24VDC 64 PT, 4.1mA	2
2	OMRON	CJ1W-OD261	CJ1 PLC OUTPUT CARD, 12-24VDC 64 PT, 0.3A, SINKING	2
3	OMRON	CJ1W-PA202	CJ1 PLC POWER SUPPLY, 14W	1
4	OMRON	CJ2M-CPU32	CJ2 PLC CPU W/ BUILT-IN ETHERNET, 2560 IO PTS, 10k PROG, 64k DATA	1
5	FERRAZ SHAMUT	GGC8/10	800mA 1/4" X 1-1/4" FAST ACTING FUSE	1
6	FERRAZ SHAMUT	GGC4	4A 1/4" X 1-1/4" FAST ACTING FUSE	4
7	FERRAZ SHAMUT	GGC6	6A 1/4" X 1-1/4" FAST ACTING FUSE	2
8	FERRAZ SHAMUT	GGM8	8A 5MMX20MM FAST ACTING FUSE	2
9	FERRAZ SHAMUT	GGM3	3A 5MMX20MM FAST ACTING FUSE	2
10	WEIDMULLER	6720001957	8-CHANNEL VARIOFACE INPUT/OUTPUT BOARD W/SCREW KITS	8
11	WEIDMULLER	7507096796	PLC OUTPUT CABLE, 40-PIN FUGITSU TO 4x14 IDC, 2M LENGTH	4
12	WEIDMULLER	7507096795	PLC INPUT CABLE, 40-PIN FUGITSU TO 4x14 IDC, 2M LENGTH	4
13	PHOENIX	2866323	24V 10A TRIO POWER SUPPLY	2
14	PHOENIX	2907918	PLUGTRAB (TVSS) PLUG AND BASE	1
15	PHOENIX	3036385	LARGE FUSE HOLDER 8.2MM, FOR CARTRIDGE FUSES (6.3x32MM) S/C	7
16	PHOENIX	2866336	24VDC, 3.8A, MINI CLASS 2 POWER SUPPLY	2
17	PHOENIX	3022276	SMALL END STOP	4
18	PHOENIX	3036369	SMALL FUSE HOLDER 6.2MM, FOR CARTRIDGE FUSES (5x20MM) S/C	4
19	PHOENIX	0800886	LARGE END STOP	26
20	PHOENIX	3030323	FIXED BRIDGE JUMPER FBS10-8 FOR LARGE FUSE HOLDERS	1
21	PHOENIX	3030726	PLUG-IN JUMPER FBS20-5 FOR 5.2MM TERMINAL BLOCKS	5
22	PHOENIX	0801733	DIN RAIL, 6FT STICK (EACH)	6
23	PHOENIX	3030459	COVER FOR 2-LEVEL TB	4
24	PHOENIX	3030417	COVER FOR SINGLE LEVEL TB	3
25	PHOENIX	3031270	2-LEVEL TB, 5.2MM WIDTH, 28-12 AWG S/C	16
26	PHOENIX	3037122	SINGLE LEVEL TB, 5.2MM WIDTH, 28-12 AWG BLACK S/C	1
27	PHOENIX	3037119	SINGLE LEVEL TB, 5.2MM WIDTH, 28-12 AWG WHITE S/C	8
28	PHOENIX	3031238	SINGLE LEVEL W/ GND TB, 5.2MM WIDTH, 28-12 AWG, GREEN S/C	8
29	PHOENIX	2908188	8-CHANNEL VARIOFACE INPUT ONLY BOARD	0
30	PHOENIX	2966171	24VDC COIL, SMALL RELAY, SCREW	0
31	PHOENIX	2304102	V8 OUTPUT ADAPTER FOR 6.2MM SMALL RELAYS	0
32	PHOENIX	2966786	CONTINUOUS PLUG-IN BRIDGE FOR RELAYS	1
33	THOMAS & BETTS	3TK2D-48	PANEL/DIN RAIL MOUNT SNAPTRACK (48")	1
34	THOMAS & BETTS	TY1X4WPG6	1"W X 4"H WIDE SLOT WIRING DUCT, 6FT, GRAY	3
35	THOMAS & BETTS	TY2X4WPG6	2"W X 4"H WIDE SLOT WIRING DUCT, 6FT, GRAY	2
36	THOMAS & BETTS	TY3X4WPG6	3"W X 4"H WIDE SLOT WIRING DUCT, 6FT, GRAY	0
37	THOMAS & BETTS	TY4X4WPG6	4"W X 4"H WIDE SLOT WIRING DUCT, 6FT, GRAY	2
38	THOMAS & BETTS	TY1CPG6	1"W WIRING DUCT COVER, 6FT, GRAY	3
39	THOMAS & BETTS	TY2CPG6	2"W WIRING DUCT COVER, 6FT, GRAY	2
40	THOMAS & BETTS	TY3CPG6	3"W WIRING DUCT COVER, 6FT, GRAY	0
41	THOMAS & BETTS	TY4CPG6	4"W WIRING DUCT COVER, 6FT, GRAY	2
42	NVENT (HOFFMAN)	A36P24-C0756	20U PANEL	3
43	NVENT (HOFFMAN)	P19RPP5UB	5U PANEL	2
44	NVENT (HOFFMAN)	NC21810	84"H x 32"W x 42"D RACK CABINET	3
45	DELL	POWEREDGE R740XD	CCTV SERVER	1
46	HARDING	DCC-S1M4-3030-S100-MDIP	DIGITAL COMMUNICATION CONTROLLER, 32 CHAN, 300 SERIES MCC CARD	1
47	HARDING	DCE-S100-3030-S1	DIGITAL COMMUNICATION EXPANDER, 32 CHAN	0
48	HARDING	PZE-110	PAGE ZONE EXPANDER	1
49	HARDING	ADM-SOF	DXL ADMINISTRATOR SOFTWARE	1
50	HARDING	QCB-120-1	3-WIRE AUDIO STATION CONNECTION BOARD	2
51	HARDING	QCB-120-2	2-WIRE AUDIO SWITCH CONNECTION BOARD	2
52	DITEK	DTK-RM12POES-DS-R7	TVSS FOR IP POE CAMERA, 12 PORTS, RACK MOUNT	1
53	SPECO	PMM-120A	120 WATT RMS PAGE AMPLIFIER	1
54	SPECO	PBMRK2	120 WATT PAGE AMP RACK EARS	1
55	TRIPPLITE	B021-000-19	RACK MOUNT KVM CONSOLE WITH 19" LCD	1
56	TRIPPLITE	PDUMH20	12 MULTI OUTLET PLUGSTRIP, 20A PLUG	2
57	TRIPPLITE	N252-048	CAT6 PATCH PANEL, 48-PORT	2
58	CISCO	CBS350-48FP-4X	CISCO 48-PORT POE 10G MANAGED SWITCH	2


PARTS LIST

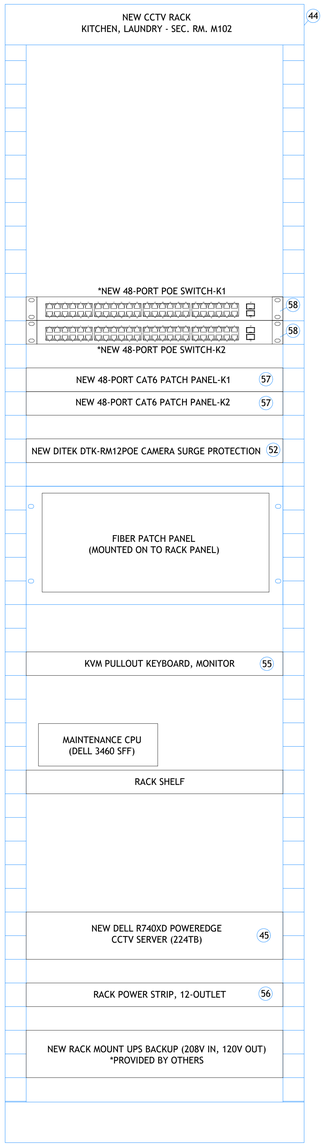


CCTV RACK - FRONT

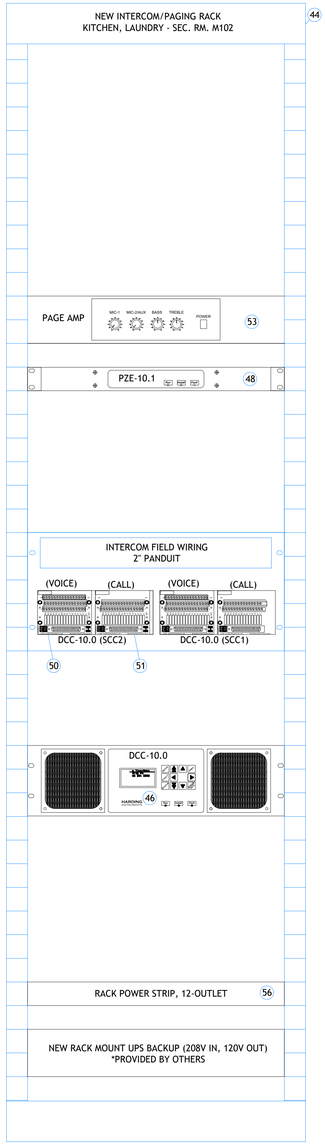

INTERCOM/PAGING RACK - FRONT

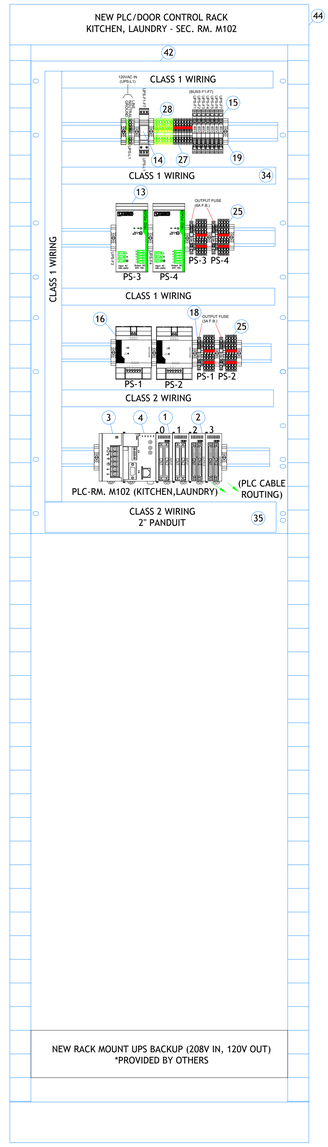

PLC/DOOR CONTROL RACK - FRONT

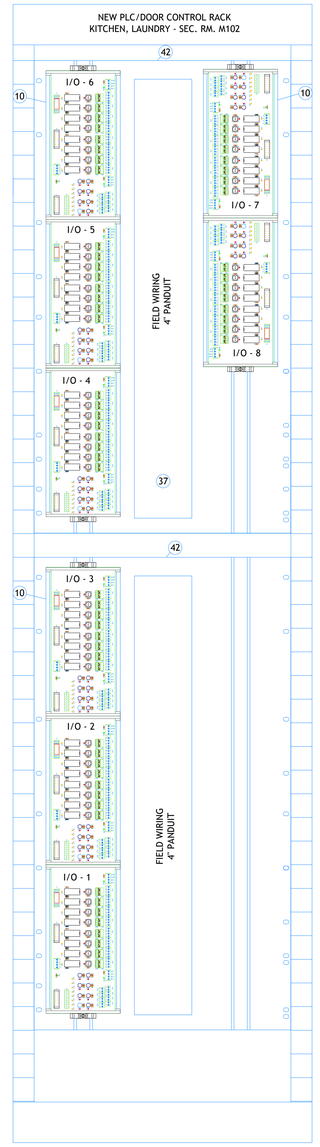

PLC/DOOR CONTROL RACK - REAR

1 RACK LAYOUTS - KITCHEN, LAUNDRY (RM. M102)
SCALE: N.T.S.

REVISION	DATE	DESCRIPTION	REVISION	DATE	DESCRIPTION	REVISION	DATE	DESCRIPTION
0	10 / 25 / 2023	SUBMITTAL	7	12 / 17 / 2024	ADDED LOCAL KEYSWITCHES: SLIDERS 100,138,140,150,122A,122B, 150A AND KICK RELEASE DOORS 106-112,115-119,123,125,130-131	X	XX / XX / XXXX	XXXXXX
1	12 / 05 / 2023	RESUBMITTAL	8	01 / 17 / 2025	RFI #297 (CARD READER 175S DELETED)			
2	05 / 14 / 2024	ASI #08 UPDATES	9	04 / 04 / 2025	RFI #316 (ADDED DOOR 174 CONTROL & INTERCOM)			
3	06 / 12 / 2024	RFI #202 UPDATES	10	06 / 15 / 2025	ADDED CAMERAS N166 AND N167			
4	07 / 02 / 2024	ASI #08-R1 UPDATES	11	08 / 25 / 2025	DESIGN CHANGES PER RFI 367			
5	08 / 26 / 2024	ASI #08-R2 UPDATES						
6	11 / 04 / 2024	RFI #259 UPDATES						

[redacted]

PROJECT
ARAPAHOE COUNTY DETENTION CENTER
ADDITION AND REMODEL
7375 S. POTOMAC ST.
CENTENNIAL, CO 80112

SHEET NAME
RACK LAYOUTS - KITCHEN, LAUNDRY (RM. M102)

SHEET NUMBER
SE401


REVISION
11

MAIN UPS FEEDER CIRCUITS	SECONDARY CIRCUIT(S)	FUSE AMPERAGES	DESCRIPTION	POWERED DEVICES
UPS-L1	UPS-F1	INPUT: 4A (LG F.B.) OUTPUT: 3A (SM F.B.)	CLASS 2, 3.8A, 24VDC PS-1	24VDC PLC I/O CARDS POWER VIA (I/O BOARDS 1-4) *CLASS 2 SIDE ONLY
	UPS-F2	INPUT: 4A (LG F.B.) OUTPUT: 3A (SM F.B.)	CLASS 2, 3.8A, 24VDC PS-2	24VDC PLC I/O CARDS POWER VIA (I/O BOARDS 5-8, IB'S 9-14, OR'S 9-14) *CLASS 2 SIDE ONLY
	UPS-F3	INPUT: 4A (LG F.B.) OUTPUT: 6A (SM F.B.)	CLASS 1, 10A, 24VDC PS-3	24VDC LOCK POWER (I/O BOARDS 1-2) *CLASS 1 SIDE ONLY
	UPS-F4	INPUT: 4A (LG F.B.) OUTPUT: 6A (SM F.B.)	CLASS 1, 10A, 24VDC PS-4	24VDC LOCK POWER (I/O BOARDS 3-4, IB'S 9-14) *CLASS 1 SIDE ONLY
	UPS-F5	800mA (LG F.B.)	PLC-RM. 175 (MENTAL HEALTH)	OMRON CJ1W-PA202
	UPS-F6	SPARE: 6A (LG F.B.)	120VAC SLIDER POWER	120VAC SLIDER POWER (I/O BOARDS 6-7) *CLASS 1 SIDE ONLY
	UPS-F7	SPARE: 4A (LG F.B.)	SPARE	


FUSE SCHEDULE

ITEM #	MANUFACTURER	PART_NUMBER	DESCRIPTION	QTY
1	OMRON	CJ1W-ID261	CJ1 PLC INPUT CARD, 24VDC 64 PT, 4.1mA	3
2	OMRON	CJ1W-OD261	CJ1 PLC OUTPUT CARD, 12-24VDC 64 PT, 0.3A, SINKING	3
3	OMRON	CJ1W-PA202	CJ1 PLC POWER SUPPLY, 14W	1
4	OMRON	CJ2M-CPU32	CJ2 PLC CPU W/ BUILT-IN ETHERNET, 2560 IO PTS, 10k PROG, 64k DATA	1
5	FERRAZ SHAMUT	GGC8/10	800mA 1/4" X 1-1/4" FAST ACTING FUSE	1
6	FERRAZ SHAMUT	GGC4	4A 1/4" X 1 -1/4" FAST ACTING FUSE	4
7	FERRAZ SHAMUT	GGC6	6A 1/4" X 1 -1/4" FAST ACTING FUSE	2
8	FERRAZ SHAMUT	GGM8	8A 5MMX20MM FAST ACTING FUSE	2
9	FERRAZ SHAMUT	GGM3	3A 5MMX20MM FAST ACTING FUSE	2
10	WEIDMULLER	6720001957	8-CHANNEL VARIOFACE INPUT/OUTPUT BOARD W/SCREW KITS	8
11	WEIDMULLER	7507096796	PLC OUTPUT CABLE, 40-PIN FUGITSU TO 4x14 IDC, 2M LENGTH	6
12	WEIDMULLER	7507096795	PLC INPUT CABLE, 40-PIN FUGITSU TO 4x14 IDC, 2M LENGTH	6
13	PHOENIX	2866323	24V 10A TRIO POWER SUPPLY	2
14	PHOENIX	2907918	PLUGTRAB (TVSS) PLUG AND BASE	1
15	PHOENIX	3036385	LARGE FUSE HOLDER 8.2MM, FOR CARTRIDGE FUSES (6.3x32MM) S/C	7
16	PHOENIX	2866336	24VDC, 3.8A, MINI CLASS 2 POWER SUPPLY	2
17	PHOENIX	3022276	SMALL END STOP	4
18	PHOENIX	3036369	SMALL FUSE HOLDER 6.2MM, FOR CARTRIDGE FUSES (5x20MM) S/C	4
19	PHOENIX	0800886	LARGE END STOP	26
20	PHOENIX	3030323	FIXED BRIDGE JUMPER FBS10-8 FOR LARGE FUSE HOLDERS	1
21	PHOENIX	3030226	PLUG-IN JUMPER FBS20-5 FOR 5.2MM TERMINAL BLOCKS	5
22	PHOENIX	0801733	DIN RAIL, 6FT STICK (EACH)	6
23	PHOENIX	3030459	COVER FOR 2-LEVEL TB	4
24	PHOENIX	3030417	COVER FOR SINGLE LEVEL TB	3
25	PHOENIX	3031270	2-LEVEL TB, 5.2MM WIDTH, 28-12 AWG S/C	16
26	PHOENIX	3037122	SINGLE LEVEL TB, 5.2MM WIDTH, 28-12 AWG BLACK S/C	1
27	PHOENIX	3037119	SINGLE LEVEL TB, 5.2MM WIDTH, 28-12 AWG WHITE S/C	8
28	PHOENIX	3031238	SINGLE LEVEL W/ GND TB, 5.2MM WIDTH, 28-12 AWG, GREEN S/C	8
29	PHOENIX	2908188	8-CHANNEL VARIOFACE INPUT ONLY BOARD	6
30	PHOENIX	2966171	24VDC COIL, SMALL RELAY, SCREW	48
31	PHOENIX	2304102	V8 OUTPUT ADAPTER FOR 6.2MM SMALL RELAYS	6
32	PHOENIX	2966786	CONTINUOUS PLUG-IN BRIDGE FOR RELAYS	1
33	THOMAS & BETTS	3TK2D-48	PANEL/DIN RAIL MOUNT SNAPTRACK (48")	1
34	THOMAS & BETTS	TY1X4WPG6	1"W X 4"H WIDE SLOT WIRING DUCT, 6FT, GRAY	3
35	THOMAS & BETTS	TY2X4WPG6	2"W X 4"H WIDE SLOT WIRING DUCT, 6FT, GRAY	2
36	THOMAS & BETTS	TY3X4WPG6	3"W X 4"H WIDE SLOT WIRING DUCT, 6FT, GRAY	0
37	THOMAS & BETTS	TY4X4WPG6	4"W X 4"H WIDE SLOT WIRING DUCT, 6FT, GRAY	2
38	THOMAS & BETTS	TY1CPG6	1"W WIRING DUCT COVER, 6FT, GRAY	3
39	THOMAS & BETTS	TY2CPG6	2"W WIRING DUCT COVER, 6FT, GRAY	2
40	THOMAS & BETTS	TY3CPG6	3"W WIRING DUCT COVER, 6FT, GRAY	0
41	THOMAS & BETTS	TY4CPG6	4"W WIRING DUCT COVER, 6FT, GRAY	2
42	HOFFMAN	A36P24-C0756	20U PANEL	3
43	HOFFMAN	P19RPP5UB	5U PANEL	2
44	HOFFMAN	P19RPP3UB	3U PANEL	1
45	DELL	POWEREDGE R740XD	CCTV SERVER	0
46	HARDING	DCC-S1M4-3030-S100-MDIP	DIGITAL COMMUNICATION CONTROLLER, 32 CHAN, 300 SERIES MCC CARD	1
47	HARDING	DCE-S100-3030-S1	DIGITAL COMMUNICATION EXPANDER, 32 CHAN	1
48	HARDING	PZE-110	PAGE ZONE EXPANDER	1
49	HARDING	ADM-SOF	DXL ADMINISTRATOR SOFTWARE	1
50	HARDING	QCB-120-1	3-WIRE AUDIO STATION CONNECTION BOARD	4
51	HARDING	QCB-120-2	2-WIRE AUDIO SWITCH CONNECTION BOARD	4
52	DITEK	DTK-RM12POES-DS-R7	TVSS FOR IP POE CAMERA, 12 PORTS, RACK MOUNT	1
53	SPECO	PMM-120A	120 WATT RMS PAGE AMPLIFIER	1
54	SPECO	PBMRK2	120 WATT PAGE AMP RACK EARS	1
55	TRIPPLITE	B021-000-19	RACK MOUNT KVM CONSOLE WITH 19" LCD	0
56	TRIPPLITE	PDUMH20	12 MULTI OUTLET PLUGSTRIP, 20A PLUG	1
57	TRIPPLITE	N252-048	CAT6 PATCH PANEL, 48-PORT	2
58	CISCO	CBS350-48FP-4X	CISCO 48-PORT POE 10G MANAGED SWITCH	2


PARTS LIST

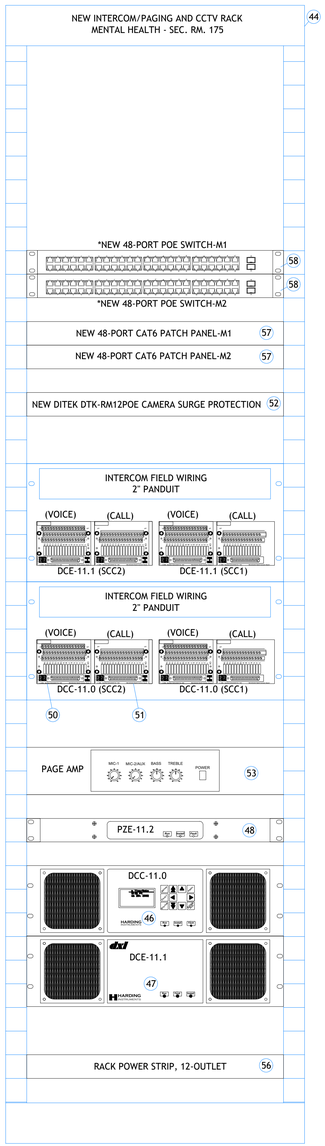

INTERCOM/PAGING, CCTV RACK - FRONT

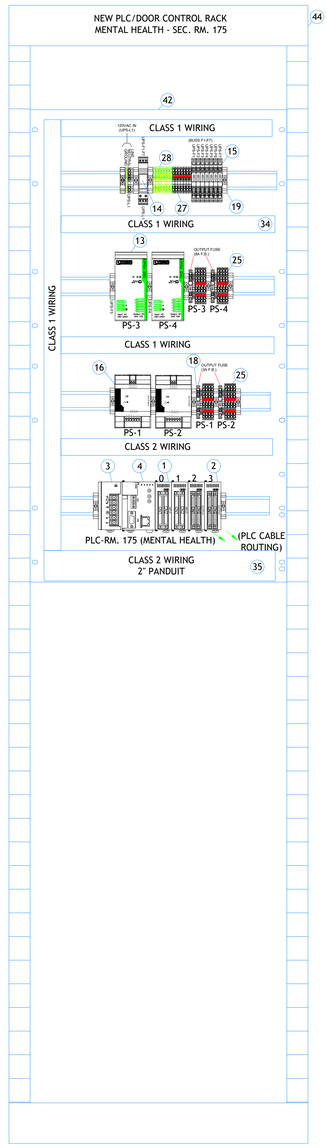

PLC/DOOR CONTROL RACK - FRONT

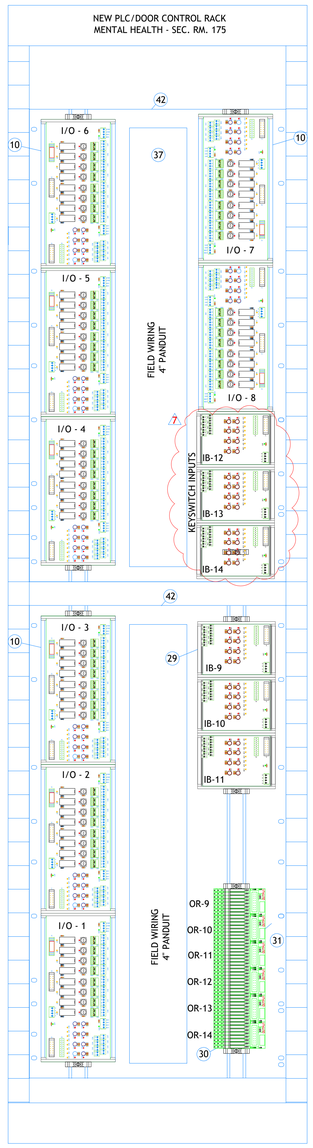

PLC/DOOR CONTROL RACK - REAR

1 RACK LAYOUTS - MENTAL HEALTH (RM. 175)
SCALE: N.T.S.

REVISION	DATE	DESCRIPTION	REVISION	DATE	DESCRIPTION	REVISION	DATE	DESCRIPTION
0	10 / 25 / 2023	SUBMITTAL	7	12 / 17 / 2024	ADDED LOCAL KEYSWITCHES: SLIDERS 100,138,140,150,122A,122B, 150A AND KICK RELEASE DOORS 106-112,115-119,123,125,130-131	X	XX / XX / XXXX	XXXXXX
1	12 / 05 / 2023	RESUBMITTAL	8	01 / 17 / 2025	RFI #297 (CARD READER 175S DELETED)			
2	05 / 14 / 2024	ASI #08 UPDATES	9	04 / 04 / 2025	RFI #316 (ADDED DOOR 174 CONTROL & INTERCOM)			
3	06 / 12 / 2024	RFI #202 UPDATES	10	06 / 15 / 2025	ADDED CAMERAS N166 AND N167			
4	07 / 02 / 2024	ASI #08-R1 UPDATES	11	08 / 25 / 2025	DESIGN CHANGES PER RFI 367			
5	08 / 26 / 2024	ASI #08-R2 UPDATES						
6	11 / 04 / 2024	RFI #259 UPDATES						

[redacted]

PROJECT
ARAPAHOE COUNTY DETENTION CENTER
ADDITION AND REMODEL
7375 S. POTOMAC ST.
CENTENNIAL, CO 80112

SHEET NAME
RACK LAYOUTS - MENTAL HEALTH (RM. 175)

SHEET NUMBER
SE402

REVISION
11