FLOOR PLAN GENERAL NOTES

1. DIMENSIONS INDICATED ARE TO FACE OF FINISH MATERIAL OF PARTITION OR WALL AND GRID LINES, UON
2. ALL DOOR FRAMES TO BE LOCATED 4" FROM PERPENDICULAR WALL, UON.

NOTE:
NO WORK AT AREAS IN
DIAGONAL HATCH

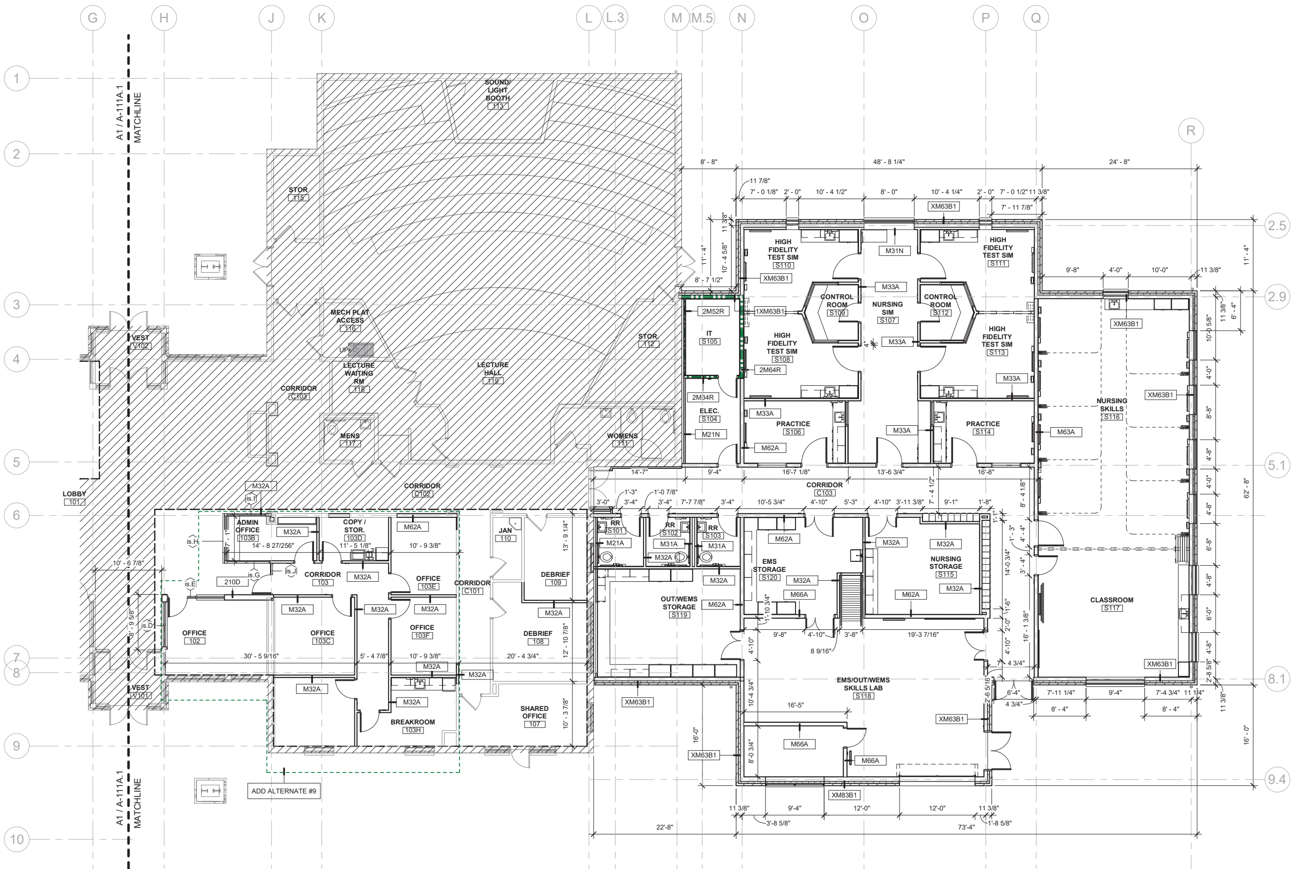
G
H
J
K
L
L.3
M
M.5
N
O
P
Q
R
1
2
3
4
5
6
7
8
9
10
2.5
2.9
5.1
8.1
9.4
A1 / A-111A.1
MATCHLINE
SOUND/ LIGHT BOOTH 113
STOR 115
MECH PLAT ACCESS 116
UP
LECTURE WAITING RM 118
LECTURE HALL 119
STOR. 112
VEST V102
CORRIDOR C103
MENS 117
WOMENS 111
LOBBY 101
CORRIDOR C102
ADMIN OFFICE 103B
COPY / STOR. 103D
CORRIDOR 103
OFFICE 103E
OFFICE 102
OFFICE 103C
OFFICE 103F
BREAKROOM 103H
CORRIDOR C101
JAN 110
DEBRIEF 109
DEBRIEF 108
SHARED OFFICE 107
VEST V101
ADD ALTERNATE #9
HIGH FIDELITY TEST SIM S110
HIGH FIDELITY TEST SIM S111
CONTROL ROOM S109
NURSING SIM S107
CONTROL ROOM S112
HIGH FIDELITY TEST SIM S108
HIGH FIDELITY TEST SIM S113
IT S105
ELEC. S104
PRACTICE S106
PRACTICE S114
NURSING SKILLS S116
CORRIDOR C103
RR S101
RR S102
RR S103
EMS STORAGE S120
NURSING STORAGE S115
OUT/WEMS STORAGE S119
CLASSROOM S117
EMS/OUT/WEMS SKILLS LAB S118
8' - 8"
48' - 8 1/4"
24' - 8"
62' - 8"
22'-8"
73'-4"
16'-5"
16'-0"
16' - 0"

A1 FIRST FLOOR DIMENSION PLAN - AREA B

A-200A-111B.1 1/8" = 1'-0"

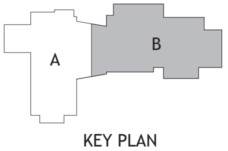

KEY PLAN

ARCHITECT
Hord Coplan Macht, Inc.
1800 Wazee Street, Suite 450
Denver, CO 80202
p. 303.607.0977
URL: www.hcm2.com

COLORADO MOUNTAIN COLLEGE
BRECKENRIDGE CAMPUS
ADDITION/RENOVATION

107 Denison Placer Road
Breckenridge, CO 80424

hord | coplan | macht
ARCHITECTURE
LANDSCAPE ARCHITECTURE
PLANNING
INTERIOR DESIGN

GWEN G. GILLEY
400629
02/10/2022

No.	Date	Revision

Project Name
BRECKENRIDGE CAMPUS ADDITION/RENOVATION
Project Number
221171
Date (YYYY/MM/DD)
2022/02/10
Drawn By TG
Checked By HRM
Drawing
FIRST FLOOR DIMENSION PLAN - AREA B

A-111B.1

100% CONTRACT DOCUMENTS

© Hord Coplan Macht, Inc.