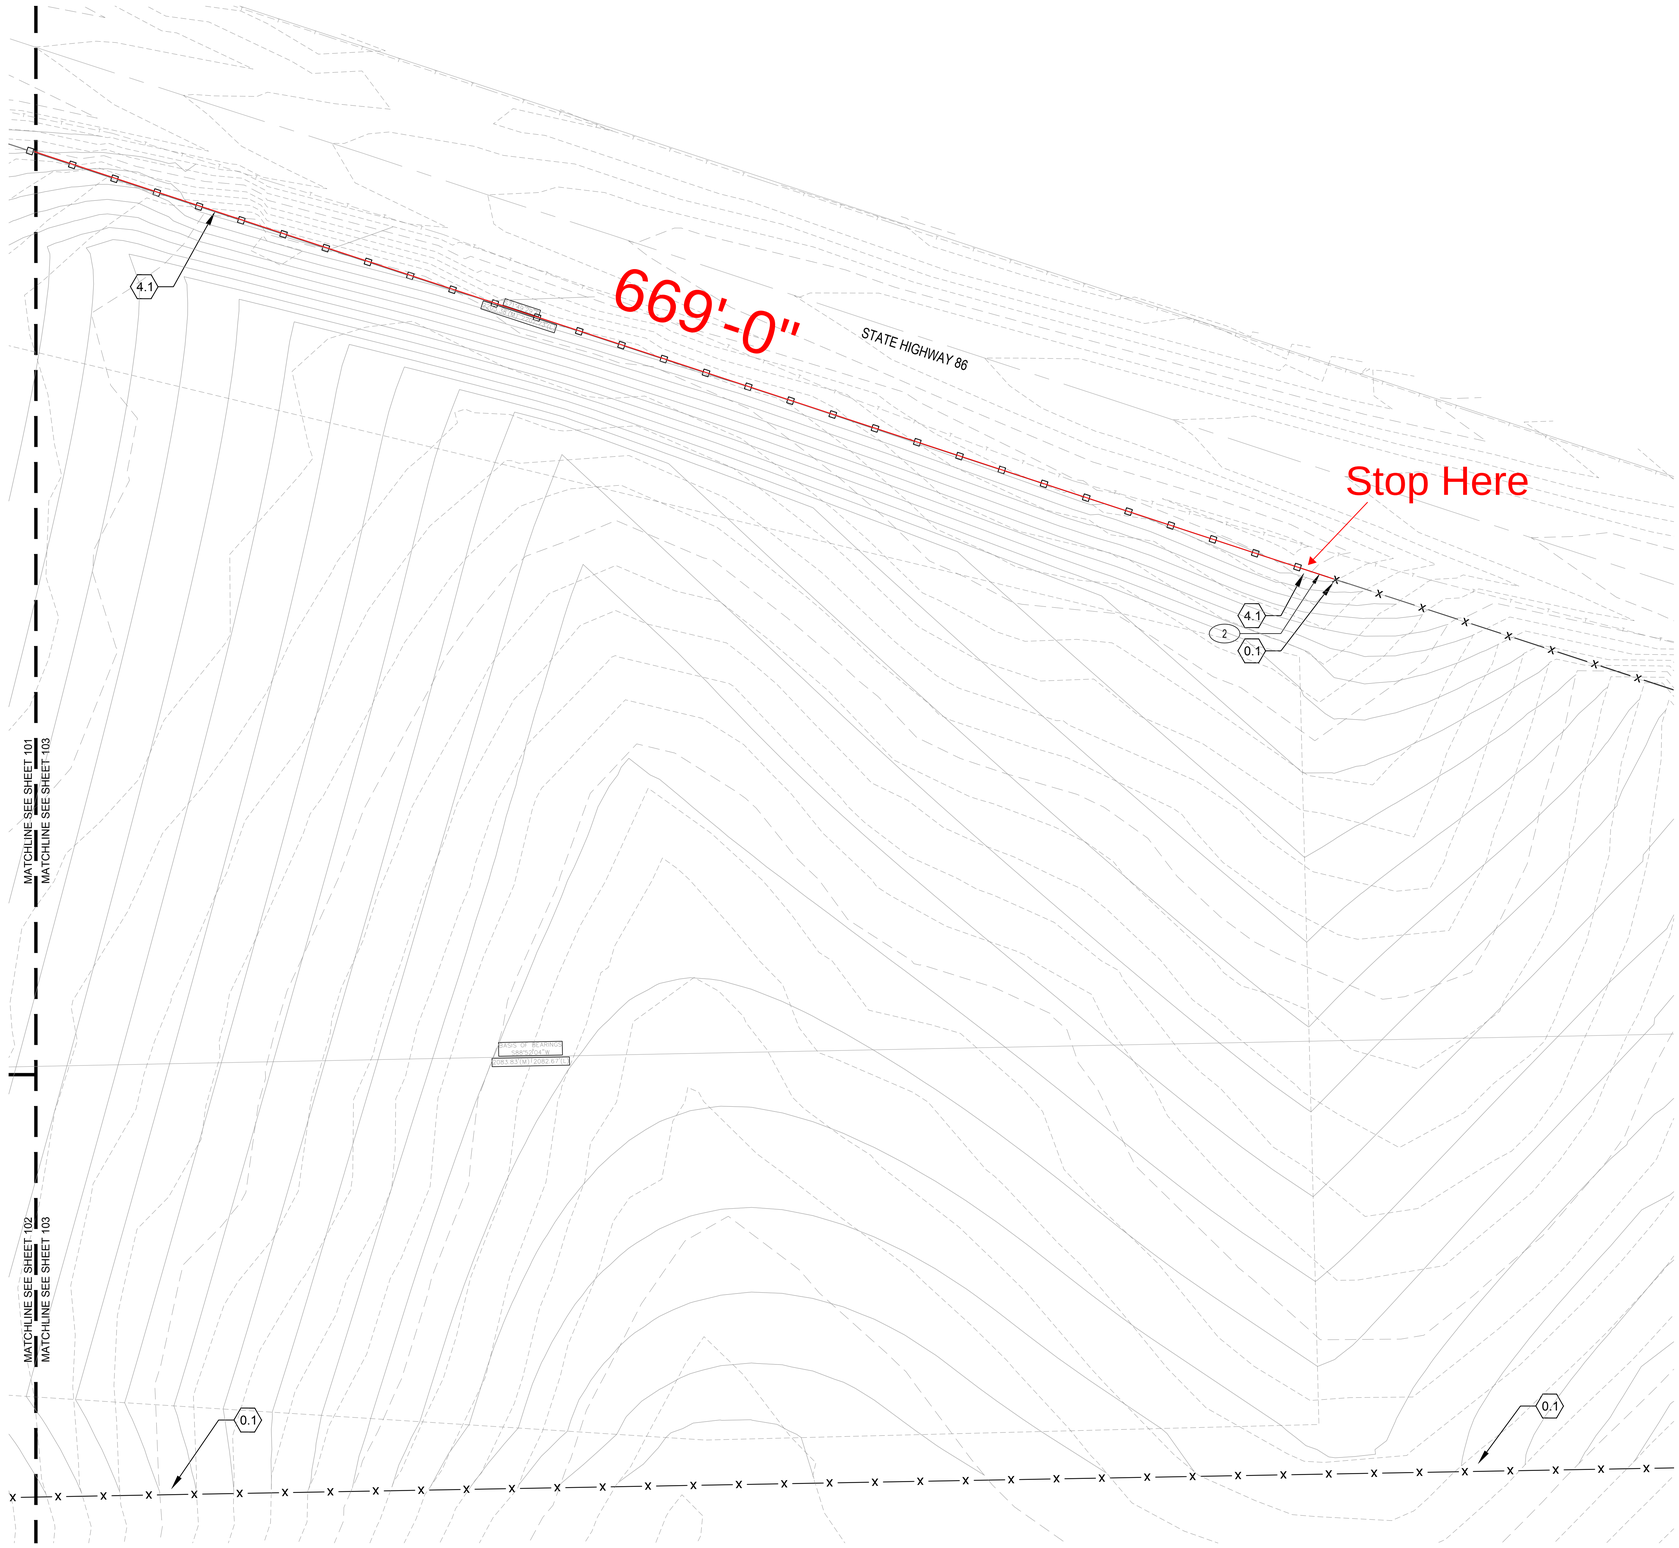


A LANDSCAPE SITE PLAN
SCALE: 1" = 30'

LEGEND

- RECYCLED ASPHALT PAVING RE: CIVIL
- CONCRETE PAVING RE: CIVIL/STRUCTURAL
- COBBLE MULCH - 1.5"
- COBBLE MULCH - 2-6"
- 6' HT. CHAINLINK FENCING
- CHAINLINK GATE
- EX FENCING
- PROPERTY LINE

SITE DETAIL KEYNOTES

0.0	**EXISTING CONDITIONS**		**DETAIL**
	0.1	EXISTING FENCING	N/A
1.0	**PAVING & SURFACING**		**DETAIL**
	1.1	RECYCLED ASPHALT	RE: CIVIL
	1.2	CONCRETE	RE: CIVIL
	1.3	CONCRETE	RE: STRUCTURAL
	1.4	COBBLE MULCH - 1.5"	A/LS501
	1.5	COBBLE MULCH - 2-6"	A/LS501
2.0	**STEPS & RAMPS**		**DETAIL**
	2.1	THIS SECTION NOT USED	
3.0	**WALLS, CURBS & EDGERS**		**DETAIL**
	3.1	STEEL EDGER	B/LS501
4.0	**FENCING & GATES**		**DETAIL**
	4.1	CHAIN LINK FENCING - 6' HT	C/LS501
	4.2	CHAIN LINK CANTILEVER SLIDE GATE - 6' HT	D/LS501
	4.3	AUTOMATIC GATE MOUNTING POST	A/LS502
	4.4	AUTOMATIC GATE OPERATOR	F/LS501
	4.5	CHAIN LINK PEDESTRIAN GATE - 6' HT	C/LS502
5.0	**SITE FURNISHINGS & SIGNS**		**DETAIL**
	5.1	BOLLARD	E/LS501
6.0	**DRAINAGE**		**DETAIL**
	6.1	STORM DRAIN INLET	RE:CIVIL
7.0	**SITE LIGHTING & ELECTRICAL**		**DETAIL**
	7.1	THIS SECTION NOT USED	
8.0	**PLANTING & LANDSCAPE**		**DETAIL**
	8.1	DECIDUOUS TREE	A-B/LP501
	8.2	SHRUB PLANTING	C/LP501
9.0	**MISCELLANEOUS**		
	9.1	FLAG POLE	RE: ARCH

SITE REFERENCE NOTES

1. REFER ELEC FOR ELECTRICAL AND TECHNOLOGY SERVICE. COORDINATE CONDUIT INSTALLATION WITH OTHER TRADES.
2. REMOVE EXISTING FENCING AT APPROXIMATE LOCATIO SHOWN. CONFIRM LIMITS OF FENCE REMOVAL WITH OWNERS REP PRIOR TO DEMOLITION.

CONSTRUCTION DOCUMENTS

Elbert County Public Works Road & Bridge Division Shop and Salt/Sand Shed

County Rd 134 & State Highway 86

Elbert County
215 Comanche Street
Kiowa, CO 80117

WOLD ARCHITECTS AND ENGINEERS
1553 Platte Street, Suite 201
Denver, Colorado 80202
woldac.com | 303 928 8800

Flow Design Collaborative
301 w 45th Ave
Denver, Colorado 80216

I hereby certify that this plan, specification or report was prepared by me or under my direct supervision and that I am a duly Licensed **Landscape Architect** under the laws of the State of **Colorado**

License Number: **Jay Henke 000917** Date

Revisions		
Description	Date	Num

Comm: **215017**
Date: **05/20/2022**
Drawn: **JB**
Check: **JH**

LANDSCAPE SITE PLAN

Scale:

LS103