CASE NO. MP-22-0029

ELBERT COUNTY PUBLIC WORKS MINOR PLAT

PART OF SECTION 21, T. 8 S, R. 63 W, 6TH P.M.
COUNTY OF ELBERT, STATE OF COLORADO

ELBERT COUNTY PUBLIC WORKS

THIS MINOR PLAT WAS REVIEWED AND APPROVED BY ELBERT COUNTY PUBLIC WORKS ON THE DAY OF JAN 2023 A.D.

DIRECTOR, ELBERT COUNTY PUBLIC WORKS

ELBERT COUNTY ENGINEERING:

THIS MINOR PLAT WAS APPROVED BY THE ELBERT COUNTY ENGINEER ON THE 24 DAY OF JAN., 2023 A.D.

ELBERT COUNTY ~~ENGINEER~~ DPW DIRECTOR

ELBERT COUNTY COMMUNITY & DEVELOPMENT SERVICES:

THIS MINOR PLAT IS APPROVED BY ELBERT COUNTY COMMUNITY & DEVELOPMENT SERVICES THIS 26 DAY OF January, 2023. A.D.

DIRECTOR COMMUNITY & DEVELOPMENT SERVICES

ORG. FEB 13, 1874

CLERK AND RECORDER'S CERTIFICATE

STATE OF COLORADO)
)SS
COUNTY OF ELBERT)

I HEREBY CERTIFY THAT THIS MINOR PLAT WAS FILED IN MY OFFICE ON THIS 26TH DAY OF JANUARY 2023, AD, AT 3:24 A.M. [✓ P.M.] AND WAS RECORDED PER RECEPTION NUMBER 624837.

BOOK 13, PAGE 211.

624837 B: 13 P: 211 PLAT
01/26/2023 03:24:51 PM Page: 1 of 1 R 0.00 D
Rhonda Braun Recorder, Elbert County, Co

Sheryl Borden, Deputy Clerk
COUNTY CLERK AND RECORDER

ACCEPTANCE OF COUNTY COMMISSIONERS:

THIS MINOR PLAT WAS ACCEPTED BY THE ELBERT COUNTY COMMISSIONERS, ON THE 24th DAY OF JANUARY, 2023.

CHAIR, BOARD OF COUNTY COMMISSIONERS

FIRE PROTECTION DISTRICT

THIS MINOR PLAT WAS REVIEWED AND APPROVED BY KIOWA FIRE PROTECTION DISTRICT ON THE 26th DAY OF January, 2023.

GERALD L. LAMANSKY /
FIRE MARSHAL,

KIOWA
FIRE PROTECTION DISTRICT

OWNERS CERTIFICATE

I, CHRISTOPHER A. RICHARDSON AS OWNER OF THE LAND AFFECTED BY THIS MINOR PLAT, ACCEPT AND APPROVE ALL CONDITIONS SET FORTH HEREIN.

OWNER: ELBERT COUNTY COMMISSIONERS DATE: 25 JAN '23

STATE OF Colorado)
) SS
COUNTY OF Elbert)

THE FOREGOING DEDICATION WAS ACKNOWLEDGED BEFORE ME THIS 25th DAY OF January 20 23, BY (NAME OF INDIVIDUAL OR AUTHORIZED PERSON [SEE BELOW]).
WITNESS MY HAND AND OFFICIAL SEAL.

SEAL Tiffany A. Hermes
NOTARY PUBLIC

MY COMMISSION EXPIRES: July 29. 2025

TIFFANY A HERMES
NOTARY PUBLIC
STATE OF COLORADO
NOTARY ID 20134019093
MY COMMISSION EXPIRES JULY 29, 2025

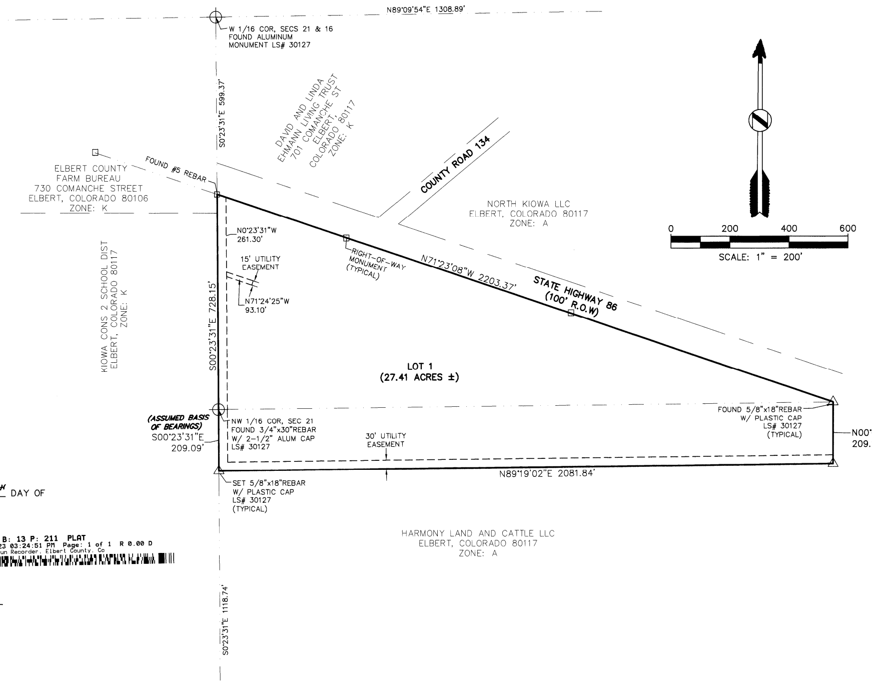

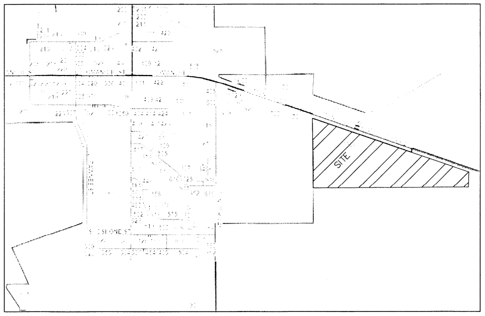

VICINITY MAP
NOT TO SCALE

STATEMENT:

LINEAL UNITS ARE IN FEET.

PROPERTY DESCRIPTION

A PARCEL OF LAND IN THE SOUTH HALF OF THE NORTH HALF OF SECTION 21, TOWNSHIP 8 SOUTH, RANGE 63 WEST OF THE 6TH P.M.,, LYING SOUTH OF STATE HIGHWAY NO. 86, ELBERT COUNTY, COLORADO, BEING MORE PARTICULARLY DESCRIBED AS FOLLOWS:

BEGINNING AT THE NORTHWEST SIXTEENTH CORNER OF SAID SECTION 21, AND CONSIDERING THE WEST LINE OF THE EAST HALF OF THE NORTHWEST QUARTER OF SAID SECTION 21 TO BEAR S00°23'31"E, WITH ALL BEARINGS CONTAINED HEREIN RELATIVE THERETO;

THENCE S00°23'31"E, ALONG SAID WEST LINE, A DISTANCE OF 209.09 FEET; THENCE N89°19'02"E, A DISTANCE OF 2081.84 FEET; THENCE N00°00'00"W, A DISTANCE OF 209.10 FEET TO A POINT ON THE SOUTH LINE OF STATE HIGHWAY 86; THENCE N71°23'08"W, ALONG THE SOUTH LINE OF STATE HIGHWAY 86, A DISTANCE OF 2203.37 FEET; THENCE S00°23'31"E, A DISTANCE OF 728.15 FEET TO THE NORTHWEST SIXTEENTH CORNER, AND THE POINT OF BEGINNING

SAID PARCEL CONTAINING 27.41 ACRES, MORE OR LESS.

ALSO KNOWN BY STREET ADDRESS 11330 STATE HIGHWAY 86, KIOWA CO 80117

DISCLAIMER: PLEASE NOTE THAT SURVEYING IS AN INEXACT SCIENCE AND IS SUBJECT TO A CERTAIN DEGREE OF INACCURACY AND OPINION.

BASIS OF BEARINGS:

CONSIDERING THE WEST LINE OF THE EAST HALF OF THE NORTHWEST QUARTER OF SEC 21 TO HAVE AN ASSUMED BEARING OF S00°23'31"E AND MONUMENTED AS SHOWN HEREON.

"NOTICE: According to Colorado law you must commence any legal action based upon any defect in this survey within three years after you first discover such defect. In no event may any action based upon any defect in this survey be commenced more than ten years from the date of the certification shown hereon."

OWNERS:

ELBERT COUNTY
COMMISSIONERS
215 COMANCHE
STREET

ZONING:

PROPOSED: INDUSTRIAL
EXISTING: AGRICULTURE
& RESIDENTIAL
AGRICULTURE

SURVEYOR'S CERTIFICATE

I, KEITH WESTFALL, A REGISTERED LAND SURVEYOR IN THE STATE OF COLORADO, DO HEREBY CERTIFY THAT THE SURVEY OF ELBERT COUNTY MINOR PLAT WAS MADE UNDER MY DIRECT SUPERVISION AND THE ACCOMPANYING PLAT ACCURATELY AND PROPERLY SHOWS SAID SUBDIVISION.

1/13/23

KEITH WESTFALL, COLORADO PLS #30127
FOR AND ON THE BEHALF OF
HIGH PRAIRIE SURVEY COMPANY

UTILITY EASEMENT ACKNOWLEDGMENT

THOSE PORTIONS OF REAL PROPERTY WHICH ARE LABELED AS UTILITY EASEMENTS ON THIS PLAT, WHETHER PRIVATE OR PUBLIC, ARE HEREBY DEDICATED, FOR THE INSTALLATION AND MAINTENANCE OF UTILITIES AND DRAINAGE FACILITIES, INCLUDING, BUT NOT LIMITED TO ELECTRIC LINES, GAS LINES, TELEPHONE LINES, CABLE T.V.; TOGETHER WITH THE RIGHT TO TRIM INTERFERING TREES AND BRUSH TOGETHER WITH A PERPETUAL RIGHT OF INGRESS AND EGRESS FOR INSTALLATION, MAINTENANCE, AND REPLACEMENT OF SUCH LINES; SAID EASEMENTS AND RIGHT TO BE UTILIZED IN A RESPONSIBLE AND PRUDENT MANNER, SUBJECT TO UTILITY PLACEMENT PERMITTING PROCEDURES FROM ELBERT COUNTY.

DEDICATION STATEMENT:

KNOW ALL MEN BY THESE PRESENTS THAT THE UNDERSIGNED, BEING THE OWNERS OF THE LAND DESCRIBED BELOW, HAVING LAID OUT AND PLATTED THE SAME INTO LOTS AND EASEMENTS AS SHOWN HEREON UNDER THE NAME AND STYLE OF ELBERT COUNTY PUBLIC WORKS MINOR PLAT

THE UTILITY EASEMENTS SHOWN HEREON ARE DEDICATED FOR PUBLIC UTILITIES AND DO BY THESE PRESENTS, OF OUR OWN FREE WILL AND VOLUNTARY WITHOUT COERCION, THREAT OR BUSINESS COMPULSION, DO HEREBY CONVEY SAID EASEMENTS TO THE COUNTY OF ELBERT, STATE OF COLORADO FOR EASEMENT PURPOSES.

COUNTY OF ELBERT
STATE OF COLORADO

REFERENCE DWG:

DATE:	REVISIONS:
06/28/2022	REVISED VC MAP
06/30/2022	REVISED COMMENTS PER GREG
11/16/2022	REVISED COMMENTS PER STEVEN
12/21/2022	REVISED 2ND ROUND REDLINES

High Prairie Survey Co.
LAND SURVEYING CONSTRUCTION STAKING
OIL AND GAS SURVEYING
303-621-8672 FAX 303-621-7749
P.O. BOX 384
KIOWA, COLORADO 80117

SCALE	DATE	DRAWN BY
1"=200'	03/03/2022	CRR

TITLE
ELBERT COUNTY PUBLIC WORKS MINOR PLAT
PART OF SEC. 21, T8S, R63W, 6TH P.M.
ELBERT COUNTY, STATE OF COLORADO

CLIENT
ELBERT COUNTY COMMISSIONERS

SHEET 1 OF 1
JOB NUMBER 21148-MP

B/3 P 211