Westminster Public Schools

2026 Bond Projects

ECC Renovations
8030 Irving St. Westminster, CO 80031
DAO No.: 2025-033
100% Construction Documents
September 25, 2026



DRAWING INDEX

GENERAL	
Cover	Cover Sheet
G0.0	Standard Symbols, Abbreviations & General Notes
G0.1	Building Code Data
ARCHITECTURE	
AD1.0	Partial Demolition Plan
AD2.0	Demolition Exterior Elevations
A1.0	First Floor Plans
A2.0	Exterior Elevations
A4.0	Wall Sections, Interior Elevations
A8.0	Details, Door Schedule
STRUCTURAL	
S1.0	General Notes, Details, And Plan
PLUMBING	
P1.0	First Floor Plumbing Plan, Details, And General Notes

NOTE: CIVIL DRAWINGS ARE NOT ISSUED AT THIS TIME. CIVIL DRAWINGS WILL BE ISSUED IN A FORTHCOMING ADDENDUM

DAO ARCHITECTURE

7230 Meade St.
Westminster, CO 80030

Phone: 720.273.0431
Email: dan@daoarch.com
Web: www.daoarch.com

OWNER:
WESTMINSTER PUBLIC SCHOOLS
7002 RALEIGH STREET
WESTMINSTER, CO 80030
CONTACT: DON CIANCIO
PHONE : 720.542.5100

ARCHITECT:
DAO ARCHITECTURE
7230 MEADE ST
WESTMINSTER, CO 80030
CONTACT: DAN ORECCHIO
PHONE : 720.273.0431

STRUCTURAL ENGINEER:
TJF STRUCTURAL
5995 GREENWOOD VILLAGE PLAZA BLVD, STE. 120
GREENWOOD VILLAGE, CO 80111
CONTACT: TROY FORNSTROM
PHONE: 303.618.4555

PLUMBING ENGINEER:
THE BALLARD GROUP
2525 S WADSWORTH BLVD, STE. 200
LAKEWOOD, CO 80227
CONTACT: NATE RUST
PHONE: 303.988.4514

CIVIL ENGINEER:
CONTERRA ENGINEERING
242 LINDEN STREET, No. 5943
FORT COLLINS, CO 80524
CONTACT: ERIK NAKOS
PHONE: 970.391.7862

Westminster Public Schools

2026 Bond Projects - ECC Renovations
8030 Irving St. Westminster, CO 80031

DAO No.: 2025-033

September 25, 2026

CONSTRUCTION DOCUMENTS

Cover

Autodesk Docs://WPS 2026 Bond Projects - ECC Renovations/WPS ECC (Revit 2026).rvt
9/25/2026 8:01:16 AM

MATERIALS SYMBOLS

EARTHWORKS

EARTH NON-COMPACTED
EARTH COMPACT/FILL
GRAVEL/POROUS FILL

CONCRETE

CONCRETE
PRECAST CONCRETE
SAND/MORTAR/PLASTER

METAL

ALUMINUM
BRASS/BRONZE
STEEL

MASONRY

CONCRETE BLOCK
COMMON/FACE BLOCK
FIRE BRICK
STRUCTURAL FACING TILE

STONE

BLUESTONE/SLATE/ SOAPSTONE/FLAGGING
LIMESTONE
RUBBLE

WOOD

FINISH
ROUGH
SHIM
PLYWOOD

GLASS

GLASS
STRUCTURAL
GLASS BLOCK

INSULATION

BATT/LOOSE FILL
RIGID
SPRAY/FOAM

FINISHES

ACOUSTICAL TILE
CARPET AND PAD
CERAMIC TILE
GYPSUM WALLBOARD
TECTUM

PARTITION INDICATIONS

CAST-IN-PLACE CONCRETE
CONCRETE MASONRY
METAL STUD
WOOD STUD

ELEVATION INDICATIONS

BRICK
CERAMIC/ PORCELAIN TILE
CONCRETE/ PLASTER/GPDW
CONCRETE MASONRY UNIT
SHEET METAL
SHINGLES/SIDING

REFERENCE SYMBOLS

1 / A1.0 — SIM — DETAIL OR SECTION NUMBER / SHEET ON WHICH IT IS FOUND
No. / Sht. — SECTION REFERENCE
No. / Sht. — DETAIL REFERENCE
No. / Sht. — WALL SECTION REFERENCE
No. / Sht. — No. / Sht. — BUILDING SECTION REFERENCE
Sht. — No. — ELEVATION REFERENCE
ROOM NAME / 101 — ROOM IDENTIFIER
1t — WINDOW/OPENING IDENTIFIER
1A101 — DOOR/OPENING IDENTIFIER
1 — EXISTING GRID LINE
Level 100'-0" — ELEVATION REFERENCE
1i — WALL TYPE REFERENCE
MATCH LINE
DEMOLITION INDICATOR
1 — REVISION INDICATOR

GENERAL NOTES

1. THE GENERAL CONTRACTOR SHALL VERIFY ALL EXISTING DIMENSIONS AND CONDITIONS SHOWN ON PLANS PRIOR TO COMMENCEMENT OF THE WORK. IT SHALL BE THE CONTRACTORS RESPONSIBILITY TO COORDINATE INSTALLATION OF NEW WORK WITHIN THESE EXISTING CONDITIONS. ANY DEVIATIONS IN EXISTING CONDITIONS OR DIMENSIONS INDICATED SHALL BE COORDINATED WITH THE ARCHITECT AND OWNER IN ORDER TO MODIFY PLANS ACCORDINGLY
2. ALL DISCIPLINES SHALL BE RESPONSIBLE FOR THEIR SCOPE OF WORK. THIS WORK IS TO BE SCHEDULED AND COMPLETED WITH THE GENERAL CONTRACTOR'S FULL KNOWLEDGE.
3. ALL HOT WORK ACTIVITIES (I.E. USING HEAT GUNS, SOLDERING, BRAZING, WELDING, GRINDING, METAL CUTTING, ETC.) OR OTHER ACTIVITIES INVOLVING FLAMES OR SPARKS SHALL BE PRECEDED BY OBTAINING AN APPROVED HOT WORK PERMIT. (IF HOT WORK REQUIRED)
4. THE PROJECT STAGING AREA / CONSTRUCTION ACTIVITIES SHALL NOT CAUSE THE OBSTRUCTION OF PATHS OF EGRESS INSIDE THE BUILDING, BLOCK EXIT DISCHARGE FROM THE BUILDING, OR IMPEDE EMERGENCY VEHICLE ACCESS TO THE BUILDING. CORRIDORS MAY NOT BE USED AS STAGING AREAS OR AS AREAS FOR DEBRIS COLLECTION.
5. ALL NECESSARY MEASURES SHALL BE TAKEN TO PREVENT THE NUISANCE ACTUATION OF ANY NEARBY SMOKE OR DUCT DETECTORS BY CONSTRUCTION ACTIVITIES THAT CREATE DUST OR FUMES INSIDE THE BUILDING.
6. THE CONTRACTOR SHALL NOT HANDLE OR DISABLE ANY FIRE SYSTEMS DEVICES. ONLY BUILDING FIRE SYSTEMS PERSONNEL MAY HANDLE OR DISABLE EXISTING FIRE SYSTEMS. ANY OUTAGES REQUIRED FOR THE EXISTING FIRE SYSTEMS SHALL BE PERFORMED ACCORDING TO THE BUILDING PROCEDURES.
7. THE ARCHITECT ASSUMES NO RESPONSIBILITY FOR THE DETECTION OR REMOVAL OF ANY HAZARDOUS MATERIALS, INCLUDING, BUT NOT LIMITED TO, ASBESTOS IN ANY FORM. PARTIES RESPONSIBLE FOR DEMOLITION SHALL NOTIFY THE OWNER IMMEDIATELY OF ANY SUSPECTED MATERIALS.
8. CONTRACTOR TO PROVIDE FINAL CLEANING SERVICES IN ALL CLASSROOMS PRIOR TO PROJECT COMPLETION, AND NO LATER THAN THE DATE THAT THE OWNER OCCUPIES THE CLASSROOMS, AHEAD OF STAFF AND STUDENTS RETURNING TO THE SCHOOL

PROJECT DESCRIPTION

THIS PROJECT ENTAILS THE REPLACEMENT OF WATERPROOFING AND INSTALLATION OF FOUNDATION DRAINAGE SYSTEMS AT THE EARLY CHILDHOOD CENTER IN WESTMINSTER, COLORADO. IN ORDER TO MITIGATE WATER INTRUSION INTO A PORTION OF THE EXISTING SCHOOL. EXTERIOR GRADE AND FLATWORK WILL BE REMOVED AND RE-INSTALLED AS REQUIRED TO REPLACE THE FAILING EXISTING DAMPPROOFING.

ADDITIONAL WORK WILL INCLUDE STAINING THE EXTERIOR BRICK FACADES OF THE EXISTING BUILDING, AND REPLACING AND/OR PAINTING EXISTING METAL AND TRIM. AN NEW DOOR WILL BE PROVIDED AT THE NORTH CORNER OF THE BUILDING. AN ADJACENT EXISTING DOOR WILL BE DEMOLISHED AND THE OPENING INFILLED. SEVERAL ABANDONED AIR LOUVERS WILL BE DEMOLISHED, AND THE OPENINGS INFILLED WITH BRICK THAT MATCHES THE EXISTING BRICK STRUCTURE. INTERIOR SPACES WILL BE RECONFIGURED ONLY AS REQUIRED TO ALLOW FOR THE NEW DOOR.

THE EXISTING BUILDING HEIGHT, AREAS, AND FIRE PROTECTION SYSTEMS ARE EXISTING-TO-REMAIN AND WILL NOT BE IMPACTED AS PART OF THIS WORK.


NO MECHANICAL, ELECTRICAL, OR TECHNOLOGY SCOPE ARE ANTICIPATED AS PART OF THIS WORK.

STANDARD ABBREVIATIONS

A/E	ARCHITECT/ENGINEER	CONN	CONNECTION	GALV	GALVANIZED	MO	MASONRY OPENING
AB	ANCHOR BOLT	CONSTR	CONSTRUCTION	GB	GRAB BAR	MOD	MODULE
ABBR	ABBREVIATE	CONT	CONTINUOUS	GDRL	GUARD RAIL	MTD	MOUNTED
ABV	ABOVE	CONTR	CONTRACTOR	GENL	GENERAL	MTG	MEETING
AC	AIR CONDITIONING	COORD	COORDINATE	GENL CONTR	GENERAL CONTRACTOR	MTL	METAL
ACID RES	ACID RESISTANT	CORR	CORRIDOR	GFI	GROUND FAULT INTERRUPTER	MTR	MORTAR
ACOUS	ACOUSTICAL	COV PL	COVER PLATE	GL	GLASS	MULL	MULLION
ACOUS INSUL	ACOUSTICAL INSULATION	CPRS	COMPRESSIBLE	GL BLK	GLASS BLOCK	MULT	MULTIPLE
ACOUS PNL	ACOUSTICAL PANEL	CPT	CARPET	GLU LAM	GLUE LAMINATED	MVBL	MOVABLE
ACOUS PLAS	ACOUSTICAL PLASTER	CRCMF	CIRCUMFERENCE	GLZ	GLAZING	N	NORTH
ACOUS TILE	ACOUSTICAL TILE	CRS	COLD ROLLED STEEL	GLZ CMU	GLAZED CONCRETE MASONRY UNIT	N/A	NOT APPLICABLE
ACT	ACTUAL	CSG	CASING	GND	GROUND	NEG	NEGATIVE
AD	AREA DRAIN	CSK	COUNTERSUNK	GPDW	GYPSUM DRY WALL	NF	NEAR FACE
ADC	AUTOMATIC DOOR CLOSER	CSMT	CASEMENT	GR BM	GRADE BEAM	NIC	NOT IN CONTRACT
ADDL	ADDITIONAL	CSWK	CASEWORK	GR	GRADE	NO	NUMBER
ADDM	ADDENDUM	CT	CERAMIC TILE	GRTG	GRATING	NOM	NOMINAL
ADJ	ADJUSTABLE	C TV	CABLE TELEVISION	GUT	GUTTER	NS	NEAR SIDE
ADJC	ADJACENT	CUB	CUBICLE	GYP	GYPSUM	NTS	NOT TO SCALE
AF	ACCESS FLOOR	CUR	CURRENT	GYP PLAS	GYPSUM PLASTER	O/O	OUT TO OUT
AFF	ABOVE FINISHED FLOOR	CW	COLD WATER	H	HIGH	OA	OVERALL
AFG	ABOVE FINISHED GRADE	DBL GLZ	DOUBLE GLAZING	H&CW	HOT & COLD WATER	OC	ON CENTER
AFS	ABOVE FINISHED SLAB	DEPT	DEPARTMENT	HB	HOSE BIBB	OD	OUTSIDE DIAMETER
AGGR	AGGREGATE	DET	DETAIL	HC	HOLLOW CORE	OD	OVERFLOW DRAIN
AHR	ANCHOR	DF	DRINKING FOUNTAIN	HC	HANDICAP	OF	OUTSIDE FACE
AHU	AIR HANDLING UNIT	DF	DRAPERY FABRIC	HCMU	HOLLOW CONCRETE MASONRY UNIT	OFCI	OWNER FURNISHED CONTRACTOR INSTALL
ALD	ALUMINUM DOOR	DFR	DOOR FRAME	HD	HEAVY DUTY	OFF	OFFICE
ALM	ALARM	DH	DOUBLE HUNG	HDJT	HEAD JOINT	OFOI	OWNER FURNISHED OWNER INSTALLED
ALT	ALTERNATE	DIA	DIAMETER	HDBD	HARDBOARD	OH	OVERHEAD
ALUM	ALUMINUM	DIM	DIMENSION	HDR	HEADER	OHD	OVERHEAD DOOR
AMB	AMBIENT	DIST	DISTANCE	HDWD	HARDWOOD	OPER	OPERABLE
AMPL	AMPLIFIER	DIV	DIVIDER	HGT	HEIGHT	OPNG	OPENING
AMT	AMOUNT	DIW	DEIONIZED WATER	HLB	HORIZONTAL LOUVER BLINDS	OPP	OPPOSITE
ANN	ANNUNCIATOR	DJ	DOUBLE JOIST	HM	HOLLOW METAL	OPT	OPTIONAL
ANOD	ANODIZED	DL	DRAPERY LINER	HMD	HOLLOW METAL DOOR	ORIG	ORIGINAL
ANT	ANTENNA	DMPF	DAMPPROOFING	HMF	HOLLOW METAL FRAME	OVHD	OVERHEAD
AP	ACCESS PANEL	DN	DOWN	HNDRL	HAND RAIL	OXY	OXYGEN
APPX	APPENDIX	DO	DITTO	HO	HOLD-OPEN	OZ	OUNCE
ARCH	ARCHITECT(URAL)	DR	DOOR	HORIZ	HORIZONTAL	PC	PRECAST
ASB	ASBESTOS	DR CLSR	DOOR CLOSURE	HR	HOUR	PAR	PARALLEL
ASC	ABOVE SUSPENDED CEILING	DS	DOWNSPOUT	HS	HIGH STRENGTH	PARG	PARGING
ASPH	ASPHALT	DST	DOOR STOP	HSB	HIGH STRENGTH BOLT	PB	PANIC BAR
ASYM	ASYMMETRICAL	DT	DRAIN TILE	HTG	HEATING	PBD	PARTICLE BOARD
AV	AUDIO VISUAL	DUPL	DUPLICATE	HVAC	HEATING, VENTILATION, AIR CONDITIONING	PC	PORTLAND CEMENT
AVE	AVENUE	DVTL	DOVETAIL	HW	HOT WATER	PCPLAS	PORTLAND CEMENT PLASTER
AWC	ACOUSTICAL WALL COVERING	DW	DISHWASHER	HYD	HYDRANT	PED	PEDESTAL
AWP	ACOUSTICAL WALL PANEL	DWG	DRAWING	ID	INSIDE DIAMETER	PERF	PERFORATED
B&B	BALLED AND BURLAPPED	DWL	DOWEL	IF	INSIDE FACE	PERIM	PERIMETER
BAF	BAFFLE	DWR	DRAWER	INCAND	INCANDESCENT	PERM	PERMANENT
BAL	BALANCE	DWTR	DUMBWAITER	INL	INLET	PERP	PERPENDICULAR
BB	BULLETIN BOARD	E	EAST	INSTL	INSTALLATION	PF	PANEL FABRIC
BC	BOTTOM OF CURB	EA	EACH	INSUL	INSULATION	PFP	PRE-FINISHED PANELS
BD	BOARD	EF	EACH FACE	INTR	INTERIOR	PGBD	PEGBOARD
BEV	BEVEL	EJ	EXPANSION JOINT	INV	INVERT	PH	PHASE
BF	BOTH FACES	EL	ELEVATION	INV EL	INVERT ELEVATION	PL	PLASTIC LAMINATE
BFF	BELOW FINISH FLOOR	ELEC	ELECTRICAL	JAN	JANITOR	PLAM	PLASTIC LAMINATE
BFP	BACKFLOW PREVENTER	ELEV	ELEVATOR	JC	JANITOR'S CLOSET	PLAS	PLASTER
BITUM	BITUMINOUS	EMER	EMERGENCY	JST	JOIST	PLAT	PLATFORM
BJT	BED JOINT	EMER SHR	EMERGENCY SHOWER	JT	JOINT	PLBG	PLUMBING
BL	BASE LINE	ENAM	ENAMEL	KB	KNEE BRACE	PLYWD	PLYWOOD
BLDG	BUILDING	ENCL	ENCLOSURE	KO	KNOCKOUT	POL	POLISHED
BLK	BLOCK	ENGR	ENGINEER	KOP	KNOCKOUT PANEL	POLY	POLYSTYRENE
BLKG	BLOCKING	ENTR	ENTRANCE	KPL	KICK PLATE	POLYISO	POLYISOCYANURATE
BLKHD	BULKHEAD	EO	ELECTRICAL OUTLET	KWY	KEYWAY	POS	POSITIVE
BLST	BALLAST	EP	ELECTRICAL PANEL	L	LEFT	PR	PAIR
BM	BEAM	EPS	EXPANDED POLYSTYRENE	LAB	LABORATORY	PREFAB	PREFABRICATED
BO	BOTTOM OF	EPX	EPOXY FLOOR	LAT	LAY-IN ACOUSTICAL TILE	PRELIM	PRELIMINARY
BOC	BACK OF CURB	EQL SP	EQUALLY SPACED	LAV	LAVATORY	PRKG	PARKING
BOW	BOTTOM OF WALL	EQ	EQUAL	LB	POUND	PROJ	PROJECT
BP	BASE PLATE	EQUIP	EQUIPMENT	LBR	LUMBER	PS	PROJECTION SCREEN
BRCG	BRACING	EQUIV	EQUIVALENT	LCMU	LIGHTWEIGHT CONCRETE MASONRY UNIT	PT	PAINT
BRDG JST	BRIDGING JOIST	ERECT	ERECTION	LD BRG	LOAD BEARING	PT	PORCELAIN TILE
BRG	BEARING	ESCAL	ESCALATOR	LDG	LANDING	PTN	PARTITION
BRG PL	BEARING PLATE	ESMT	EASEMENT	LF	LINEAR FOOT	PVC	POLYVINYL CHLORIDE
BRK	BRICK	EST	ESTIMATE	LG	LENGTH	PVG	PAVING
BRKT	BRACKET	EW	EACH WAY	LH	LEFT HAND	PVMT	PAVEMENT
BRS	BRASS	EXC	EXCAVATE	LHR	LEFT HAND REVERSE	PWR	POWER
BRZ	BRONZE	EXG	EXISTING	LIN	LINOLEUM	QT	QUARRY TILE
BS	BOTH SIDES	EXH HD	EXHAUST HOOD	LIQ	LIQUID	QTY	QUANTITY
BSMT	BASEMENT	EXH FN	EXHAUST FAN	LKR	LOCKER	QUAL	QUALITY
BTM	BOTTOM	EXP	EXPANSION	LKR RM	LOCKER ROOM	R	RISER
BUR	BUILT-UP ROOF	EXSP	EXPOSED	LL	LIVE LOAD	RAD	RADIUS
BW	BOTH WAYS	EXST	EXISTING	LNTL	LINTEL	RB	RUBBER BASE
BOW	BOTTOM OF WALL	EXST GR	EXISTING GRADE	LOC	LOCATION	RBR	RUBBER
C/C	CENTER TO CENTER	EXT	EXTERIOR	LONG	LONGITUDINAL	RC	REINFORCED CONCRETE
C&G	CURB AND GUTTER	EXTN	EXTENSION	LRG	LARGE	RCP	REINFORCED CONCRETE PIPE
CAB	CABINET	EIFS	EXTERIOR INSULATION & FINISH SYSTEM	LS	LUMP SUM	RD	ROOF DRAIN
CARP	CARPET	F BRK	FIRE BRICK	LT	LIGHT	REC	RECESSED
CAV	CAVITY	F/F	FACE TO FACE	LT WT	LIGHTWEIGHT	RECD	RECEIVED
CB	CATCH BASIN	FBD	FIBERBOARD	LTG	LIGHTING	RECPT	RECEPTACLE
CCTV	CLOSED CIRCUIT TELEVISION	FC	FIRE COATED	LVL	LEVEL	RECT	RECTANGULAR
CEM	CEMENT	FD	FLOOR DRAIN	LVR	LOUVER	REF	REFERENCE
CEM PLAS	CEMENT PLASTER	FDN	FOUNDATION	LW PLAS	LIGHTWEIGHT PLASTER	REINF	REINFORCEMENT
CER	CERAMIC	FEC	FIRE EXTINGUISHER CABINET	LWC	LIGHTWEIGHT CONCRETE	REM	REMOVABLE
CER TILE	CERAMIC TILE	FF	FACTORY FINISH	M	METER	REQD	REQUIRED
C FLG	COUNTER FLASHING	FFE	FINISH FLOOR ELEVATION	MAINT	MAINTENANCE	RESIL	RESILIENT
CH BD	CHALKBOARD	FGL	FIBERGLASS	MARB	MARBLE	RFM	RECESSED FLOOR MAT
CG	CORNER GUARD	FIN GR	FINISH GRADE	MAS	MASONRY	RFG	ROOFING
CHAN	CHANNEL	FIN FL	FINISH FLOOR	MATL	MATERIAL	RH	RIGHT HAND
CHFR	CHAMFER	FIN	FINISH	MAX	MAXIMUM	RHR	RIGHT HAND REVERSE
CHK	CHECK	FL	FLOWLINE	MB	MARKERBOARD	RND	ROUND
CI	CAST IRON	FLDG	FOLDING	MBR	MEMBER	RO	ROUGH OPENING
CIP	CAST IN PLACE	FLG	FLANGE	MC	METAL CLAD	RST	RUBBER STAIR TREAD
CIR	CIRCLE	FLR	FLOOR	MDF	MEDIUM DENSITY FIBERBOARD	RT	RUBBER TILE
CJ	CONTROL JOINT	FLR SK	FLOOR SINK	MDO	MEDIUM DENSITY OVERLOAD	RV	ROOF VENT
CL	CENTER LINE	FLR PL	FLOOR PLATE	ME	MATCH EXISTING	RVS	REVERSE
CLG	CEILING	FLR FIN	FLOOR FINISH	ME	MISCELLANEOUS EQUIPMENT	S	SOUTH
CLG DIFF	CEILING DIFFUSER	FLT GL	FLOAT GLASS	MECH	MECHANICAL	S	SEATING
CLG HT	CEILING HEIGHT	FLOUR	FLUORESCENT	MED	MEDIUM	SALV	SALVAGE
CLL	CONTRACT LIMIT LINE	FOC	FACE OF CONCRETE	MEMB	MEMBRANE	SB	SPLASH BLOCK
CLOS	CLOSET	FOM	FACE OF MASONRY	MEZZ	MEZZANINE	SC	SOLID CORE
CLR	CLEAR	FOS	FACE OF STUD	MFG	MANUFACTURING	SCH	SCHEDULE
CLSR	CLOSURE	FPL	FIREPLACE	MFR	MANUFACTURER	SCMU	SOLID CONCRETE MASONRY UNIT
CMPST	COMPOSITE	FPRF	FIREPROOFING	MH	MANHOLE	SCRN	SCREEN
CMU	CONCRETE MASONRY UNIT	FRM	FRAME	MIL	MILLIMETER	SD	STORM DRAIN
CNR	CORNER	FRNT	FRONT	MIN	MINIMUM	SECT	SECTION
CNTR	COUNTER	FS	FULL SIZE	MIR	MIRROR	SF	SYSTEMS FURNITURE
CO	CLEANOUT	FSP	FIRE STANDPIPE	MISC	MISCELLANEOUS	SGL	SINGLE
COL	COLUMN	FSTNR	FASTENER	MK	MARK	SHR	SHOWER
COMM	COMMERCIAL	FTG	FOOTING	MKRBD	MARKERBOARD	SHTHG	SHEATHING
COMPL	COMPLETE	FURR	FURRING	ML	MATCH LINE	SHVL	SHELVES
CONC	CONCRETE	FUT	FUTURE	MLC	METAL LABORATORY CASEWORK	SIM	SIMILAR
CONC FL	CONCRETE FLOOR	FXTR	FIXTURE	MLDG	MOLDING	SJ	SLIP JOINT
CONF	CONFERENCE	GA	GYPSUM ASSOCIATION	MLWK	MILLWORK	SK	SINK

SLA	SLATE
SLP	SLOPE
SLS	SUB-FLOOR LEVELING SYSTEM
SLV	SLEEVE
SM	SHEET METAL
SMLS	SEAMLESS
SP	SPACING
SPCL	SPECIAL
SPEC	SPECIFICATION
SPKLR	SPRINKLER
SPKR	SPEAKER
SPRT	SUPPORT
SQFT	SQUARE FOOT
SQ	SQUARE
SQIN	SQUARE INCH
SQYD	SQUARE YARD
SSK	SERVICE SINK
SS	STAINLESS STEEL
SSM	SOLID SURFACING MATERIAL
ST	STAIN
ST	STREET
STAG	STAGGERED
STC	SOUND TRANSMISSION CLASS
STD	STANDARD
STIR	STIRRUP
STL JST	STEEL JOIST
STL PL	STEEL PLATE
STL	STEEL
STN	STONE
STOR	STORAGE
STRUCT	STRUCTURAL
STRUCT STL	STRUCTURAL STEEL
SUPPL	SUPPLEMENT
SURF	SURFACE
SUSP	SUSPENDED
SUSP CLG	SUSPENDED CEILING
SVB	SHEET VINYL BASE
SVF	SHEET VINYL FLOOR
SYM	SYMBOL
SYMM	SYMMETRICAL
SYST	SYSTEM
T&B	TOP & BOTTOM
T&G	TONGUE & GROOVE
T	TABLE
TB	TACKBOARD
TB-xx	TEST BORING-xx (E.G. TB-1)
TC	TOP OF CURB
TD	TRENCH DRAIN
TE	TRANSITION EDGE
TECH	TECHNICAL
TEMP	TEMPORARY
TER	TERRAZZO
THK	THICK
THRES	THRESHOLD
THRU	THROUGH
TKBD	TACKBOARD
TLT	TOILET
TMPD	TEMPERED
TMPD GL	TEMPERED GLASS
TNL	TUNNEL
TO	TOP OF
TOF	TOP OF FLANGE
TOFF	TOP OF FINISH FLOOR
TOJ	TOP OF JOIST
TOL	TOLERANCE
TOS	TOP OF STEEL
TOT	TOTAL
TOW	TOP OF WALL
TRNBKL	TURNBUCKLE
TS	TUBE STEEL
TV	TELEVISION
TYP	TYPICAL
UF	UPHOLSTERY FABRIC
UFD	UNDER FLOOR DUCT
UG	UNDERGROUND
UL	UNDERWRITERS LABORATORY
ULT	ULTIMATE
UNEX	UNEXCAVATED
UNFIN	UNFINISHED
UNO	UNLESS NOTED OTHERWISE
UPS	UNITERRUPTIBLE POWER SUPPLY
UR	URINAL
UTIL	UTILITY
V	VOLT
VAC	VACUUM
VAV	VARIABLE AIR VOLUME
VB	VAPOR BARRIER
VB	VINYL BASE
VCT	VINYL COMPOSITION TILE
VDB	VISUAL DISPLAY BOARD
VERT	VERTICAL
VEST	VESTIBULE
VIB	VIBRATION
VNR	VENEER
VOL	VOLUME
VR	VAPOR RETARDER
VT	VINYL TILE
VWC	VINYL WALL COVERING
W/	WITH
W/W	WALL TO WALL
W/O	WITHOUT
W	WEST
WC	WATER CLOSET
WC	WALL COVERING
WCPT	WALL CARPET
WD	WOOD
WDD	WOOD DOOR
WDW	WINDOW
WF	WOOD FLOORING
WF	WIDE FLANGE
WGL	WIRE GLASS
WH	WALL HUNG
WHSE	WAREHOUSE
WL	WIND LOAD
WLD	WELDED
WR	WATER RESISTANT
WS	WEATHERSTRIPPING
WSCT	WAINSCOT
WT	WEIGHT
WTR	WATER
WTRPRF	WATERPROOFING
WWM	WELDED WIRE MESH
X SECT	CROSS SECTION

VICINITY MAP

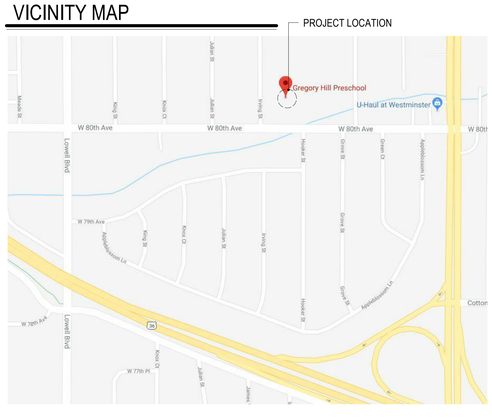

DAO ARCHITECTURE
7230 Meade St.
Westminster, CO 80030
Phone: 720.273.0431
Email: dan@daoarch.com
Web: www.daoarch.com

Westminster Public Schools

2026 Bond Projects - ECC Renovations
8030 Irving St. Westminster, CO 80031

DAO No.:2025-033

September 25, 2026

Standard Symbols, Abbreviations & General Notes

G0.0

Autodesk Docs://WPS 2026 Bond Projects - ECC Renovations/WPS ECC (Revit 2026).rvt
9/25/2026 8:01:16 AM

CODE REVIEW

This project entails an addition and interior renovations to the Early Childhood Center in Westminster, Colorado. This building is an existing E Occupancy building and will remain an E Occupancy.

In general, the scope of the addition and renovations will consist of the replacement of exterior finishes and the replacement of exterior waterproofing. There will be modifications to a small area of interior space, including the relocation of a door and the demolition of (2) walls.

2021 IEBC
The project is considered an Repair and Alteration per prescriptive section 503 of the 2021 IEBC. As such, any alterations shall comply with the requirements for the 2021 International Building Code, and the existing building shall be no less conforming to the provisions of the IBC than the existing building was prior to the alteration. This project's work area is less than 50% of the building area (0 / 78,843 square feet = 0% of the building).

Chapter 3 - Provisions for All Compliance Methods
301 - Administration
- 301.2 Repairs - Repairs shall comply with the requirements of Chapter 4.
- 301.3 Alteration, addition, or change of occupancy - The alteration of this existing building shall comply with section 301.3.1.
  - 301.3.1 - Prescriptive compliance method - Alterations complying with Chapter 5 of this code in buildings complying with the International Fire Code shall be considered in compliance with the provisions of this code

302 - General Provisions
- 302.3 Existing Materials - Materials already in use in a building in compliance with requirements or approvals in effect at the time of their erection or installation shall be permitted to remain in use unless determined by the code official to be unsafe.
- 302.4 New and replacement materials - Except as otherwise required or permitted by this code, materials permitted by the applicable code shall be used. Like materials shall be permitted for repairs or alterations, provided that unsafe conditions are not created. Hazardous materials shall not be used where the code for new construction would not permit their use in buildings of similar occupancy, purpose, and location.

Chapter 4 - Repairs
401 - General
- 401.2 Compliance - The work shall not make the building less complying than it was before the repair was undertaken.

403 - Fire Protection
- 403.1 General - Repairs shall be done in a manner that maintains the level of fire protection provided.

404 - Means of Egress
- 404.1 General - Repairs shall be done in a manner that maintains the level of protection provided for the means of egress.

Chapter 5 - Prescriptive Compliance Method
Section 503 - Alterations
- 503.1 - General - Alterations to any building or structure shall comply with the requirements of the International Building Code for new construction. Alterations shall be such that the existing building or structure is not less complying with the provisions of the International Building Code than the existing building or structure was prior to the alteration.
- 503.3 & 503.4 - This project is not altering the existing structural gravity or lateral systems in such a way as to trigger compliance with sections 503.3 or 503.4.

2021 IBC
Chapter 3 - Use and Occupancy Classification
305 - Educational: Group E
- The Occupancy type and use of the space are not changing as a part of this project.

Chapter 4 - Special Detailed Requirements Based on Use and Occupancy
Not Applicable

Chapter 5 - General Building Heights and Areas

504 - Building height and Number of Stories
- Building Height is existing and will not be altered by the scope of this project

506 - Building Area
- Building Area is existing and will not be altered by the scope of this project.

Chapter 6 - Types of Construction
602 - Construction Classification
- 602.3 - Type IIIB - The existing building is assumed to be type IIIB, as the exterior walls are of noncombustible materials, and the interior building elements are of any material permitted by IBC.

Chapter 7 - Fire and Smoke Protection Features
707 - Fire Barriers
- 707.3.10 Fire Areas - Existing Fire Areas will not be altered by the scope of this project.

Chapter 8 - Interior Finishes
Not Applicable

Chapter 9 - Fire Protection Systems
903 - Automatic Sprinkler Systems
- 903.2.3 Group E - *The existing building is unsprinklered. Sprinklers would not otherwise be required as no area of the building exceeds 12,000SF*
  - Fire Area A-1 = 11,762 SF
  - Fire Area A-2 = 9,103 SF
  - Fire Area A-3 = 3,282 SF
  - As such, fire sprinklers are not required.

907 - Fire Alarm and Detection Systems
- *Fire alarm and detection systems are existing and will not be impacted by the scope of this work.*

Chapter 10 - Means of Egress
1006 - Number of Exits
- 1006.2.1 - Spaces with (1) Exit A and B occupancies, Unsprinklered: 49 Occupants, 75'

1017 - Exit Access Travel Distance
- 1017.2 Exist Access Travel Distance- A and B occupancies, Unsprinklered, 200'

Chapter 11 - Accessibility
Accessibility features are existing conditions that will not be altered by this scope of work

Chapter 13 - Energy Efficiency
The existing building thermal envelope is existing and will not be altered by this scope of work.

Chapter 29 - Plumbing Systems
Plumbing features are existing conditions that will not be altered by this scope of work

Colorado Model Electric Ready and Solar Ready Code
CMERSRC is not applicable to the scope of this project as it is not a major renovation, addition, or first tenant finish to the building.

APPLICABLE BUILDING CODES

All new work shall comply with the requirements of the codes and standards adopted by the State of Colorado. The primary Applicable Codes and Standards are:

The 2021 International Code Series:
- The 2021 International Existing Building Code (IEBC)
- The 2021 International Building Code (IBC)
- The 2021 International Fire Code (IFC)
- The 2021 International Mechanical Code (IMC)
- The 2021 International Energy Conservation Code (IECC)

The 2024 Colorado Plumbing Code (CPC)
The 2024 Colorado Fuel Gas Code (CFGC)
The 2013 National Electrical Code
The 2026 ICC A117.1, Accessible and Usable Buildings and Facilities
The 2023 Colorado Model Electric and Solar Ready Code

EGRESS TRAVEL DISTANCES	
PATH NAME	DISTANCE
1A	50' - 11"

LIFE SAFETY SYMBOLS

FEC — FIRE EXTINGUISHER CABINET (NEW)
FEC — FIRE EXTINGUISHER CABINET (EXISTING)
1 HOUR FIRE PARTITION (NEW)
1 HOUR FIRE PARTITION (EXISTING)
2 HOUR FIRE BARRIER (NEW)
2 HOUR FIRE BARRIER (EXISTING)
XX — PATH OF TRAVEL (FOR CUMULATIVE DISTANCES REFER TO SCHEDULE)
EXIT DISCHARGE
P: XX" / R: XX" — WIDTH PROVIDED / WIDTH REQUIRED


Table 2902.1

Classification	Occupancy	Description	Water Closets Male	Water Closets Female	Lavatories Male	Lavatories Female	Bathtubs/ Showers	Drinking Fountains	Other
Educational	E	Educational facilities	329 / 50	329 / 50	329 / 50	329 / 50	N/A	658 / 100	1 Service Sink
			6.58	**6.58**	**6.58**	**6.58**		**6.58**	
		Total Required	**6.58**	**6.58**	**6.58**	**6.58**	N/A	**6.58**	1 Service Sink
		Total Provided	10	9	14	14	N/A	19	**1 Service Sink**

*ALL PLUMBING FIXTURES ARE EXISTING-TO-REMAIN AND WILL NOT BE ALTERED BY THIS PROJECT

Occupant Load Table

Number	Name	Occupancy Classification	Area	Area Function	SF Per Occupant	Occupant Load	Required Exiting Width
000	Vestibule	(none)	109 SF	(none)		0	0
1	Classroom	(IBC) E	742 SF	IBC_Educational: Classroom area	20 SF	38	7.5
2	Classroom	(IBC) E	747 SF	IBC_Educational: Classroom area	20 SF	38	7.6
3	Classroom	(IBC) E	761 SF	IBC_Educational: Classroom area	20 SF	39	7.7
4	Classroom	(IBC) E	761 SF	IBC_Educational: Classroom area	20 SF	39	7.7
5	Classroom	(IBC) E	747 SF	IBC_Educational: Classroom area	20 SF	38	7.6
6	Classroom	(IBC) E	746 SF	IBC_Educational: Classroom area	20 SF	38	7.6
7	Classroom	(IBC) E	745 SF	IBC_Educational: Classroom area	20 SF	38	7.6
8	Hearing and Vision	(IBC) E	566 SF	IBC_Educational: Classroom area	20 SF	29	5.8
9	Classroom	(IBC) E	748 SF	IBC_Educational: Classroom area	20 SF	38	7.6
10	Classroom	(IBC) E	746 SF	IBC_Educational: Classroom area	20 SF	38	7.6
11	Classroom	(IBC) E	747 SF	IBC_Educational: Classroom area	20 SF	38	7.6
12	Classroom	(IBC) E	763 SF	IBC_Educational: Classroom area	20 SF	39	7.7
13	Classroom	(IBC) E	763 SF	IBC_Educational: Classroom area	20 SF	39	7.7
14	Classroom	(IBC) E	747 SF	IBC_Educational: Classroom area	20 SF	38	7.6
15	Classroom	(IBC) E	833 SF	IBC_Educational: Classroom area	20 SF	42	8.4
16	Corridor	(none)	270 SF	(none)		0	0
17	Corridor	(none)	307 SF	(none)		0	0
18	Corridor	(none)	268 SF	(none)		0	0
19	Corridor	(none)	1230 SF	(none)		0	0
26	Corridor	(none)	542 SF	(none)		0	0
39	Corridor	(none)	301 SF	(none)		0	0
40	Corridor	(none)	394 SF	(none)		0	0
43	Gym Storage	(IBC) S-1	449 SF	IBC_Accessory storage areas, mechanical equipment room	300 SF	2	0.4
45	Corridor	(none)	158 SF	(none)		0	0
47	Vestibule	(none)	59 SF	(none)		0	0
48	Vestibule	(none)	59 SF	(none)		0	0
100A	Reception / Waiting	(IBC) B	313 SF	IBC_Business areas	100 SF	4	0.7
100B	Sec.	(IBC) B	115 SF	IBC_Business areas	100 SF	2	0.3
100C	Infirmary	(IBC) B	94 SF	IBC_Business areas	100 SF	1	0.3
100D	Workarea	(IBC) B	70 SF	IBC_Business areas	100 SF	1	0.2
100E	Principal	(IBC) B	200 SF	IBC_Business areas	100 SF	2	0.5
100F	Storage	(IBC) B	94 SF	IBC_Accessory storage areas, mechanical equipment room	300 SF	1	0.2
120	Girls	(none)	123 SF	(none)		0	0
121	Kitchen	(IBC) B	465 SF	IBC_Kitchens, commercial	200 SF	3	0.6
123	Elec.	(IBC) E	60 SF	IBC_Accessory storage areas, mechanical equipment room	300 SF	1	0.1
124	Boys	(none)	124 SF	(none)		0	0
125	Girls	(none)	165 SF	(none)		0	0
126	Boiler	(IBC) E	315 SF	IBC_Accessory storage areas, mechanical equipment room	300 SF	2	0.3
127	Boys	(none)	157 SF	(none)		0	0
128	MDF	(IBC) E	129 SF	IBC_Accessory storage areas, mechanical equipment room	300 SF	1	0.2
130	Workroom / Lounge	(IBC) E	607 SF	IBC_Assembly: without fixed seats - Unconcentrated (tables and chairs)	15 SF	41	8.2
132	Flex	(IBC) E	194 SF	IBC_Assembly: without fixed seats - Unconcentrated (tables and chairs)	15 SF	13	2.7
133	Flex	(IBC) E	237 SF	IBC_Assembly: without fixed seats - Unconcentrated (tables and chairs)	15 SF	16	3.3
134	Storage	(IBC) S-1	180 SF	IBC_Accessory storage areas, mechanical equipment room	300 SF	1	0.2
135	Janitor	(none)	73 SF	IBC_Accessory storage areas, mechanical equipment room	300 SF	1	0.1
136	Storage	(IBC) S-1	91 SF	IBC_Accessory storage areas, mechanical equipment room	300 SF	1	0.2
137a	Toilet	(none)	52 SF	(none)		0	0
137b	Toilet	(none)	50 SF	(none)		0	0
: 49			19214 SF			658	131.6
All Purpose Room							
41	All Purpose Room	(IBC) E	3163 SF	IBC_Assembly: without fixed seats - Concentrated (chairs only - not fixed)	7 SF	452	90.5
All Purpose Room: 1			3163 SF			452	90.5
Health Clinic							
42	Health Clinic	(IBC) B	1154 SF	IBC_Business areas	100 SF	12	2.4
Health Clinic: 1			1154 SF			12	2.4
Grand total: 51			23531 SF			1122	224.4

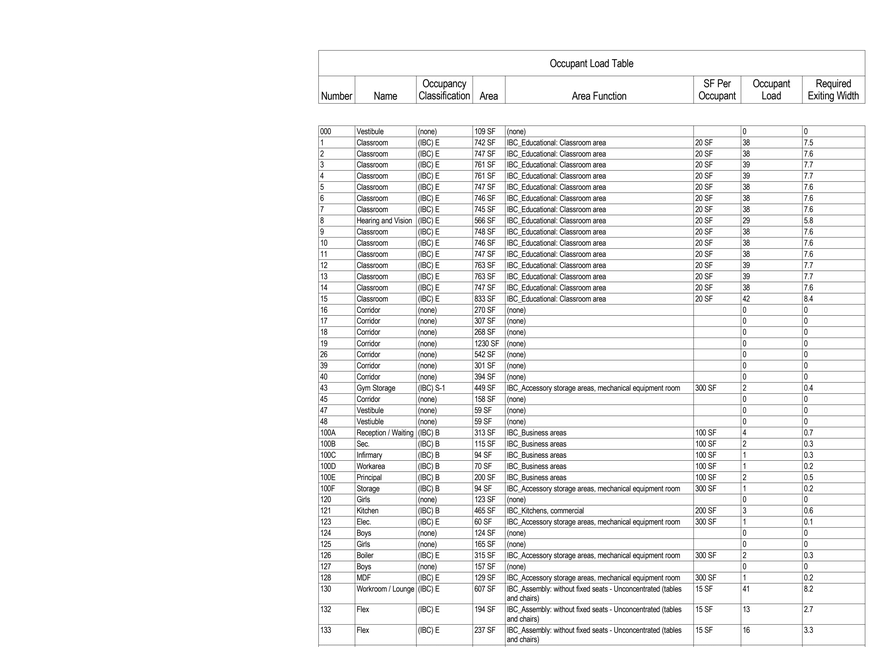

Life Safety Plan
SCALE: 1/16" = 1'-0"

DAO ARCHITECTURE
7230 Meade St.
Westminster, CO 80030
Phone: 720.273.0431
Email: dan@daoarch.com
Web: www.daoarch.com

Westminster Public Schools

2026 Bond Projects - ECC Renovations
8030 Irving St. Westminster, CO 80031


DAO No.:2025-033

September 25, 2026

Building Code Data


G0.1

Autodesk Docs://WPS 2026 Bond Projects - ECC Renovations/WPS ECC (Revit 2025).rvt
9/25/2026 8:01:17 AM

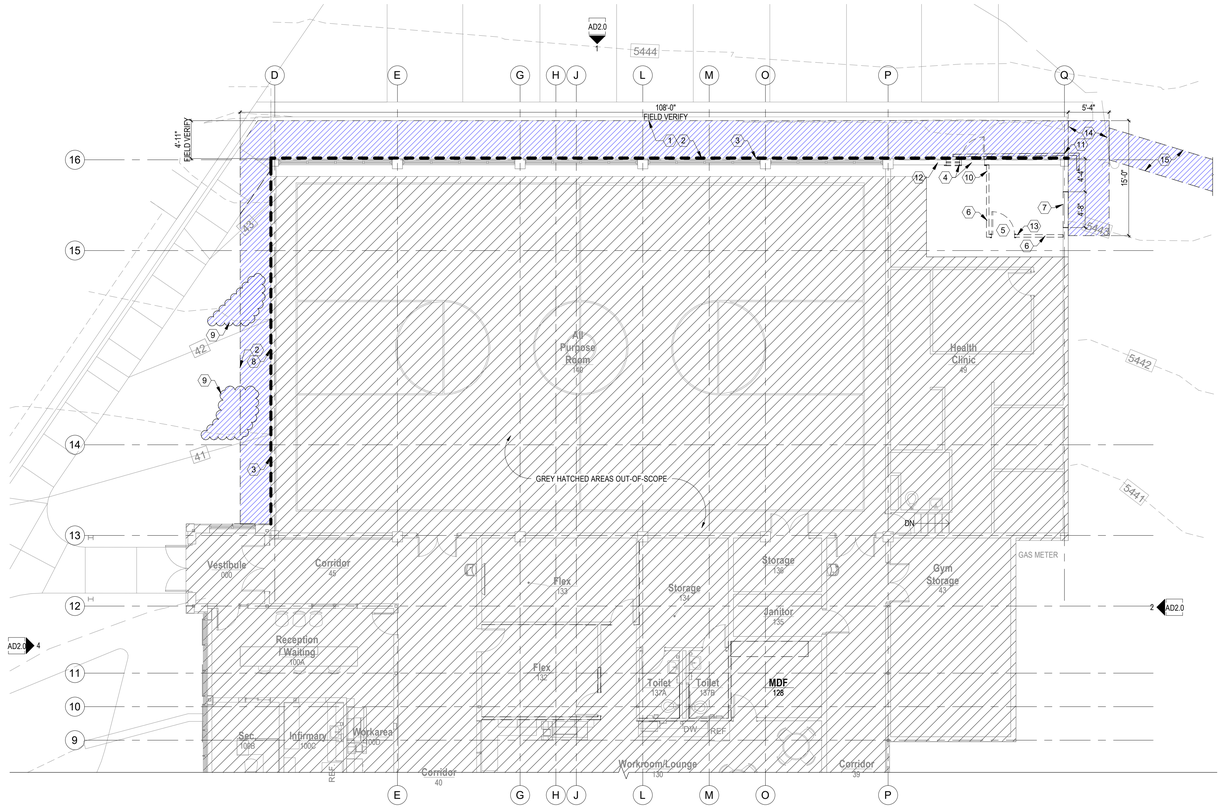

1 First Floor Demolition Plan

SCALE: 1/8" = 1'-0"

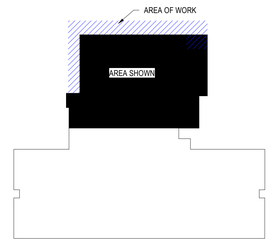

2 Key Plan

SCALE: 1" = 50'-0"

GENERAL DEMOLITION NOTES

1. THE GENERAL CONTRACTOR SHALL VERIFY ALL EXISTING DIMENSIONS AND CONDITIONS SHOWN ON THE PLANS PRIOR TO COMMENCEMENT OF THE WORK. IT SHALL BE THE CONTRACTORS RESPONSIBILITY TO COORDINATE INSTALLATION OF NEW WORK WITHIN THESE EXISTING CONDITIONS. ANY DEVIATIONS IN EXISTING CONDITIONS OR DIMENSIONS INDICATED SHALL BE COORDINATED WITH THE ARCHITECT/ENGINEER AND OWNER IN ORDER TO MODIFY THE PLANS ACCORDINGLY.
2. THE EXISTING BUILDING SHALL BE PROTECTED FROM WEATHER AT ALL TIMES. OPENINGS AND PENETRATIONS SHALL BE PROTECTED WITH DURABLE, INSULATED TEMPORARY CONSTRUCTION. COORDINATE SECURITY REQUIREMENTS WITH THE OWNER.
3. ALL WORK IS TO BE PERFORMED IN SUCH A MANNER AS TO MINIMIZE THE IMPACT ON AREAS ADJACENT TO THE AREAS OF CONSTRUCTION.
4. REMOVE EXISTING FLOORS, WALLS AND CEILINGS AS REQUIRED FOR NEW CONSTRUCTION. PATCH, REPAIR AND PREPARE ADJACENT SURFACES AS REQUIRED FOR NEW CONSTRUCTION AND FINISHES.
5. REFER TO MECHANICAL, ELECTRICAL, PLUMBING, LOW VOLTAGE, ROOF, AND LANDSCAPE/CIVIL DRAWINGS FOR ADDITIONAL INFORMATION PERTAINING TO DEMOLITION.
6. REMOVE EXISTING FURNITURE, FIXTURES AND EQUIPMENT (INCLUDING ARTWORK AND MARKER/TACK BOARDS AS REQUIRED FOR NEW CONSTRUCTION. COORDINATE SALVAGE AND STORAGE OF EQUIPMENT WITH OWNER AS REQUIRED. PROTECT AND STORE ALL ITEMS DESIGNATED TO BE SALVAGED FOR REINSTALLATION.
7. REMOVE EXISTING SIGNAGE AS REQUIRED FOR DEMOLITION AND STORE DURING CONSTRUCTION. REINSTALL WHEN APPLICABLE. PATCH AND PREPARE ADJACENT SURFACES AS REQUIRED FOR NEW FINISHES. ALL NEW SIGNAGE TO BE PROVIDED BY OWNER.
8. ALL OPENINGS AND VOIDS LEFT BY THE REMOVAL OF EXISTING CONSTRUCTION, EQUIPMENT, PIPING, DUCTS, ETC. SHALL BE PROPERLY PATCHED AND CLOSED OFF TO MAINTAIN PROPER FIRE RATING IN WALLS, IF APPLICABLE. PATCH AND PREPARE ANY AREAS TO RECEIVE NEW FINISHES AS REQUIRED.
9. THE ARCHITECT ASSUMES NO RESPONSIBILITY FOR THE DETECTION OR REMOVAL OF ANY HAZARDOUS MATERIALS, INCLUDING, BUT NOT LIMITED TO, ASBESTOS IN ANY FORM. PARTIES RESPONSIBLE FOR DEMOLITION SHALL NOTIFY THE OWNER IMMEDIATELY OF ANY SUSPECTED MATERIALS.
10. OWNER HAS RIGHT TO CLAIM ANY MATERIALS AND/OR EQUIPMENT THAT IS SCHEDULED TO BE DEMOLISHED OR REMOVED FROM THE SITE.
11. ALL EXISTING BUILDING ELEMENTS TO REMAIN SHALL BE PROTECTED DURING CONSTRUCTION.
12. REMOVE EXISTING FLOOR FINISHES WHERE INDICATED. DEMOLITION INCLUDES REMOVAL OF EXISTING ADHESIVES, GROUTING BED, ETC. PATCH AND PREPARE FLOOR AND WALL SURFACES AS REQUIRED FOR NEW CONSTRUCTION AND FINISHES. WHERE FLOOR FINISH IS REMOVED, BASE WILL BE REMOVED. SEE FINISH PLAN FOR ADDITIONAL INFORMATION.
13. PREPARE EXISTING SUBSTRATES TO REMAIN AS REQUIRED TO RECEIVE NEW FINISHES.
14. EXISTING FLOOR SLABS ARE CONCRETE. ANY DEMOLISHING OF EXISTING FLOOR SLABS WILL REQUIRE GPR X-RAY PRIOR TO DEMOLITION.

DEMOLITION KEY NOTES

1. REMOVE EXISTING CONCRETE SIDEWALK AS REQUIRED FOR INSTALLATION OF NEW DAMPPROOFING SYSTEM. PROTECT ADJACENT EXISTING CONCRETE, PAVEMENT, AND BUILDING ELEMENTS TO REMAIN. PATCH AND PREPARE ADJACENT SURFACES AS REQUIRED FOR NEW CONSTRUCTION. RE: CIVIL
2. REMOVE EXISTING BACKFILL AS REQUIRED FOR INSTALLATION OF NEW DAMPPROOFING SYSTEM AND STORE FOR REINSTALLATION. PATCH AND PREPARE ADJACENT SURFACES AS REQUIRED FOR NEW CONSTRUCTION. RE: CIVIL
3. REMOVE EXISTING DAMPPROOFING SYSTEM IN ITS ENTIRETY, TO THE EXTENT POSSIBLE WITHOUT DAMAGING EXISTING BRICK. PREPARE REMAINING SUBSTRATE AS REQUIRED FOR INSTALLATION OF NEW DAMPPROOFING SYSTEM. PATCH AND PREPARE ADJACENT SURFACES AS REQUIRED FOR NEW CONSTRUCTION.
4. REMOVE EXISTING HOLLOW METAL DOOR, FRAME, AND SIDELITE ASSEMBLY IN ITS ENTIRETY. PATCH AND PREPARE ADJACENT SURFACES AS REQUIRED FOR NEW CONSTRUCTION.
5. REMOVE EXISTING DOOR AND FRAME ASSEMBLY IN ITS ENTIRETY. PATCH AND PREPARE ADJACENT SURFACES AS REQUIRED FOR NEW CONSTRUCTION.
6. REMOVE EXISTING GPDW AND STUD WALL ASSEMBLY AS INDICATED. PATCH AND PREPARE ADJACENT SURFACES AS REQUIRED FOR NEW CONSTRUCTION.
7. REMOVE EXISTING CMU AND FACE BRICK WALL ASSEMBLY AS REQUIRED FOR NEW DOOR AND FRAME. FIELD LOCATE AND ALIGN CUTS TO ADJACENT MORTAR JOINTS PATCH AND PREPARE ADJACENT SURFACES AS REQUIRED FOR NEW CONSTRUCTION.
8. REMOVE EXISTING LANDSCAPE MATERIAL AS REQUIRED AND STORE FOR RE-INSTALLATION. PATCH AND PREPARE ADJACENT SURFACES AS REQUIRED FOR NEW CONSTRUCTION
9. REMOVE EXISTING PLANTING AS REQUIRED FOR EXCAVATION. DOCUMENT TYPES OF PLANTS REMOVED FOR REPLACEMENT AFTER CONSTRUCTION. PATCH AND PREPARE ADJACENT SURFACES AS REQUIRED FOR NEW CONSTRUCTION.
10. REMOVE EXISTING SECURITY KEYPAD AND SALVAGE FOR RE-INSTALLATION. DEMOLISH LOW-VOLTAGE LINES AS REQUIRED FOR WALL DEMOLITION. COORDINATE WITH OWNER AS REQUIRED TO TEMPORARILY DISABLE THE SECURITY SYSTEM. PATCH AND PREPARE ADJACENT SURFACES AS REQUIRED FOR NEW CONSTRUCTION.
11. DEMOLISH EXISTING TRENCH DRAIN IN ITS ENTIRETY. PATCH AND PREPARE ADJACENT SURFACES AS REQUIRED FOR NEW CONSTRUCTION. RE: CIVIL
12. REMOVE EXISTING FIRE ALARM PULL STATION AND SALVAGE FOR RE-INSTALLATION. COORDINATE WITH OWNER AND FIRE ALARM CONTRACTOR AS REQUIRED TO MODIFY THE SYSTEM. PATCH AND PREPARE ADJACENT SURFACES AS REQUIRED FOR NEW CONSTRUCTION.
13. REMOVE EXISTING OCCUPANCY SENSOR AND DIMMER. EXISTING FIXTURE IS TO REMAIN. TIE EXISTING FIXTURE INTO LIGHTING CONTROLS FOR OVERALL SPACE. PATCH AND PREPARE ADJACENT SURFACES AS REQUIRED FOR NEW CONSTRUCTION
14. REMOVE EXISTING ASPHALT AS REQUIRE FOR INSTALLATION OF NEW CONCRETE WALK AND/OR INSTALLATION OF NEW DRAIN LINE. PATCH AND PREPARE ADJACENT SURFACES AS REQUIRED FOR NEW CONSTRUCTION
15. REMOVE ASPHALT AS REQUIRED FOR INSTALLATION OF NEW FOUNDATION DRAIN LINE AND NEW DRYWELL. PATCH AND PREPARE ADJACENT SURFACES AS REQUIRED FOR NEW CONSTRUCTION. SEE CIVIL FOR ADDITIONAL INFORMATION.

DAO ARCHITECTURE
7230 Meade St.
Westminster, CO 80030
Phone: 720.273.0431
Email: dan@daoarch.com
Web: www.daoarch.com

Westminster Public Schools

2026 Bond Projects - ECC Renovations
8030 Irving St. Westminster, CO 80031


DAO No.:2025-033

September 25, 2026

Partial Demolition Plan

AD1.0


Autodesk Docs://WPS 2026 Bond Projects - ECC Renovations/WPS ECC (Revit 2026).rvt
9/25/2026 8:01:18 AM

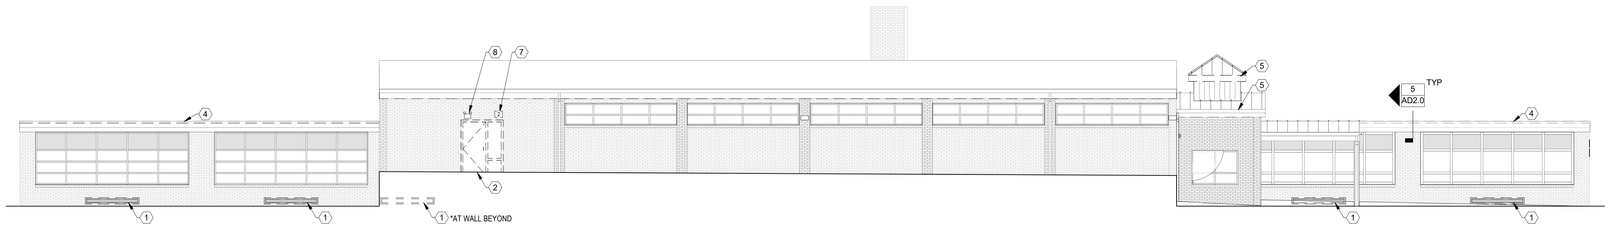

1 Demolition North Elevation

SCALE: 1/8" = 1'-0"


1 | AD1.0

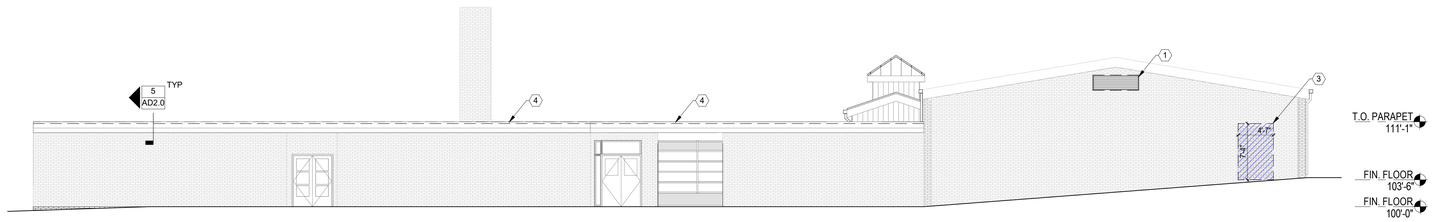

2 Demolition East Elevation

SCALE: 1/8" = 1'-0"


1 | AD1.0

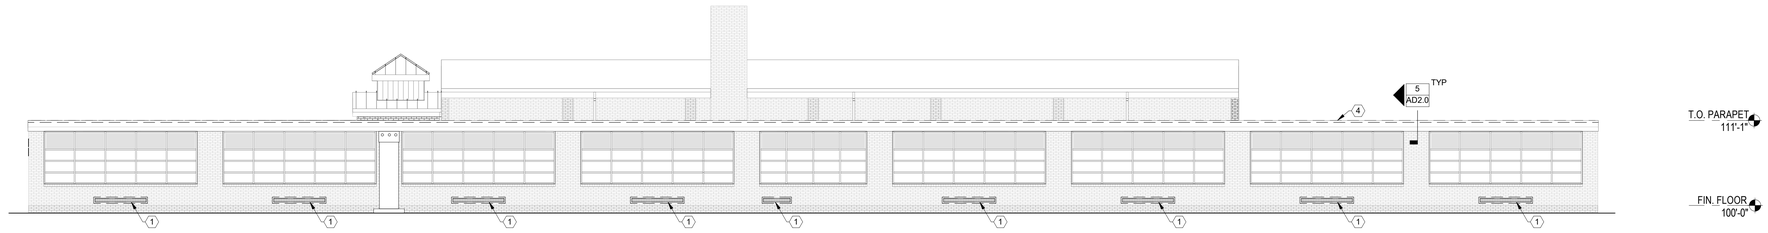

3 Demolition South Elevation

SCALE: 1/8" = 1'-0"


1 | AD1.0

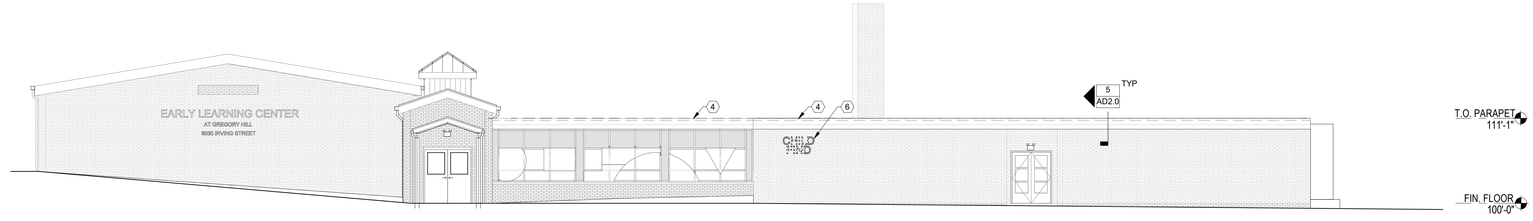

4 Demoltion East Elevation

SCALE: 1/8" = 1'-0"

1 | AD1.0

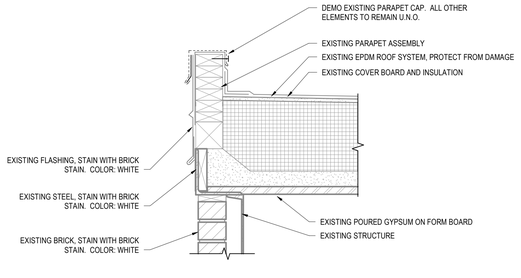

5 Typ. Flashing Demo

SCALE: 1 1/2" = 1'-0"

GENERAL DEMOLITION NOTES

1. THE GENERAL CONTRACTOR SHALL VERIFY ALL EXISTING DIMENSIONS AND CONDITIONS SHOWN ON THE PLANS PRIOR TO COMMENCEMENT OF THE WORK. IT SHALL BE THE CONTRACTORS RESPONSIBILITY TO COORDINATE INSTALLATION OF NEW WORK WITHIN THESE EXISTING CONDITIONS. ANY DEVIATIONS IN EXISTING CONDITIONS OR DIMENSIONS INDICATED SHALL BE COORDINATED WITH THE ARCHITECT/ENGINEER AND OWNER IN ORDER TO MODIFY THE PLANS ACCORDINGLY.
2. THE EXISTING BUILDING SHALL BE PROTECTED FROM WEATHER AT ALL TIMES. OPENINGS AND PENETRATIONS SHALL BE PROTECTED WITH DURABLE, INSULATED TEMPORARY CONSTRUCTION. COORDINATE SECURITY REQUIREMENTS WITH THE OWNER.
3. ALL WORK IS TO BE PERFORMED IN SUCH A MANNER AS TO MINIMIZE THE IMPACT ON AREAS ADJACENT TO THE AREAS OF CONSTRUCTION.
4. REMOVE EXISTING FLOORS, WALLS AND CEILINGS AS REQUIRED FOR NEW CONSTRUCTION. PATCH, REPAIR AND PREPARE ADJACENT SURFACES AS REQUIRED FOR NEW CONSTRUCTION AND FINISHES.
5. REFER TO MECHANICAL, ELECTRICAL, PLUMBING, LOW VOLTAGE, ROOF, AND LANDSCAPE/CIVIL DRAWINGS FOR ADDITIONAL INFORMATION PERTAINING TO DEMOLITION.
6. REMOVE EXISTING FURNITURE, FIXTURES AND EQUIPMENT (INCLUDING ARTWORK AND MARKER/TACK BOARDS AS REQUIRED FOR NEW CONSTRUCTION. COORDINATE SALVAGE AND STORAGE OF EQUIPMENT WITH OWNER AS REQUIRED. PROTECT AND STORE ALL ITEMS DESIGNATED TO BE SALVAGED FOR REINSTALLATION.
7. REMOVE EXISTING SIGNAGE AS REQUIRED FOR DEMOLITION AND STORE DURING CONSTRUCTION. REINSTALL WHEN APPLICABLE. PATCH AND PREPARE ADJACENT SURFACES AS REQUIRED FOR NEW FINISHES. ALL NEW SIGNAGE TO BE PROVIDED BY OWNER.
8. ALL OPENINGS AND VOIDS LEFT BY THE REMOVAL OF EXISTING CONSTRUCTION, EQUIPMENT, PIPING, DUCTS, ETC. SHALL BE PROPERLY PATCHED AND CLOSED OFF TO MAINTAIN PROPER FIRE RATING IN WALLS, IF APPLICABLE. PATCH AND PREPARE ANY AREAS TO RECEIVE NEW FINISHES AS REQUIRED.
9. THE ARCHITECT ASSUMES NO RESPONSIBILITY FOR THE DETECTION OR REMOVAL OF ANY HAZARDOUS MATERIALS, INCLUDING, BUT NOT LIMITED TO, ASBESTOS IN ANY FORM. PARTIES RESPONSIBLE FOR DEMOLITION SHALL NOTIFY THE OWNER IMMEDIATELY OF ANY SUSPECTED MATERIALS.
10. OWNER HAS RIGHT TO CLAIM ANY MATERIALS AND/OR EQUIPMENT THAT IS SCHEDULED TO BE DEMOLISHED OR REMOVED FROM THE SITE.
11. ALL EXISTING BUILDING ELEMENTS TO REMAIN SHALL BE PROTECTED DURING CONSTRUCTION.
12. REMOVE EXISTING FLOOR FINISHES WHERE INDICATED. DEMOLITION INCLUDES REMOVAL OF EXISTING ADHESIVES, GROUTING BED, ETC. PATCH AND PREPARE FLOOR AND WALL SURFACES AS REQUIRED FOR NEW CONSTRUCTION AND FINISHES. WHERE FLOOR FINISH IS REMOVED, BASE WILL BE REMOVED. SEE FINISH PLAN FOR ADDITIONAL INFORMATION.
13. PREPARE EXISTING SUBSTRATES TO REMAIN AS REQUIRED TO RECEIVE NEW FINISHES.
14. EXISTING FLOOR SLABS ARE CONCRETE. ANY DEMOLISHING OF EXISTING FLOOR SLABS WILL REQUIRE GPR X-RAY PRIOR TO DEMOLITION.

DEMOLITION KEY NOTES

1. REMOVE EXISTING ABANDONED AIR LOUVER IN ITS ENTIRETY, AND ADJACENT BRICK AS REQUIRED TO TOOTH-IN NEW BRICK INFILL. PATCH AND PREPARE ADJACENT SURFACES AS REQUIRED FOR NEW CONSTRUCTION.
2. REMOVE EXISTING HOLLOW METAL DOOR, FRAME, AND SIDELITE ASSEMBLY IN ITS ENTIRETY. PATCH AND PREPARE ADJACENT SURFACES AS REQUIRED FOR NEW CONSTRUCTION.
3. REMOVE EXISTING CMU AND FACE BRICK WALL ASSEMBLY AS REQUIRED FOR NEW DOOR AND FRAME. PATCH AND PREPARE ADJACENT SURFACES AS REQUIRED FOR NEW CONSTRUCTION.
4. REMOVE EXISTING PARAPET CAP, ALL OTHER ELEMENTS TO REMAIN. RE: ROOFING. SEE 5/AD2.0 FOR ADDITIONAL INFORMATION
5. NOT USED
6. REMOVE EXISTING METAL LETTER SIGNAGE AND SALVAGE FOR RETURN TO THE OWNER. PATCH AND PREPARE ADJACENT SURFACES AS REQUIRED FOR NEW CONSTRUCTION
7. REMOVE EXISTING DOOR IDENTIFICATION SIGNAGE AS REQUIRED AND SALVAGE FOR RE-INSTALLATION AT NEW DOOR LOCATION. PATCH AND PREPARE ADJACENT SURFACES AS REQUIRED FOR NEW CONSTRUCTION.
8. REMOVE EXITING WALL-PACK FIXTURE AND SALVAGE FOR RE-INSTALLATION. PROVIDE WEATHER-PROOF CAP ON EXISTING J-BOX. PATCH AND PREPARE ADJACENT SURFACES AS REQUIRED FOR NEW CONSTRUCTION.

DAO ARCHITECTURE

7230 Meade St.
Westminster, CO 80030

Phone: 720.273.0431
Email: dan@daoarch.com
Web: www.daoarch.com

Westminster Public Schools

2026 Bond Projects - ECC Renovations
8030 Irving St. Westminster, CO 80031


DAO No.:2025-033

September 25, 2026

Demolition Exterior Elevations

AD2.0

Autodesk Docs://WPS 2026 Bond Projects - ECC Renovations/WPS ECC (Revit 2026).rvt
9/25/2026 8:01:29 AM

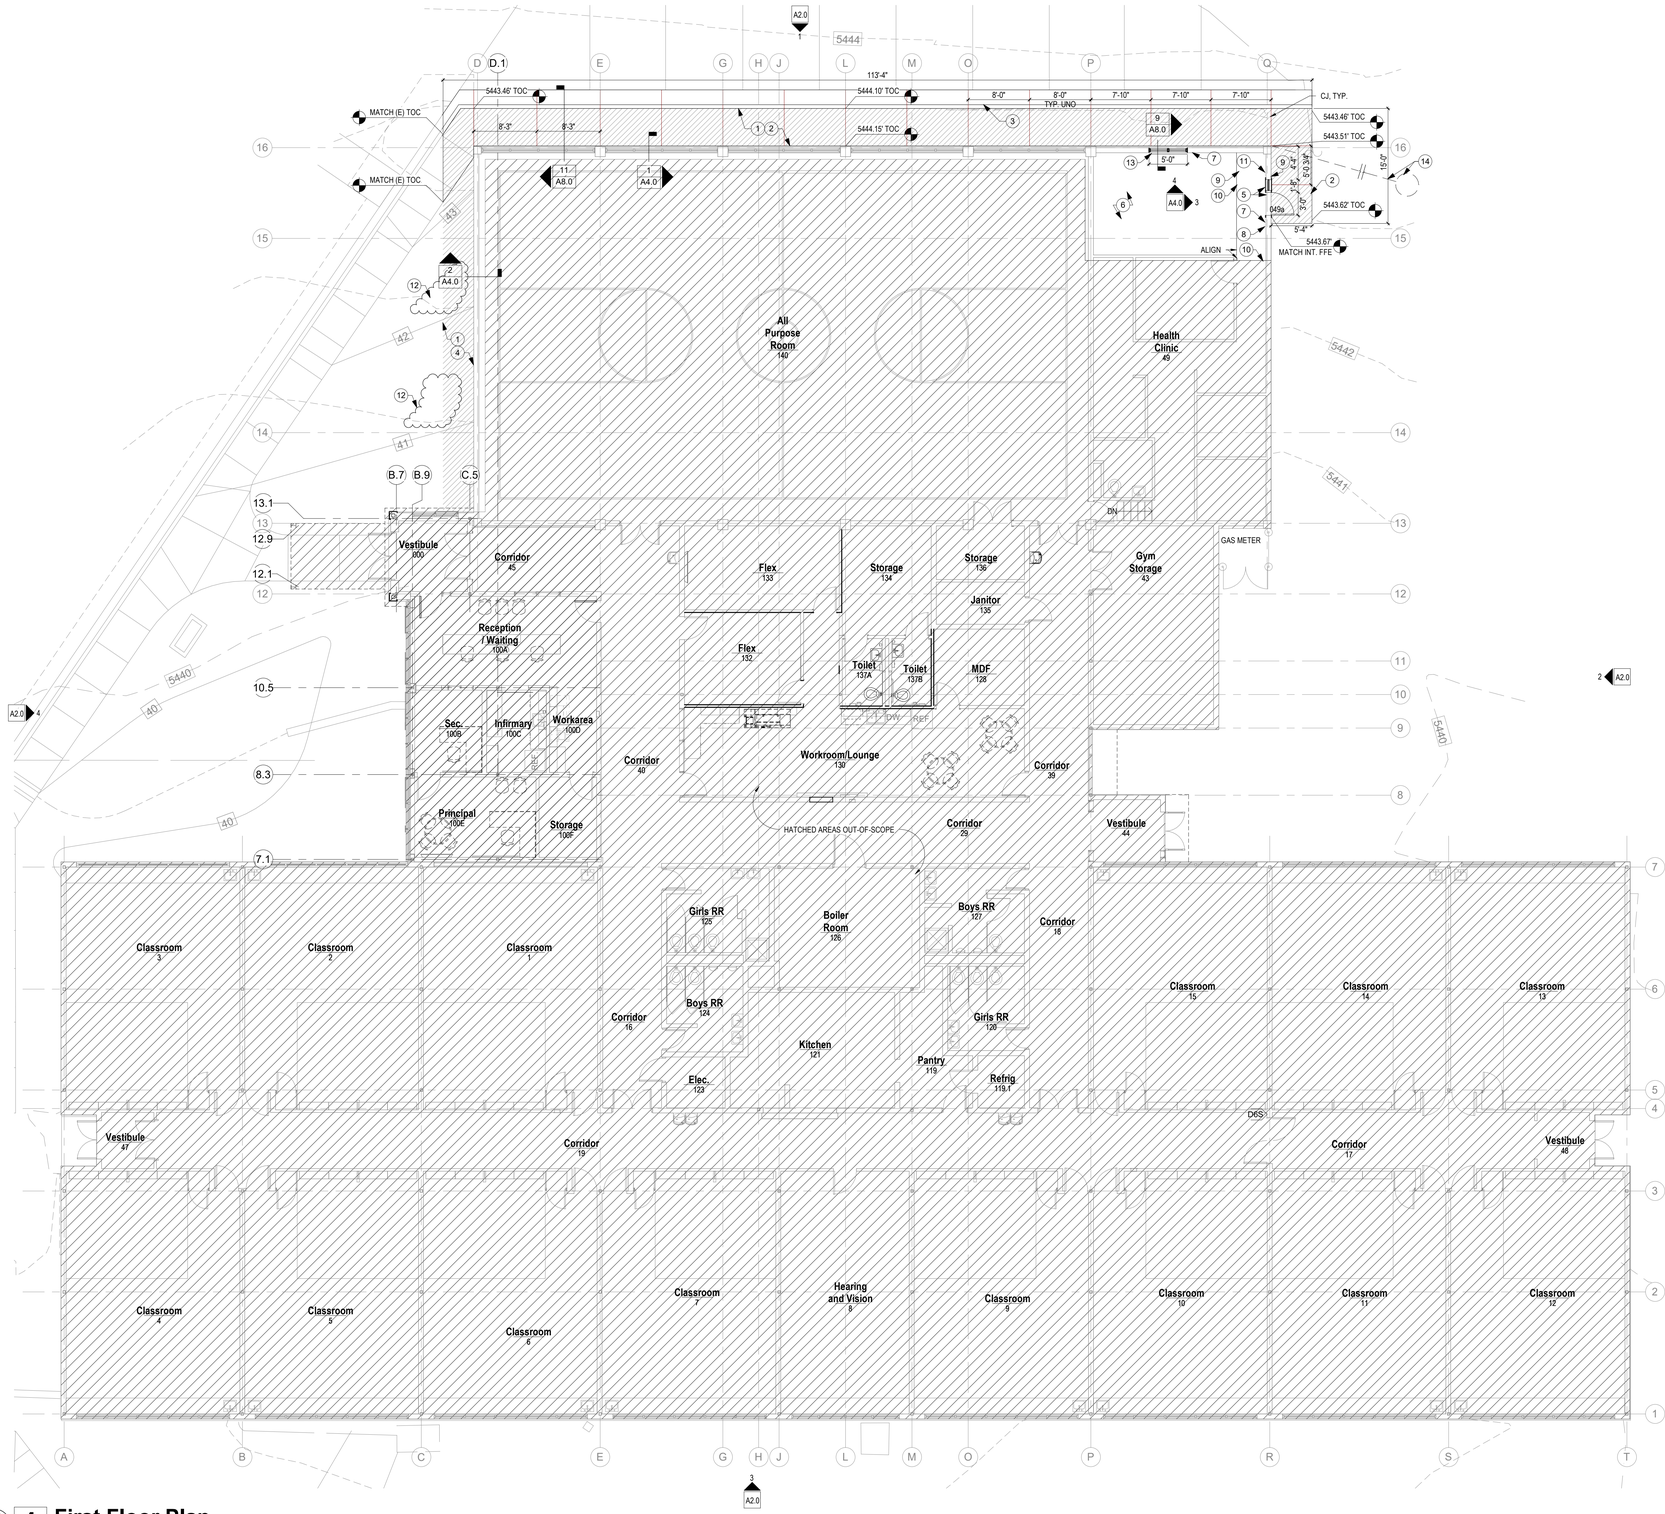

1 First Floor Plan

SCALE: 1/8" = 1'-0"

GENERAL PLAN NOTES

1. DRAWINGS & SPECIFICATIONS ARE COMPLIMENTARY COMPONENTS OF THE CONTRACT DOCUMENTS, REVIEW ALL DRAWINGS AND SPECIFICATIONS FOR THE COMPLETE SCOPE OF WORK. NOTIFY ARCHITECT IMMEDIATELY FOR CLARIFICATION IF INCONSISTENCIES, CONTRADICTIONS OR OMISSIONS ARE DISCOVERED.
2. DO NOT SCALE DRAWINGS, IF DIMENSIONAL INFORMATION IS REQUIRED & NOT FOUND, NOTIFY ARCHITECT IMMEDIATELY FOR CLARIFICATION.
3. ALL DIMENSIONS ARE TO COLUMN CENTERLINES OR FACE OF FINISHED WALLS OR SURFACES UNLESS NOTED OTHERWISE.
4. REFER TO DEMOLITION DRAWINGS FOR WORK REQUIRED IN ADVANCE OF CONSTRUCTION AND COORDINATE ACCORDINGLY.
5. ALL NEW DOOR FRAMES ARE TO BE INSTALLED 4" AWAY OF ADJACENT PERPENDICULAR WALLS UNLESS NOTED OTHERWISE.
6. REFER TO STRUCTURAL, MECHANICAL, ELECTRICAL, PLUMBING, LOW VOLTAGE, ROOF, LANDSCAPE, AND CIVIL DRAWINGS FOR ADDITIONAL INFORMATION.
7. INTERIOR SIGNAGE TO BE PROVIDED BY OWNER.
8. FURNITURE AND EQUIPMENT TO BE PROVIDED BY OWNER.
9. AT ALL LOCATIONS WHERE A NEW OR EXISTING WALL MEETS A STOREFRONT MULLION, SEAL EACH SIDE WITH ACOUSTICAL SEALANT.

KEY NOTES

1. REPLACE BACKFILL REMOVED FOR INSTALLATION OF NEW DAMPPROOFING. COMPACT IN 8" LIFTS TO MINIMUM COMPACTION OF 95% OR MORE AS DETERMINED BY APPLICABLE ASTM TESTING. RE: CIVIL
2. NEW CONCRETE SIDEWALK. PROVIDE 6" CONCRETE PAVING OVER 6" CDOT CLASS 6 AGGREGATE BASE COURSE. SEE 8/A8.0. RE: CIVIL
3. NEW CONCRETE CURB. SEE 8/A8.0. RE: CIVIL.
4. REPLACE LANDSCAPE MATERIAL, LEVEL AND EQUAL THE DEPTH OF ADJACENT AREAS.
5. NEW INSULATED HOLLOW METAL DOOR AND FRAME ASSEMBLY WITH INSULATED GLAZED SIDE LITE.
6. NEW CARPET, TARKETT POWER BOND VISUAL PATH, 20150. PROVIDE SAMPLES FOR APPROVAL BEFORE INSTALLATION
7. PROVIDE NEW WALL BASE, MATCHING EXISTING WALL BASE. COORDINATE WITH OWNER FOR USE OF ATTIC STOCK
8. RE-INSTALL SALVAGED SECURITY KEY PAD. PROVIDE NEW LOW-VOLTAGE CONNECTIONS AS REQUIRED. COORDINATE WITH OWNER AS REQUIRED TO RE-PROGRAM SECURITY SYSTEM.
9. PROVIDE NEW CARD READER. PROVIDE NEW LOW-VOLTAGE CONNECTIONS AS REQUIRED. COORDINATE WITH OWNER AS REQUIRED TO CONNECT TO POWERED DOOR HARDWARE AND SECURITY SYSTEM.
9. NEW WALK-OFF CARPET, TANDUS ABRASIVE ACTION II 02578 COLOR: WINTER GRAY 19103. PROVIDE SAMPLES FOR APPROVAL BEFORE INSTALLATION
10. FLOORING TRANSITION. JOHNSONITE BY TARKETT SLT OR EQUAL. COLOR BLACK
11. REINSTALL FIRE ALARM PULL STATION. EXTEND EXISTING ADDRESSABLE FIRE ALARM CIRCUIT AS REQUIRED. COORDINATE WITH OWNER FOR EXACT LOCATION.
12. APPROXIMATE LOCATION OF NEW PLANTING. MATCH NUMBER AND TYPE OF PLANTING REMOVED DURING DEMOLITION.
13. ROLLER SHADE AT WINDOW. LUTEK OR EQUAL. MANUAL ROLLER SHADE, FABRIC: ONYX, FASCIA: ANODIZED, HARDWARE: GRAY, FABRIC WRAPPED END CAPS
14. BELOW GRADE DRYWELL AND DRAIN LINE CONNECTED FROM THE NEW FOUNDATION DRAIN. RE: CIVIL

DAO ARCHITECTURE

7230 Meade St.
Westminster, CO 80030

Phone: 720.273.0431
Email: dan@daoarch.com
Web: www.daoarch.com

Westminster Public Schools

2026 Bond Projects - ECC Renovations
8030 Irving St. Westminster, CO 80031


DAO No.:2025-033

September 25, 2026

First Floor Plans

A1.0


Autodesk Docs://WPS 2026 Bond Projects - ECC Renovations/WPS ECC (Revit 2026).rvt
9/25/2026 6:01:21 AM

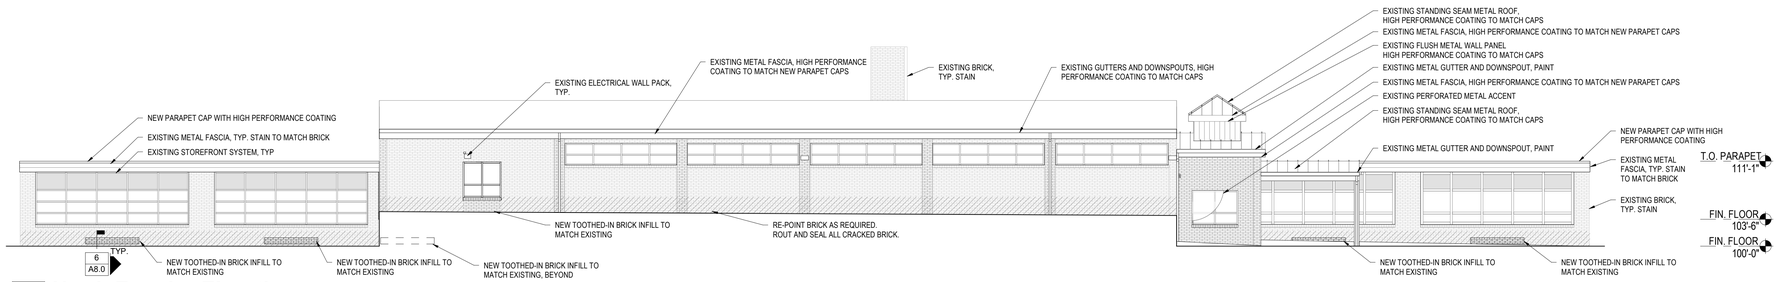

1 North Exterior Elevation

SCALE: 1/8" = 1'-0"


1 | A1.0

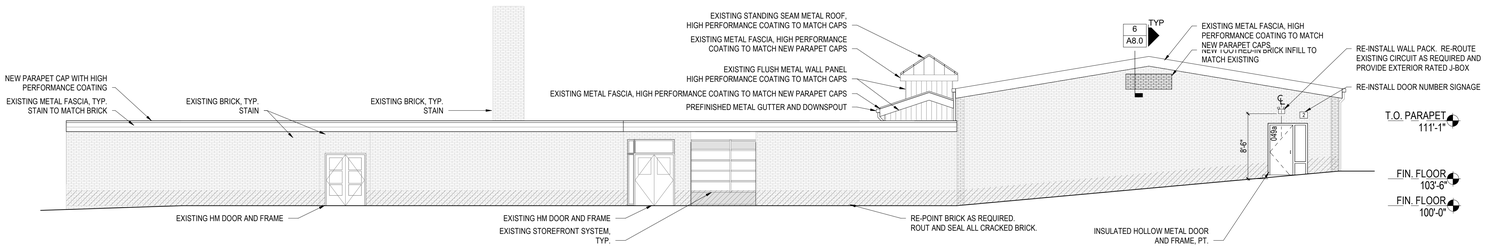

2 East Exterior Elevation

SCALE: 1/8" = 1'-0"


1 | A1.0

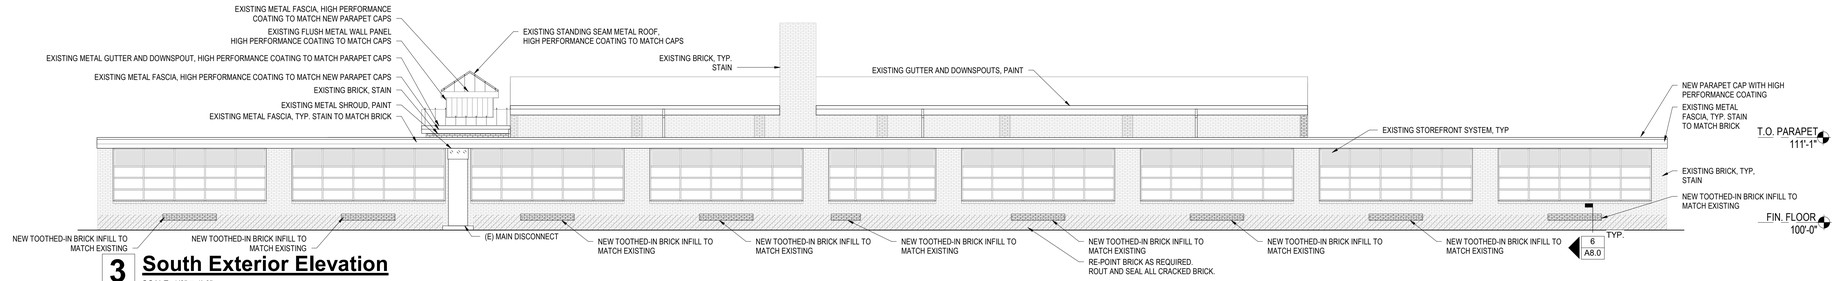

3 South Exterior Elevation

SCALE: 1/8" = 1'-0"

1 | A1.0

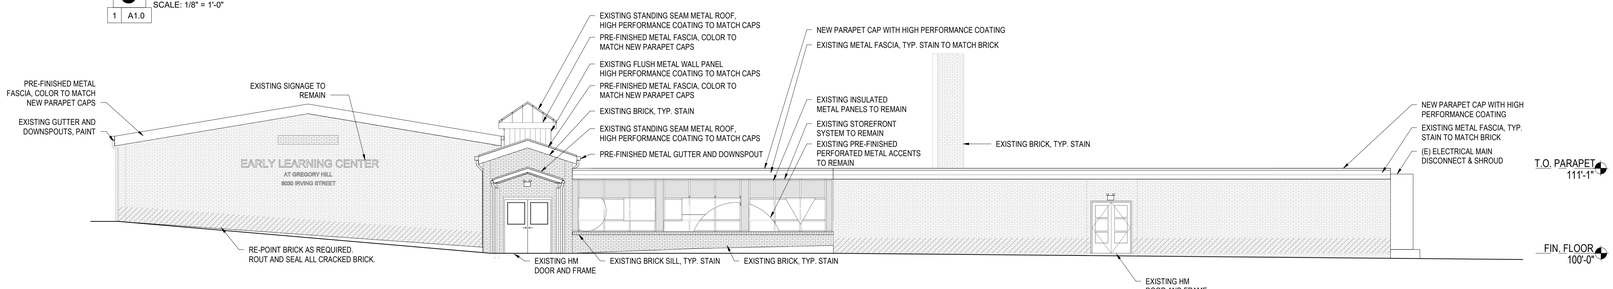

4 West Exterior Elevation

SCALE: 1/8" = 1'-0"

1 | A1.0

BASIS OF DESIGN LEGEND

EXISTING BRICK

ALL BRICK TO BE STAINED, BASIS OF DESIGN: BRICK IMAGING, COLOR SELECTED BY ARCHITECT

NEW PRE-FINISHED PARAPET CAPS AND FLASHING, BASIS OF DESIGN: SHERWIN-WILLIAMS GENESIS. COLOR: COPPER PENNY

BRICK REPAIR SCOPE GENERAL NOTES:

1. CONTRACTOR TO FIELD VERIFY EXTENTS OF ALL CRACKED AND/OR DAMAGED BRICK. CONFIRM WITH OWNER FOR DIRECTION ON REPAIR AND REPLACEMENT
2. CONTRACTOR TO PROVIDE NOT-TO-EXCEED PRICING FOR BRICK RE-POINTING AND REPAIR IN AREAS INDICATED ON THE DRAWINGS, ESTIMATED AT 1,800 SF. CONTRACTOR TO PROVIDE UNIT PRICING FOR ADDITIONAL AREAS OF REPAIR, AND/OR TO CREDIT AREAS INDICATED THAT ARE FOUND TO NOT NEED REPAIR.

DAO ARCHITECTURE

7230 Meade St.
Westminster, CO 80030

Phone: 720.273.0431
Email: dan@daoarch.com
Web: www.daoarch.com

Westminster Public Schools

2026 Bond Projects - ECC Renovations
8030 Irving St. Westminster, CO 80031


DAO No.:2025-033

September 25, 2026

Exterior Elevations

A2.0


Autodesk Docs://WPS 2026 Bond Projects - ECC Renovations/WPS ECC (Revit 2026).rvt
9/25/2026 8:01:23 AM

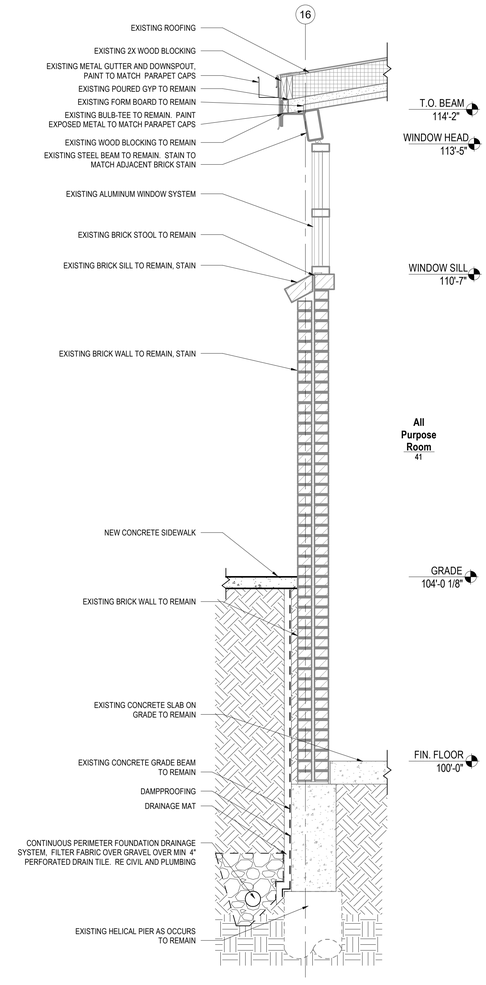

1 Wall Section at North Gym Wall

SCALE: 3/4" = 1'-0"


1 A1.0

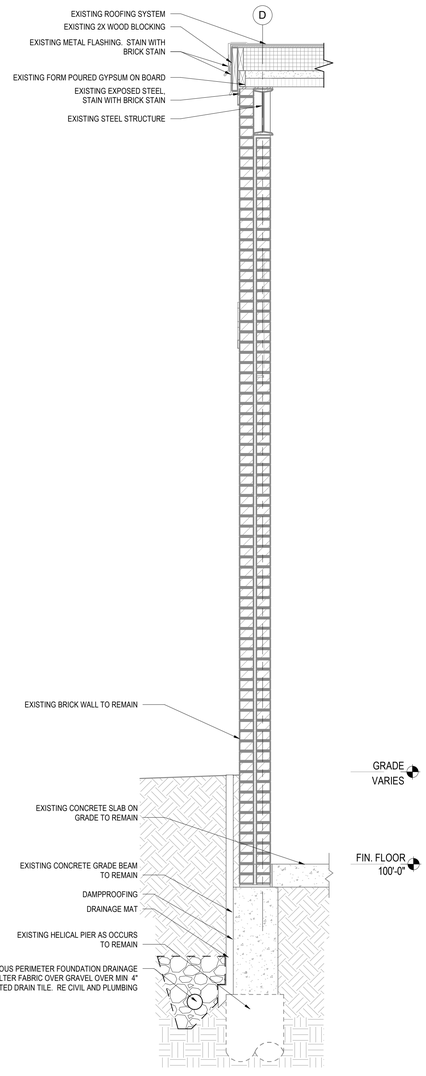

2 Wall Section at West Gym Wall

SCALE: 3/4" = 1'-0"


1 A1.0

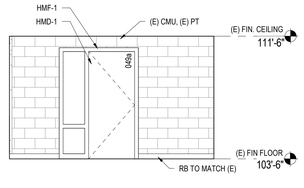

3 Clinic (049) - East

SCALE: 1/4" = 1'-0"

1 A1.0

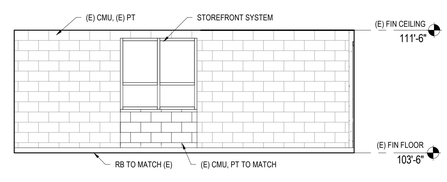

4 Clinic (049) - North

SCALE: 1/4" = 1'-0"

1 A1.0

DAO ARCHITECTURE

7230 Meade St.
Westminster, CO 80030

Phone: 720.273.0431
Email: dan@daoarch.com
Web: www.daoarch.com

Westminster Public Schools

2026 Bond Projects - ECC Renovations
8030 Irving St. Westminster, CO 80031


DAO No.:2025-033

September 25, 2026

Wall Sections, Interior Elevations

A4.0


Autodesk Docs://WPS 2026 Bond Projects - ECC Renovations/WPS ECC (Revit 2025).rvt
9/25/2026 8:01:23 AM

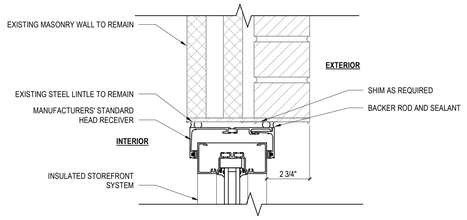

1 Window Infill - Head

SCALE: 3" = 1'-0"


10 | A8.0

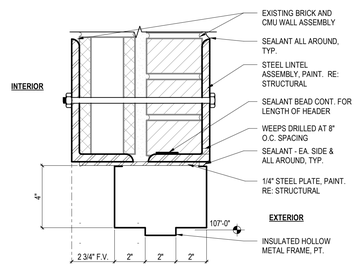

2 Hollow Metal Head


SCALE: 3" = 1'-0"

10 | A8.0

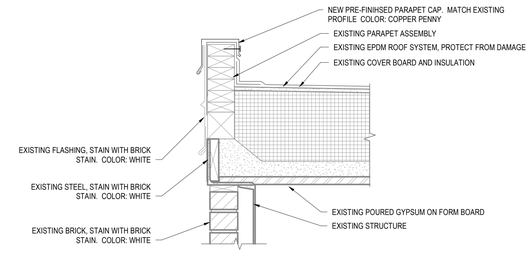

3 New Parapet Cap


SCALE: 1 1/2" = 1'-0"

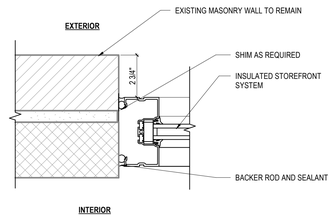

4 Window Infill - Jamb

SCALE: 3" = 1'-0"


10 | A8.0

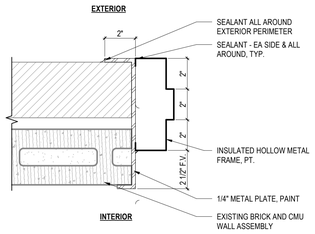

5 Hollow Metal Jamb

SCALE: 3" = 1'-0"


10 | A8.0

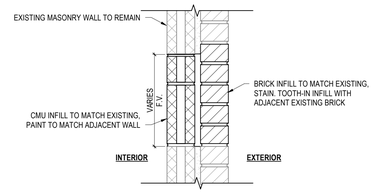

6 Louver Infill Detail

SCALE: 1 1/2" = 1'-0"


1 | A2.0

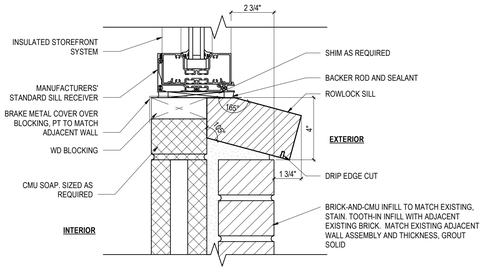

7 Window Infill - Sill

SCALE: 3" = 1'-0"


10 | A8.0

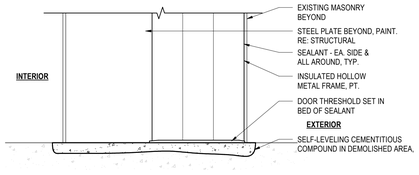

8 Hollow Metal Sill

SCALE: 3" = 1'-0"

10 | A8.0

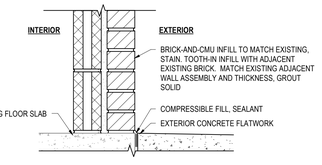

9 Door Infill Detail


SCALE: 1 1/2" = 1'-0"

1 | A1.0

DOOR AND FRAME SCHEDULE

IDENTIFICATION			DOOR						
DOOR NO.	ROOM NO.	ROOM NAME	DIMENSIONS WIDTH	HEIGHT	TYPE	FRAME TYPE	DOOR/FRAME FIRE RATING	HARDWARE	REMARKS
049a	49	Health Clinic	3' - 0"	7' - 0"	HMD-1	HMF-1		01	Storeroom, Card Reader

NOTE:
(E) = EXISTING DOOR AND FRAME
1. GENERAL CONTRACTOR TO VERIFY EXISTING DOORS AND/OR FRAMES AND COORDINATE REQUIRED PREPARATION.
2. DO NOT PAINT ANY EXISTING PRE-FINISHED MULLIONS WHICH ARE TO REMAIN.
3. NEW DOOR LITES SHALL BE PROVIDED WITH THE ANEMOSTAT LOW-PRO INSTALLATION KIT.

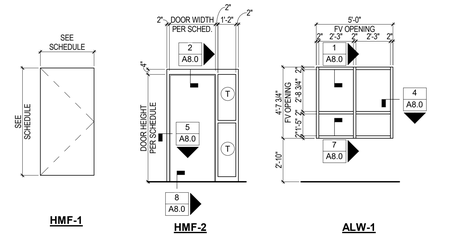

T INDICATES TEMPERED GLAZING AT THESE LOCATIONS


MAXIMUM ASSEMBLY U-FACTOR FOR:
EXTERIOR DOORS: U-0.37
EXTERIOR STOREFRONT: U-0.36

BASIS-OF-DESIGN:
1. EXTERIOR HOLLOW METAL DOORS: CURRIES 707 Q-MAX OR EQUAL
2. EXTERIOR STOREFRONT: KAWNEER 451 UT WITH INSULATED GLAZING. COLOR:CLEAR ANNODIZED

PROVIDE AND INSTALL 3M S800 SECURITY FILM AND CAULKING AT ENTRY DOORS AND ASSOCIATED SIDELITES. COORDINATE FINAL LOCATIONS WITH THE OWNER

10 Door and Frame Types

SCALE: 1/4" = 1'-0"

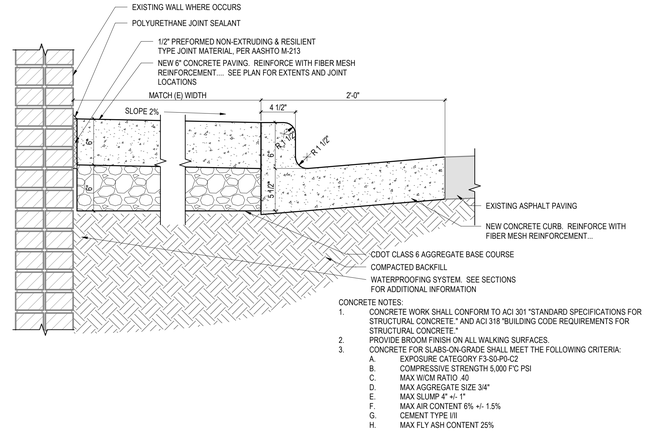

CONCRETE NOTES:
1. CONCRETE WORK SHALL CONFORM TO ACI 301 "STANDARD SPECIFICATIONS FOR STRUCTURAL CONCRETE." AND ACI 318 "BUILDING CODE REQUIREMENTS FOR STRUCTURAL CONCRETE."
2. PROVIDE BROOM FINISH ON ALL WALKING SURFACES.
3. CONCRETE FOR SLABS-ON-GRADE SHALL MEET THE FOLLOWING CRITERIA:
   - A. EXPOSURE CATEGORY F3-S0-P0-C2
   - B. COMPRESSIVE STRENGTH 5,000 F'C PSI
   - C. MAX W/CM RATIO .40
   - D. MAX AGGREGATE SIZE 3/4"
   - E. MAX SLUMP 4" +/- 1"
   - F. MAX AIR CONTENT 6% +/- 1.5%
   - G. CEMENT TYPE I/II
   - H. MAX FLY ASH CONTENT 25%

11 Typ. Curb and Sidewalk

SCALE: 1 1/2" = 1'-0"

1 | A1.0

DAO ARCHITECTURE

7230 Meade St.
Westminster, CO 80030

Phone: 720.273.0431
Email: dan@daoarch.com
Web: www.daoarch.com

Westminster Public Schools

2026 Bond Projects - ECC Renovations
8030 Irving St. Westminster, CO 80031

DAO No.:2025-033

September 25, 2026

Details, Door Schedule

A8.0

Autodesk Docs://WPS 2026 Bond Projects - ECC Renovations/WPS ECC (Revit 2026).rvt
9/25/2026 8:01:23 AM

STRUCTURAL GENERAL NOTES

01-GENERAL REQUIREMENTS

1. GOVERNING DESIGN CODES:
A. COLORADO STATE BUILDING CODE: INTERNATIONAL BUILDING CODE (IBC-21).
B. MINIMUM DESIGN LOADS FOR BUILDINGS AND OTHER STRUCTURES (ASCE 7-16).
C. BUILDING CODE REQUIREMENTS FOR STRUCTURAL CONCRETE (ACI 318-19).
D. BUILDING CODE REQUIREMENTS FOR MASONRY STRUCTURES (TMS 402-16).
E. AISC MANUAL OF STEEL CONSTRUCTION (AISC 360-16).

2. DESIGN LOAD CRITERIA:
A. RISK CATEGORY: III
B. DEAD LOADS:
- EXISTING BUILDING ROOF (1960 --GYPCRETE OVER GLULAM BEAMS) = 28 PSF
C. LIVE LOADS:
- CLASSROOMS = 40 PSF
- STAIRS AND FIRST FLOOR CORRIDORS = 100 PSF
- LIGHT STORAGE = 125 PSF
D. SNOW LOADS:
- GROUND SNOW LOAD, P_g = 40 PSF
- FLAT ROOF SNOW LOAD, P_f = 31 PSF
- SNOW EXPOSURE FACTOR, C_e = 1.0
- SNOW LOAD IMPORTANCE FACTOR, I_s = 1.1
- THERMAL FACTOR, C_t = 1.0
- SNOW DRIFT LOADING PER CODE
E. WIND LOADS:
- ULTIMATE WIND SPEED (3-SECOND GUST) = 135 MPH
- WIND EXPOSURE CATEGORY = C
- GROUND ELEVATION FACTOR, K_e = 0.85
- INTERNAL PRESSURE COEFFICIENT, GC_{pi} = +/- 0.18
- COMPONENTS AND CLADDING ULTIMATE WIND PRESSURES (PSF):

ZONE	20 FT²	50 FT²	100 FT²
ROOF INTERIOR (ZONE 1)	+16 / -50	+16 / -46	+16 / -42
ROOF END (ZONE 2)	+16 / -67	+16 / -60	+16 / -56
ROOF CORNER (ZONE 3)	+16 / -88	+16 / -76	+16 / -67
WALL INTERIOR (ZONE 4)	+30 / -32	+28 / -31	+27 / -29
WALL END (ZONE 5)	+30 / -39	+28 / -35	+27 / -32

F. SEISMIC LOADS:
- SEISMIC IMPORTANCE FACTOR, I_E = 1.25
- SITE CLASS = D
- Ss = 0.211g
- S1 = 0.058g
- Sds = 0.225g
- Sd1 = 0.093g
- SEISMIC DESIGN CATEGORY B
- BASIC SEISMIC FORCE RESISTING SYSTEMS:
  ORDINARY PLAIN MASONRY SHEAR WALLS, R = 1.5
- OVERSTRENGTH FACTOR Ω_0 = 3
- DEFLECTION AMPLIFICATION FACTOR, C_d = 3
- SEISMIC RESPONSE COEFFICIENT, C_S = 0.188
G. RAIN INTENSITY = 2.4 INCH / HOUR

3. STRUCTURAL SCOPE NARRATIVE:
A. STRUCTURAL SCOPE FOR THE RENOVATION INCLUDES INSTALLING A NEW STEEL LINTEL AT ONE NEW DOOR OPENING THROUGH A MASONRY WALL.
B. STRUCTURAL MEMBERS CARRYING GRAVITY LOADS INCLUDE A NEW STEEL LINTEL THAT WAS DESIGNED PER THE REQUIREMENTS OF THE INTERNATIONAL BUILDING CODE.
C. THIS DESCRIPTION IS FOR GENERAL ORIENTATION ONLY. THE GENERAL CONTRACTOR IS RESPONSIBLE FOR ALL SCOPE ITEMS DESCRIBED IN THE DRAWINGS AND PROJECT SPECIFICATIONS AS WELL AS FOR ALL MATERIAL AND LABOR THAT CAN BE REASONABLY INFERRED THERE FROM.

4. STRUCTURAL OBSERVATION:
A. STRUCTURAL OBSERVATIONS OF NEW STRUCTURAL ELEMENTS FOR GENERAL CONFORMANCE TO THE CONSTRUCTION DOCUMENTS WILL BE PROVIDED BY THE ENGINEER FOR THE FOLLOWING TYPES OF WORK:
1. STEEL LINTEL INSTALLATION
2. CONTRACTOR TO PROVIDE AT LEAST 24 HOURS ADVANCE NOTICE FOR OBSERVATIONS.

5. STATEMENT OF SPECIAL INSPECTIONS AND QUALITY CONTROL:
A. SPECIAL INSPECTIONS AND TESTING SHALL BE PER THE STATEMENT OF SPECIAL INSPECTIONS BELOW.

STATEMENT OF SPECIAL INSPECTIONS

SPECIAL INSPECTIONS:
A. SPECIAL INSPECTION AND TESTING SHALL BE PERFORMED AS REQUIRED BY THE LOCAL JURISDICTION, THE BUILDING CODE AND THE CONSTRUCTION DOCUMENTS.
B. COORDINATE AND SCHEDULE INSPECTION AND TESTING PRIOR TO THE START OF WORK REQUIRING INSPECTION AND TESTING WHILE PROVIDING SPECIAL INSPECTOR REASONABLE NOTICE.
C. ALL DEFICIENCIES SHALL BE CORRECTED FOR ACCEPTANCE BY THE TESTING AGENCY.
D. INSPECTIONS PREFORMED BY THE LOCAL JURISDICTION DO NOT REPLACE INSPECTION OR TESTING REQUIRED BY THE OWNERS TESTING AGENCY.
E. SPECIAL INSPECTION AND TESTING IS REQUIRED FOR THE ITEMS SHOWN IN THE SPECIAL INSPECTIONS AND TESTING TABLE.
F. THE OWNER'S TESTING AGENCY SHALL PERFORM TESTING AND SPECIAL INSPECTIONS REQUIRED BY THE STRUCTURAL DOCUMENTS, BUILDING CODE AND THE LOCAL AUTHORITY. THE TESTING AGENCY SHALL COMPLY WITH ASTM E329 AND UPON COMPLETION OF WORK, THE TESTING AGENCY SHALL FURNISH A CERTIFICATE OF COMPLIANCE, SIGNED BY THE PROFESSIONAL ENGINEER OVERSEEING SPECIAL INSPECTIONS AND TESTING. THE PROFESSIONAL ENGINEER MUST BE REGISTERED AND LICENSED IN THE STATE WHERE THE PROJECT IS LOCATED.
G. THE TESTING AGENCY'S INDIVIDUAL OVERSEEING TESTING AND INSPECTION OF SOILS AND FOUNDATIONS SHALL BE A PROFESSIONAL ENGINEER PRACTICING THE DISCIPLINE OF GEOTECHNICAL ENGINEERING, REFERRED TO AS THE GEOTECHNICAL ENGINEER IN THE STRUCTURAL PORTION OF THE CONSTRUCTION DOCUMENTS. THE GEOTECHNICAL ENGINEER IS RESPONSIBLE FOR TESTING AND INSPECTIONS OF SOILS, EARTHWORK AND FOUNDATIONS FOR CONFORMANCE TO THE FOUNDATION DESIGN AND THE GEOTECHNICAL REPORT. SEE FOUNDATION SECTION OF THE GENERAL NOTES.

SPECIAL INSPECTIONS AND TESTING

CATEGORY/MATERIAL	COMPONENT/WORK	FREQUENCY	
		PERIODIC	CONTINUOUS
STRUCTURAL STEEL	VERIFY WELDER QUALIFICATIONS		X
	VERIFY CONNECTION ERECTION AND ASSEMBLY	X	
	VERIFY BOLTS IN SNUG TIGHT JOINTS	X	
	VERIFY SINGLE PASS FILLET WELDS 5/16" OR LESS PER AWS D1.1	X	
	VERIFY MEMBER SIZES, LOCATIONS AND CONNECTIONS	X	

NOTES:
1. SPECIAL INSPECTION AND TESTING SHALL CONFORM TO CHAPTER 17 OF THE IBC AND THE LOCAL BUILDING DEPARTMENT
2. PERIODIC INSPECTIONS ARE DEFINED AS PART-TIME OR INTERMITTENT OF THE WORK. IT IS THE SPECIAL INSPECTOR'S RESPONSIBILITY TO DETERMINE AND COORDINATE THE FREQUENCY AND DURATION OF THE INSPECTION RELATIVE TO THE CONTRACTOR'S SCHEDULE AND SEQUENCING OF THE WORK IN ORDER TO MEET THE INSPECTION AND REPORTING REQUIREMENTS.

02-MASONRY

1. CONCRETE MASONRY UNITS:
A. ALL CONCRETE MASONRY WORK INCLUDING FABRICATION AND PLACEMENT OF REINFORCING SHALL BE PERFORMED IN ACCORDANCE WITH REQUIREMENTS GIVEN IN ACI 530 AND ACI 530.1.
B. MASONRY BLOCK UNITS SHALL CONFORM TO ASTM C90 (LIGHTWEIGHT BLOCK).
C. MORTAR USED IN MASONRY CONSTRUCTION SHALL CONFORM TO ASTM C270 AS FOLLOWS:
1. EXTERIOR WALLS AND INTERIOR BEARING WALLS: TYPE S
2. FOUNDATION WALLS AND WALLS EXPOSED TO EARTH: TYPE M
D. GROUT USED IN MASONRY CONSTRUCTION SHALL CONFORM TO ASTM C476 AND SHALL DEVELOP 3,000 PSI (MINIMUM) COMPRESSIVE STRENGTH IN 28-DAYS WHEN TESTED IN ACCORDANCE WITH C1019.
E. MASONRY SHALL DEVELOP 1,500 PSI (MINIMUM) COMPRESSIVE STRENGTH (f'm) IN 28 DAYS WHEN TESTED IN ACCORDANCE WITH PROJECT SPECIFICATIONS.
F. ALL REINFORCING STEEL SHALL HAVE A MINIMUM YIELD STRENGTH OF 60,000 PSI AND SHALL MEET THE REQUIREMENTS OF ASTM A615 OR ASTM A706.
G. HORIZONTAL JOINT REINFORCING SHALL CONFORM TO ASTM A951 (LADDER-TYPE) WITH CROSS WIRES AT 16" ON CENTER. SIDE RODS SHALL BE SIZE AND SHALL CONFORM TO ASTM A82.
H. REINFORCING DETAILING:
1. ALL REINFORCING SHALL BE DETAILED IN ACCORDANCE WITH ACI 530 AND ACI 530.1
2. VERTICAL REINFORCING SHALL EXTEND THE FULL HEIGHT OF THE WALL AND SHALL BE GROUTED IN PLACE.
3. CONTINUOUS REINFORCING MAY BE SPLICED AS REQUIRED USING BARS OF LONGEST PRACTICAL LENGTH.
4. HORIZONTAL REINFORCING SHALL BE CONTINUOUS AROUND WALL CORNERS AND INTERSECTIONS.
5. VERTICAL REINFORCING SHALL BE DOWELED INTO FOUNDATION OR SLAB SUPPORTING MASONRY. PROVIDE DOWELS OF ADEQUATE LENGTH FOR DEVELOPMENT LENGTH INTO FOUNDATION AND LAP SPLICE PROJECTION ABOVE. DOWEL SIZE AND SPACING SHALL MATCH VERTICAL REINFORCING.
6. LAP SPLICE MASONRY WALL REINFORCING A MINIMUM OF 48 BAR DIAMETERS.
7. BARS SHALL BE HELD SECURELY IN PLACE AT 4'-0 ON CENTER VERTICALLY USING PREFABRICATED REBAR POSITIONERS.
I. MINIMUM WALL REINFORCING:
1. PROVIDE 1-#5 BAR AT ALL CORNERS, ENDS OF WALLS, EACH SIDE OF OPENINGS AND EACH SIDE OF CONTROL JOINTS.
2. PROVIDE HORIZONTAL JOINT LADDER-TYPE REINFORCING AT 16" ON CENTER UNLESS NOTED OTHERWISE. PROVIDE PREFABRICATED JOINT REINFORCING ASSEMBLIES FOR CORNERS AND INTERSECTIONS. LAP SPLICE JOINT REINFORCING 8" KEEPING CELL OPENING CLEAR OF CROSS WIRES.
J. GROUTING:
1. FILL ALL BLOCK CELLS CONTAINING REINFORCING WITH GROUT.
2. FILL ALL VOIDS AND CELLS WITH GROUT FOR A DISTANCE OF 24" BELOW AND 16" EACH SIDE OF ALL BEAM AND LINTEL REACTIONS OR OTHER CONCENTRATED LOADS UNLESS SHOWN OTHERWISE.
3. FILL ALL VOIDS AND CELLS OF MASONRY BLOCK SUPPORTING SLABS OR STEEL DECK FOR A DISTANCE OF 8" BELOW BEARING ELEVATION.
4. GROUT CELLS CONTAINING ANCHORS OR EMBEDMENTS PLUS ADJACENT CELLS BELOW, ABOVE AND EACH SIDE.
5. ALL REINFORCING SHALL HAVE A MINIMUM GROUT COVER OF ONE BAR DIAMETER.
6. FILL ALL CELLS BELOW GRADE WITH GROUT.
K. MASONRY WALL CONSTRUCTION SHALL BE RUNNING BOND UNLESS NOTED OTHERWISE ON THE DRAWINGS.
L. TUCKPOINT MORTAR JOINTS AS REQUIRED AFTER INSTALLING NEW STEEL LINTELS.
M. CLEAN OUT ANY CRACKED MORTAR JOINTS IN THE EXISTING CMU BEARING WALLS AND TUCKPOINT JOINT WITH NEW MORTAR.

03-STEEL

1. STRUCTURAL STEEL:
A. STRUCTURAL STEEL SHALL BE DETAILED, FABRICATED AND ERECTED IN ACCORDANCE WITH THE AISC MANUAL OF STEEL CONSTRUCTION AND THE AISC CODE OF STANDARD PRACTICE. (REFERENCED EDITIONS).
B. MATERIAL REQUIREMENTS: STRUCTURAL STEEL SHALL CONFORM TO THE FOLLOWING DESIGNATIONS UNLESS NOTED OTHERWISE ON THE DRAWINGS:
1. ANGLES, CHANNELS AND PLATES: ASTM A36 OR ASTM A572, GRADE 50
2. THREADED RODS: ASTM A36
3. WELDING ELECTRODES: AWS D1.1 E70 SERIES
C. SHOP PRIMING OF STEEL: SEE ARCHITECTURAL DRAWINGS FOR REQUIREMENTS FOR PRIMING OF STRUCTURAL STEEL. OMIT PRIMER ON SURFACES ENCLOSED IN CONCRETE, SURFACES TO BE WELDED.
D. WELDED CONNECTIONS:
1. ALL WELDERS SHALL HAVE EVIDENCE OF PASSING THE AWS STANDARD QUALIFICATION TESTS.
2. WELD SIZES AND LENGTHS ARE SHOWN ON THE DRAWINGS. WELD SIZES ARE THE NET EFFECTIVE SIZE REQUIRED. INCREASE WELD SIZE IF GAPS EXIST AT FAYING SURFACE.
3. MINIMUM FILLET WELD SIZE IS 3/16".
4. WELDS SHALL BE CONTINUOUS UNLESS SHOWN OTHERWISE.
E. STRUCTURAL STEEL SHALL NOT BE CUT IN FIELD OR MODIFIED WITHOUT PRIOR APPROVAL OF THE ENGINEER. SPLICING STEEL MEMBERS IS NOT PERMITTED EXCEPT WHERE SHOWN ON THE DRAWINGS OR WHERE APPROVED BY THE ENGINEER.


04-INSTRUCTIONS AND COORDINATION

1. COORDINATION:
A. ANY DIFFERENCES BETWEEN THE ARCHITECTURAL AND STRUCTURAL DRAWINGS SHALL BE REPORTED TO THE ARCHITECT BEFORE PROCEEDING WITH THE WORK.
B. CONFLICTS WITHIN THE STRUCTURAL DRAWINGS OR BETWEEN THE STRUCTURAL DRAWINGS AND GENERAL NOTES SHALL BE REPORTED TO THE STRUCTURAL ENGINEER FOR RESOLUTION BEFORE PROCEEDING WITH MODIFICATIONS OR ADJUSTMENT.

2. EXISTING STRUCTURES:
A. CONTRACT DOCUMENTS HAVE BEEN PREPARED USING SITE OBSERVATION AND EXISTING STRUCTURAL DRAWINGS BY ROLAND M. JOHNSON ARCHITECT DATED NOVEMBER 22, 1960.
B. CONTRACTOR SHALL NOTIFY THE ARCHITECT AND ENGINEER OF ANY CONDITIONS WHICH ARE NOT NOW KNOWN OR NOT PER THE CONTRACT DOCUMENTS. EXAMPLES INCLUDE:
1. SIZES OR DIMENSIONS OTHER THAN THOSE SHOWN
2. DAMAGE OR DETERIORATION OF EXISTING STRUCTURE OR COMPONENTS
3. ITEMS NOTED AS EXISTING ON THE DRAWINGS BUT NOT FOUND IN THE FIELD

3. SUBMITTALS:
A. THE FOLLOWING DOCUMENTS SHALL BE SUBMITTED TO THE STRUCTURAL ENGINEER, IN AN INDUSTRY STANDARD SUBMITTAL FORMAT, FOR REVIEW AND APPROVAL PRIOR TO INSTALLATION / CONSTRUCTION OF RESPECTIVE ITEMS / MATERIALS. SUBMITTALS SHALL BE PROVIDED A MINIMUM OF (5) DAYS PRIOR TO FABRICATION AND/OR INSTALLATION TO ALLOW ADEQUATE TIME FOR REVIEW AND REVISIONS:
1. STRUCTURAL STEEL SHOP DRAWINGS SHOWING ALL DIMENSIONS, MEMBER LAYOUT AND CONNECTIONS BETWEEN MEMBERS.

4.. INSTRUCTIONS TO CONTRACTOR:
A. TEMPORARY BRACING: DURING ERECTION OF THE BUILDING, THE CONTRACTOR SHALL BE RESPONSIBLE FOR THE DESIGN AND PLACEMENT OF TEMPORARY BRACING TO WITHSTAND ALL LOADS TO WHICH THE STRUCTURE MAY BE SUBJECTED INCLUDING LATERAL LOADS, STOCKPILES OF MATERIAL, AND EQUIPMENT. BRACING SHALL BE LEFT IN PLACE AS LONG AS NECESSARY FOR SAFETY AND UNTIL ALL STRUCTURAL FRAMING AND ROOF DIAPHRAGMS ARE IN PLACE WITH CONNECTIONS COMPLETE.
B. STORAGE: THE CONTRACTOR SHALL NOT STOCKPILE MATERIAL OR EQUIPMENT IN A MANNER THAT EXCEEDS THE LOAD CAPACITY OF THE STRUCTURE OR CAUSES DAMAGE OR EXCESSIVE DEFLECTION OF STRUCTURAL ELEMENTS.

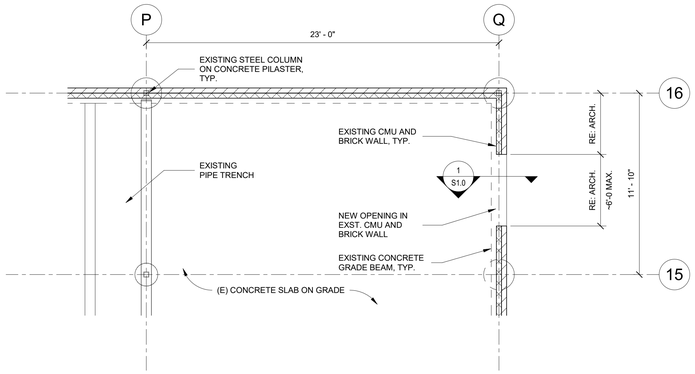

FIRST FLOOR PARTIAL PLAN - NORTHEAST

SCALE: 1/4" = 1'-0"

NOTES:
1. EXISTING FLOOR SLAB IS A 6" THICK CONCRETE SLAB ON GRADE, TO BE VERIFIED IN FIELD. EXISTING STRUCTURE CONSISTS OF STEEL BEAMS AND COLUMNS SUPPORTED WITH CONCRETE GRADE BEAMS AND DRILLED PIERS. CONTACT ENGINEER IF CONDITIONS UNCOVERED IN THE FIELD DIFFER FROM THOSE SHOWN ON PLAN.
2. REFER TO STRUCTURAL GENERAL NOTES AND TYPICAL DETAILS FOR ADDITIONAL FRAMING INFORMATION.
3. CONTRACTOR TO FIELD VERIFY ALL EXISTING CONDITIONS, DIMENSIONS, AND ELEVATIONS SHOWN AND CONTACT ARCHITECT AND STRUCTURAL ENGINEER WITH ANY DISCREPANCIES PRIOR TO STARTING WORK.

1 S1.0 NEW STEEL LINTEL AT EXTERIOR MASONRY WALL

SCALE: 1 1/2" = 1'-0"

DAO ARCHITECTURE
7230 Meade St.
Westminster, CO 80030
Phone: 720.273.0431
Email: dan@daoarch.com
Web: www.daoarch.com

TJF STRUCTURAL design, inc.
5995 GREENWOOD PLAZA BLVD, SUITE 120
GREENWOOD VILLAGE, CO 80111
(303) 618-4555

Rev. #	Description	Rev. Date
Revision Schedule		

Westminster Public Schools

E.C.C. Gym Infiltration Reno.

8030 Irving Street
Westminster, CO 80031


TJF No.: 26024

September 25, 2026

GENERAL NOTES, DETAILS AND PLAN

S1.0

C:\TJF Structural\TJF Projects\2026 Projects\26024 - WPS 2026 Bond Projects\CAD\Structural\WPS-ECC_Structural_R25.rvt
9/23/2026 2:05:49 PM

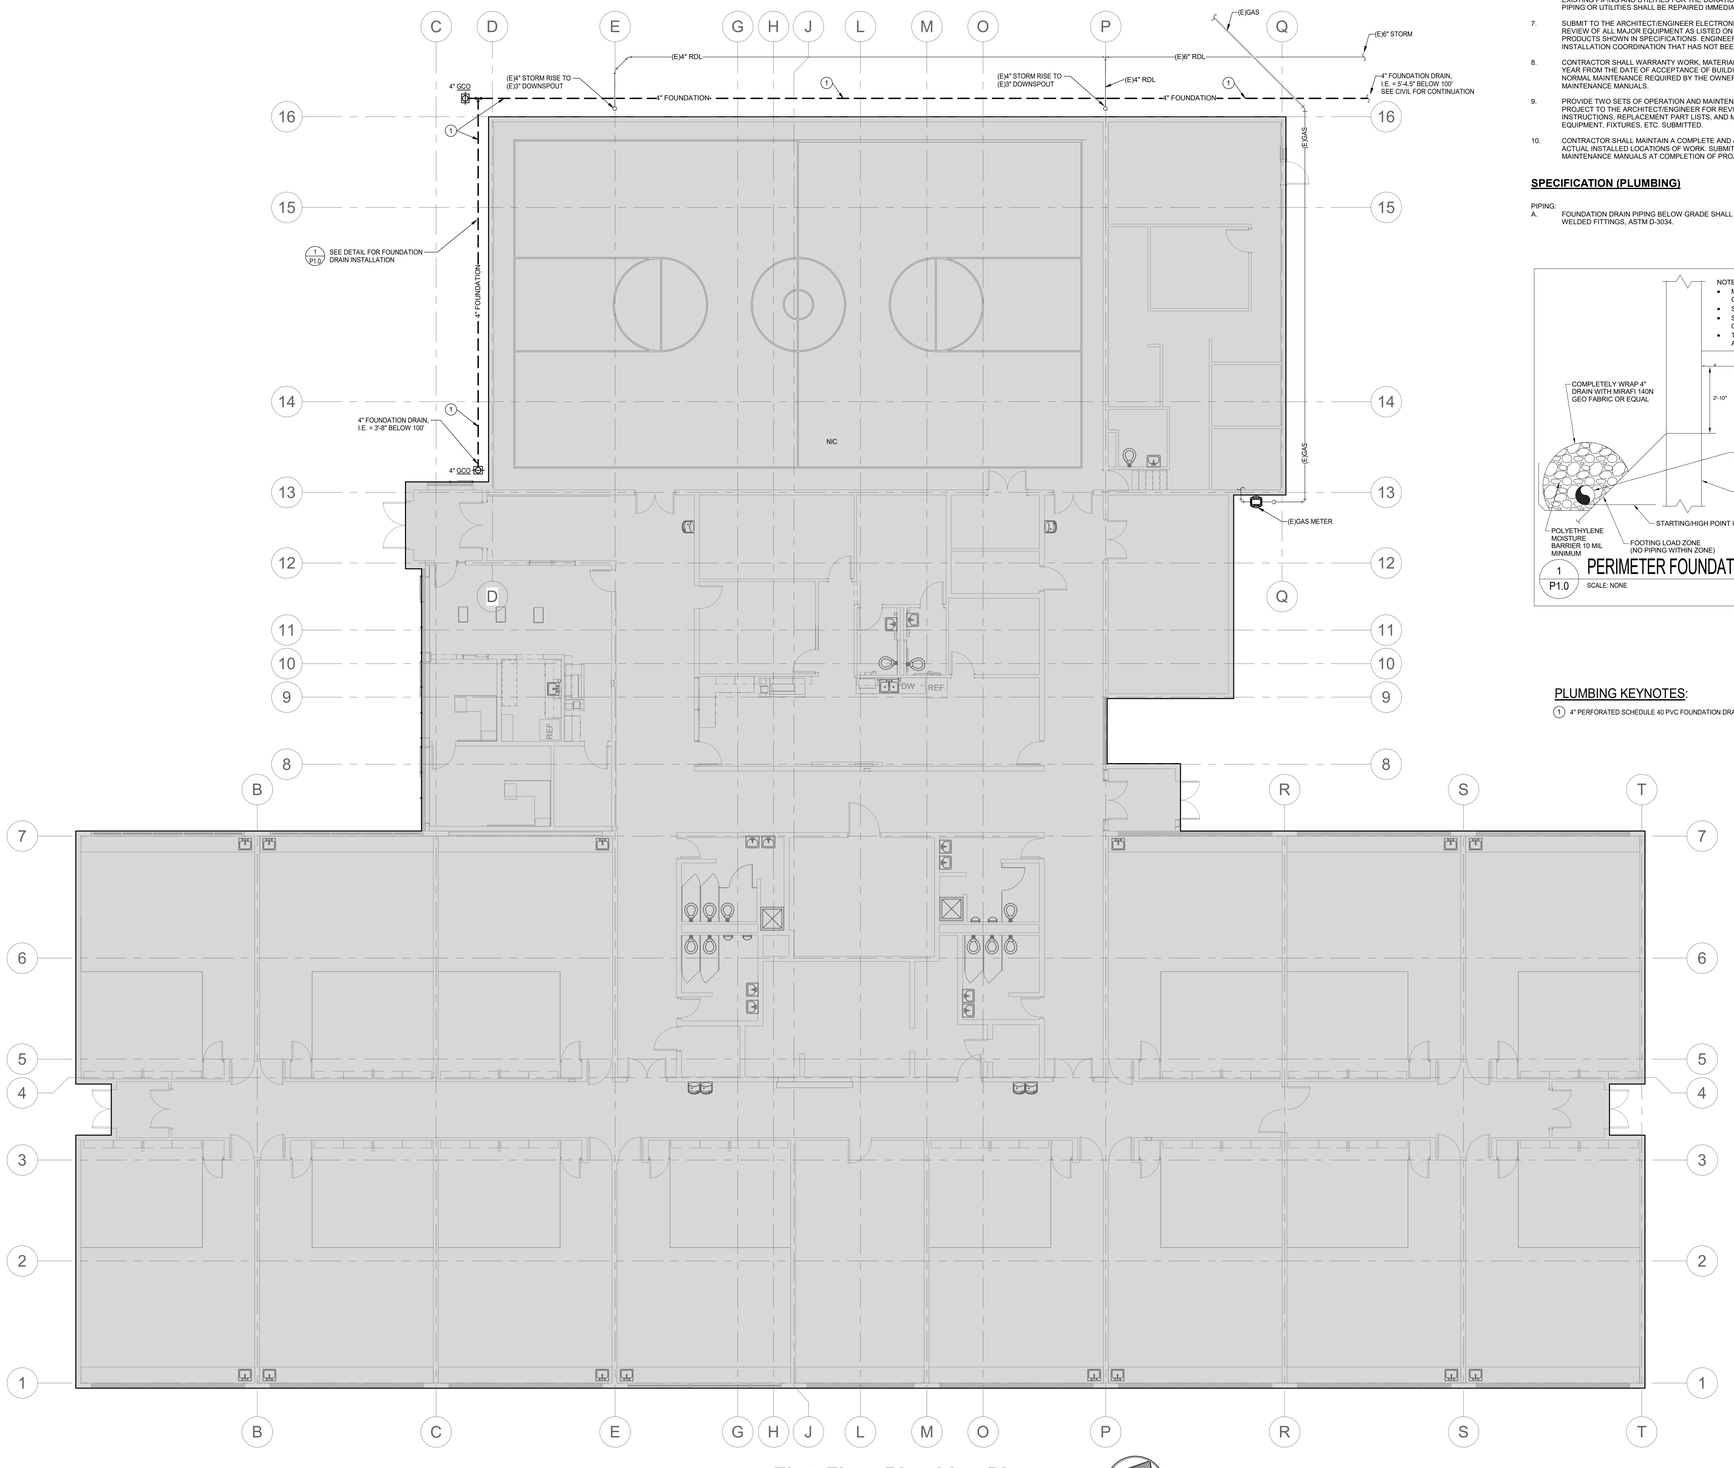

First Floor Plumbing Plan

SCALE: 1/8" = 1'-0"

PLUMBING DEMOLITION GENERAL NOTES

1. COORDINATE DEMOLITION REQUIREMENTS WITH THE GENERAL CONTRACTOR.
2. COORDINATE EXTENT OF DEMOLITION WITH THE NEW CONSTRUCTION AS SHOWN IN THESE DOCUMENTS.
3. EXISTING PLUMBING PIPING, EQUIPMENT ETC IS SHOWN LIGHT.
4. THE GENERAL CONTRACTOR SHALL MAKE REPAIRS TO ALL EXISTING BUILDING COMPONENTS THAT HAVE BEEN AFFECTED BY THE DEMOLITION OF PLUMBING SYSTEMS.


PLUMBING GENERAL NOTES

1. FIELD VERIFY EXACT LOCATION OF ALL CONNECTIONS PRIOR TO CONSTRUCTION.
2. CONTRACTOR SHALL INSPECT SITE TO THOROUGHLY FAMILIARIZE HIMSELF WITH THE AREA OF WORK. ANY DISCREPANCES BETWEEN THESE DOCUMENTS AND ACTUAL CONDITIONS SHALL BE REPORTED TO THE ARCHITECT/ENGINEER FOR RESOLUTION PRIOR TO BID PRICING. NO EXTRAS WILL BE ALLOWED DUE TO LACK OF KNOWLEDGE OF EXISTING CONDITIONS.
3. COMPLY WITH ALL BUILDING AND HEALTH DEPARTMENT REGULATIONS FOR PLUMBING INSTALLATION. VERIFY ALL REQUIREMENTS PRIOR TO SUBMITTING BID OR COMMENCING WORK.
4. OFFSET ALL PIPING AS REQUIRED TO AVOID STRUCTURAL MEMBERS, CANTS, FLASHING, MECHANICAL, OR ELECTRICAL EQUIPMENT.
5. PROTECT ALL EXISTING EQUIPMENT INDICATED AS REMAINING IN PLACE OR BEING RELOCATED. REPLACE DAMAGED EQUIPMENT IMMEDIATELY WITH EXACT DUPLICATE AT NO ADDITIONAL COST TO THE OWNER.
6. PLUMBING CONTRACTOR SHALL BE RESPONSIBLE FOR PROPERLY LOCATING AND PROTECTING ALL EXISTING PIPING AND UTILITIES FOR THE DURATION OF THE WORK. ANY DAMAGE CAUSED TO EXISTING PIPING OR UTILITIES SHALL BE REPAIRED IMMEDIATELY AT NO ADDITIONAL COST TO THE OWNER.
7. SUBMIT TO THE ARCHITECT/ENGINEER ELECTRONIC PDF FILES OF MECHANICAL SUBMITTALS FOR REVIEW OF ALL MAJOR EQUIPMENT AS LISTED ON DRAWING EQUIPMENT SCHEDULES, AS WELL AS PRODUCTS SHOWN IN SPECIFICATIONS. ENGINEER ASSUMED NO RESPONSIBILITY FOR EQUIPMENT OR INSTALLATION COORDINATION THAT HAS NOT BEEN SUBMITTED FOR REVIEW.
8. CONTRACTOR SHALL WARRANTY WORK, MATERIALS, AND PROPER OPERATION FOR A PERIOD OF ONE YEAR FROM THE DATE OF ACCEPTANCE OF BUILDING BY OWNER. THIS GUARANTEE SHALL NOT INCLUDE NORMAL MAINTENANCE REQUIRED BY THE OWNER AS DESCRIBED IN THE OPERATION AND MAINTENANCE MANUALS.
9. PROVIDE TWO SETS OF OPERATION AND MAINTENANCE (O&M) MANUALS FOR OWNER AT COMPLETION OF PROJECT TO THE ARCHITECT/ENGINEER FOR REVIEW. MANUALS TO INCLUDE INSTALLATION INSTRUCTIONS, REPLACEMENT PART LISTS, AND MAINTENANCE INFORMATION ON ALL MECHANICAL EQUIPMENT, FIXTURES, ETC. SUBMITTED.
10. CONTRACTOR SHALL MAINTAIN A COMPLETE AND ACCURATE SET OF RECORD DRAWINGS SHOWING ACTUAL INSTALLED LOCATIONS OF WORK. SUBMIT THESE DRAWINGS AS PART OF THE OPERATION AND MAINTENANCE MANUALS AT COMPLETION OF PROJECT.

SPECIFICATION (PLUMBING)

PIPING:

A. FOUNDATION DRAIN PIPING BELOW GRADE SHALL BE PERFORATED PVC (SDR 35) WITH SOLVENT WELDED FITTINGS, ASTM D-3034.

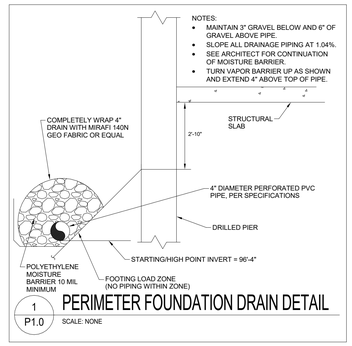

1 P1.0 PERIMETER FOUNDATION DRAIN DETAIL

SCALE: NONE

PLUMBING KEYNOTES:

1. 4" PERFORATED SCHEDULE 40 PVC FOUNDATION DRAIN SLOPED AT 1.04%.

DAO ARCHITECTURE
7230 Meade St.
Westminster, CO 80030
Phone: 720.273.0431
Email: dan@daoarch.com
Web: www.daoarch.com

The Ballard Group, Inc.
Mechanical Consulting Engineers
2525 S. Wadsworth Blvd, Suite 200
Lakewood, CO 80227
(303) 988-4514

Westminster Public Schools

E.C.C. Gym Infiltration Reno.

8030 Irving St.
Westminster, CO
80031

DAO No.:2019-001

September 25, 2026

First Floor Plumbing Plan, Details & General Notes

P1.0

Autodesk Docs://WPS 2026 Bond Projects - ECC Renovations/25094 ECC 2026 Bond Projects-PLBG-R26.rvt
9/24/2026 3:54:22 PM