Westminster Public Schools

Hodgkins Leadership Academy Classroom Conversion Project

3475 W 67th Ave, Denver, CO 80221

DAO No.: 2021-033

Construction Documents

September 25, 2026



TYP. CLASSROOM PERSPECTIVE

DRAWING INDEX

GENERAL

Cover	Cover Sheet
G0.0	Standard Symbols, Abbreviations & General Notes
G0.1	Building Code Data

ARCHITECTURE

AD1.0	Lower Level Demolition Plan
AD1.1	Main Level Demolition Plan Area 'A'
AD1.2	Main Level Demolition Plan Area 'B'
AD1.3	Lower Level Demolition RCP
AD1.4	Main Level Demolition RCP
A1.0	Lower Level Floor Plan
A1.1	Main Level Floor Plan Area 'A'
A1.2	Main Level Plan Area 'B'
A1.3	Lower Level RCP
A1.4	Main Level RCP
A6.0	Interior Elevations
A6.1	Interior Elevations
A6.2	Interior Elevations
A6.5	Corridor Elevations & Casework Sections & Door Details
A9.0	Lower Level Finish Plan
A9.1	Main Level Finish Plan Area 'A'
A9.2	Main Level Finish Plan Area 'B'

MECHANICAL

M0.0	Mechanical Cover Sheet
MD1.0	Lower Level HVAC Demolition Plan
MD1.1	Main Level HVAC Demolition Plan
M1.0	Lower Level HVAC Floor Plan
M1.1	Main Level HVAC Floor Plan

ELECTRICAL

E0.1	Electrical Notes, Legends, & Details
E0.3	Electrical One-Line Diagram
ED1.2	Lower Level Power Demolition Plan
ED1.3B	Main Level Power Demolition Plan - Area B
ED1.4	Lower Level Lighting Demolition Plan
ED1.5B	Main Level Lighting Demolition Plan - Area B
E1.2	Lower Level Power Plan
E1.3B	Main Level Power Plan - Area B
E1.4	Lower Level Lighting Plan
E1.5B	Main Level Lighting Plan - Area B
E3.0	Electrical Panel Schedules
E5.0	Electrical Details

DAO ARCHITECTURE

7230 Meade St.
Westminster, CO 80030

Phone: 720.273.0431
Email: dan@daoarch.com
Web: www.daoarch.com

OWNER:
WESTMINSTER PUBLIC SCHOOLS
7002 RALEIGH STREET
WESTMINSTER, CO 80030
CONTACT: DON CIANCIO
PHONE #: 720.542.5100

ARCHITECT:
DAO ARCHITECTURE
7230 MEADE ST
WESTMINSTER, CO 80030
CONTACT: DAN ORECCHIO
PHONE #: 720.273.0431

MECHANICAL ENGINEERS:
THE BALLARD GROUP, INC.
2525 S WADSWORTH BLVD. SUITE 200
LAKEWOOD, CO 80227
CONTACT: ERIC BAALMAN
PHONE #: 303.988.4514

ELECTRICAL ENGINEERS:
CATOR RUMA & ASSOCIATES, CO.
896 TABOR STREET
LAKEWOOD, CO 80401
CONTACT: KEVIN MILLER
PHONE #: 303.232.6200

Westminster Public Schools

Hodgkins Leadership Academy Classroom Conversion Project

3475 W 67th Ave,
Denver, CO 80221

DAO No.: 2021-033

September 25, 2026

CONSTRUCTION DOCUMENTS

Cover

Autodesk Docs://WPS 2026 Bond Projects - Hodgkins Classroom Conversion/Hodgkins ES Classroom Conversion (Revit 2026).rvt
9/25/2026 9:14:05 AM

MATERIALS SYMBOLS

EARTHWORKS

EARTH NON-COMPACTED

EARTH COMPACT/FILL

GRAVEL/POROUS FILL

CONCRETE

CONCRETE

PRECAST CONCRETE

SAND/MORTAR/PLASTER

METAL

ALUMINUM

BRASS/BRONZE

STEEL

MASONRY

CONCRETE BLOCK

COMMON/FACE BLOCK

FIRE BRICK

STONE

BLUESTONE/SLATE/ SOAPSTONE/FLAGGING

LIMESTONE

RUBBLE

WOOD

FINISH

ROUGH

SHIM

PLYWOOD

GLASS

GLASS

STRUCTURAL

GLASS BLOCK

INSULATION

BATT/LOOSE FILL

RIGID

SPRAY/FOAM

FINISHES

ACOUSTICAL TILE

CARPET AND PAD

CERAMIC TILE

GYPSUM WALLBOARD

TECTUM

PARTITION INDICATIONS

CAST-IN-PLACE CONCRETE

CONCRETE MASONRY

METAL STUD

WOOD STUD

ELEVATION INDICATIONS

BRICK

CERAMIC/ PORCELAIN TILE

CONCRETE/ PLASTER/GPDW

CONCRETE MASONRY UNIT

SHEET METAL

SHINGLES/SIDING

REFERENCE SYMBOLS

1 / A1.0 — SIM — DETAIL OR SECTION NUMBER / SHEET ON WHICH IT IS FOUND

No. / Sht. — SECTION REFERENCE

No. / Sht. — DETAIL REFERENCE

No. / Sht. — WALL SECTION REFERENCE

No. / Sht. — No. / Sht. — BUILDING SECTION REFERENCE

Sht. — No. — ELEVATION REFERENCE

View Name — SCALE: — NO. / SHT. — VIEW TITLE

ROOM NAME 101 — ROOM IDENTIFIER

1t — WINDOW/OPENING IDENTIFIER

1A101 — DOOR/OPENING IDENTIFIER

1 — EXISTING GRID LINE

Level 100'-0" — ELEVATION REFERENCE

1i — WALL TYPE REFERENCE

MATCH LINE

DEMOLITION INDICATOR

1 — REVISION INDICATOR

GENERAL NOTES

1. THE GENERAL CONTRACTOR SHALL VERIFY ALL EXISTING DIMENSIONS AND CONDITIONS SHOWN ON PLANS PRIOR TO COMMENCEMENT OF THE WORK . IT SHALL BE THE CONTRACTORS RESPONSIBILITY TO COORDINATE INSTALLATION OF NEW WORK WITHIN THESE EXISTING CONDITIONS. ANY DEVIATIONS IN EXISTING CONDITIONS OR DIMENSIONS INDICATED SHALL BE COORDINATED WITH THE ARCHITECT AND OWNER IN ORDER TO MODIFY PLANS ACCORDINGLY.

2. ALL DISCIPLINES SHALL BE RESPONSIBLE FOR THEIR SCOPE OF WORK. THIS WORK IS TO BE SCHEDULED AND COMPLETED WITH THE GENERAL CONTRACTOR'S FULL KNOWLEDGE.

3. ALL HOT WORK ACTIVITIES (I.E. USING HEAT GUNS, SOLDERING, BRAZING, WELDING, GRINDING, METAL CUTTING, ETC.) OR OTHER ACTIVITIES INVOLVING FLAMES OR SPARKS SHALL BE PRECEDED BY OBTAINING AN APPROVED HOT WORK PERMIT. (IF HOT WORK REQUIRED)

4. THE PROJECT STAGING AREA / CONSTRUCTION ACTIVITIES SHALL NOT CAUSE THE OBSTRUCTION OF PATHS OF EGRESS INSIDE THE BUILDING, BLOCK EXIT DISCHARGE FROM THE BUILDING, OR IMPEDE EMERGENCY VEHICLE ACCESS TO THE BUILDING. CORRIDORS MAY NOT BE USED AS STAGING AREAS OR AS AREAS FOR DEBRIS COLLECTION.

5. ALL NECESSARY MEASURES SHALL BE TAKEN TO PREVENT THE NUISANCE ACTUATION OF ANY NEARBY SMOKE OR DUCT DETECTORS BY CONSTRUCTION ACTIVITIES THAT CREATE DUST OR FUMES INSIDE THE BUILDING.

6. THE CONTRACTOR SHALL NOT HANDLE OR DISABLE ANY FIRE SYSTEMS DEVICES. ONLY BUILDING FIRE SYSTEMS PERSONNEL MAY HANDLE OR DISABLE EXISTING FIRE SYSTEMS. ANY OUTAGES REQUIRED FOR THE EXISTING FIRE SYSTEMS SHALL BE PERFORMED ACCORDING TO THE BUILDING PROCEDURES.

7. THE ARCHITECT ASSUMES NO RESPONSIBILITY FOR THE DETECTION OR REMOVAL OF ANY HAZARDOUS MATERIALS, INCLUDING, BUT NOT LIMITED TO, ASBESTOS IN ANY FORM. PARTIES RESPONSIBLE FOR DEMOLITION SHALL NOTIFY THE OWNER IMMEDIATELY OF ANY SUSPECTED MATERIALS.

PROJECT DESCRIPTION

ARCHITECTURALLY, THIS PROJECT ENTAILS THE REMODEL OF FOUR EXISTING OPEN EDUCATIONAL AREAS (TWO ON EACH LEVEL) AT HODGKINS LEADERSHIP ACADEMY. THESE SPACES WILL BE ENCLOSED AND SEPARATED FROM THE CORRIDOR BY NEW METAL STUD FRAMED WALLS. THE CLASSROOMS WILL BE ACCESSED BY NEW WOOD DOORS WITH HOLLOW METAL FRAMES. THE CLASSROOMS WILL BE FINISHED, WITH NEW CARPET AND RUBBER BASE, CASEWORK, PAINT, AND LED LIGHTING. PORTIONS OF THE EXISTING LEARNING CENTER WILL RECEIVE NEW PAINT AND RUBBER BASE. CASEWORK WILL BE REMOVED, FLOORING REPLACED, AND TEACHING WALLS PROVIDED IN (3) EXISTING CLASSROOMS ON THE LOWER LEVEL. ADDITIONAL AREAS THROUGHOUT THE BUILDING WILL HAVE EXISTING VCT FLOORING REPLACED.

NO MODIFICATION TO THE EXISTING STRUCTURAL SYSTEM IS ANTICIPATED AS PART OF THIS PROJECT SCOPE.

MECHANICALLY, THE EXISTING HVAC UNITS WILL BE REUSED. NEW DUCTWORK WILL BE INSTALLED AS REQUIRED TO MODIFY THE RETURN AIR PATH TO ACCOMMODATE THE NEWLY ENCLOSED SPACES. EXISTING FIRE SPRINKLER WILL BE RECONFIGURED AS REQUIRED.

ELECTRICALLY, POWER WILL BE RECONFIGURED AS REQUIRED WITHIN THE NEW CLASSROOMS. THE EXISTING ELECTRICAL SERVICE AND DISTRIBUTION WILL BE MAINTAINED. FIRE ALARM DEVICES WILL BE RELOCATED AS NECESSARY TO ACCOMMODATE THE RECONFIGURED PLAN. POWER WILL BE PROVIDED AS REQUIRED TO SUPPORT NEW TEACHING WALLS.

LOW-VOLTAGE SYSTEMS, SUCH AS INTERCOM AND DATA, WILL BE RECONFIGURED AND AUGMENTED AS REQUIRED TO ACCOMMODATE THE RECONFIGURED PLAN. DATA WILL BE PROVIDED AS REQUIRED TO SUPPORT NEW TEACHING WALLS

STANDARD ABBREVIATIONS

A/E	ARCHITECT/ENGINEER	CONN	CONNECTION	GALV	GALVANIZED	MO	MASONRY OPENING
AB	ANCHOR BOLT	CONSTR	CONSTRUCTION	GB	GRAB BAR	MOD	MODULE
ABBR	ABBREVIATE	CONT	CONTINUOUS	GDRL	GUARD RAIL	MTD	MOUNTED
ABV	ABOVE	CONTR	CONTRACTOR	GENL	GENERAL	MTG	MEETING
AC	AIR CONDITIONING	COORD	COORDINATE	GENL CONTR	GENERAL CONTRACTOR	MTL	METAL
ACID RES	ACID RESISTANT	CORR	CORRIDOR	GFI	GROUND FAULT INTERRUPTER	MTR	MORTAR
ACOUS	ACOUSTICAL	COV PL	COVER PLATE	GL	GLASS	MULL	MULLION
ACOUS INSUL	ACOUSTICAL INSULATION	CPRS	COMPRESSIBLE	GL BLK	GLASS BLOCK	MULT	MULTIPLE
ACOUS PNL	ACOUSTICAL PANEL	CPT	CARPET	GLU LAM	GLUE LAMINATED	MVBL	MOVABLE
ACOUS PLAS	ACOUSTICAL PLASTER	CRCMF	CIRCUMFERENCE	GLZ	GLAZING	N	NORTH
ACOUS TILE	ACOUSTICAL TILE	CRS	COLD ROLLED STEEL	GLZ CMU	GLAZED CONCRETE MASONRY UNIT	N/A	NOT APPLICABLE
ACT	ACTUAL	CSG	CASING	GND	GROUND	NEG	NEGATIVE
AD	AREA DRAIN	CSK	COUNTERSUNK	GPDW	GYPSUM DRY WALL	NF	NEAR FACE
ADC	AUTOMATIC DOOR CLOSER	CSMT	CASEMENT	GR BM	GRADE BEAM	NIC	NOT IN CONTRACT
ADDL	ADDITIONAL	CSWK	CASEWORK	GR	GRADE	NO	NUMBER
ADDM	ADDENDUM	CT	CERAMIC TILE	GRTG	GRATING	NOM	NOMINAL
ADJ	ADJUSTABLE	C TV	CABLE TELEVISION	GUT	GUTTER	NS	NEAR SIDE
ADJC	ADJACENT	CUB	CUBICLE	GYP	GYPSUM	NTS	NOT TO SCALE
AF	ACCESS FLOOR	CUR	CURRENT	GYP PLAS	GYPSUM PLASTER	O/O	OUT TO OUT
AFF	ABOVE FINISHED FLOOR	CW	COLD WATER	H	HIGH	OA	OVERALL
AFG	ABOVE FINISHED GRADE	DBL GLZ	DOUBLE GLAZING	H&CW	HOT & COLD WATER	OC	ON CENTER
AFS	ABOVE FINISHED SLAB	DEPT	DEPARTMENT	HB	HOSE BIBB	OD	OUTSIDE DIAMETER
AGGR	AGGREGATE	DET	DETAIL	HC	HOLLOW CORE	OD	OVERFLOW DRAIN
AHR	ANCHOR	DF	DRINKING FOUNTAIN	HC	HANDICAP	OF	OUTSIDE FACE
AHU	AIR HANDLING UNIT	DF	DRAPERY FABRIC	HCMU	HOLLOW CONCRETE MASONRY UNIT	OFCI	OWNER FURNISHED CONTRACTOR INSTALL
ALD	ALUMINUM DOOR	DFR	DOOR FRAME	HD	HEAVY DUTY	OFF	OFFICE
ALM	ALARM	DH	DOUBLE HUNG	HDJT	HEAD JOINT	OFOI	OWNER FURNISHED OWNER INSTALLED
ALT	ALTERNATE	DIA	DIAMETER	HDBD	HARDBOARD	OH	OVERHEAD
ALUM	ALUMINUM	DIM	DIMENSION	HDR	HEADER	OHD	OVERHEAD DOOR
AMB	AMBIENT	DIST	DISTANCE	HDWD	HARDWOOD	OPER	OPERABLE
AMPL	AMPLIFIER	DIV	DIVIDER	HGT	HEIGHT	OPNG	OPENING
AMT	AMOUNT	DIW	DEIONIZED WATER	HLB	HORIZONTAL LOUVER BLINDS	OPP	OPPOSITE
ANN	ANNUNCIATOR	DJ	DOUBLE JOIST	HM	HOLLOW METAL	OPT	OPTIONAL
ANOD	ANODIZED	DL	DRAPERY LINER	HMD	HOLLOW METAL DOOR	ORIG	ORIGINAL
ANT	ANTENNA	DMPF	DAMPPROOFING	HMF	HOLLOW METAL FRAME	OVHD	OVERHEAD
AP	ACCESS PANEL	DN	DOWN	HNDRL	HAND RAIL	OXY	OXYGEN
APPX	APPENDIX	DO	DITTO	HO	HOLD-OPEN	OZ	OUNCE
ARCH	ARCHITECT(URAL)	DR	DOOR	HORIZ	HORIZONTAL	PC	PRECAST
ASB	ASBESTOS	DR CLSR	DOOR CLOSURE	HR	HOUR	PAR	PARALLEL
ASC	ABOVE SUSPENDED CEILING	DS	DOWNSPOUT	HS	HIGH STRENGTH	PARG	PARGING
ASPH	ASPHALT	DST	DOOR STOP	HSB	HIGH STRENGTH BOLT	PB	PANIC BAR
ASYM	ASYMMETRICAL	DT	DRAIN TILE	HTG	HEATING	PBD	PARTICLE BOARD
AV	AUDIO VISUAL	DUPL	DUPLICATE	HVAC	HEATING, VENTILATION, AIR CONDITIONING	PC	PORTLAND CEMENT
AVE	AVENUE	DVTL	DOVETAIL	HW	HOT WATER	PCPLAS	PORTLAND CEMENT PLASTER
AWC	ACOUSTICAL WALL COVERING	DW	DISHWASHER	HYD	HYDRANT	PED	PEDESTAL
AWP	ACOUSTICAL WALL PANEL	DWG	DRAWING	ID	INSIDE DIAMETER	PERF	PERFORATED
B&B	BALLED AND BURLAPPED	DWL	DOWEL	IF	INSIDE FACE	PERIM	PERIMETER
BAF	BAFFLE	DWR	DRAWER	INCAND	INCANDESCENT	PERM	PERMANENT
BAL	BALANCE	DWTR	DUMBWAITER	INL	INLET	PERP	PERPENDICULAR
BB	BULLETIN BOARD	E	EAST	INSTL	INSTALLATION	PF	PANEL FABRIC
BC	BOTTOM OF CURB	EA	EACH	INSUL	INSULATION	PFP	PRE-FINISHED PANELS
BD	BOARD	EF	EACH FACE	INTR	INTERIOR	PGBD	PEGBOARD
BEV	BEVEL	EJ	EXPANSION JOINT	INV	INVERT	PH	PHASE
BF	BOTH FACES	EL	ELEVATION	INV EL	INVERT ELEVATION	PL	PLASTIC LAMINATE
BFF	BELOW FINISH FLOOR	ELEC	ELECTRICAL	JAN	JANITOR	PLAM	PLASTIC LAMINATE
BFP	BACKFLOW PREVENTER	ELEV	ELEVATOR	JC	JANITOR'S CLOSET	PLAS	PLASTER
BITUM	BITUMINOUS	EMER	EMERGENCY	JST	JOIST	PLAT	PLATFORM
BJT	BED JOINT	EMER SHR	EMERGENCY SHOWER	JT	JOINT	PLBG	PLUMBING
BL	BASE LINE	ENAM	ENAMEL	KB	KNEE BRACE	PLYWD	PLYWOOD
BLDG	BUILDING	ENCL	ENCLOSURE	KO	KNOCKOUT	POL	POLISHED
BLK	BLOCK	ENGR	ENGINEER	KOP	KNOCKOUT PANEL	POLY	POLYSTYRENE
BLKG	BLOCKING	ENTR	ENTRANCE	KPL	KICK PLATE	POLYISO	POLYISOCYANURATE
BLKHD	BULKHEAD	EO	ELECTRICAL OUTLET	KWY	KEYWAY	POS	POSITIVE
BLST	BALLAST	EP	ELECTRICAL PANEL	L	LEFT	PR	PAIR
BM	BEAM	EPS	EXPANDED POLYSTYRENE	LAB	LABORATORY	PREFAB	PREFABRICATED
BO	BOTTOM OF	EPX	EPOXY FLOOR	LAT	LAY-IN ACOUSTICAL TILE	PRELIM	PRELIMINARY
BOC	BACK OF CURB	EQL SP	EQUALLY SPACED	LAV	LAVATORY	PRKG	PARKING
BOW	BOTTOM OF WALL	EQ	EQUAL	LB	POUND	PROJ	PROJECT
BP	BASE PLATE	EQUIP	EQUIPMENT	LBR	LUMBER	PS	PROJECTION SCREEN
BRCG	BRACING	EQUIV	EQUIVALENT	LCMU	LIGHTWEIGHT CONCRETE MASONRY UNIT	PT	PAINT
BRDG JST	BRIDGING JOIST	ERECT	ERECTION	LD BRG	LOAD BEARING	PT	PORCELAIN TILE
BRG	BEARING	ESCAL	ESCALATOR	LDG	LANDING	PTN	PARTITION
BRG PL	BEARING PLATE	ESMT	EASEMENT	LF	LINEAR FOOT	PVC	POLYVINYL CHLORIDE
BRK	BRICK	EST	ESTIMATE	LG	LENGTH	PVG	PAVING
BRKT	BRACKET	EW	EACH WAY	LH	LEFT HAND	PVMT	PAVEMENT
BRS	BRASS	EXC	EXCAVATE	LHR	LEFT HAND REVERSE	PWR	POWER
BRZ	BRONZE	EXG	EXISTING	LIN	LINOLEUM	QT	QUARRY TILE
BS	BOTH SIDES	EXH HD	EXHAUST HOOD	LIQ	LIQUID	QTY	QUANTITY
BSMT	BASEMENT	EXH FN	EXHAUST FAN	LKR	LOCKER	QUAL	QUALITY
BTM	BOTTOM	EXP	EXPANSION	LKR RM	LOCKER ROOM	R	RISER
BUR	BUILT-UP ROOF	EXSP	EXPOSED	LL	LIVE LOAD	RAD	RADIUS
BW	BOTH WAYS	EXST	EXISTING	LNTL	LINTEL	RB	RUBBER BASE
BOW	BOTTOM OF WALL	EXST GR	EXISTING GRADE	LOC	LOCATION	RBR	RUBBER
C/C	CENTER TO CENTER	EXT	EXTERIOR	LONG	LONGITUDINAL	RC	REINFORCED CONCRETE
C&G	CURB AND GUTTER	EXTN	EXTENSION	LRG	LARGE	RCP	REINFORCED CONCRETE PIPE
CAB	CABINET	EIFS	EXTERIOR INSULATION & FINISH SYSTEM	LS	LUMP SUM	RD	ROOF DRAIN
CARP	CARPET	F BRK	FIRE BRICK	LT	LIGHT	REC	RECESSED
CAV	CAVITY	F/F	FACE TO FACE	LT WT	LIGHTWEIGHT	RECD	RECEIVED
CB	CATCH BASIN	FBD	FIBERBOARD	LTG	LIGHTING	RECPT	RECEPTACLE
CCTV	CLOSED CIRCUIT TELEVISION	FC	FIRE COATED	LVL	LEVEL	RECT	RECTANGULAR
CEM	CEMENT	FD	FLOOR DRAIN	LVR	LOUVER	REF	REFERENCE
CEM PLAS	CEMENT PLASTER	FDN	FOUNDATION	LW PLAS	LIGHTWEIGHT PLASTER	REINF	REINFORCEMENT
CER	CERAMIC	FEC	FIRE EXTINGUISHER CABINET	LWC	LIGHTWEIGHT CONCRETE	REM	REMOVABLE
CER TILE	CERAMIC TILE	FF	FACTORY FINISH	M	METER	REQD	REQUIRED
C FLG	COUNTER FLASHING	FFE	FINISH FLOOR ELEVATION	MAINT	MAINTENANCE	RESIL	RESILIENT
CH BD	CHALKBOARD	FGL	FIBERGLASS	MARB	MARBLE	RFM	RECESSED FLOOR MAT
CG	CORNER GUARD	FIN GR	FINISH GRADE	MAS	MASONRY	RFG	ROOFING
CHAN	CHANNEL	FIN FL	FINISH FLOOR	MATL	MATERIAL	RH	RIGHT HAND
CHFR	CHAMFER	FIN	FINISH	MAX	MAXIMUM	RHR	RIGHT HAND REVERSE
CHK	CHECK	FL	FLOWLINE	MB	MARKERBOARD	RND	ROUND
CI	CAST IRON	FLDG	FOLDING	MBR	MEMBER	RO	ROUGH OPENING
CIP	CAST IN PLACE	FLG	FLANGE	MC	METAL CLAD	RST	RUBBER STAIR TREAD
CIR	CIRCLE	FLR	FLOOR	MDF	MEDIUM DENSITY FIBERBOARD	RT	RUBBER TILE
CJ	CONTROL JOINT	FLR SK	FLOOR SINK	MDO	MEDIUM DENSITY OVERLOAD	RV	ROOF VENT
CL	CENTER LINE	FLR PL	FLOOR PLATE	ME	MATCH EXISTING	RVS	REVERSE
CLG	CEILING	FLR FIN	FLOOR FINISH	ME	MISCELLANEOUS EQUIPMENT	S	SOUTH
CLG DIFF	CEILING DIFFUSER	FLT GL	FLOAT GLASS	MECH	MECHANICAL	S	SEATING
CLG HT	CEILING HEIGHT	FLOUR	FLUORESCENT	MED	MEDIUM	SALV	SALVAGE
CLL	CONTRACT LIMIT LINE	FOC	FACE OF CONCRETE	MEMB	MEMBRANE	SB	SPLASH BLOCK
CLOS	CLOSET	FOM	FACE OF MASONRY	MEZZ	MEZZANINE	SC	SOLID CORE
CLR	CLEAR	FOS	FACE OF STUD	MFG	MANUFACTURING	SCH	SCHEDULE
CLSR	CLOSURE	FPL	FIREPLACE	MFR	MANUFACTURER	SCMU	SOLID CONCRETE MASONRY UNIT
CMPST	COMPOSITE	FPRF	FIREPROOFING	MH	MANHOLE	SCRN	SCREEN
CMU	CONCRETE MASONRY UNIT	FRM	FRAME	MIL	MILLIMETER	SD	STORM DRAIN
CNR	CORNER	FRNT	FRONT	MIN	MINIMUM	SECT	SECTION
CNTR	COUNTER	FS	FULL SIZE	MIR	MIRROR	SF	SYSTEMS FURNITURE
CO	CLEANOUT	FSP	FIRE STANDPIPE	MISC	MISCELLANEOUS	SGL	SINGLE
COL	COLUMN	FSTNR	FASTENER	MK	MARK	SHR	SHOWER
COMM	COMMERCIAL	FTG	FOOTING	MKRBD	MARKERBOARD	SHTHG	SHEATHING
COMPL	COMPLETE	FURR	FURRING	ML	MATCH LINE	SHVL	SHELVES
CONC	CONCRETE	FUT	FUTURE	MLC	METAL LABORATORY CASEWORK	SIM	SIMILAR
CONC FL	CONCRETE FLOOR	FXTR	FIXTURE	MLDG	MOLDING	SJ	SLIP JOINT
CONF	CONFERENCE	GA	GYPSUM ASSOCIATION	MLWK	MILLWORK	SK	SINK
						SLA	SLATE
						SLP	SLOPE
						SLS	SUB-FLOOR LEVELING SYSTEM
						SLV	SLEEVE
						SM	SHEET METAL
						SMLS	SEAMLESS
						SP	SPACING
						SPCL	SPECIAL
						SPEC	SPECIFICATION
						SPKLR	SPRINKLER
						SPKR	SPEAKER
						SPRT	SUPPORT
						SQFT	SQUARE FOOT
						SQ	SQUARE
						SQIN	SQUARE INCH
						SQYD	SQUARE YARD
						SSK	SERVICE SINK
						SS	STAINLESS STEEL
						SSM	SOLID SURFACING MATERIAL
						ST	STAIN
						ST	STREET
						STAG	STAGGERED
						STC	SOUND TRANSMISSION CLASS
						STD	STANDARD
						STIR	STIRRUP
						STL JST	STEEL JOIST
						STL PL	STEEL PLATE
						STL	STEEL
						STN	STONE
						STOR	STORAGE
						STRUCT	STRUCTURAL
						STRUCT STL	STRUCTURAL STEEL
						SUPPL	SUPPLEMENT
						SURF	SURFACE
						SUSP	SUSPENDED
						SUSP CLG	SUSPENDED CEILING
						SVB	SHEET VINYL BASE
						SVF	SHEET VINYL FLOOR
						SYM	SYMBOL
						SYMM	SYMMETRICAL
						SYST	SYSTEM
						T&B	TOP & BOTTOM
						T&G	TONGUE & GROOVE
						T	TABLE
						TB	TACKBOARD
						TB-xx	TEST BORING-xx (E.G. TB-1)
						TC	TOP OF CURB
						TD	TRENCH DRAIN
						TE	TRANSITION EDGE
						TECH	TECHNICAL
						TEMP	TEMPORARY
						TER	TERRAZZO
						THK	THICK
						THRES	THRESHOLD
						THRU	THROUGH
						TKBD	TACKBOARD
						TLT	TOILET
						TMPD	TEMPERED
						TMPD GL	TEMPERED GLASS
						TNL	TUNNEL
						TO	TOP OF
						TOF	TOP OF FLANGE
						TOFF	TOP OF FINISH FLOOR
						TOJ	TOP OF JOIST
						TOL	TOLERANCE
						TOS	TOP OF STEEL
						TOT	TOTAL
						TOW	TOP OF WALL
						TRNBKL	TURNBUCKLE
						TS	TUBE STEEL
						TV	TELEVISION
						TYP	TYPICAL
						UF	UPHOLSTERY FABRIC
						UFD	UNDER FLOOR DUCT
						UG	UNDERGROUND
						UL	UNDERWRITERS LABORATORY
						ULT	ULTIMATE
						UNEX	UNEXCAVATED
						UNFIN	UNFINISHED
						UNO	UNLESS NOTED OTHERWISE
						UPS	UNINTERRUPTIBLE POWER SUPPLY
						UR	URINAL
						UTIL	UTILITY
						V	VOLT
						VAC	VACUUM
						VAV	VARIABLE AIR VOLUME
						VB	VAPOR BARRIER
						VB	VINYL BASE
						VCT	VINYL COMPOSITION TILE
						VDB	VISUAL DISPLAY BOARD
						VERT	VERTICAL
						VEST	VESTIBULE
						VIB	VIBRATION
						VNR	VENEER
						VOL	VOLUME
						VR	VAPOR RETARDER
						VT	VINYL TILE
						VWC	VINYL WALL COVERING
						W	WITH
						W/W	WALL TO WALL
						W/O	WITHOUT
						W	WEST
						WC	WATER CLOSET
						WC	WALL COVERING
						WCPT	WALL CARPET
						WD	WOOD
						WDD	WOOD DOOR
						WDW	WINDOW
						WF	WOOD FLOORING
						WF	WIDE FLANGE
						WGL	WIRE GLASS
						WH	WALL HUNG
						WHSE	WAREHOUSE
						WL	WIND LOAD
						WLD	WELDED
						WR	WATER RESISTANT
						WS	WEATHERSTRIPPING
						WSCT	WAINSCOT
						WT	WEIGHT
						WTR	WATER
						WTRPRF	WATERPROOFING
						WWM	WELDED WIRE MESH
						X SECT	CROSS SECTION

VICINITY MAP

N.T.S.



DAO ARCHITECTURE

7230 Meade St.
Westminster, CO 80030

Phone: 720.273.0431
Email: dan@daoarch.com
Web: www.daoarch.com

Westminster Public Schools

Hodgkins Leadership Academy Classroom Conversion Project

3475 W 67th Ave,
Denver, CO 80221

DAO No.:2021-033

September 25, 2026

Standard Symbols, Abbreviations & General Notes

G0.0

Autodesk Docs://WPS 2026 Bond Projects - Hodgkins Classroom Conversion/Hodgkins ES Classroom Conversion (Revit 2026)_rvt
9/25/2026 9:14:06 AM

CODE REVIEW

This project entails a classroom remodel at Hodgkins Leadership Academy in Denver, CO.
This building is an E Occupancy and will remain an E Occupancy.

In general, the scope of the renovation project will consist of remodeling four existing open educational areas (two on each level) into enclosed classroom spaces. Casework will be removed, and existing VCT flooring will be replaced throughout the building.

Any alterations shall comply with the requirements of the International Building Code, and the existing building shall be no less conforming to the provisions of the IBC than the existing building was prior to the alteration.

2021 IEBC
The project is considered an Alteration per prescriptive section 503 of the 2021 IEBC. As such, any alterations shall comply with the requirements for the 2021 International Building Code, and the existing building shall be no less conforming to the provisions of the IBC than the existing building was prior to the alteration. This project's work area is less than 50% of the building area (1,533 / 78,843 square feet = 12.5% of the building).

Chapter 3 - Provisions for All Compliance Methods
301 - Administration
301.3 - Alteration, addition, or change of occupancy - The alteration of this existing building shall comply with section 301.3.1.
301.3.1 - Prescriptive compliance method - Alterations complying with Chapter 5 of this code in buildings complying with the International Fire Code shall be considered in compliance with the provisions of this code
302 - General Provisions
302.3 - Existing Materials - Materials already in use in a building in compliance with requirements or approvals in effect at the time of their erection or installation shall be permitted to remain in use unless determined by the code official to be unsafe.
302.4 - New and replacement materials - Except as otherwise required or permitted by this code, materials permitted by the applicable code shall be used. Like materials shall be permitted for repairs or alterations, provided that unsafe conditions are not created. Hazardous materials shall not be used where the code for new construction would not permit their use in buildings of similar occupancy, purpose, and location.
Section 306 - Accessibility for Existing Buildings
306.7 - Alterations - A facility that is altered shall comply with the applicable provisions in Chapter 11 of the International Building Code, ICC A117.1, and the provisions of sections 306.7.1 through 306.7.16, unless technically infeasible. Where compliance with this section is technically infeasible, the alteration shall provide access to the maximum extent technically feasible.
306.7.1 Alterations affecting an area containing a primary function - Where an alteration affects the accessibility to, or contains an area of primary function, the route to the primary function shall be accessible. The accessible route to the primary function shall include toilet facilities and drinking fountains serving the area of primary function.
Exceptions: 1. The costs of providing the accessible route are not required to exceed 20 percent of the costs of the alterations a affecting the area of primary function.
306.7.2 - Accessible means of egress - Accessible means of egress required by Chapter 10 of the International Building Code are not required to be added in existing facilities.

Chapter 5 - Prescriptive Compliance Method
Section 503 - Alterations
503.1 - General - Alterations to any building or structure shall comply with the requirements of the International Building Code for new construction. Alterations shall be such that the existing building or structure is not less complying with the provisions of the International Building Code than the existing building or structure was prior to the alteration.
503.3 & 503.4 - We are not altering the existing structural gravity or lateral systems in such a way as to trigger compliance with sections 503.3 or 503.4.

2021 IBC
Chapter 3 - Use and Occupancy Classification
305 - Educational Group E
305.1 - Educational Group E occupancy includes, among others, the use of a building or structure, or a portion thereof, by six or more persons at any one time for educational purposes through the 12th grade.

Chapter 4 - Special Detailed Requirements Based on Use and Occupancy
Not applicable to new work.

Chapter 5 - General Building Heights and Areas
Building height and area are existing and are not being modified by this project.

Chapter 6 - Types of Construction
602 - Construction Classification
Type IIB (Assumed) - Primary Structural Frame - 0 hours
Bearing Walls - Interior/Exterior - 0 hours
Nonbearing walls and partitions - Exterior - (E Occupancy, Type IIB) - 0 hour
Nonbearing walls and partitions - Interior - 0 hours
Floor construction and secondary members - 0 hours
Roof construction and secondary members - 0 hours

Chapter 7 - Fire and Smoke Protection Features
The existing building is fully sprinklered, no fire and/or smoke protected features are required for this project.

Chapter 8 - Interior Finishes
803 - Wall and Ceiling Finishes
803.1 General - Interior wall and ceiling finish materials shall be classified for fire performance and smoke development in accordance with Section 803.1.1 or 803.1.2.
803.13 - Interior finish requirements based on occupancy. - Per Table 803.13
E (sprinklered) - Exit enclosures and exit passageways - Class B
Corridors - Class C
Rooms and Enclosed Spaces - Class C
804 - Interior Floor Finish
804.4.2 - In all occupancies, interior floor finish and floor covering materials in enclosures for stairways and ramps, exit passageways, corridors and rooms or spaces not separated from corridors by partitions extending from the floor to the underside of the ceiling shall withstand a minimum critical radiant flux. The minimum critical radiant flux shall be not less than Class I in Groups I-1, I-2 and I-3 and not less than Class II in Groups A, B, E, H, I-4, M, R-1, R-2 and S.
EXCEPTION: Where a building is equipped throughout with an automatic sprinkler system in accordance with Section 903.3.1.1 or 903.3.1.2, Class II materials are permitted in any area where Class I materials are required, and materials complying with DOC FF-1 "pill test" (CPSC 16 CFR Part 1630) or with ASTM D2859 are permitted in any area where Class II materials are required.
808 - Acoustical Ceiling Systems
808.1 Acoustical Ceiling Systems - The quality, design, fabrication and erection of metal suspension systems for acoustical tile and lay-in panel ceilings in buildings or structures shall conform to generally accepted engineering practice, the provisions of this chapter and other applicable requirements of this code.

Chapter 9 - Fire Protection Systems
903 - Automatic Sprinkler System - The building is equipped throughout with an existing sprinkler system.
906 - Portable Fire Extinguishers
906.1 Where required - Portable fire extinguishers shall be installed in E Occupancies. *Existing fire extinguisher locations are not being modified by this project.*
906.3 Size and Distribution - The size and distribution of portable fire extinguishers shall be in accordance with Sections 906.3.1 through 906.3.4.
Table 906.3 - Light (Low) Hazard Occupancy
Minimum-rated single extinguisher - 2-A
Maximum floor area per unit of A - 3,000 square feet
Maximum floor area for extinguisher - 11,250 square feet
Maximum distance of travel to extinguisher - 75 feet
907 - Fire Alarm and Detection Systems - The building is equipped throughout with an existing Fire Alarm system.
REFERENCE: 2021 IFC Chapter 11 Construction Requirements for Existing Buildings
1103.7 Fire Alarm Systems - An approved fire alarm system shall be installed in existing buildings and structures in accordance with Sections 1103.7.1 through 1103.7.6 and provide occupant notification in accordance with Section 907.5 unless other requirements are provided by other sections of this code.
Exception: Occupancies with an existing, previously approved fire alarm system.

Chapter 10 - Means of Egress
1001 - Administration
1001.2 Minimum requirements - It shall be unlawful to alter a building or structure in a manner that will reduce the number of exits or the minimum width or required capacity of the means of egress to less that required by code.
1003 - General Means of Egress
1003.2 Ceiling Height - The means of egress shall have a ceiling height of not less than 7 feet 6 inches above the finished floor.
1004 - Occupant Load
1004.1 Design Occupant Load - See *Occupant Load Table*
1005 - Means of Egress Sizing
1005.3.2 Other Egress Components - The capacity, in inches, of means of egress components other than stairways shall be calculated by multiplying the occupant load served by such component by a means of egress capacity factor of 0.2 inch per occupant.
EXCEPTION 1: For other than Group H and I-2 occupancies, the capacity, in inches, of means of egress components other than stairways shall be calculated by multiplying the occupant load served by such component by a means of egress capacity factor of .15 inch (3.8 mm) per occupant in buildings equipped throughout with an automatic sprinkler system installed in accordance with Section 903.3.1.1 or 903.3.1.2 and an emergency voice/alarm communication system in accordance with Section 907.5.2.2.
1005.7.1 Doors - Doors, when fully opened, shall not reduce the required width by more than 7 inches. Doors in any position shall not reduce the required width by more than one-half.
1006 - Number of Exits and Exit Access Doorways
1006.2 Egress from Spaces - Rooms, areas or spaces, including mezzanines, within a story or basement shall be provided with the number of exits or access to exits in accordance with this section.
1006.2.1 Egress Based on Occupant Load and Common Path of Egress Travel Distance - Two exits or exit access doorways from any space shall be provided where the design occupant load or the common path of egress travel distance exceeds the values listed in Table 1006.2.1. The cumulative occupant load from adjacent rooms, areas or spaces shall be determined in accordance with Section 1004.2.
E Occupancy - Greater than 49 occupants, or more than 75' CPET distance.
The newly separated classrooms do not exceed these requirements, and as such, have a single means of egress.
1009 - Accessible Means of Egress
1009.1 Accessible Means of Egress Required - Accessible means of egress shall comply with this section. Accessible spaces shall be provided with not less than one accessible means of egress. Where more than one means of egress is required by Section 1006.2 or 1006.3 from any accessible space, each accessible portion of the space shall be served by not less than two accessible means of egress.
1010 - Doors, Gates, and Turnstiles
1010.1.1 Size of Doors - The required capacity of each door opening shall be sufficient for the occupant load thereof and shall provide a minimum clear opening width of 32 inches.
1010.1.2 Door Swing - Egress doors shall be of the pivoted or side-hinged swinging type.
1010.1.2.1 Direction of Swing - Pivot or side-hinged swinging doors shall swing in the direction of egress travel where serving a room or area containing an occupant load of 50 or more persons.
1010.2.8 Locking arrangements in educational occupancies - In group E occupancies, Group B educational occupancies and Group I-4 occupancies, egress doors from classrooms, offices and other occupied rooms with locking arrangements designed to keep intruders from entering the room shall comply with all of the following conditions:
1. The door shall be capable of being unlocked from outside the room with a key or other approved means.
2. The door shall be operable from within the room in accordance with Section 1010.2.
3. Modifications shall not be made to listed panic hardware, fire door hardware or door closers.
4. Modifications to fire door assemblies shall be in accordance with NFPA.
Remote locking or unlocking of doors from an approved location shall be permitted in addition to the unlocking operation in Item 1.
1013 - Exit Signs
1013.1 Where Required - Exits and exit access doors shall be marked by an approved exit sign readily visible from any direction of egress travel. The path of egress travel to exits and within exits shall be marked by readily visible exit signs to clearly indicate the direction of egress travel in cases where the exit or the path of egress travel is not immediately visible to the occupants.
EXCEPTION 1: Exit signs are not required in rooms or areas that require only one exit or exit access.
1017 - Exit Access Travel Distance
1017.2 Limitations - Exit access travel distance shall not exceed the values given in Table 1017.2.
TABLE 1017.2 - E Occupancy (sprinklered) - 250'
1020 - Corridors
1020.1 Construction - Corridors shall be fire-resistance rated in accordance with Table 1020.1 The corridor walls required to be fire-resistance rated shall comply with Section 708 for fire partitions.
TABLE 1020.1 - E occupancy, greater than 30 occupants served by corridor, sprinklered - 0 hours.

Chapter 11 - Accessibility
1103 - Scoping Requirements
1103.1 Where Required - Sites, buildings, structures, facilities, elements and spaces, temporary or permanent, shall be accessible to individuals with disabilities.
1104 - Accessible Route
1104.3 Connected Spaces - Where a building or portion of a building is required to be accessible, at least one accessible route shall be provided to each portion of the building, to accessible building entrances connecting accessible pedestrian walkways and to the public way.

Chapter 13 - Energy Efficiency
No exterior work is being performed. The envelope will be made no less conforming than it was prior to the project.

Chapter 29 - Plumbing Systems
The existing plumbing fixture count has not been altered as a result of this project, and the occupant load has not been increased from existing conditions, as such, the fixture count remains the same.

Colorado Model Electric Ready and Solar Ready Code
CMERSRC is not applicable to the scope of this project as it is not a major renovation, addition, or first tenant finish to the building.

APPLICABLE BUILDING CODES

All new work shall comply with the requirements of the codes and standards adopted by the State of Colorado.
The primary Applicable Codes and Standards are:

The 2021 International Code Series:
The 2021 International Existing Building Code (IEBC)
The 2021 International Building Code (IBC)
The 2021 International Fire Code (IFC)
The 2021 International Mechanical Code (IMC)
The 2021 International Energy Conservation Code (IECC)
The 2023 National Electrical Code
The 2021 Colorado Fuel Gas Code
The 2024 Colorado Plumbing Code
The 2017 ICC A117.1, Accessible and Usable Buildings and Facilities
The 2023 Colorado Model Electric Ready and Solar Ready Code

EGRESS TRAVEL DISTANCES	
PATH NAME	DISTANCE
1A	244' - 0"
1B	181' - 0"
1C	157' - 0"
1D	150' - 0"

NOTE: With the number of exits on each level, the max travel distance will never exceed 250 feet in any instance.

LIFE SAFETY SYMBOLS

FEC — FIRE EXTINGUISHER CABINET (EXISTING)
XX — PATH OF TRAVEL (FOR CUMULATIVE DISTANCES REFER TO SCHEDULE)
EXIT DISCHARGE
P: XX' / R: XX' — WIDTH PROVIDED / WIDTH REQUIRED
PORTION OF EXISTING BUILDING NOT INCLUDED WITH THIS PROJECT
PORTION OF EXISTING BUILDING WHERE SCOPE IS LIMITED TO FLOOR REPLACEMENT
EXISTING 1-HOUR FIRE WALL
EXISTING SMOKE BARRIER

Occupant Load Table


Number	Name	Area	Area Function	SF Per Occupant	Occupant Load	Required Exiting Width
LOWER LEVEL						
B002	Storage Room	235 SF	IBC_Accessory storage areas, mechanical equipment room	300 SF	0.78	0.2
B002A	Elec. Room	92 SF	IBC_Accessory storage areas, mechanical equipment room	300 SF	0.31	0.1
B004	Elevator Room	61 SF	IBC_Accessory storage areas, mechanical equipment room	300 SF	0.20	0
B005	Work Room Office	222 SF	IBC_Business areas	100 SF	2.22	0.4
B006	Conf. Room	213 SF	IBC_Business areas	100 SF	2.13	0.4
B007	Computer Classroom	725 SF	IBC_Educational:Shops and other vocational rooms	50 SF	14.50	2.9
B009	Learning Center	2372 SF	IBC_Library: Reading rooms	50 SF	47.43	9.5
B010	Building Resource	723 SF	IBC_H-5 Fabrication and manufacturing areas	200 SF	3.62	0.7
B011	Comm. Closet	241 SF	IBC_Accessory storage areas, mechanical equipment room	300 SF	0.80	0.2
B011B	IDF	102 SF	IBC_Accessory storage areas, mechanical equipment room	300 SF	0.34	0.1
B012A	Closet	28 SF	(none)		0.00	0
B012B	Closet	28 SF	(none)		0.00	0
B012C	Closet	28 SF	(none)		0.00	0
B013	Classroom	850 SF	IBC_Educational: Classroom area	20 SF	42.51	8.5
B014	Classroom	843 SF	IBC_Educational: Classroom area	20 SF	42.15	8.4
B015	Classroom	837 SF	IBC_Educational: Classroom area	20 SF	41.83	8.4
B016	Cust.	61 SF	IBC_Accessory storage areas, mechanical equipment room	300 SF	0.20	0
B017	Boy's	181 SF	(none)		0.00	0
B018	Girl's	192 SF	(none)		0.00	0
B019	Staff RR	56 SF	(none)		0.00	0
** B020	Classroom	679 SF	IBC_Educational: Classroom area	20 SF	33.97	6.8
B021	Classroom	830 SF	IBC_Educational: Classroom area	20 SF	41.50	8.3
B022	Classroom	821 SF	IBC_Educational: Classroom area	20 SF	41.05	8.2
B023A	Closet	28 SF	(none)		0.00	0
B023B	Closet	28 SF	(none)		0.00	0
B024	Classroom	818 SF	IBC_Educational: Classroom area	20 SF	40.89	8.2
B025	Classroom	838 SF	IBC_Educational: Classroom area	20 SF	41.89	8.4
B026	Small Group	158 SF	IBC_Educational: Classroom area	20 SF	7.91	1.6
B028	Small Group	156 SF	IBC_Educational: Classroom area	20 SF	7.79	1.6
B029	Classroom	837 SF	IBC_Educational: Classroom area	20 SF	41.85	8.4
** B030	Classroom	675 SF	IBC_Educational: Classroom area	20 SF	33.75	6.8
B031	Classroom	817 SF	IBC_Educational: Classroom area	20 SF	40.87	8.2
B032A	Closet	28 SF	(none)		0.00	0
B032B	Closet	28 SF	(none)		0.00	0
B032C	Closet	25 SF	(none)		0.00	0
B032D	Closet	39 SF	(none)		0.00	0
B033	Classroom	822 SF	IBC_Educational: Classroom area	20 SF	41.08	8.2
B034	Classroom	836 SF	IBC_Educational: Classroom area	20 SF	41.80	8.4
B036	Girl's	194 SF	(none)		0.00	0
B037	Boy's	184 SF	(none)		0.00	0
B038	Custodial	59 SF	IBC_Accessory storage areas, mechanical equipment room	300 SF	0.20	0
B039	Classroom	832 SF	IBC_Educational: Classroom area	20 SF	41.58	8.3
B040	E.L.L.	846 SF	IBC_Educational: Classroom area	20 SF	42.31	8.5
B041	Classroom	850 SF	IBC_Educational: Classroom area	20 SF	42.51	8.5
B253	Staff Restroom	57 SF	(none)		0.00	0
S001	Stair	245 SF	(none)		0.00	0
S003	Stair	245 SF	(none)		0.00	0
S004	Stair	438 SF	(none)		0.00	0
LOWER LEVEL: 48		20505 SF			739.98	148
MAIN LEVEL						
A102A	Closet	26 SF	(none)		0.00	0
A103	Gymnasium	4506 SF	IBC_Assembly: without fixed seats - Concentrated (chairs only - not fixed)	7 SF	643.73	128.7
A103A	Gym Storage	179 SF	IBC_Accessory storage areas, mechanical equipment room	300 SF	0.60	0.1
A103B	P.E. Office	120 SF	IBC_Business areas	100 SF	1.20	0.2
A104	Classroom	949 SF	IBC_Educational: Classroom area	20 SF	47.46	9.5
A104A	Kiln	56 SF	(none)		0.00	0
A104B	Storage	57 SF	IBC_Accessory storage areas, mechanical equipment room	300 SF	0.19	0
A105	Classroom	1004 SF	IBC_Educational: Classroom area	20 SF	50.20	10
A105A	Storage	146 SF	IBC_Accessory storage areas, mechanical equipment room	300 SF	0.49	0.1
A106	Laundry	51 SF	IBC_Accessory storage areas, mechanical equipment room	300 SF	0.17	0
A107	Janitor	40 SF	IBC_Accessory storage areas, mechanical equipment room	300 SF	0.13	0
A108	Custodial	49 SF	IBC_Accessory storage areas, mechanical equipment room	300 SF	0.16	0
A109	Mechanical	824 SF	IBC_Accessory storage areas, mechanical equipment room	300 SF	2.75	0.5
A109A	Electrical	160 SF	IBC_Accessory storage areas, mechanical equipment room	300 SF	0.53	0.1
A109B	MDF	140 SF	IBC_Accessory storage areas, mechanical equipment room	300 SF	0.47	0.1
A110	School Care	68 SF	IBC_Business areas	100 SF	0.68	0.1
A111	Kitchen	450 SF	IBC_Kitchens, commercial	200 SF	2.25	0.4
A111C	Toilet	57 SF	(none)		0.00	0
A111D	Dry Storage	138 SF	IBC_Accessory storage areas, mechanical equipment room	300 SF	0.46	0.1
A112	Multi-Purpose	2354 SF	IBC_Assembly: without fixed seats - Concentrated (chairs only - not fixed)	7 SF	336.34	67.3
A112A	Multi-Purpose Storage	363 SF	IBC_Accessory storage areas, mechanical equipment room	300 SF	1.21	0.2
A114	Girl's	253 SF	(none)		0.00	0
A115	Boy's	242 SF	(none)		0.00	0

Occupant Load Table


Number	Name	Area	Area Function	SF Per Occupant	Occupant Load	Required Exiting Width
B000	IDF/Storage	144 SF	IBC_Accessory storage areas, mechanical equipment room	300 SF	0.48	0.1
B001	Mechanical	43 SF	IBC_Accessory storage areas, mechanical equipment room	300 SF	0.14	0
B101	Main Office	499 SF	IBC_Business areas	100 SF	4.99	1
B102	Nurse	275 SF	IBC_Business areas	100 SF	2.75	0.6
B102A	Toilet	63 SF	(none)		0.00	0
B102B	Storage	49 SF	IBC_Accessory storage areas, mechanical equipment room	300 SF	0.16	0
B104	Work Room	270 SF	IBC_Business areas	100 SF	2.70	0.5
B105	In-School Suspension	96 SF	IBC_Assembly: without fixed seats - Unconcentrated (tables and chairs)	15 SF	6.40	1.3
B106	Assist. Principal	234 SF	IBC_Business areas	100 SF	2.34	0.5
B107	Assist. Principal	248 SF	IBC_Business areas	100 SF	2.48	0.5
B108	Record Room	79 SF	IBC_Accessory storage areas, mechanical equipment room	300 SF	0.26	0.1
B109	Staff Lounge	517 SF	IBC_Assembly: without fixed seats - Unconcentrated (tables and chairs)	15 SF	34.47	6.9
B111B	Closet	28 SF	(none)		0.00	0
B112	Electrical	61 SF	IBC_Accessory storage areas, mechanical equipment room	300 SF	0.20	0
B115	Toilet	50 SF	(none)		0.00	0
B116	Social Worker	120 SF	IBC_Business areas	100 SF	1.20	0.2
B117	Toilet	50 SF	(none)		0.00	0
B118	Speech Language	88 SF	IBC_Business areas	100 SF	0.88	0.2
B119	Special Ed	912 SF	IBC_Educational: Classroom area	20 SF	45.62	9.1
B119A	Toilet	78 SF	(none)		0.00	0
B119B	Special Ed. Office	211 SF	IBC_Business areas	100 SF	2.11	0.4
B123	Classroom	1169 SF	IBC_Educational: Classroom area	20 SF	58.45	11.7
B123A	Storage	62 SF	IBC_Accessory storage areas, mechanical equipment room	300 SF	0.21	0
B123B	Toilet	54 SF	(none)		0.00	0
B124	Classroom	1151 SF	IBC_Educational: Classroom area	20 SF	57.57	11.5
B124A	Toilet	54 SF	(none)		0.00	0
B124B	Storage	55 SF	IBC_Accessory storage areas, mechanical equipment room	300 SF	0.18	0
B125	Storage	166 SF	IBC_Accessory storage areas, mechanical equipment room	300 SF	0.55	0.1
B126	Classroom	1179 SF	IBC_Educational: Classroom area	20 SF	58.93	11.8
B126A	Toilet	54 SF	(none)		0.00	0
B126B	Storage	60 SF	IBC_Accessory storage areas, mechanical equipment room	300 SF	0.20	0
B128B	Closet	26 SF	(none)		0.00	0
B128C	Closet	25 SF	(none)		0.00	0
B128D	Closet	26 SF	(none)		0.00	0
B130	Classroom	979 SF	IBC_Educational: Classroom area	20 SF	48.94	9.8
B130A	Storage	62 SF	IBC_Accessory storage areas, mechanical equipment room	300 SF	0.21	0
B130B	Toilet	54 SF	(none)		0.00	0
B131	Classroom	852 SF	IBC_Educational: Classroom area	20 SF	42.62	8.5
B132	Classroom	975 SF	IBC_Educational: Classroom area	20 SF	48.73	9.7
B132A	Toilet	54 SF	(none)		0.00	0
B132B	Storage	63 SF	IBC_Accessory storage areas, mechanical equipment room	300 SF	0.21	0
B133	Custodial	92 SF	IBC_Accessory storage areas, mechanical equipment room	300 SF	0.31	0.1
B134	Staff Restroom	51 SF	(none)		0.00	0
* B135	Classroom	675 SF	IBC_Educational: Classroom area	20 SF	33.74	6.7
B136	Small Group	171 SF	IBC_Educational: Classroom area	20 SF	8.55	1.7
B137	Classroom	1386 SF	IBC_Educational: Classroom area	20 SF	69.28	13.9
B137A	Toilet	54 SF	(none)		0.00	0
B137B	Storage	88 SF	IBC_Accessory storage areas, mechanical equipment room	300 SF	0.29	0.1
B138	Washing	166 SF	IBC_Accessory storage areas, mechanical equipment room	300 SF	0.55	0.1
B138A	Closet	27 SF	(none)		0.00	0
B138B	Closet	27 SF	(none)		0.00	0
B140	Classroom	837 SF	IBC_Educational: Classroom area	20 SF	41.87	8.4
B141	Title Office	295 SF	IBC_Business areas	100 SF	2.95	0.6
B142	Refrigerator	103 SF	IBC_Accessory storage areas, mechanical equipment room	300 SF	0.34	0.1
B143	Small Group	280 SF	IBC_Educational: Classroom area	20 SF	13.98	2.8
B144	Classroom	840 SF	IBC_Educational: Classroom area	20 SF	42.02	8.4
* B145	Classroom	675 SF	IBC_Educational: Classroom area	20 SF	33.75	6.8
B146	Classroom	849 SF	IBC_Educational: Classroom area	20 SF	42.43	8.5
B147A	Closet	27 SF	(none)		0.00	0
B147B	Closet	25 SF	(none)		0.00	0
B147C	Closet	25 SF	(none)		0.00	0
B148	Classroom	826 SF	IBC_Educational: Classroom area	20 SF	41.30	8.3
B149	Classroom	841 SF	IBC_Educational: Classroom area	20 SF	42.03	8.4
B150	Custodial	63 SF	IBC_Accessory storage areas, mechanical equipment room	300 SF	0.21	0
B151	Girl's	195 SF	(none)		0.00	0
B152	Boy's	184 SF	(none)		0.00	0
B153	Storage	60 SF	IBC_Accessory storage areas, mechanical equipment room	300 SF	0.20	0
B154	Classroom	846 SF	IBC_Educational: Classroom area	20 SF	42.29	8.5
B155	E.L.L.	848 SF	IBC_Educational: Classroom area	20 SF	42.39	8.5
B156	Classroom	856 SF	IBC_Educational: Classroom area	20 SF	42.80	8.6
B157	Storage	70 SF	IBC_Accessory storage areas, mechanical equipment room	300 SF	0.23	0
B179	Closet	13 SF	(none)		0.00	0
B209	Classroom	817 SF	IBC_Educational: Classroom area	20 SF	40.87	8.2
MAIN LEVEL: 99		35781 SF			2055.42	411.1
Mezzanine						
A200	Mezzanine	494 SF	IBC_Accessory storage areas, mechanical equipment room	300 SF	1.65	0.3
Mezzanine: 1		494 SF			1.65	0.3
Grand total: 148		56780 SF			2797.05	559.4

** = Spaces affected by this project. These spaces were previously considered classroom spaces, and will remain classroom spaces once separated from the corridor.

Mezzanine Life Safety Plan
SCALE: 1" = 20'-0"

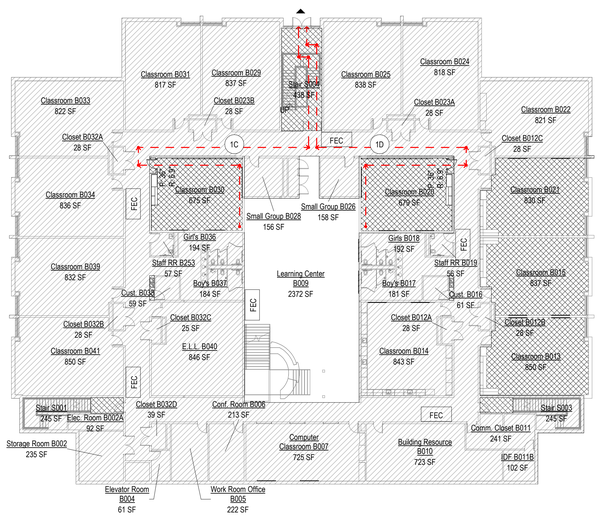

Lower Level Code Plan
SCALE: 1" = 20'-0"

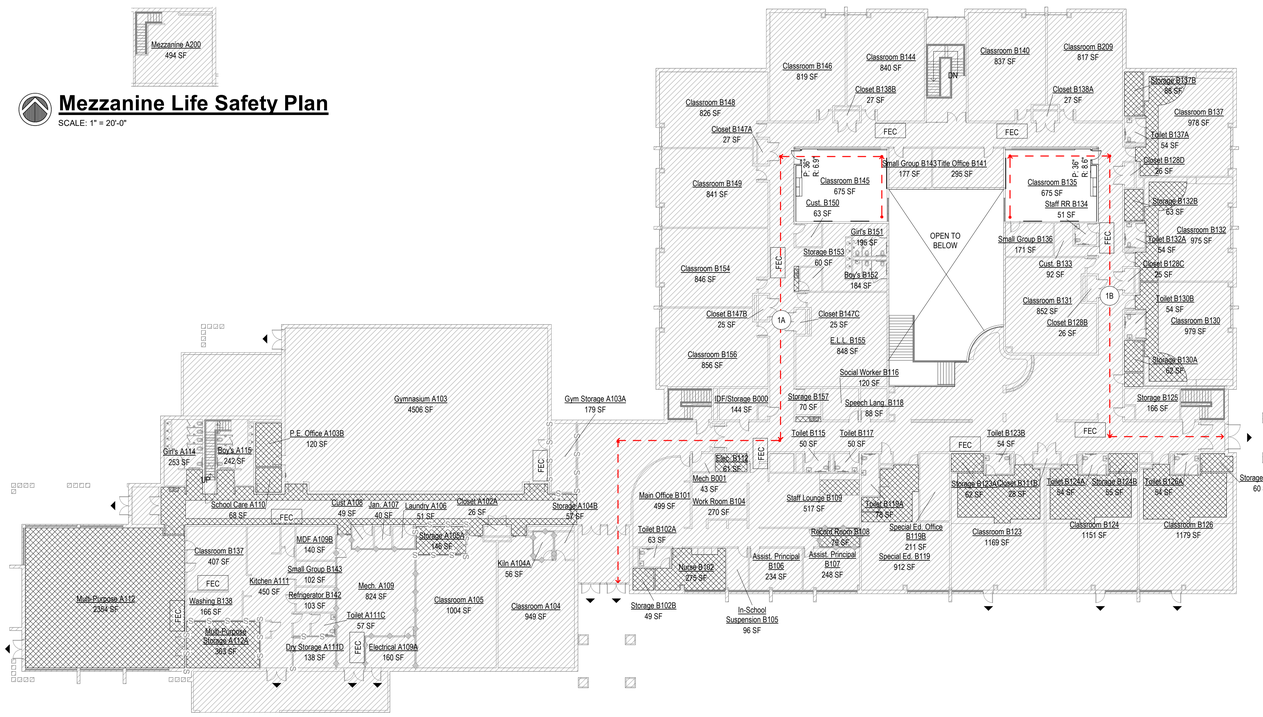

Main Level Life Safety Plan
SCALE: 1" = 20'-0"

DAO ARCHITECTURE
7230 Meade St.
Westminster, CO 80030
Phone: 720.273.0431
Email: dan@daoarch.com
Web: www.daoarch.com

Westminster Public Schools

Hodgkins Leadership Academy Classroom Conversion Project

3475 W 67th Ave,
Denver, CO 80221


DAO No.:2021-033

September 25, 2026

Building Code Data

G0.1

Autodesk Docs://WPS 2026 Bond Projects - Hodgkins Classroom Conversion/Hodgkins ES Classroom Conversion (Revit 2026)_rvt
9/25/2026 9:14:09 AM

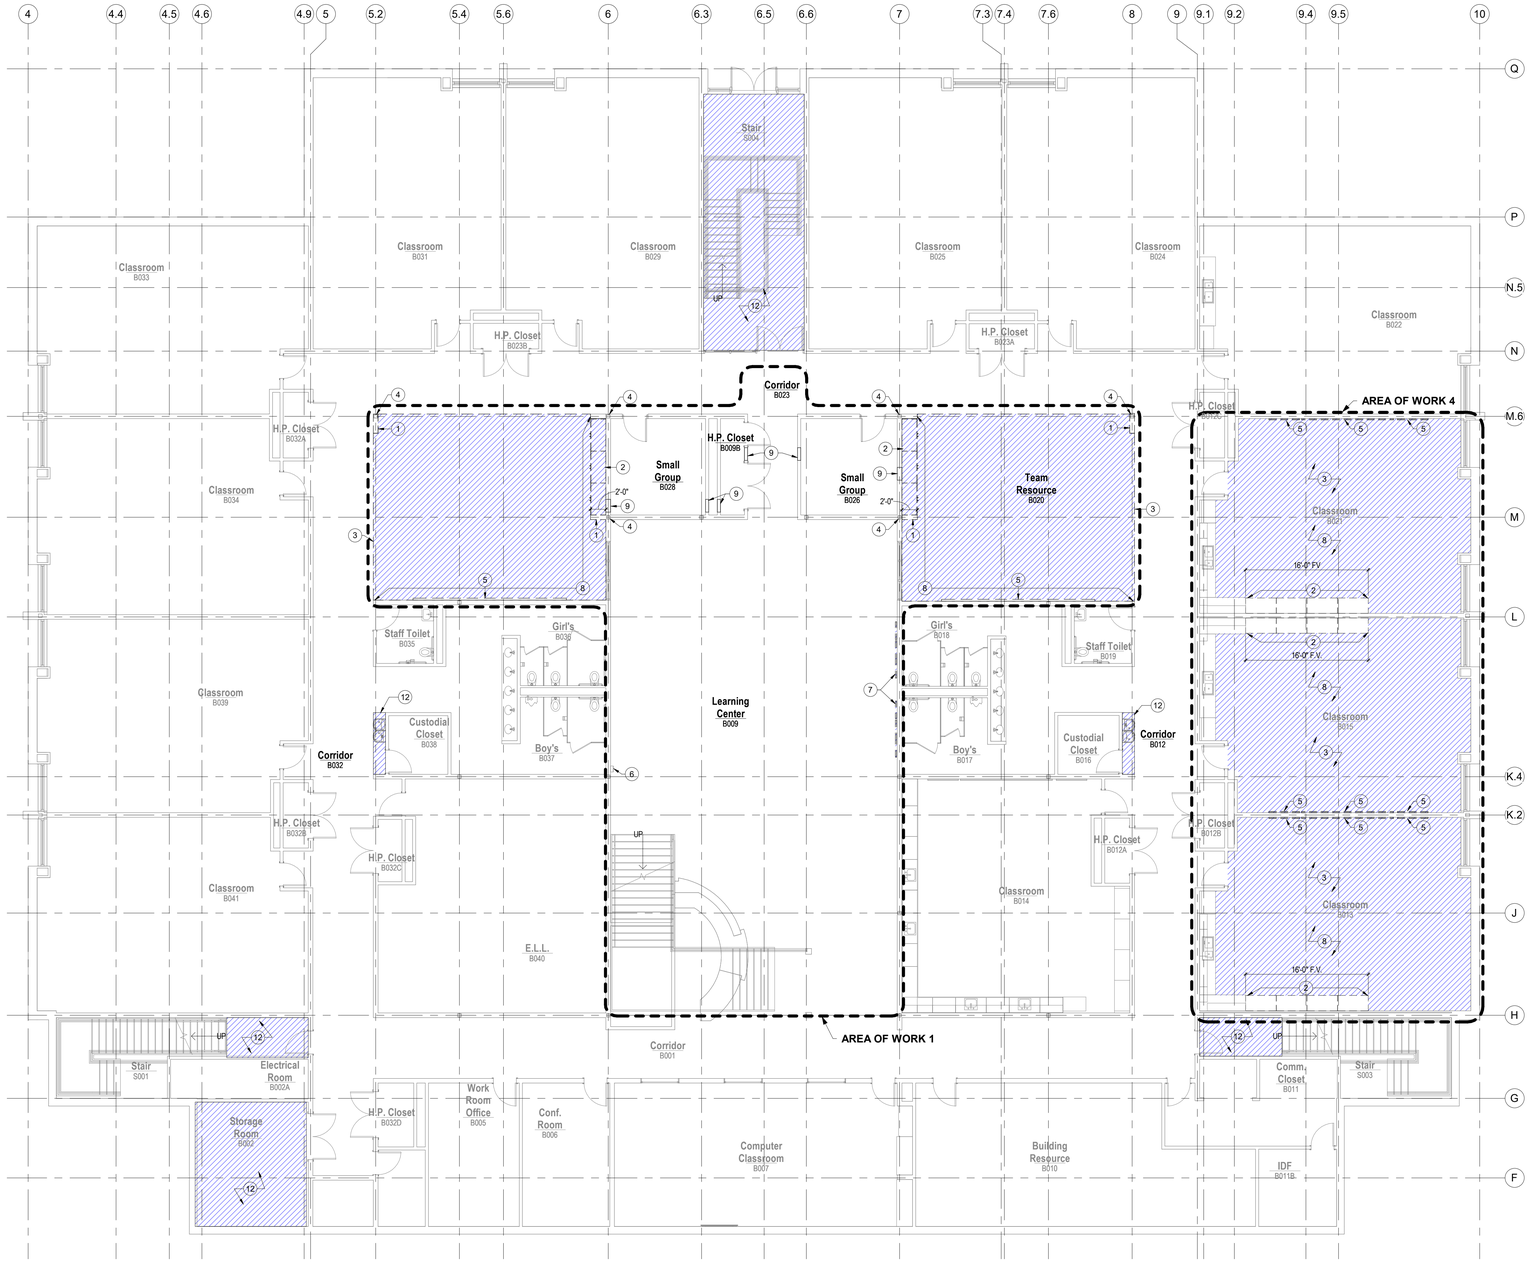

1 Lower Level Demo Plan


SCALE: 1/8" = 1'-0"

GENERAL DEMOLITION NOTES

1. THE GENERAL CONTRACTOR SHALL VERIFY ALL EXISTING DIMENSIONS AND CONDITIONS SHOWN ON THE PLANS PRIOR TO COMMENCEMENT OF THE WORK. IT SHALL BE THE CONTRACTORS RESPONSIBILITY TO COORDINATE INSTALLATION OF NEW WORK WITHIN THESE EXISTING CONDITIONS. ANY DEVIATIONS IN EXISTING CONDITIONS OR DIMENSIONS INDICATED SHALL BE COORDINATED WITH THE ARCHITECT/ENGINEER AND OWNER IN ORDER TO MODIFY THE PLANS ACCORDINGLY.
2. THE EXISTING BUILDING SHALL BE PROTECTED FROM WEATHER AT ALL TIMES. OPENINGS AND PENETRATIONS SHALL BE PROTECTED WITH DURABLE, INSULATED TEMPORARY CONSTRUCTION. COORDINATE SECURITY REQUIREMENTS WITH THE OWNER.
3. ALL WORK IS TO BE PERFORMED IN SUCH A MANNER AS TO MINIMIZE THE IMPACT ON AREAS ADJACENT TO THE AREAS OF CONSTRUCTION.
4. REMOVE EXISTING FLOORS, WALLS AND CEILINGS AS REQUIRED FOR NEW CONSTRUCTION. PATCH, REPAIR AND PREPARE ADJACENT SURFACES AS REQUIRED FOR NEW CONSTRUCTION AND FINISHES.
5. REFER TO MECHANICAL AND ELECTRICAL DRAWINGS FOR ADDITIONAL INFORMATION PERTAINING TO DEMOLITION.
6. REMOVE EXISTING FURNITURE, FIXTURES AND EQUIPMENT (INCLUDING ARTWORK AND MARKER/TACK BOARDS) AS REQUIRED FOR NEW CONSTRUCTION. COORDINATE SALVAGE AND STORAGE OF EQUIPMENT WITH OWNER AS REQUIRED. PROTECT AND STORE ALL ITEMS DESIGNATED TO BE SALVAGED FOR REINSTALLATION.
7. REMOVE EXISTING SIGNAGE AS REQUIRED FOR DEMOLITION AND STORE DURING CONSTRUCTION. REINSTALL WHEN APPLICABLE. PATCH AND PREPARE ADJACENT SURFACES AS REQUIRED FOR NEW FINISHES. ALL NEW SIGNAGE TO BE PROVIDED BY OWNER.
8. ALL OPENINGS AND VOIDS LEFT BY THE REMOVAL OF EXISTING CONSTRUCTION, EQUIPMENT, PIPING, DUCTS, ETC. SHALL BE PROPERLY PATCHED AND CLOSED OFF TO MAINTAIN PROPER FIRE RATING IN WALLS, IF APPLICABLE. PATCH AND PREPARE ANY AREAS TO RECEIVE NEW FINISHES AS REQUIRED.
9. THE ARCHITECT ASSUMES NO RESPONSIBILITY FOR THE DETECTION OR REMOVAL OF ANY HAZARDOUS MATERIALS, INCLUDING, BUT NOT LIMITED TO, ASBESTOS IN ANY FORM. PARTIES RESPONSIBLE FOR DEMOLITION SHALL NOTIFY THE OWNER IMMEDIATELY OF ANY SUSPECTED MATERIALS.
10. THE OWNER HAS THE RIGHT TO CLAIM ANY MATERIALS AND/OR EQUIPMENT THAT ARE SCHEDULED TO BE DEMOLISHED OR REMOVED FROM THE SITE.
11. ALL EXISTING BUILDING ELEMENTS TO REMAIN SHALL BE PROTECTED DURING CONSTRUCTION.
12. REMOVE EXISTING FLOOR FINISHES WHERE INDICATED. DEMOLITION INCLUDES REMOVAL OF EXISTING ADHESIVES, GROUTING BED, ETC. PATCH AND PREPARE FLOOR AND WALL SURFACES AS REQUIRED FOR NEW CONSTRUCTION AND FINISHES. WHERE FLOOR FINISH IS REMOVED, BASE WILL BE REMOVED. SEE FINISH PLAN FOR ADDITIONAL INFORMATION.
13. PREPARE EXISTING SUBSTRATES TO REMAIN AS REQUIRED TO RECEIVE NEW FINISHES.

DEMOLITION KEY NOTES

1. REMOVE EXISTING WALL ASSEMBLY IN ITS ENTIRETY OR AS REQUIRED FOR NEW CONSTRUCTION. PATCH AND PREPARE ADJACENT SURFACES AS REQUIRED FOR NEW CONSTRUCTION.
2. REMOVE EXISTING CASEWORK AS INDICATED. PATCH AND PREPARE ADJACENT SURFACES AS REQUIRED FOR NEW CONSTRUCTION AND/OR TO RECEIVE NEW FINISHES..
3. REMOVE THE INDICATED PORTION OF THE EXISTING FLOOR FINISH MATERIAL AS REQUIRED FOR NEW CONSTRUCTION. PATCH AND PREPARE EXISTING SURFACES AS REQUIRED FOR NEW CONSTRUCTION
4. EXISTING COLUMN TO REMAIN.
5. REMOVE EXISTING MARKERBOARDS AND TACKBOARDS IN THEIR ENTIRETY. SALVAGE FOR RETURN TO THE OWNER. PATCH AND PREPARE ADJACENT SURFACES AS REQUIRED FOR NEW CONSTRUCTION.
6. ROUT SEPARATION CRACK IN EXISTING CONCRETE SLAB AS REQUIRED FOR THE INSTALLATION OF A NEW SEALANT JOINT. EDGES SHALL BE STRAIGHT AND PREPARED AS REQUIRED FOR THE INSTALLATION OF THE JOINT. PATCH AND PREPARE ADJACENT SURFACES AS REQUIRED FOR NEW CONSTRUCTION
7. REMOVE EXISTING ACOUSTICAL PANELS AND SALVAGE FOR REINSTALLATION. PATCH AND PREPARE ADJACENT SURFACES AS REQUIRED FOR NEW CONSTRUCTION.
8. REMOVE EXISTING RUBBER BASE IN ITS ENTIRETY . PATCH AND PREPARE ADJACENT SURFACES AS REQUIRED FOR NEW CONSTRUCTION.
9. REMOVE A PORTION OF THE EXISTING WALL ASSEMBLY AS REQUIRED FOR INSTALLATION OF NEW DUCT WORK. COORDINATE SPECIFIC LOCATIONS AND EXTENTS WITH MECHANICAL. PROVIDE ADDITIONAL FRAMING AROUND THE NEW OPENING AS REQUIRED TO MAINTAIN INTEGRITY OF THE WALL ASSEMBLY. PATCH AND PREPARE ADJACENT SURFACES AS REQUIRED FOR NEW CONSTRUCTION.
10. NOT USED
11. NOT USED
12. REMOVE EXISTING VCT FLOORING AND ASSOCIATED BASE IN ITS ENTIRETY AND PREPARE FLOORS AS REQUIRED FOR NEW FINISHES. PATCH AND PREPARE ADJACENT SURFACES AS REQUIRED FOR NEW CONSTRUCTION

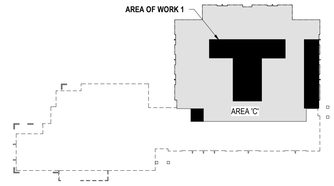

2 Lower Level Key Plan

SCALE: 1" = 80'-0"

DAO ARCHITECTURE

7230 Meade St.
Westminster, CO 80030

Phone: 720.273.0431
Email: dan@daoarch.com
Web: www.daoarch.com

Westminster Public Schools

Hodgkins Leadership Academy Classroom Conversion Project

3475 W 67th Ave,
Denver, CO 80221


DAO No.:2021-033

September 25, 2026

Lower Level Demolition Plan


AD1.0

Autodesk Docs://WPS 2026 Bond Projects - Hodgkins Classroom Conversion/Hodgkins ES Classroom Conversion (Revit 2026).rvt
9/25/2026 9:14:10 AM

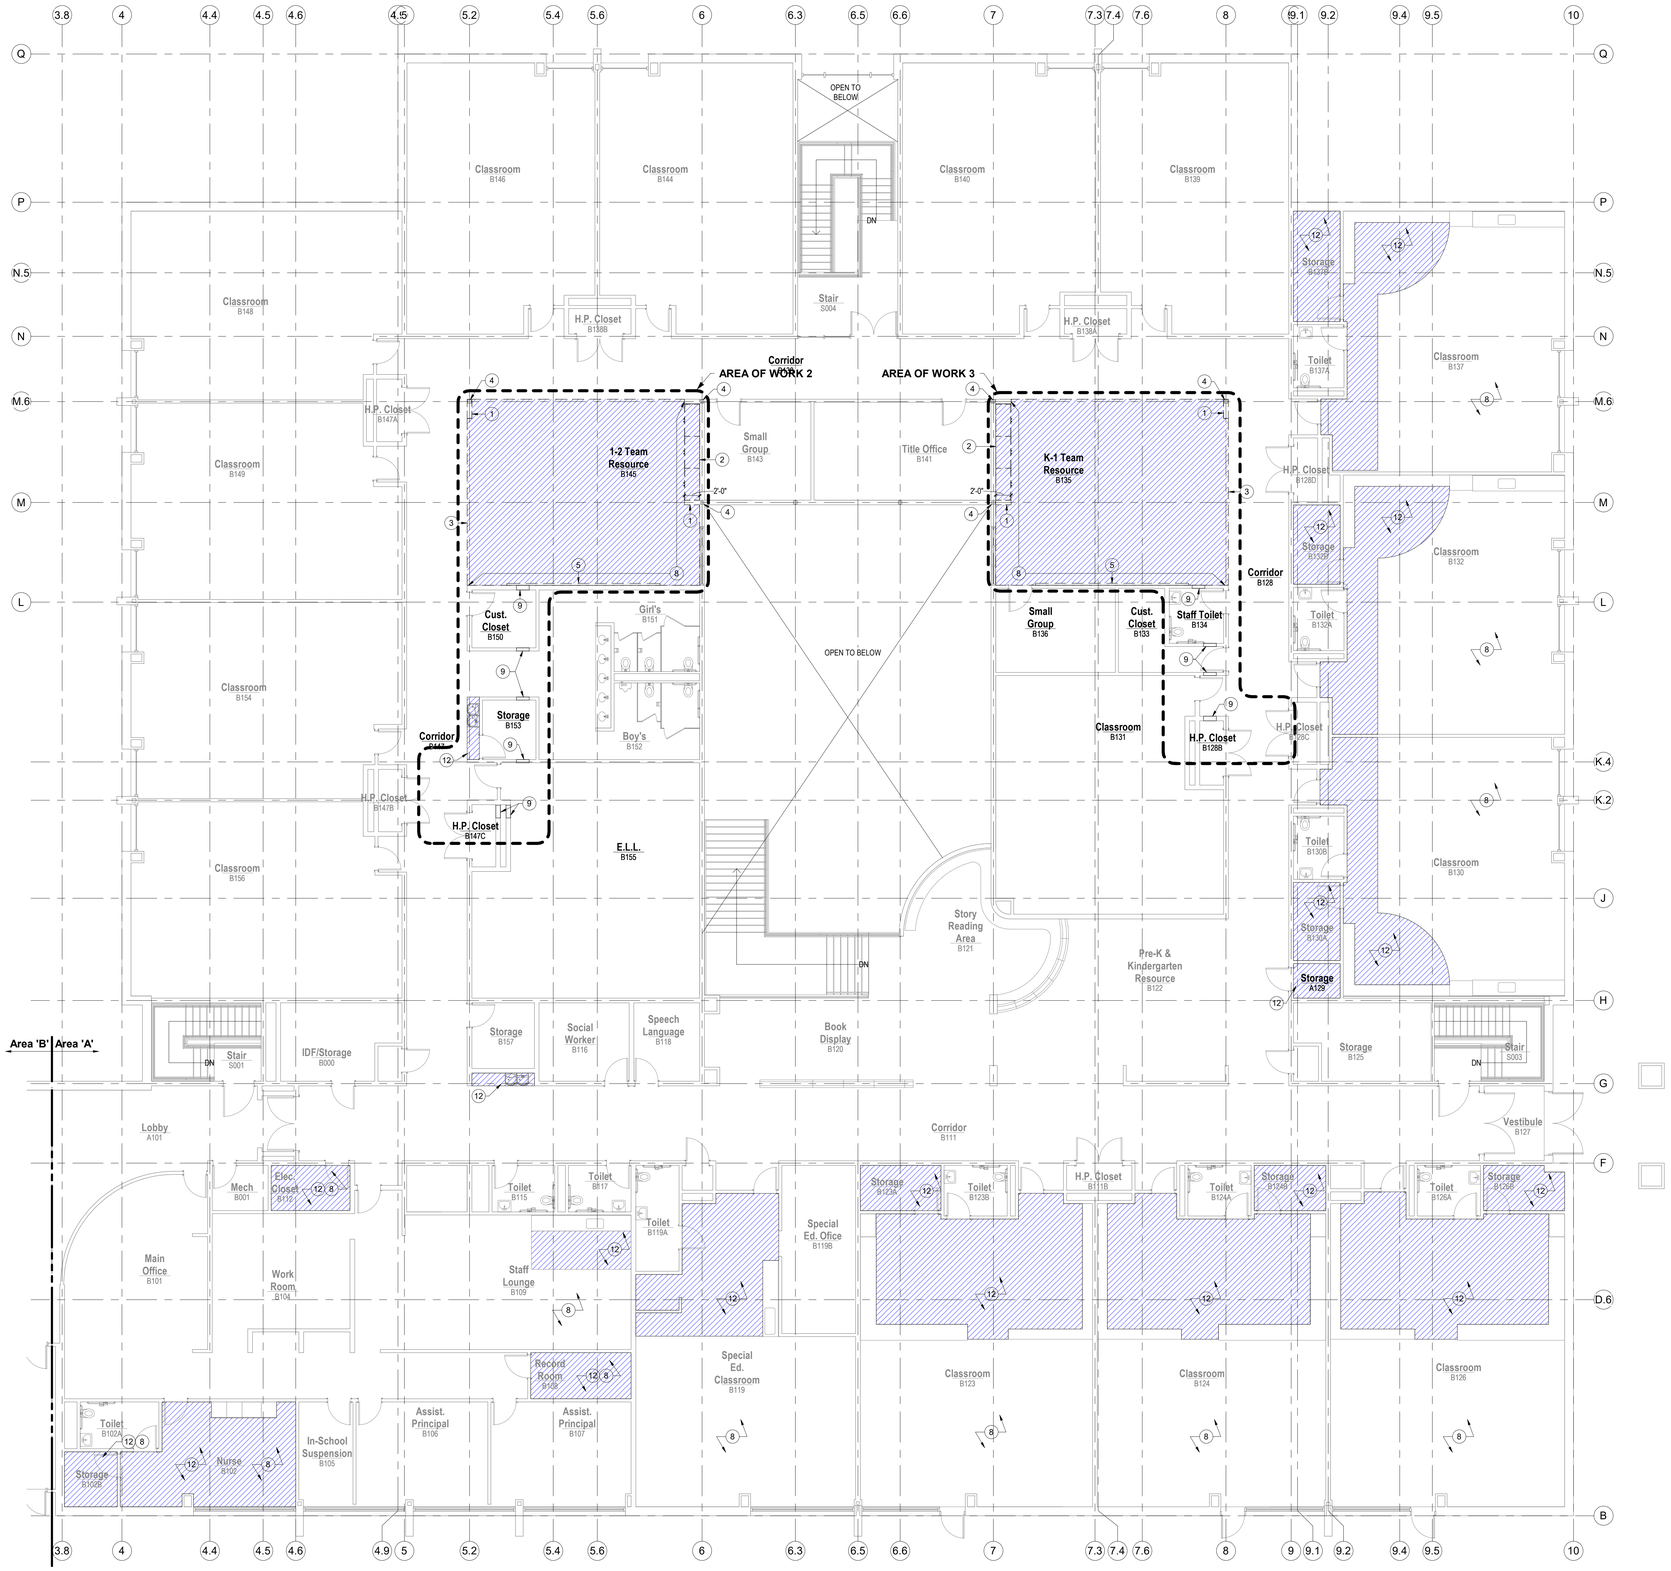

1 Main Level Demo Plan

SCALE: 1/8" = 1'-0"

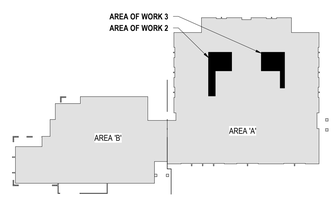

2 Main Level Key Plan

SCALE: 1" = 80'-0"

GENERAL DEMOLITION NOTES

1. THE GENERAL CONTRACTOR SHALL VERIFY ALL EXISTING DIMENSIONS AND CONDITIONS SHOWN ON THE PLANS PRIOR TO COMMENCEMENT OF THE WORK. IT SHALL BE THE CONTRACTORS RESPONSIBILITY TO COORDINATE INSTALLATION OF NEW WORK WITHIN THESE EXISTING CONDITIONS. ANY DEVIATIONS IN EXISTING CONDITIONS OR DIMENSIONS INDICATED SHALL BE COORDINATED WITH THE ARCHITECT/ENGINEER AND OWNER IN ORDER TO MODIFY THE PLANS ACCORDINGLY.
2. THE EXISTING BUILDING SHALL BE PROTECTED FROM WEATHER AT ALL TIMES. OPENINGS AND PENETRATIONS SHALL BE PROTECTED WITH DURABLE, INSULATED TEMPORARY CONSTRUCTION. COORDINATE SECURITY REQUIREMENTS WITH THE OWNER.
3. ALL WORK IS TO BE PERFORMED IN SUCH A MANNER AS TO MINIMIZE THE IMPACT ON AREAS ADJACENT TO THE AREAS OF CONSTRUCTION.
4. REMOVE EXISTING FLOORS, WALLS AND CEILINGS AS REQUIRED FOR NEW CONSTRUCTION. PATCH, REPAIR AND PREPARE ADJACENT SURFACES AS REQUIRED FOR NEW CONSTRUCTION AND FINISHES.
5. REFER TO MECHANICAL AND ELECTRICAL DRAWINGS FOR ADDITIONAL INFORMATION PERTAINING TO DEMOLITION.
6. REMOVE EXISTING FURNITURE, FIXTURES AND EQUIPMENT (INCLUDING ARTWORK AND MARKER/TACK BOARDS) AS REQUIRED FOR NEW CONSTRUCTION. COORDINATE SALVAGE AND STORAGE OF EQUIPMENT WITH OWNER AS REQUIRED. PROTECT AND STORE ALL ITEMS DESIGNATED TO BE SALVAGED FOR REINSTALLATION.
7. REMOVE EXISTING SIGNAGE AS REQUIRED FOR DEMOLITION AND STORE DURING CONSTRUCTION. REINSTALL WHEN APPLICABLE. PATCH AND PREPARE ADJACENT SURFACES AS REQUIRED FOR NEW FINISHES. ALL NEW SIGNAGE TO BE PROVIDED BY OWNER.
8. ALL OPENINGS AND VOIDS LEFT BY THE REMOVAL OF EXISTING CONSTRUCTION, EQUIPMENT, PIPING, DUCTS, ETC. SHALL BE PROPERLY PATCHED AND CLOSED OFF TO MAINTAIN PROPER FIRE RATING IN WALLS, IF APPLICABLE. PATCH AND PREPARE ANY AREAS TO RECEIVE NEW FINISHES AS REQUIRED.
9. THE ARCHITECT ASSUMES NO RESPONSIBILITY FOR THE DETECTION OR REMOVAL OF ANY HAZARDOUS MATERIALS, INCLUDING, BUT NOT LIMITED TO, ASBESTOS IN ANY FORM. PARTIES RESPONSIBLE FOR DEMOLITION SHALL NOTIFY THE OWNER IMMEDIATELY OF ANY SUSPECTED MATERIALS.
10. THE OWNER HAS THE RIGHT TO CLAIM ANY MATERIALS AND/OR EQUIPMENT THAT ARE SCHEDULED TO BE DEMOLISHED OR REMOVED FROM THE SITE.
11. ALL EXISTING BUILDING ELEMENTS TO REMAIN SHALL BE PROTECTED DURING CONSTRUCTION.
12. REMOVE EXISTING FLOOR FINISHES WHERE INDICATED. DEMOLITION INCLUDES REMOVAL OF EXISTING ADHESIVES, GROUTING BED, ETC. PATCH AND PREPARE FLOOR AND WALL SURFACES AS REQUIRED FOR NEW CONSTRUCTION AND FINISHES. WHERE FLOOR FINISH IS REMOVED, BASE WILL BE REMOVED. SEE FINISH PLAN FOR ADDITIONAL INFORMATION.
13. PREPARE EXISTING SUBSTRATES TO REMAIN AS REQUIRED TO RECEIVE NEW FINISHES.

DEMOLITION KEY NOTES

1. REMOVE EXISTING WALL ASSEMBLY IN ITS ENTIRETY OR AS REQUIRED FOR NEW CONSTRUCTION. PATCH AND PREPARE ADJACENT SURFACES AS REQUIRED FOR NEW CONSTRUCTION.
2. REMOVE EXISTING CASEWORK AS INDICATED. PATCH AND PREPARE ADJACENT SURFACES AS REQUIRED FOR NEW CONSTRUCTION AND/OR TO RECEIVE NEW FINISHES.
3. REMOVE THE INDICATED PORTION OF THE EXISTING FLOOR FINISH MATERIAL AS REQUIRED FOR NEW CONSTRUCTION. PATCH AND PREPARE EXISTING SURFACES AS REQUIRED FOR NEW CONSTRUCTION
4. EXISTING COLUMN TO REMAIN.
5. REMOVE EXISTING MARKERBOARDS AND TACKBOARDS IN THEIR ENTIRETY. SALVAGE FOR RETURN TO THE OWNER. PATCH AND PREPARE ADJACENT SURFACES AS REQUIRED FOR NEW CONSTRUCTION.
6. ROUT SEPARATION CRACK IN EXISTING CONCRETE SLAB AS REQUIRED FOR THE INSTALLATION OF A NEW SEALANT JOINT. EDGES SHALL BE STRAIGHT AND PREPARED AS REQUIRED FOR THE INSTALLATION OF THE JOINT. PATCH AND PREPARE ADJACENT SURFACES AS REQUIRED FOR NEW CONSTRUCTION
7. REMOVE EXISTING ACOUSTICAL PANELS AND SALVAGE FOR REINSTALLATION. PATCH AND PREPARE ADJACENT SURFACES AS REQUIRED FOR NEW CONSTRUCTION.
8. REMOVE EXISTING RUBBER BASE IN ITS ENTIRETY . PATCH AND PREPARE ADJACENT SURFACES AS REQUIRED FOR NEW CONSTRUCTION.
9. REMOVE A PORTION OF THE EXISTING WALL ASSEMBLY AS REQUIRED FOR INSTALLATION OF NEW DUCT WORK. COORDINATE SPECIFIC LOCATIONS AND EXTENTS WITH MECHANICAL. PROVIDE ADDITIONAL FRAMING AROUND THE NEW OPENING AS REQUIRED TO MAINTAIN INTEGRITY OF THE WALL ASSEMBLY. PATCH AND PREPARE ADJACENT SURFACES AS REQUIRED FOR NEW CONSTRUCTION.
10. NOT USED
11. NOT USED
12. REMOVE EXISTING VCT FLOORING AND ASSOCIATED BASE IN ITS ENTIRETY AND PREPARE FLOORS AS REQUIRED FOR NEW FINISHES. PATCH AND PREPARE ADJACENT SURFACES AS REQUIRED FOR NEW CONSTRUCTION

DAO ARCHITECTURE
7230 Meade St.
Westminster, CO 80030
Phone: 720.273.0431
Email: dan@daoarch.com
Web: www.daoarch.com

Westminster Public Schools

Hodgkins Leadership Academy Classroom Conversion Project

3475 W 67th Ave,
Denver, CO 80221


DAO No.:2021-033

September 25, 2026

Main Level Demolition Plan
Area 'A'

AD1.1

Autodesk Docs://WPS 2026 Bond Projects - Hodgkins Classroom Conversion/Hodgkins ES Classroom Conversion (Revit 2026).rvt
9/25/2026 9:14:11 AM

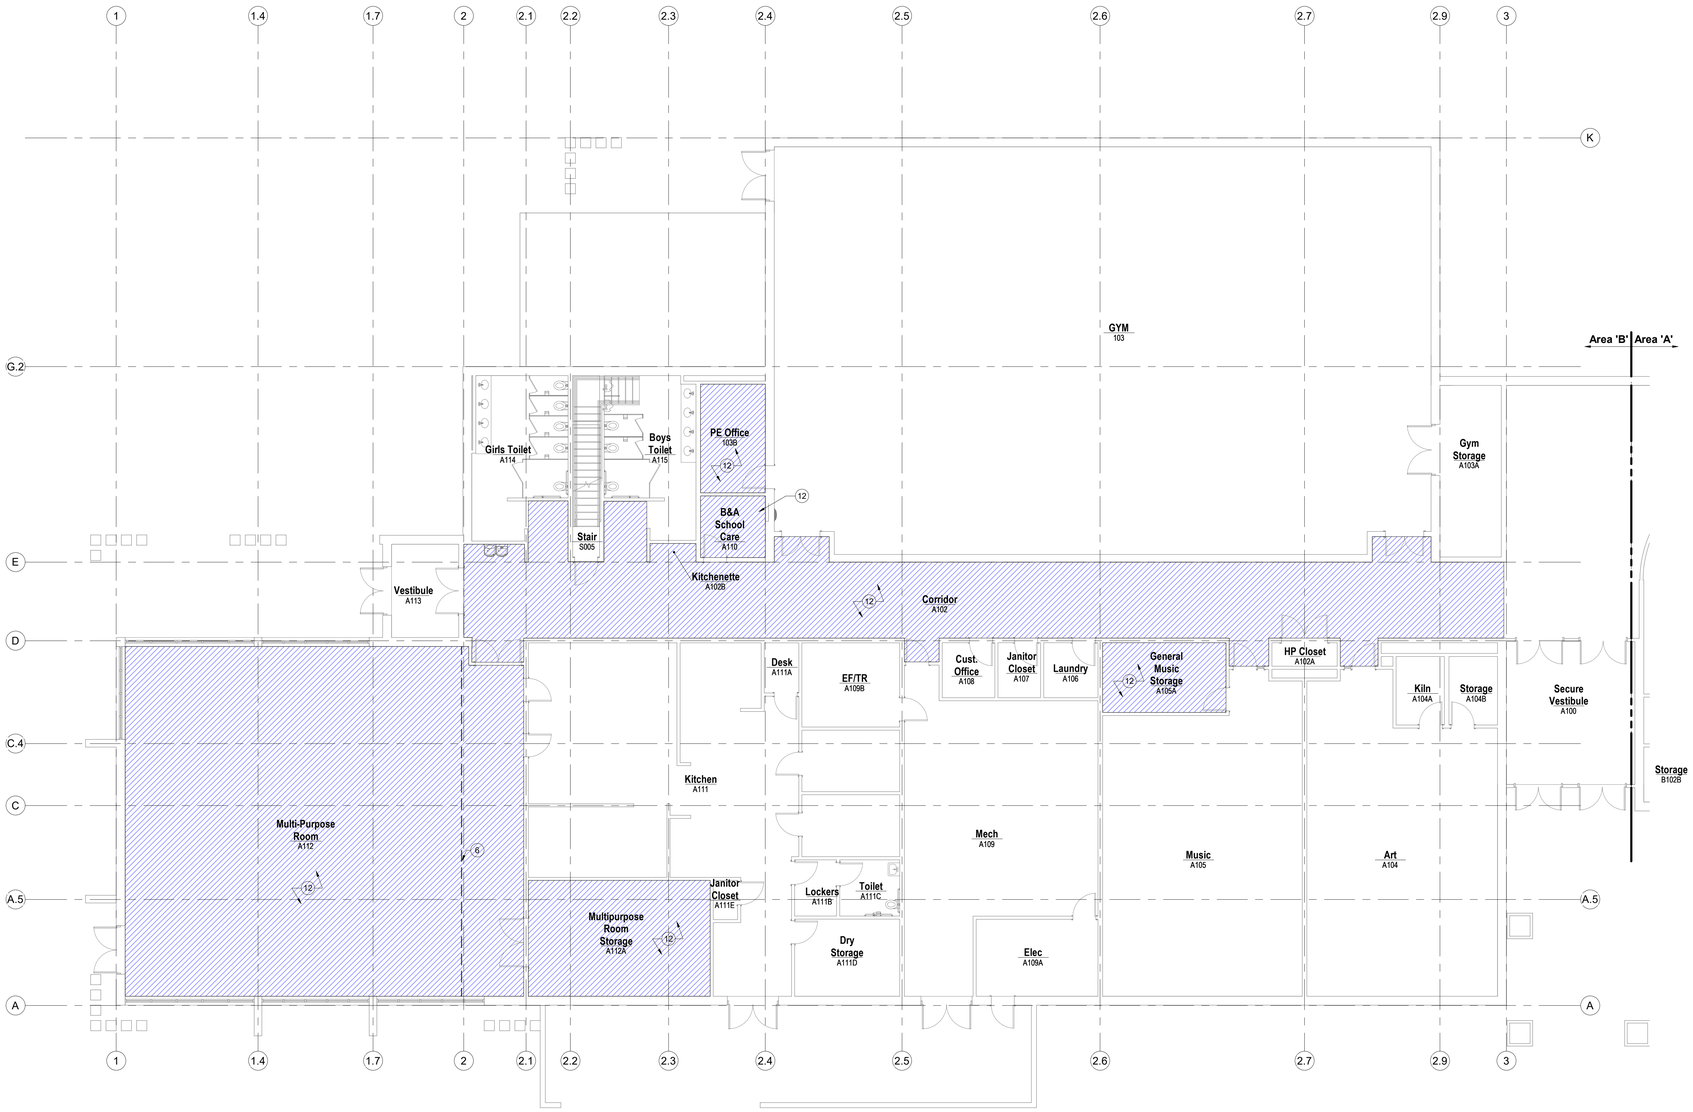

1 Main Level Demo Plan Area B


SCALE: 1/8" = 1'-0"

GENERAL DEMOLITION NOTES

1. THE GENERAL CONTRACTOR SHALL VERIFY ALL EXISTING DIMENSIONS AND CONDITIONS SHOWN ON THE PLANS PRIOR TO COMMENCEMENT OF THE WORK. IT SHALL BE THE CONTRACTORS RESPONSIBILITY TO COORDINATE INSTALLATION OF NEW WORK WITHIN THESE EXISTING CONDITIONS. ANY DEVIATIONS IN EXISTING CONDITIONS OR DIMENSIONS INDICATED SHALL BE COORDINATED WITH THE ARCHITECT/ENGINEER AND OWNER IN ORDER TO MODIFY THE PLANS ACCORDINGLY.
2. THE EXISTING BUILDING SHALL BE PROTECTED FROM WEATHER AT ALL TIMES. OPENINGS AND PENETRATIONS SHALL BE PROTECTED WITH DURABLE, INSULATED TEMPORARY CONSTRUCTION. COORDINATE SECURITY REQUIREMENTS WITH THE OWNER.
3. ALL WORK IS TO BE PERFORMED IN SUCH A MANNER AS TO MINIMIZE THE IMPACT ON AREAS ADJACENT TO THE AREAS OF CONSTRUCTION.
4. REMOVE EXISTING FLOORS, WALLS AND CEILINGS AS REQUIRED FOR NEW CONSTRUCTION. PATCH, REPAIR AND PREPARE ADJACENT SURFACES AS REQUIRED FOR NEW CONSTRUCTION AND FINISHES.
5. REFER TO MECHANICAL AND ELECTRICAL DRAWINGS FOR ADDITIONAL INFORMATION PERTAINING TO DEMOLITION.
6. REMOVE EXISTING FURNITURE, FIXTURES AND EQUIPMENT (INCLUDING ARTWORK AND MARKER/TACK BOARDS) AS REQUIRED FOR NEW CONSTRUCTION. COORDINATE SALVAGE AND STORAGE OF EQUIPMENT WITH OWNER AS REQUIRED. PROTECT AND STORE ALL ITEMS DESIGNATED TO BE SALVAGED FOR REINSTALLATION.
7. REMOVE EXISTING SIGNAGE AS REQUIRED FOR DEMOLITION AND STORE DURING CONSTRUCTION. REINSTALL WHEN APPLICABLE. PATCH AND PREPARE ADJACENT SURFACES AS REQUIRED FOR NEW FINISHES. ALL NEW SIGNAGE TO BE PROVIDED BY OWNER.
8. ALL OPENINGS AND VOIDS LEFT BY THE REMOVAL OF EXISTING CONSTRUCTION, EQUIPMENT, PIPING, DUCTS, ETC. SHALL BE PROPERLY PATCHED AND CLOSED OFF TO MAINTAIN PROPER FIRE RATING IN WALLS, IF APPLICABLE. PATCH AND PREPARE ANY AREAS TO RECEIVE NEW FINISHES AS REQUIRED.
9. THE ARCHITECT ASSUMES NO RESPONSIBILITY FOR THE DETECTION OR REMOVAL OF ANY HAZARDOUS MATERIALS, INCLUDING, BUT NOT LIMITED TO, ASBESTOS IN ANY FORM. PARTIES RESPONSIBLE FOR DEMOLITION SHALL NOTIFY THE OWNER IMMEDIATELY OF ANY SUSPECTED MATERIALS.
10. THE OWNER HAS THE RIGHT TO CLAIM ANY MATERIALS AND/OR EQUIPMENT THAT ARE SCHEDULED TO BE DEMOLISHED OR REMOVED FROM THE SITE.
11. ALL EXISTING BUILDING ELEMENTS TO REMAIN SHALL BE PROTECTED DURING CONSTRUCTION.
12. REMOVE EXISTING FLOOR FINISHES WHERE INDICATED. DEMOLITION INCLUDES REMOVAL OF EXISTING ADHESIVES, GROUTING BED, ETC. PATCH AND PREPARE FLOOR AND WALL SURFACES AS REQUIRED FOR NEW CONSTRUCTION AND FINISHES. WHERE FLOOR FINISH IS REMOVED, BASE WILL BE REMOVED. SEE FINISH PLAN FOR ADDITIONAL INFORMATION.
13. PREPARE EXISTING SUBSTRATES TO REMAIN AS REQUIRED TO RECEIVE NEW FINISHES.

DEMOLITION KEY NOTES

1. REMOVE EXISTING WALL ASSEMBLY IN ITS ENTIRETY OR AS REQUIRED FOR NEW CONSTRUCTION. PATCH AND PREPARE ADJACENT SURFACES AS REQUIRED FOR NEW CONSTRUCTION.
2. REMOVE EXISTING CASEWORK AS INDICATED. PATCH AND PREPARE ADJACENT SURFACES AS REQUIRED FOR NEW CONSTRUCTION AND/OR TO RECEIVE NEW FINISHES.
3. REMOVE THE INDICATED PORTION OF THE EXISTING FLOOR FINISH MATERIAL AS REQUIRED FOR NEW CONSTRUCTION. PATCH AND PREPARE EXISTING SURFACES AS REQUIRED FOR NEW CONSTRUCTION
4. EXISTING COLUMN TO REMAIN.
5. REMOVE EXISTING MARKERBOARDS AND TACKBOARDS IN THEIR ENTIRETY. SALVAGE FOR RETURN TO THE OWNER. PATCH AND PREPARE ADJACENT SURFACES AS REQUIRED FOR NEW CONSTRUCTION.
6. ROUT SEPARATION CRACK IN EXISTING CONCRETE SLAB AS REQUIRED FOR THE INSTALLATION OF A NEW SEALANT JOINT. EDGES SHALL BE STRAIGHT AND PREPARED AS REQUIRED FOR THE INSTALLATION OF THE JOINT. PATCH AND PREPARE ADJACENT SURFACES AS REQUIRED FOR NEW CONSTRUCTION
7. REMOVE EXISTING ACOUSTICAL PANELS AND SALVAGE FOR REINSTALLATION. PATCH AND PREPARE ADJACENT SURFACES AS REQUIRED FOR NEW CONSTRUCTION.
8. REMOVE EXISTING RUBBER BASE IN ITS ENTIRETY . PATCH AND PREPARE ADJACENT SURFACES AS REQUIRED FOR NEW CONSTRUCTION.
9. REMOVE A PORTION OF THE EXISTING WALL ASSEMBLY AS REQUIRED FOR INSTALLATION OF NEW DUCT WORK. COORDINATE SPECIFIC LOCATIONS AND EXTENTS WITH MECHANICAL. PROVIDE ADDITIONAL FRAMING AROUND THE NEW OPENING AS REQUIRED TO MAINTAIN INTEGRITY OF THE WALL ASSEMBLY. PATCH AND PREPARE ADJACENT SURFACES AS REQUIRED FOR NEW CONSTRUCTION.
10. NOT USED
11. NOT USED
12. REMOVE EXISTING VCT FLOORING AND ASSOCIATED BASE IN ITS ENTIRETY AND PREPARE FLOORS AS REQUIRED FOR NEW FINISHES. PATCH AND PREPARE ADJACENT SURFACES AS REQUIRED FOR NEW CONSTRUCTION

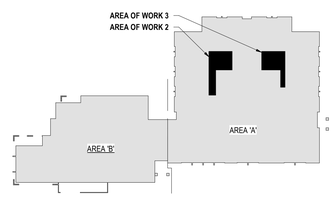

2 Main Level Key Plan

SCALE: 1" = 80'-0"

DAO ARCHITECTURE

7230 Meade St.
Westminster, CO 80030

Phone: 720.273.0431
Email: dan@daoarch.com
Web: www.daoarch.com

Westminster Public Schools

Hodgkins Leadership Academy Classroom Conversion Project

3475 W 67th Ave,
Denver, CO 80221


DAO No.:2021-033

September 25, 2026

Main Level Demolition Plan Area 'B'

AD1.2

Autodesk Docs://WPS 2026 Bond Projects - Hodgkins Classroom Conversion/Hodgkins ES Classroom Conversion (Revit 2026).rvt
9/25/2026 9:14:12 AM

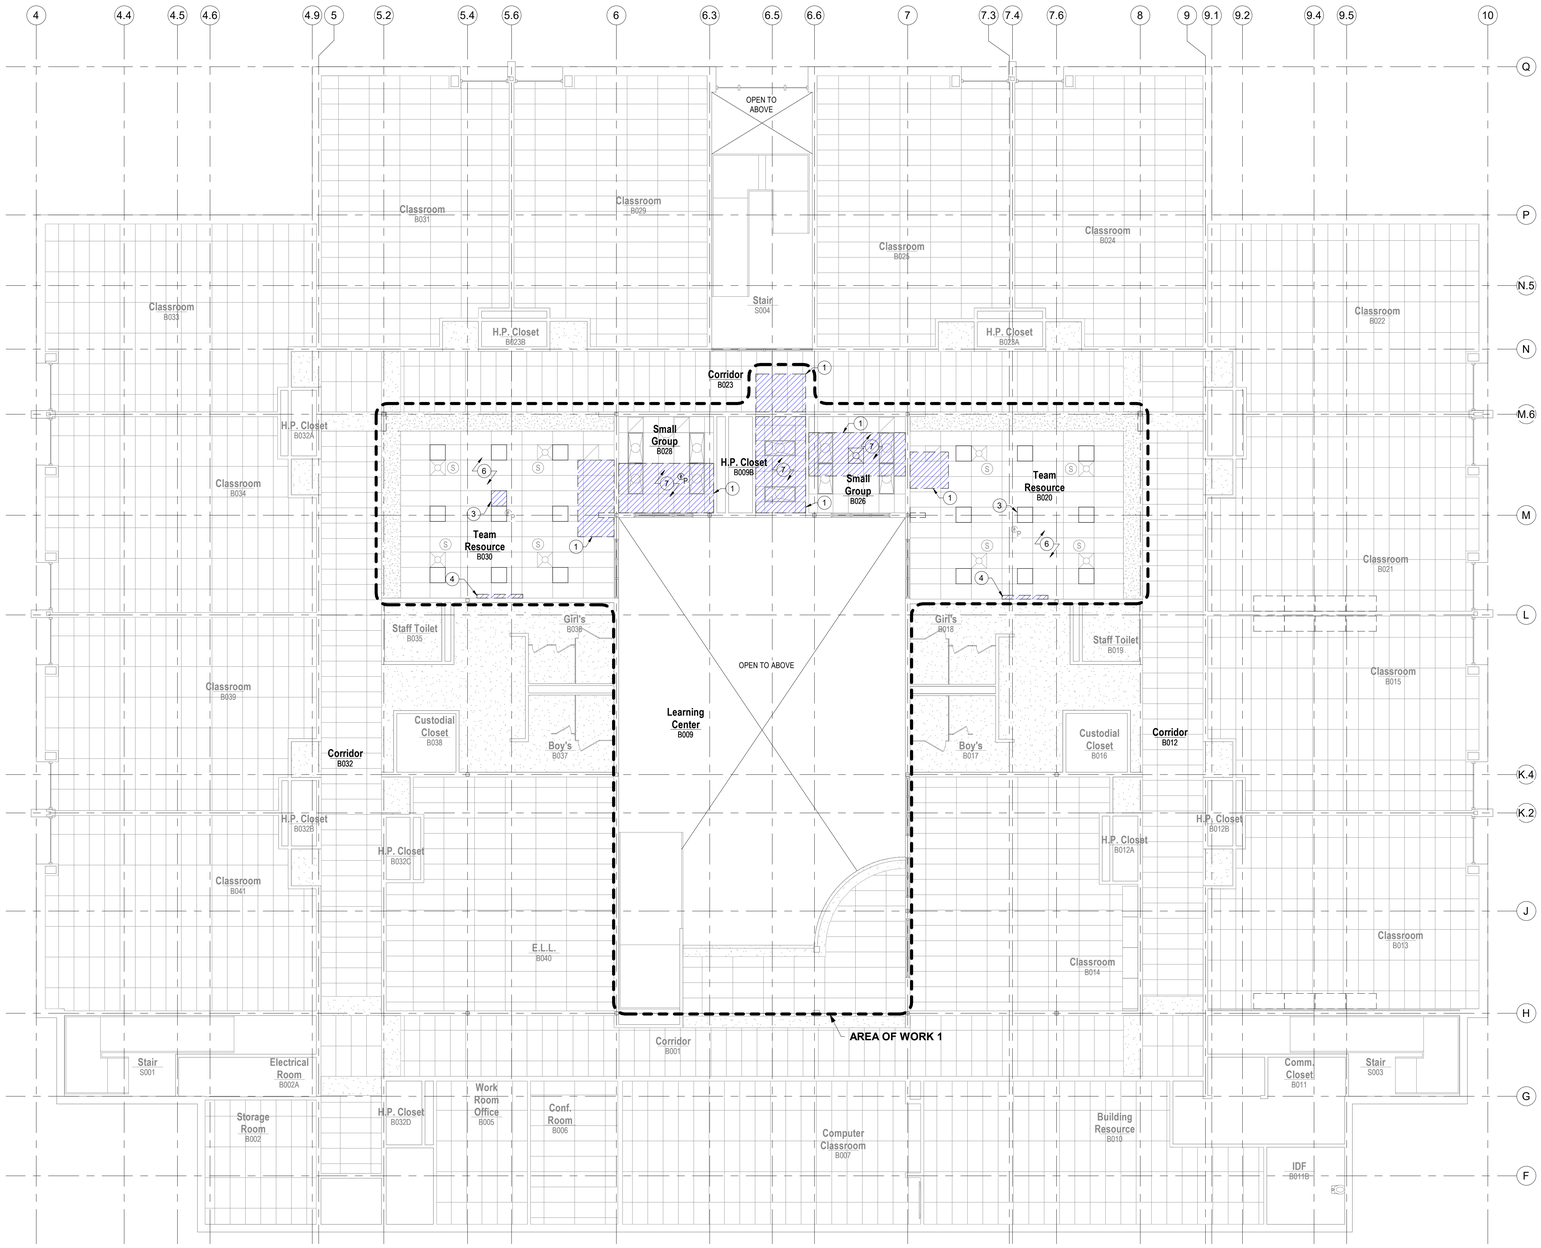

1 Lower Level Demo RCP

SCALE: 1/8" = 1'-0"

GENERAL DEMOLITION RCP NOTES


1. THE GENERAL CONTRACTOR SHALL VERIFY ALL EXISTING DIMENSIONS AND CONDITIONS SHOWN ON THE PLANS PRIOR TO COMMENCEMENT OF THE WORK. IT SHALL BE THE CONTRACTORS RESPONSIBILITY TO COORDINATE INSTALLATION OF NEW WORK WITHIN THESE EXISTING CONDITIONS. ANY DEVIATIONS IN EXISTING CONDITIONS OR DIMENSIONS INDICATED SHALL BE COORDINATED WITH THE ARCHITECT/ENGINEER AND OWNER IN ORDER TO MODIFY THE PLANS ACCORDINGLY.
2. ALL WORK IS TO BE PERFORMED IN SUCH A MANNER AS TO MINIMIZE THE IMPACT ON AREAS ABOVE, BELOW AND ADJACENT TO THE AREAS OF CONSTRUCTION.
3. REMOVE EXISTING FLOORS, WALLS AND CEILINGS AS REQUIRED FOR NEW CONSTRUCTION. PATCH, REPAIR AND PREPARE ADJACENT SURFACES AS REQUIRED FOR NEW CONSTRUCTION AND FINISHES.
4. REFER TO MECHANICAL, ELECTRICAL, AND PLUMBING DRAWINGS FOR ADDITIONAL INFORMATION PERTAINING TO DEMOLITION.
5. ALL OPENINGS AND VOIDS LEFT BY THE REMOVAL OF EXISTING CONSTRUCTION, EQUIPMENT, PIPING, DUCTS, ETC. SHALL BE PROPERLY PATCHED AND CLOSED OFF TO MAINTAIN PROPER FIRE RATING IN WALLS. PATCH AND PREPARE ANY AREAS TO RECEIVE NEW FINISHES AS REQUIRED.
6. THE ARCHITECT ASSUMES NO RESPONSIBILITY FOR THE DETECTION OR REMOVAL OF ANY HAZARDOUS MATERIALS, INCLUDING, BUT NOT LIMITED TO, ASBESTOS IN ANY FORM. PARTIES RESPONSIBLE FOR DEMOLITION SHALL NOTIFY THE OWNER IMMEDIATELY OF ANY SUSPECTED MATERIALS.
7. THE OWNER HAS THE RIGHT TO CLAIM ANY MATERIALS AND/OR EQUIPMENT THAT ARE SCHEDULED TO BE DEMOLISHED OR REMOVED FROM THE SITE.
8. ALL EXISTING BUILDING ELEMENTS TO REMAIN SHALL BE PROTECTED DURING CONSTRUCTION.
9. PREPARE EXISTING SUBSTRATES TO REMAIN AS REQUIRED TO RECEIVE NEW FINISHES.

DEMOLITION RCP KEY NOTES

1. REMOVE PORTION OF EXISTING ACT CEILING SYSTEM AS REQUIRED FOR INSTALLATION OF NEW MECHANICAL SYSTEM. REPAIR ACT SYSTEM AS REQUIRED FOR NEW CONSTRUCTION. REFER TO MECHANICAL DRAWINGS FOR ADDITIONAL INFORMATION.
2. REMOVE EXISTING LIGHT FIXTURES IN THEIR ENTIRETY. PATCH AND PREPARE ADJACENT SURFACES AS REQUIRED FOR NEW CONSTRUCTION.
3. REMOVE EXISTING PROJECTOR AND ADJACENT METAL PANEL IN THEIR ENTIRETY. SALVAGE FOR RETURN TO THE OWNER. PATCH AND PREPARE ADJACENT SURFACES AS REQUIRED FOR NEW CONSTRUCTION.
4. REMOVE EXISTING WALL MOUNTED PROJECTION SCREEN IN ITS ENTIRETY. SALVAGE FOR RETURN TO THE OWNER. PATCH AND PREPARE ADJACENT SURFACES AS REQUIRED.
5. REMOVE PORTION OF EXISTING GPDW CEILING SYSTEM AS REQUIRED FOR INSTALLATION OF NEW MECHANICAL SYSTEM. REPAIR GPDW CEILING AS REQUIRED FOR NEW CONSTRUCTION. REFER TO MECHANICAL DRAWINGS FOR ADDITIONAL INFORMATION.
6. REMOVE PORTION OF EXISTING ACT CEILING SYSTEM AND ALL ASSOCIATED ELECTRICAL, MECHANICAL, AND PLUMBING DEVICES AS REQUIRED FOR NEW CONSTRUCTION. REPAIR ACT SYSTEM AS REQUIRED FOR NEW CONSTRUCTION.
7. REMOVE EXISTING MECHANICAL, ELECTRICAL, AND LOW VOLTAGE DEVICE(S) AS REQUIRED FOR INSTALLATION OF NEW DUCT WORK AND SALVAGE FOR REINSTALLATION. PATCH AND PREPARE ADJACENT SURFACES AS REQUIRED FOR NEW CONSTRUCTION.

RCP SYMBOL LEGEND

- ACOUSTICAL TILE CEILING (24X48)
- GPDW CEILING
- RECESSED LIGHT FIXTURE
- Φ_P PHOTOELECTRIC SMOKE DETECTOR
- HVAC SUPPLY DIFFUSER
- HVAC RETURN DIFFUSER
- (S) CEILING MOUNTED SPEAKER

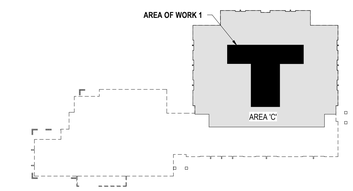

2 Lower Level Key Plan

SCALE: 1" = 80'-0"

DAO ARCHITECTURE
7230 Meade St.
Westminster, CO 80030
Phone: 720.273.0431
Email: dan@daoarch.com
Web: www.daoarch.com

Westminster Public Schools

Hodgkins Leadership Academy Classroom Conversion Project

3475 W 67th Ave,
Denver, CO 80221


DAO No.:2021-033

September 25, 2026

Lower Level Demolition RCP

AD1.3

Autodesk Docs://WPS 2026 Bond Projects - Hodgkins Classroom Conversion/Hodgkins ES Classroom Conversion (Revit 2026).rvt
9/25/2026 9:14:13 AM

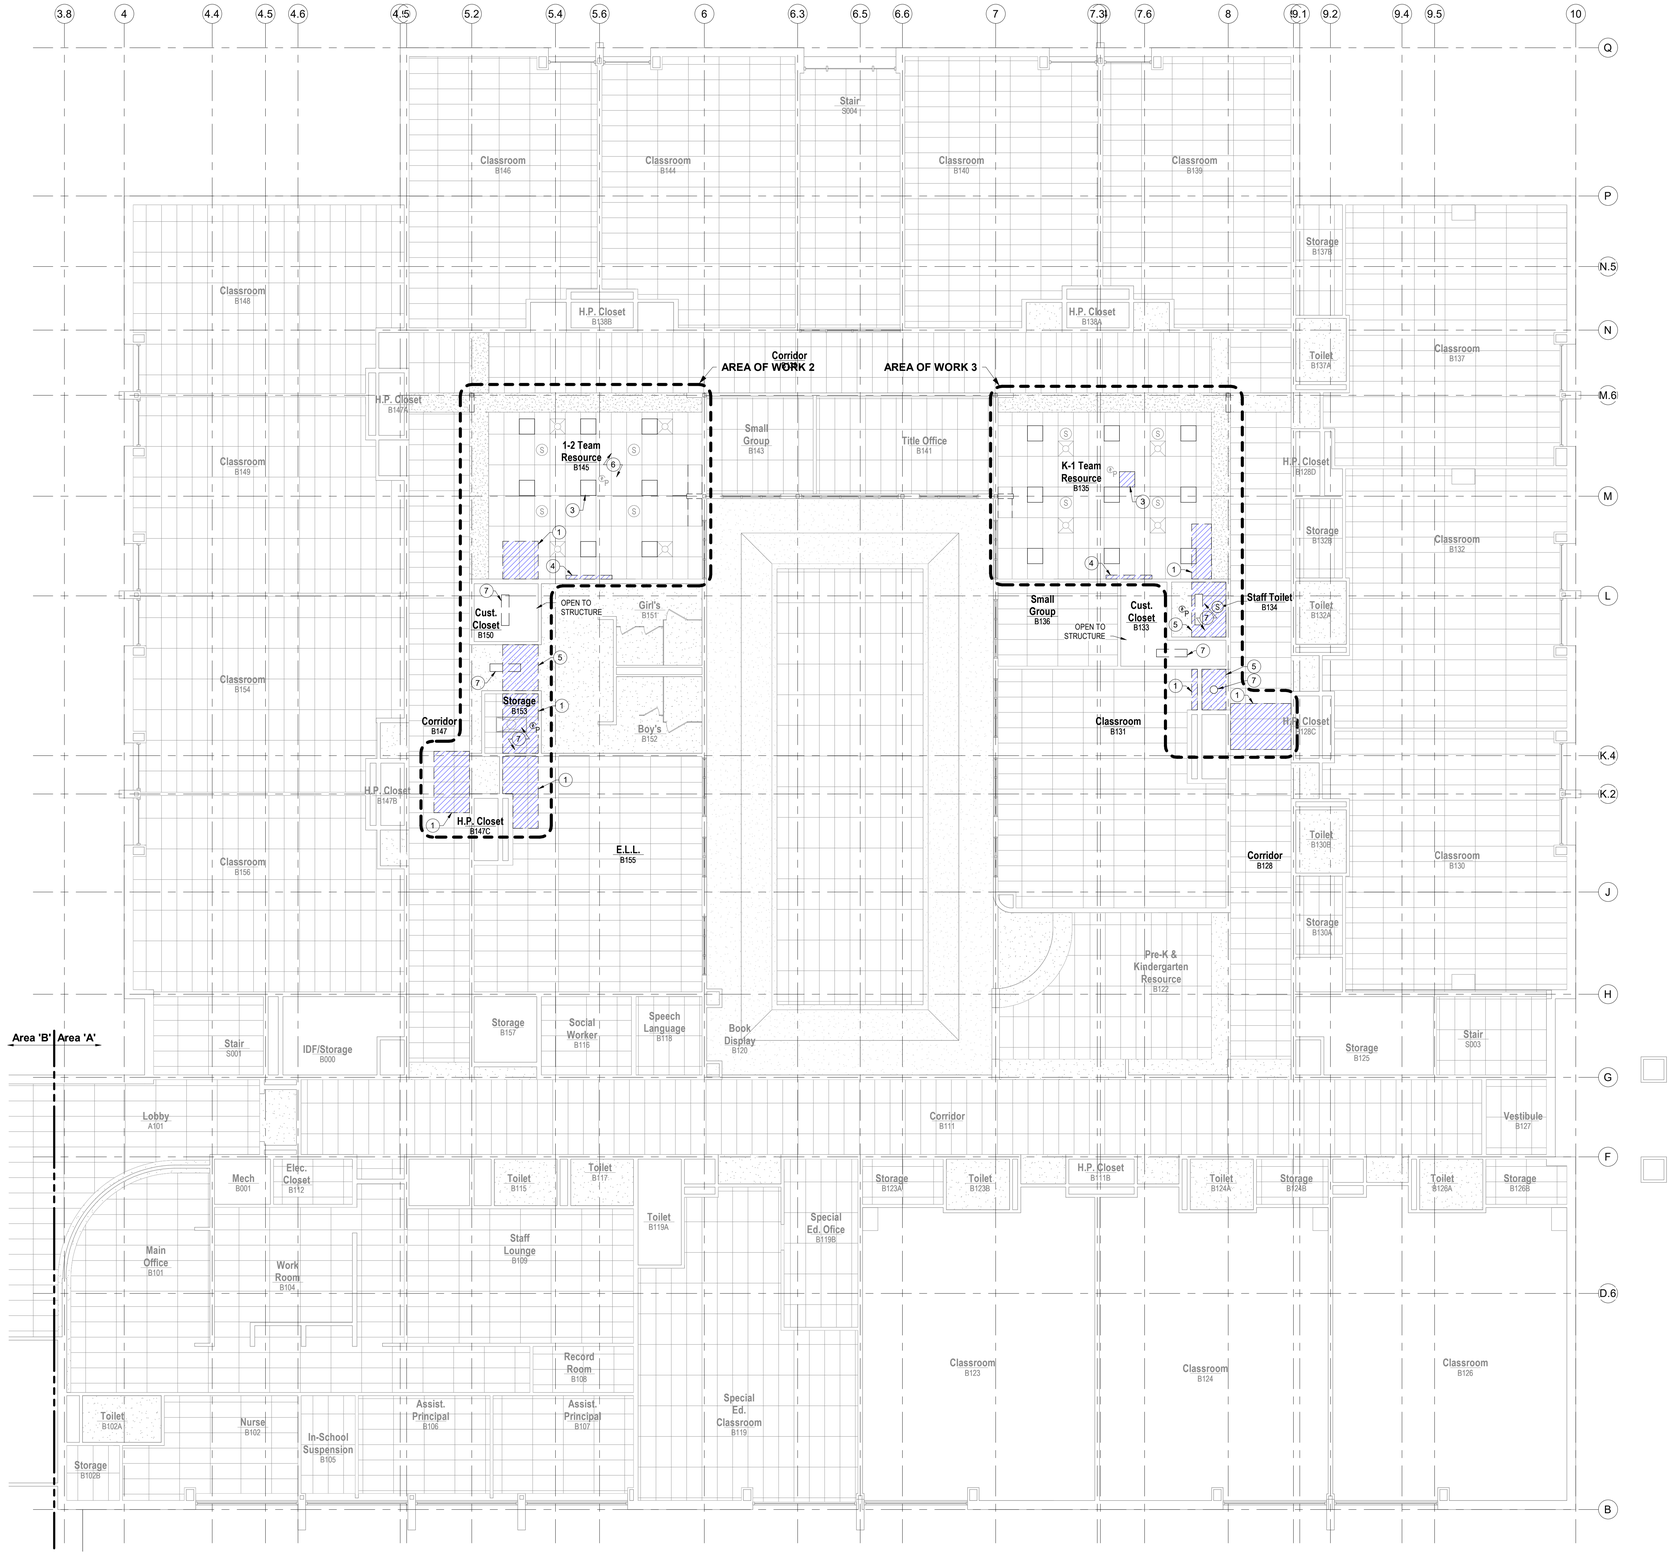

1 Main Level Demo RCP
SCALE: 1/8" = 1'-0"

GENERAL DEMOLITION RCP NOTES


1. THE GENERAL CONTRACTOR SHALL VERIFY ALL EXISTING DIMENSIONS AND CONDITIONS SHOWN ON THE PLANS PRIOR TO COMMENCEMENT OF THE WORK. IT SHALL BE THE CONTRACTORS RESPONSIBILITY TO COORDINATE INSTALLATION OF NEW WORK WITHIN THESE EXISTING CONDITIONS. ANY DEVIATIONS IN EXISTING CONDITIONS OR DIMENSIONS INDICATED SHALL BE COORDINATED WITH THE ARCHITECT/ENGINEER AND OWNER IN ORDER TO MODIFY THE PLANS ACCORDINGLY.
2. ALL WORK IS TO BE PERFORMED IN SUCH A MANNER AS TO MINIMIZE THE IMPACT ON AREAS ABOVE, BELOW AND ADJACENT TO THE AREAS OF CONSTRUCTION.
3. REMOVE EXISTING FLOORS, WALLS AND CEILINGS AS REQUIRED FOR NEW CONSTRUCTION. PATCH, REPAIR AND PREPARE ADJACENT SURFACES AS REQUIRED FOR NEW CONSTRUCTION AND FINISHES.
4. REFER TO MECHANICAL, ELECTRICAL, AND PLUMBING DRAWINGS FOR ADDITIONAL INFORMATION PERTAINING TO DEMOLITION.
5. ALL OPENINGS AND VOIDS LEFT BY THE REMOVAL OF EXISTING CONSTRUCTION, EQUIPMENT, PIPING, DUCTS, ETC. SHALL BE PROPERLY PATCHED AND CLOSED OFF TO MAINTAIN PROPER FIRE RATING IN WALLS. PATCH AND PREPARE ANY AREAS TO RECEIVE NEW FINISHES AS REQUIRED.
6. THE ARCHITECT ASSUMES NO RESPONSIBILITY FOR THE DETECTION OR REMOVAL OF ANY HAZARDOUS MATERIALS, INCLUDING, BUT NOT LIMITED TO, ASBESTOS IN ANY FORM. PARTIES RESPONSIBLE FOR DEMOLITION SHALL NOTIFY THE OWNER IMMEDIATELY OF ANY SUSPECTED MATERIALS.
7. THE OWNER HAS THE RIGHT TO CLAIM ANY MATERIALS AND/OR EQUIPMENT THAT ARE SCHEDULED TO BE DEMOLISHED OR REMOVED FROM THE SITE.
8. ALL EXISTING BUILDING ELEMENTS TO REMAIN SHALL BE PROTECTED DURING CONSTRUCTION.
9. PREPARE EXISTING SUBSTRATES TO REMAIN AS REQUIRED TO RECEIVE NEW FINISHES.

DEMOLITION RCP KEY NOTES

1. REMOVE PORTION OF EXISTING ACT CEILING SYSTEM AS REQUIRED FOR INSTALLATION OF NEW MECHANICAL SYSTEM. REPAIR ACT SYSTEM AS REQUIRED FOR NEW CONSTRUCTION. REFER TO MECHANICAL DRAWINGS FOR ADDITIONAL INFORMATION.
2. REMOVE EXISTING LIGHT FIXTURES IN THEIR ENTIRETY. PATCH AND PREPARE ADJACENT SURFACES AS REQUIRED FOR NEW CONSTRUCTION.
3. REMOVE EXISTING PROJECTOR AND ADJACENT METAL PANEL IN THEIR ENTIRETY. SALVAGE FOR RETURN TO THE OWNER. PATCH AND PREPARE ADJACENT SURFACES AS REQUIRED FOR NEW CONSTRUCTION.
4. REMOVE EXISTING WALL MOUNTED PROJECTION SCREEN IN ITS ENTIRETY. SALVAGE FOR RETURN TO THE OWNER. PATCH AND PREPARE ADJACENT SURFACES AS REQUIRED.
5. REMOVE PORTION OF EXISTING GPDW CEILING SYSTEM AS REQUIRED FOR INSTALLATION OF NEW MECHANICAL SYSTEM. REPAIR GPDW CEILING AS REQUIRED FOR NEW CONSTRUCTION. REFER TO MECHANICAL DRAWINGS FOR ADDITIONAL INFORMATION.
6. REMOVE PORTION OF EXISTING ACT CEILING SYSTEM AND ALL ASSOCIATED ELECTRICAL, MECHANICAL, AND PLUMBING DEVICES AS REQUIRED FOR NEW CONSTRUCTION. REPAIR ACT SYSTEM AS REQUIRED FOR NEW CONSTRUCTION.
7. REMOVE EXISTING MECHANICAL, ELECTRICAL, AND LOW VOLTAGE DEVICE(S) AS REQUIRED FOR INSTALLATION OF NEW DUCT WORK AND SALVAGE FOR REINSTALLATION. PATCH AND PREPARE ADJACENT SURFACES AS REQUIRED FOR NEW CONSTRUCTION.

RCP SYMBOL LEGEND

- ACOUSTICAL TILE CEILING (24X48)
- GPDW CEILING
- RECESSED LIGHT FIXTURE
- PHOTOELECTRIC SMOKE DETECTOR
- HVAC SUPPLY DIFFUSER
- HVAC RETURN DIFFUSER
- (S) CEILING MOUNTED SPEAKER

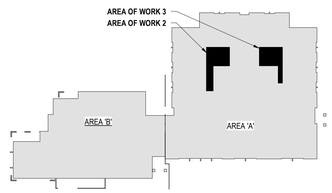

2 Main Level Key Plan
SCALE: 1" = 80'-0"

DAO ARCHITECTURE
7230 Meade St.
Westminster, CO 80030
Phone: 720.273.0431
Email: dan@daoarch.com
Web: www.daoarch.com

Westminster Public Schools

Hodgkins Leadership Academy Classroom Conversion Project

3475 W 67th Ave,
Denver, CO 80221


DAO No.:2021-033

September 25, 2026

Main Level Demolition RCP

AD1.4

Autodesk Docs://WPS 2026 Bond Projects - Hodgkins Classroom Conversion/Hodgkins ES Classroom Conversion (Revit 2026).rvt
9/25/2026 9:14:14 AM

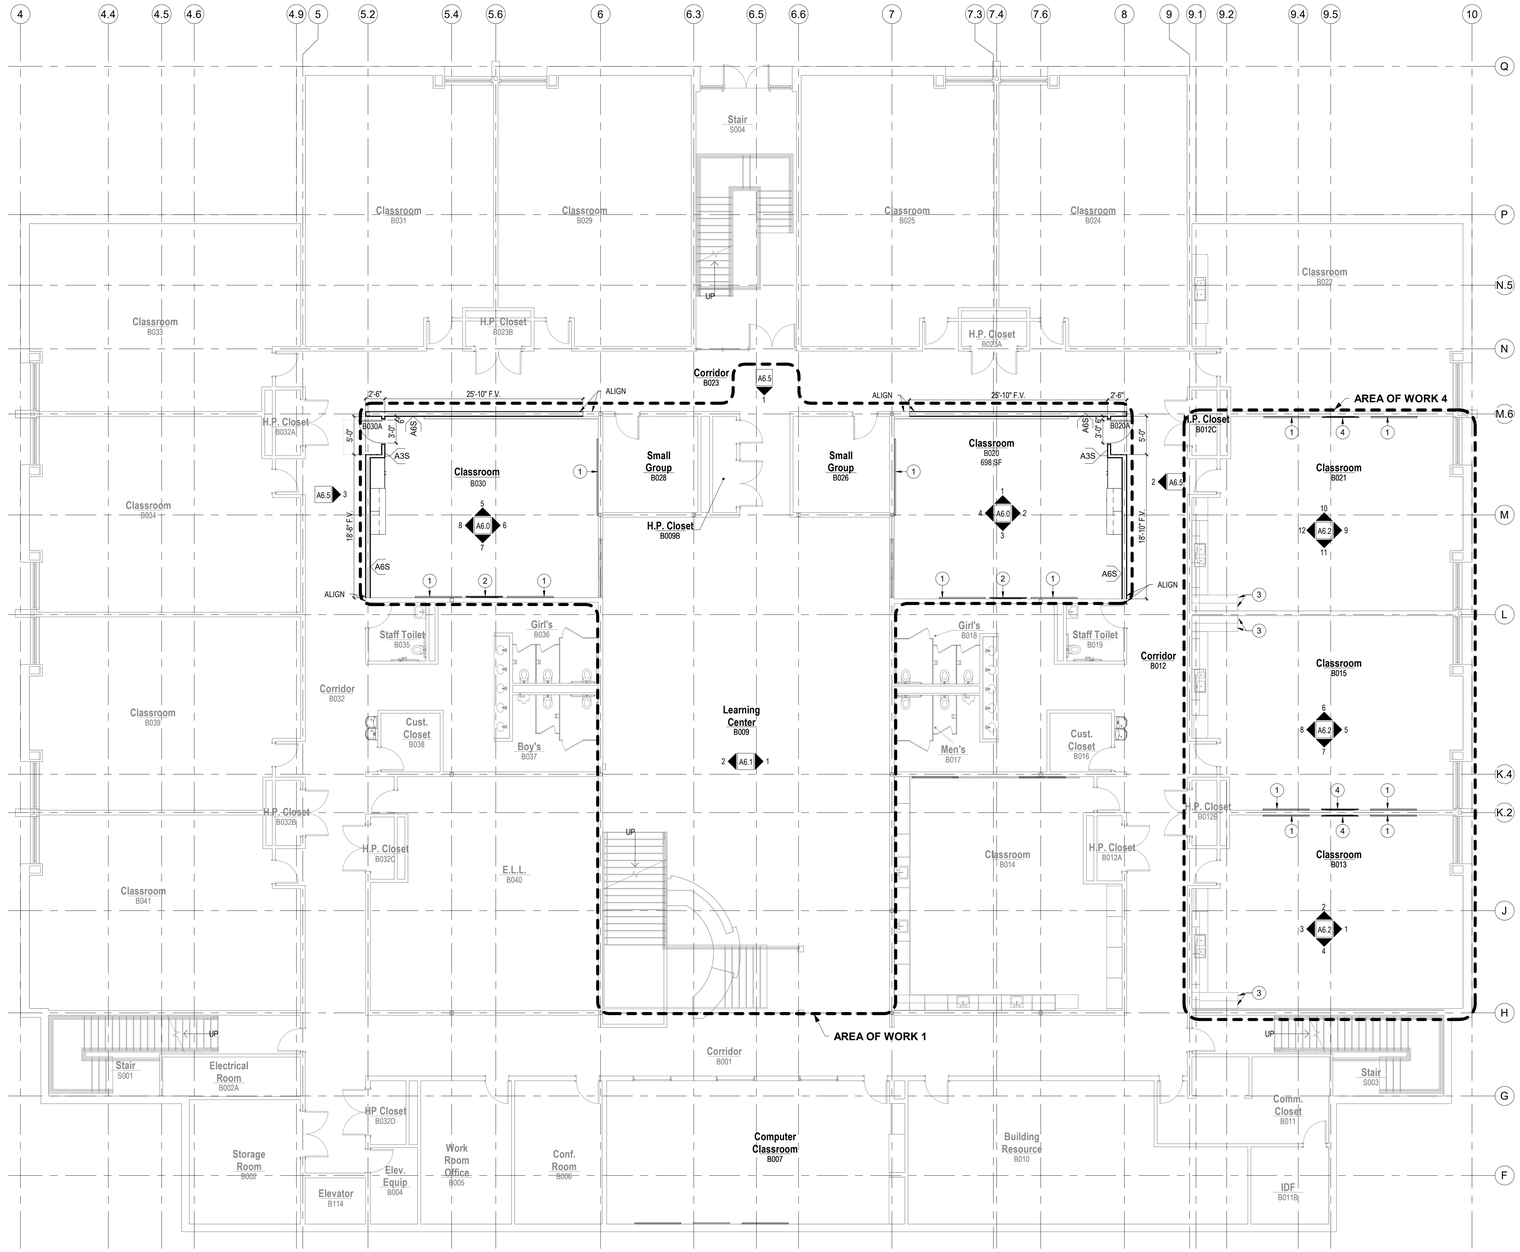

1 Lower Level Plan

SCALE: 1/8" = 1'-0"

GENERAL PLAN NOTES

1. DRAWINGS & SPECIFICATIONS ARE COMPLIMENTARY COMPONENTS OF THE CONTRACT DOCUMENTS. REVIEW ALL DRAWINGS AND SPECIFICATIONS FOR THE COMPLETE SCOPE OF WORK. NOTIFY ARCHITECT IMMEDIATELY FOR CLARIFICATION IF INCONSISTENCIES, CONTRADICTIONS OR OMISSIONS ARE DISCOVERED.
2. DO NOT SCALE DRAWINGS, IF DIMENSIONAL INFORMATION IS REQUIRED & NOT FOUND, NOTIFY ARCHITECT IMMEDIATELY FOR CLARIFICATION.
3. ALL DIMENSIONS ARE TO COLUMN CENTERLINES OR FACE OF FINISHED WALLS OR SURFACES UNLESS NOTED OTHERWISE.
4. REFER TO DEMOLITION DRAWINGS FOR WORK REQUIRED IN ADVANCE OF CONSTRUCTION AND COORDINATE ACCORDINGLY.
5. ALL DOOR FRAMES ARE TO BE INSTALLED 4" AWAY OF ADJACENT PERPENDICULAR WALLS UNLESS NOTED OTHERWISE.
6. REFER TO MECHANICAL AND ELECTRICAL DRAWINGS FOR ADDITIONAL INFORMATION.
7. INTERIOR SIGNAGE TO BE PROVIDED BY OWNER.
8. FURNITURE AND EQUIPMENT PROVIDED BY OWNER.
9. AT ALL LOCATIONS OF NEW DUCT PENETRATIONS THROUGH NEW OR EXISTING WALLS, FINISH THE DRYWALL TIGHT TO THE PERIMETER OF THE DUCTWORK AND SEAL THE JOINT BETWEEN THE DUCTWORK AND THE WALL ASSEMBLY.


KEY NOTES

1. PROVIDE AND INSTALL 4'x6' WALL MOUNTED MARKERBOARDS, CLARIDGE SERIES 4 OR EQUAL.
2. PROVIDE AND INSTALL WALL-MOUNTED MONITOR. COORDINATE MONITOR AND STAND MODEL SELECTION WITH OWNER AND ARCHITECT. INSTALL BACKING IN WALL AS REQUIRED
3. PROVIDE AND INSTALL PLASTIC LAMINATE VENEER TO THE END OF THE EXISTING CASEWORK. MATCH THE EXISTING COLOR AND PATTERN
4. PROVIDE AND INSTALL WALL-MOUNTED MONITOR STAND AND MONITOR. COORDINATE MONITOR AND STAND MODEL SELECTION WITH OWNER AND ARCHITECT. INSTALL BACKING IN WALL AS REQUIRED
5. INSTALL BACKER ROD AND TRAFFIC-RATED SELF-LEVELING POURABLE URETHANE SEALANT WITHIN ROUTED CRACK.

WALL PARTITION TYPES

A3S — 5/8" TYPE 'X' GPDW, 3-5/8" 20 GAUGE METAL STUDS AT 16" O.C. WITH SOUND BATT INSULATION BETWEEN STUDS, 5/8" TYPE 'X' GPDW. FROM FINISHED FLOOR TO GPDW SOFFIT ABOVE.

A6S — 5/8" TYPE 'X' GPDW, 6" 20 GAUGE METAL STUDS AT 16" O.C. WITH SOUND BATT INSULATION BETWEEN STUDS, 5/8" TYPE 'X' GPDW. FROM FINISHED FLOOR TO GPDW SOFFIT ABOVE.

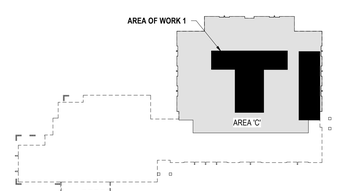

2 Lower Level Key Plan

SCALE: 1" = 80'-0"

DAO ARCHITECTURE
7230 Meade St.
Westminster, CO 80030
Phone: 720.273.0431
Email: dan@daoarch.com
Web: www.daoarch.com

Westminster Public Schools

Hodgkins Leadership Academy Classroom Conversion Project

3475 W 67th Ave,
Denver, CO 80221


DAO No.:2021-033

September 25, 2026


Lower Level Floor Plan

A1.0

Autodesk Docs://WPS 2026 Bond Projects - Hodgkins Classroom Conversion/Hodgkins ES Classroom Conversion (Revit 2026).rvt
9/25/2026 9:14:15 AM

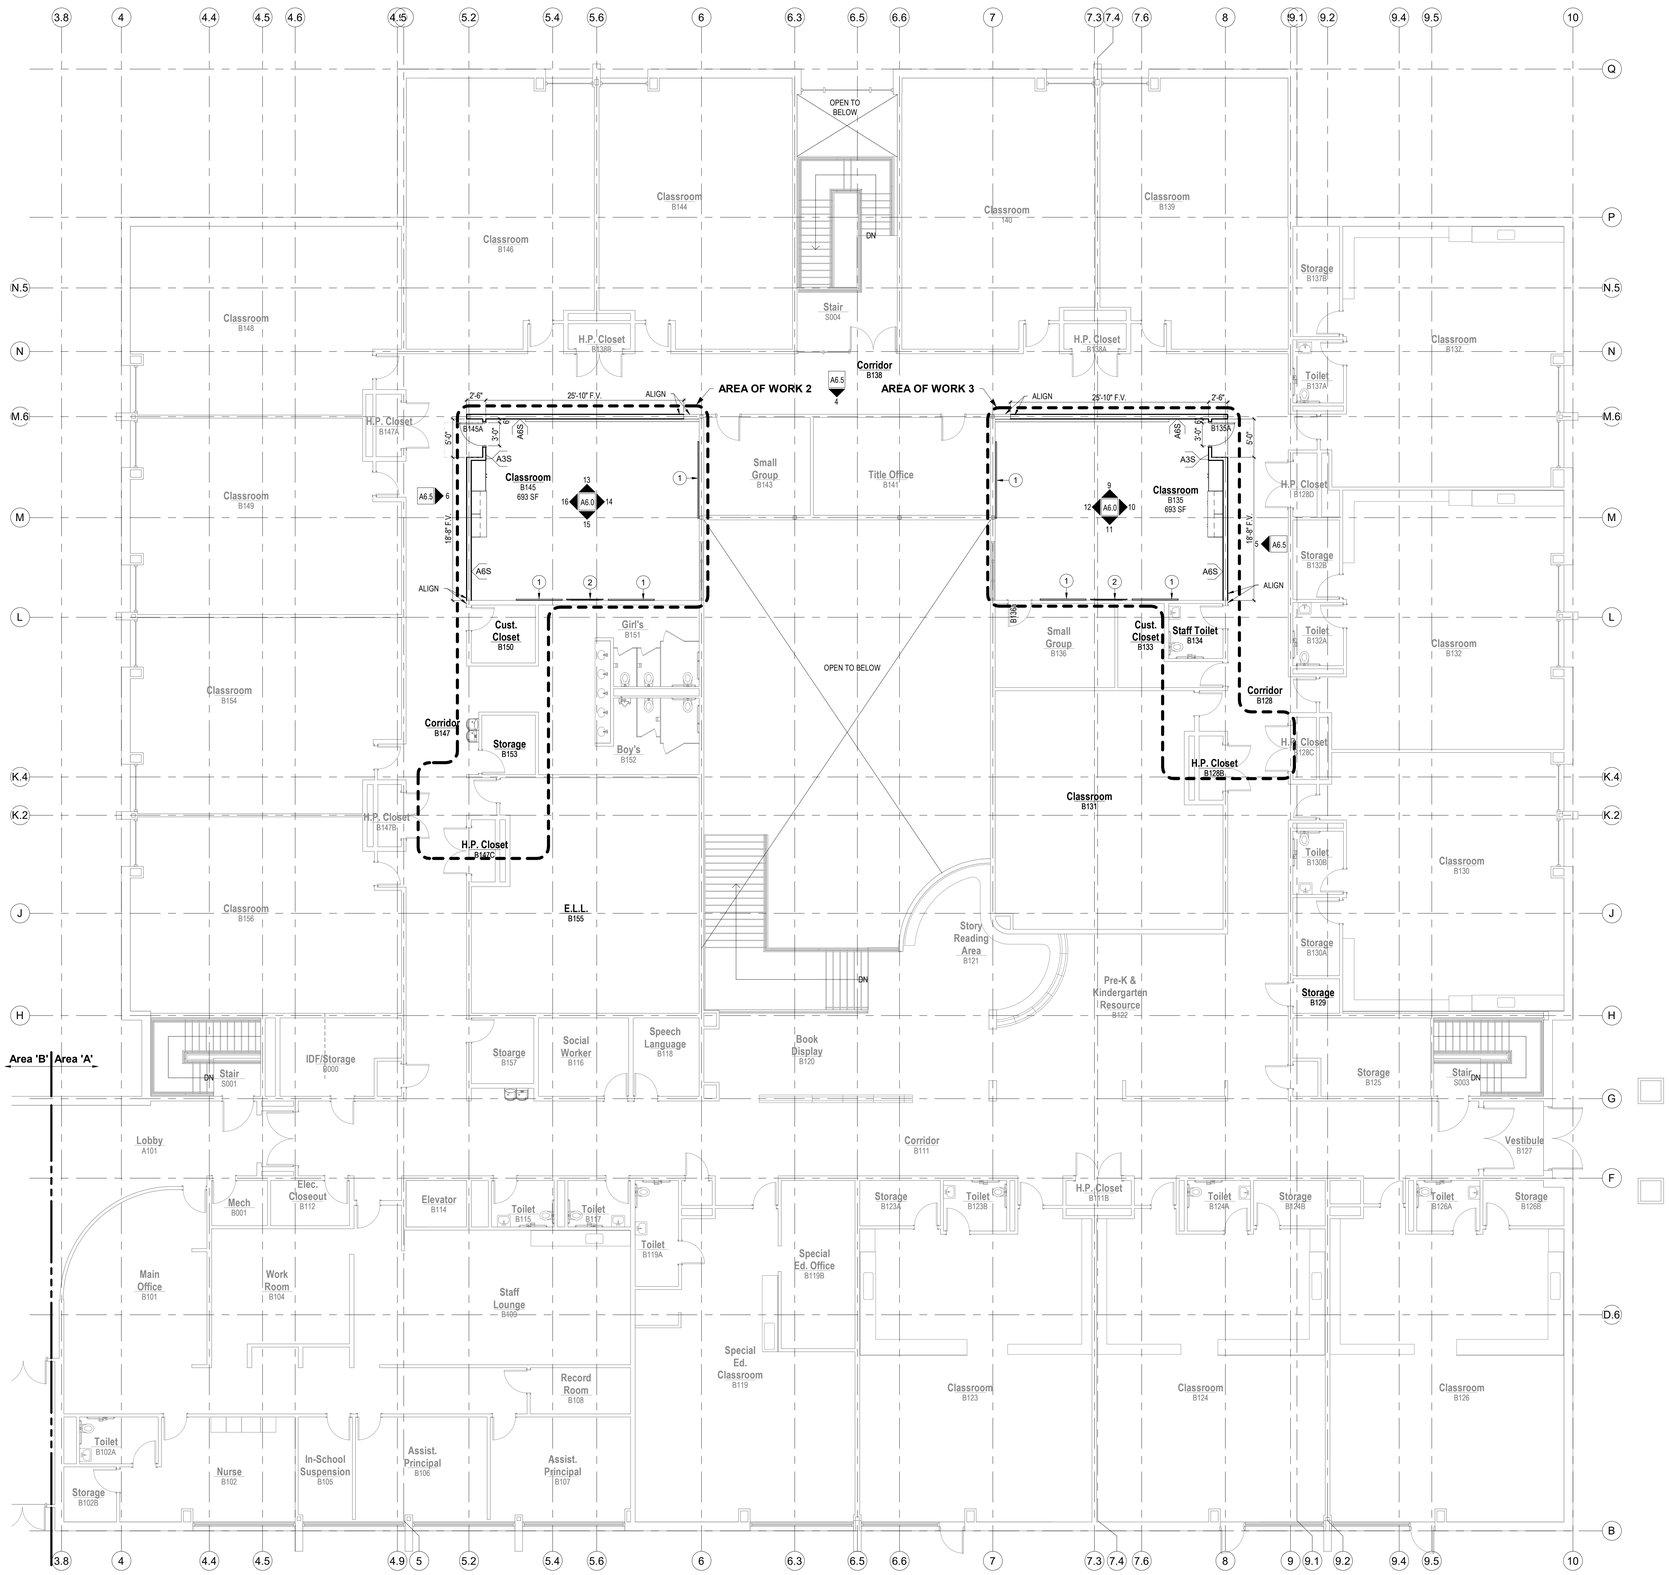

1 Main Level Plan
SCALE: 1/8" = 1'-0"

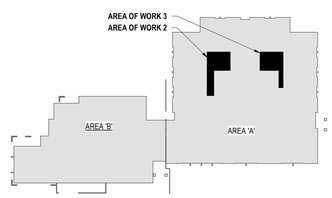

2 Main Level Key Plan
SCALE: 1" = 80'-0"

GENERAL PLAN NOTES

1. DRAWINGS & SPECIFICATIONS ARE COMPLIMENTARY COMPONENTS OF THE CONTRACT DOCUMENTS. REVIEW ALL DRAWINGS AND SPECIFICATIONS FOR THE COMPLETE SCOPE OF WORK. NOTIFY ARCHITECT IMMEDIATELY FOR CLARIFICATION IF INCONSISTENCIES, CONTRADICTIONS OR OMISSIONS ARE DISCOVERED.
2. DO NOT SCALE DRAWINGS, IF DIMENSIONAL INFORMATION IS REQUIRED & NOT FOUND, NOTIFY ARCHITECT IMMEDIATELY FOR CLARIFICATION.
3. ALL DIMENSIONS ARE TO COLUMN CENTERLINES OR FACE OF FINISHED WALLS OR SURFACES UNLESS NOTED OTHERWISE.
4. REFER TO DEMOLITION DRAWINGS FOR WORK REQUIRED IN ADVANCE OF CONSTRUCTION AND COORDINATE ACCORDINGLY.
5. ALL DOOR FRAMES ARE TO BE INSTALLED 4" AWAY OF ADJACENT PERPENDICULAR WALLS UNLESS NOTED OTHERWISE.
6. REFER TO MECHANICAL AND ELECTRICAL DRAWINGS FOR ADDITIONAL INFORMATION.
7. INTERIOR SIGNAGE TO BE PROVIDED BY OWNER.
8. FURNITURE AND EQUIPMENT PROVIDED BY OWNER.
9. AT ALL LOCATIONS OF NEW DUCT PENETRATIONS THROUGH NEW OR EXISTING WALLS, FINISH THE DRYWALL TIGHT TO THE PERIMETER OF THE DUCTWORK AND SEAL THE JOINT BETWEEN THE DUCTWORK AND THE WALL ASSEMBLY.

KEY NOTES

1. PROVIDE AND INSTALL 4'x6' WALL MOUNTED MARKERBOARDS, CLARIDGE SERIES 4 OR EQUAL.
2. PROVIDE AND INSTALL WALL-MOUNTED MONITOR. COORDINATE MONITOR AND STAND MODEL SELECTION WITH OWNER AND ARCHITECT. INSTALL BACKING IN WALL AS REQUIRED
3. PROVIDE AND INSTALL PLASTIC LAMINATE VENEER TO THE END OF THE EXISTING CASEWORK. MATCH THE EXISTING COLOR AND PATTERN
4. PROVIDE AND INSTALL WALL-MOUNTED MONITOR STAND AND MONITOR. COORDINATE MONITOR AND STAND MODEL SELECTION WITH OWNER AND ARCHITECT. INSTALL BACKING IN WALL AS REQUIRED
5. INSTALL BACKER ROD AND TRAFFIC-RATED SELF-LEVELING POURABLE URETHANE SEALANT WITHIN ROUTED CRACK.

WALL PARTITION TYPES

- A3S — 5/8" TYPE 'X' GPDW, 3-5/8" 20 GAUGE METAL STUDS AT 16" O.C. WITH SOUND BATT INSULATION BETWEEN STUDS, 5/8" TYPE 'X' GPDW. FROM FINISHED FLOOR TO GPDW SOFFIT ABOVE.
- A6S — 5/8" TYPE 'X' GPDW, 6" 20 GAUGE METAL STUDS AT 16" O.C. WITH SOUND BATT INSULATION BETWEEN STUDS, 5/8" TYPE 'X' GPDW. FROM FINISHED FLOOR TO GPDW SOFFIT ABOVE.

DAO ARCHITECTURE
7230 Meade St.
Westminster, CO 80030
Phone: 720.273.0431
Email: dan@daoarch.com
Web: www.daoarch.com

Westminster Public Schools

Hodgkins Leadership Academy Classroom Conversion Project

3475 W 67th Ave,
Denver, CO 80221

DAO No.:2021-033

September 25, 2026

Main Level Floor Plan Area 'A'

A1.1

Autodesk Docs://WPS 2026 Bond Projects - Hodgkins Classroom Conversion/Hodgkins ES Classroom Conversion (Revit 2026).rvt
9/25/2026 9:14:16 AM



1 Main Level Demo Plan Area B Copy 1

SCALE: 1/8" = 1'-0"

GENERAL PLAN NOTES

1. DRAWINGS & SPECIFICATIONS ARE COMPLIMENTARY COMPONENTS OF THE CONTRACT DOCUMENTS, REVIEW ALL DRAWINGS AND SPECIFICATIONS FOR THE COMPLETE SCOPE OF WORK. NOTIFY ARCHITECT IMMEDIATELY FOR CLARIFICATION IF INCONSISTENCIES, CONTRADICTIONS OR OMISSIONS ARE DISCOVERED.
2. DO NOT SCALE DRAWINGS, IF DIMENSIONAL INFORMATION IS REQUIRED & NOT FOUND, NOTIFY ARCHITECT IMMEDIATELY FOR CLARIFICATION.
3. ALL DIMENSIONS ARE TO COLUMN CENTERLINES OR FACE OF FINISHED WALLS OR SURFACES UNLESS NOTED OTHERWISE.
4. REFER TO DEMOLITION DRAWINGS FOR WORK REQUIRED IN ADVANCE OF CONSTRUCTION AND COORDINATE ACCORDINGLY.
5. ALL DOOR FRAMES ARE TO BE INSTALLED 4" AWAY OF ADJACENT PERPENDICULAR WALLS UNLESS NOTED OTHERWISE.
6. REFER TO MECHANICAL AND ELECTRICAL DRAWINGS FOR ADDITIONAL INFORMATION.
7. INTERIOR SIGNAGE TO BE PROVIDED BY OWNER.
8. FURNITURE AND EQUIPMENT PROVIDED BY OWNER.
9. AT ALL LOCATIONS OF NEW DUCT PENETRATIONS THROUGH NEW OR EXISTING WALLS, FINISH THE DRYWALL TIGHT TO THE PERIMETER OF THE DUCTWORK AND SEAL THE JOINT BETWEEN THE DUCTWORK AND THE WALL ASSEMBLY.


KEY NOTES

1. PROVIDE AND INSTALL 4'x6' WALL MOUNTED MARKERBOARDS, CLARIDGE SERIES 4 OR EQUAL.
2. PROVIDE AND INSTALL WALL-MOUNTED MONITOR. COORDINATE MONITOR AND STAND MODEL SELECTION WITH OWNER AND ARCHITECT. INSTALL BACKING IN WALL AS REQUIRED
3. PROVIDE AND INSTALL PLASTIC LAMINATE VENEER TO THE END OF THE EXISTING CASEWORK. MATCH THE EXISTING COLOR AND PATTERN
4. PROVIDE AND INSTALL WALL-MOUNTED MONITOR STAND AND MONITOR. COORDINATE MONITOR AND STAND MODEL SELECTION WITH OWNER AND ARCHITECT. INSTALL BACKING IN WALL AS REQUIRED
5. INSTALL BACKER ROD AND TRAFFIC-RATED SELF-LEVELING POURABLE URETHANE SEALANT WITHIN ROUTED CRACK.

WALL PARTITION TYPES

A3S 5/8" TYPE 'X' GPDW, 3-5/8" 20 GAUGE METAL STUDS AT 16" O.C. WITH SOUND BATT INSULATION BETWEEN STUDS, 5/8" TYPE 'X' GPDW. FROM FINISHED FLOOR TO GPDW SOFFIT ABOVE.

A6S 5/8" TYPE 'X' GPDW, 6" 20 GAUGE METAL STUDS AT 16" O.C. WITH SOUND BATT INSULATION BETWEEN STUDS, 5/8" TYPE 'X' GPDW. FROM FINISHED FLOOR TO GPDW SOFFIT ABOVE.

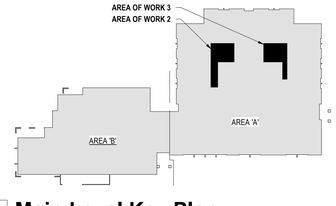

2 Main Level Key Plan

SCALE: 1" = 80'-0"

DAO ARCHITECTURE
7230 Meade St.
Westminster, CO 80030
Phone: 720.273.0431
Email: dan@daoarch.com
Web: www.daoarch.com

Westminster Public Schools

Hodgkins Leadership Academy Classroom Conversion Project

3475 W 67th Ave,
Denver, CO 80221


DAO No.:2021-033

September 25, 2026

Main Level Plan Area 'B'

A1.2

Autodesk Docs://WPS 2026 Bond Projects - Hodgkins Classroom Conversion/Hodgkins ES Classroom Conversion (Revit 2026).rvt
9/25/2026 9:14:17 AM

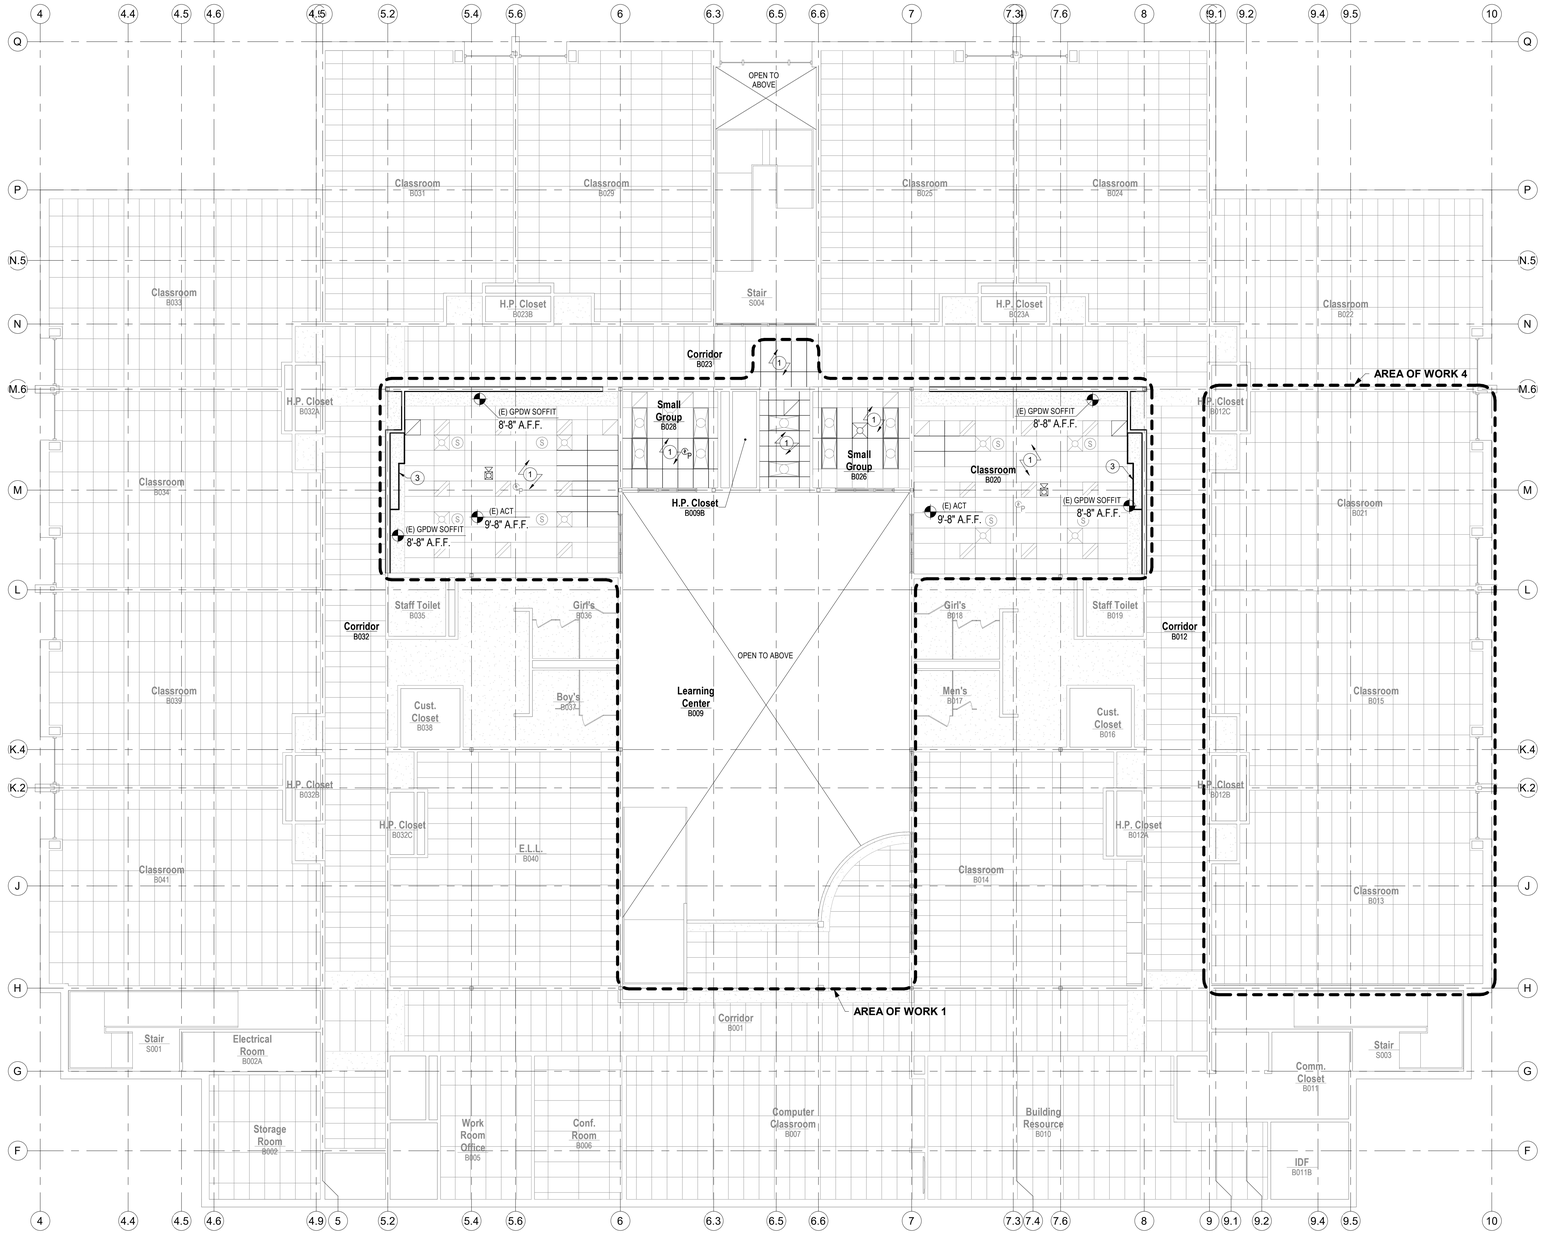

1 Lower Level RCP

SCALE: 1/8" = 1'-0"

RCP GENERAL NOTES:


1. DRAWINGS & SPECIFICATIONS ARE COMPLIMENTARY COMPONENTS OF THE CONTRACT DOCUMENTS. REVIEW ALL DRAWINGS AND SPECIFICATIONS FOR THE COMPLETE SCOPE OF WORK. NOTIFY ARCHITECT IMMEDIATELY FOR CLARIFICATION IF INCONSISTENCIES, CONTRADICTIONS OR OMISSIONS ARE DISCOVERED.
2. DO NOT SCALE DRAWINGS. IF DIMENSIONAL INFORMATION IS REQUIRED & NOT FOUND, NOTIFY ARCHITECT IMMEDIATELY FOR CLARIFICATION.
3. ALL DIMENSIONS ARE TO COLUMN CENTERLINES, CENTER OF SUSPENDED CEILING GRIDS OR FACE OF FINISHED WALLS/SOFFITS UNLESS NOTED OTHERWISE.
4. REFER TO ELECTRICAL DRAWINGS FOR ADDITIONAL LIGHT FIXTURE SPECIFIC INFORMATION.
5. REFER TO MECHANICAL DRAWINGS FOR ADDITIONAL DIFFUSER SPECIFIC INFORMATION.

RCP KEY NOTES

1. REPLACE ACOUSTICAL TILE CEILING SYSTEM DAMAGED BY THE REMOVAL OF EXISTING DEVICES OR WALLS AS REQUIRED. REINSTALL ANY EXISTING DEVICES THAT WERE TEMPORARILY REMOVED AS PART OF THE DEMOLITION.
2. REPLACE GPDW CEILING SYSTEM DAMAGED BY THE REMOVAL OF EXISTING DEVICES OR WALLS AS REQUIRED. REINSTALL ANY EXISTING DEVICES THAT WERE TEMPORARILY REMOVED AS PART OF THE DEMOLITION.
3. MAPLE VENEERED PLYWOOD SOFFIT ABOVE CASEWORK. ALIGN FACE OF SOFFIT WITH FACE OF CASEWORK.
4. REPLACE EXISTING DEVICES THAT WERE REMOVED AS PART OF THE DEMOLITION.

RCP SYMBOL LEGEND

- EXISTING ACOUSTICAL TILE CEILING (24X48)
- NEW ACOUSTICAL TILE CEILING (24X48)
- EXISTING GPDW CEILING
- NEW GPDW CEILING
- EXISTING/REINSTALLED RECESSED LIGHT FIXTURE
- NEW RECESSED LIGHT FIXTURE
- EXISTING/REINSTALLED PHOTOELECTRIC SMOKE DETECTOR
- EXISTING/REINSTALLED HVAC SUPPLY DIFFUSER
- EXISTING/REINSTALLED HVAC RETURN DIFFUSER
- EXISTING/REINSTALLEDCEILING MOUNTED SPEAKER
- NEW FIRE ALARM HORN/STROBE COMBINATION

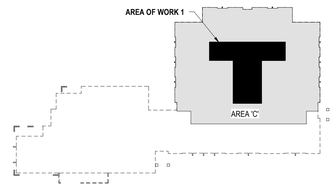

2 Lower Level Key Plan

SCALE: 1" = 80'-0"

DAO ARCHITECTURE
7230 Meade St.
Westminster, CO 80030
Phone: 720.273.0431
Email: dan@daoarch.com
Web: www.daoarch.com

Westminster Public Schools

Hodgkins Leadership Academy Classroom Conversion Project

3475 W 67th Ave,
Denver, CO 80221


DAO No.:2021-033

September 25, 2026

Lower Level RCP


A1.3

Autodesk Docs://WPS 2026 Bond Projects - Hodgkins Classroom Conversion/Hodgkins ES Classroom Conversion (Revit 2026).rvt
9/25/2026 9:14:18 AM

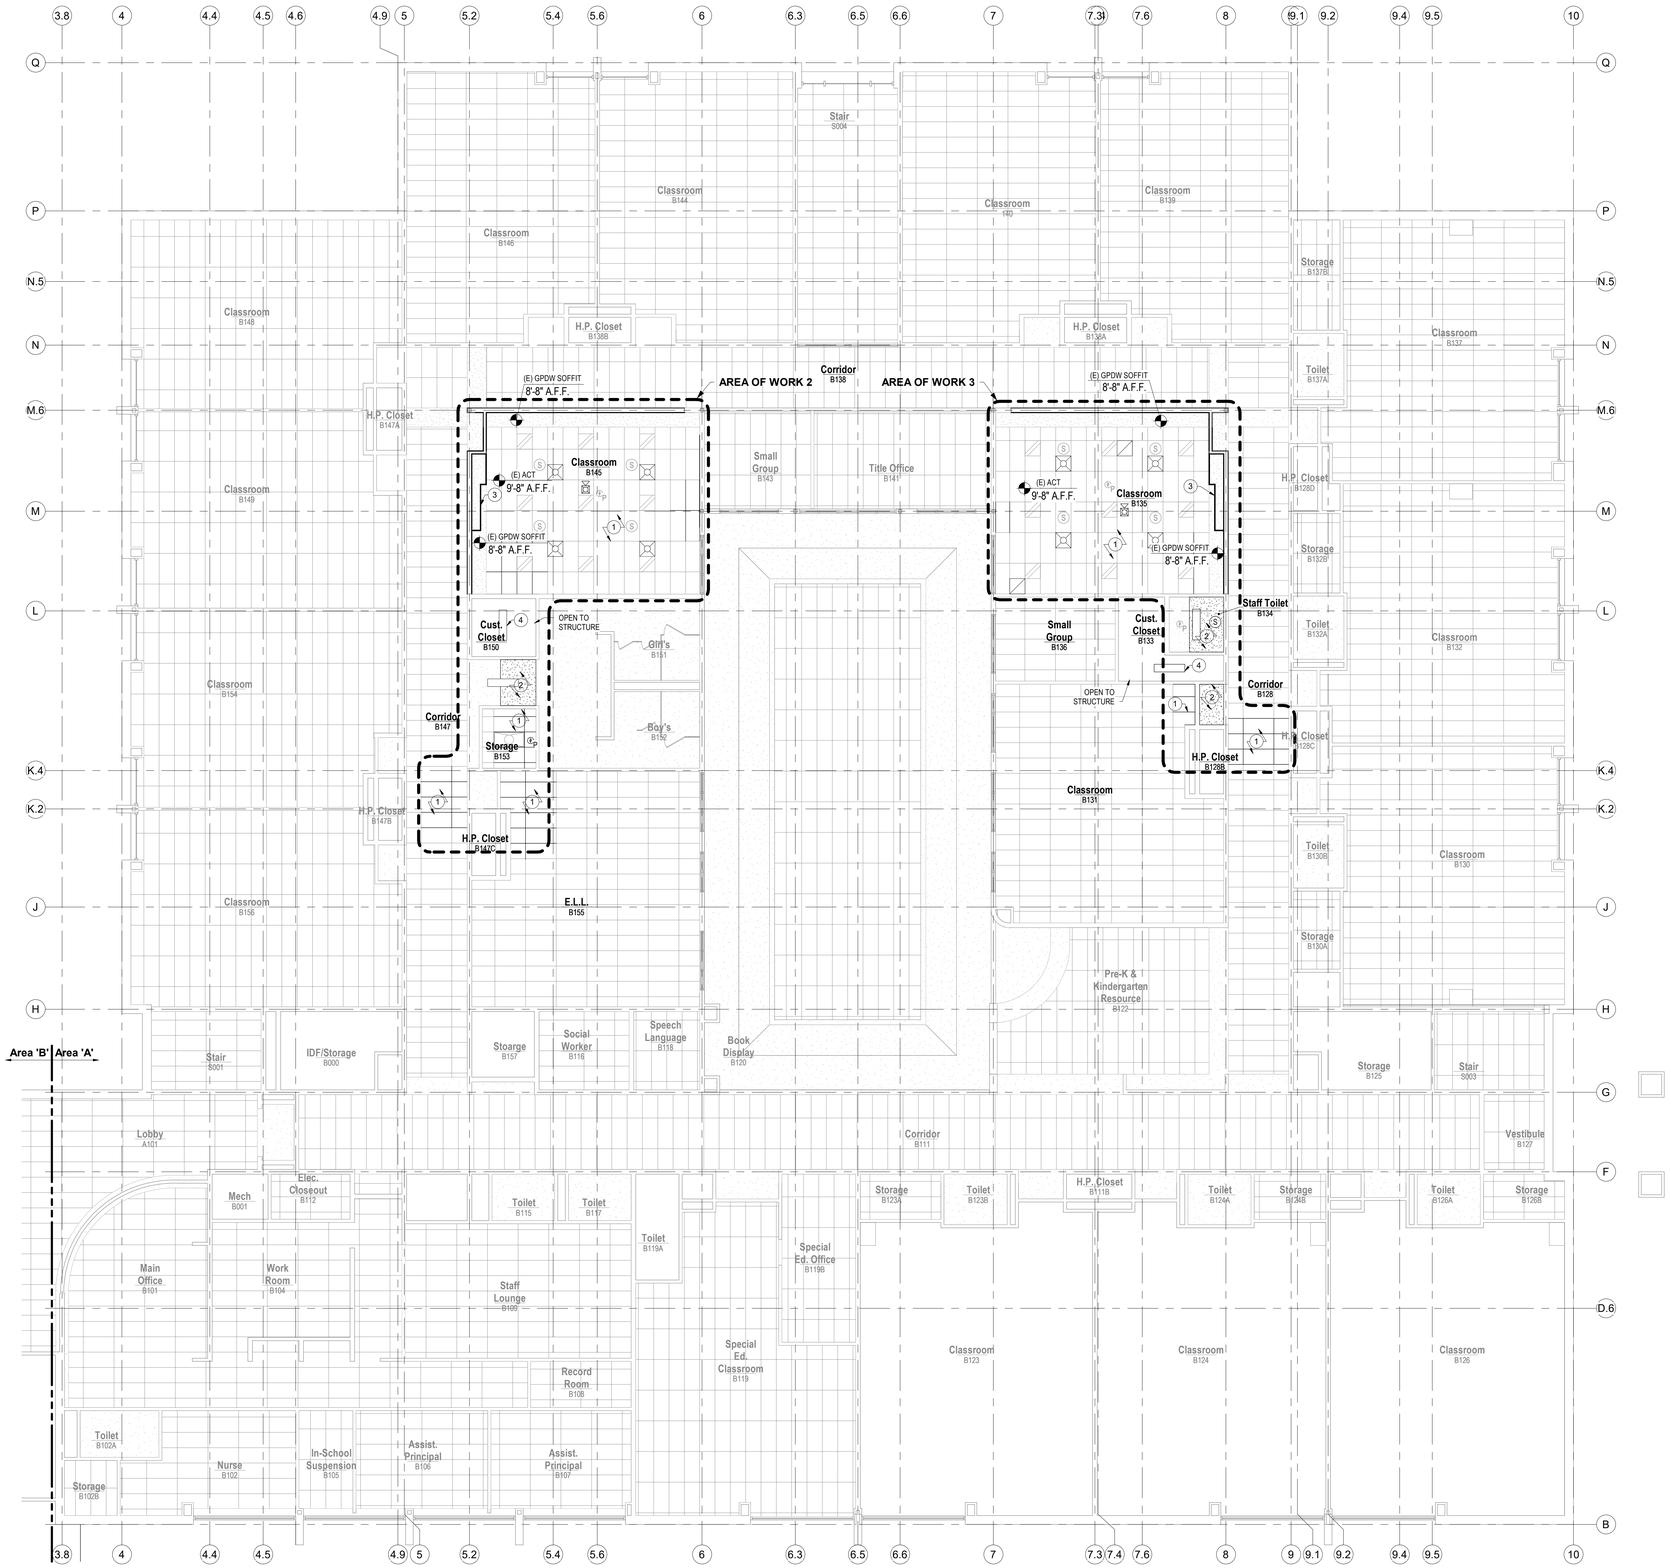

1 Main Level RCP

SCALE: 1/8" = 1'-0"

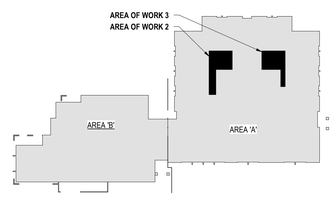

2 Main Level Key Plan

SCALE: 1" = 80'-0"

RCP GENERAL NOTES:

1. DRAWINGS & SPECIFICATIONS ARE COMPLIMENTARY COMPONENTS OF THE CONTRACT DOCUMENTS. REVIEW ALL DRAWINGS AND SPECIFICATIONS FOR THE COMPLETE SCOPE OF WORK. NOTIFY ARCHITECT IMMEDIATELY FOR CLARIFICATION IF INCONSISTENCIES, CONTRADICTIONS OR OMISSIONS ARE DISCOVERED.
2. DO NOT SCALE DRAWINGS, IF DIMENSIONAL INFORMATION IS REQUIRED & NOT FOUND, NOTIFY ARCHITECT IMMEDIATELY FOR CLARIFICATION.
3. ALL DIMENSIONS ARE TO COLUMN CENTERLINES, CENTER OF SUSPENDED CEILING GRIDS OR FACE OF FINISHED WALLS/SOFFITS UNLESS NOTED OTHERWISE.
4. REFER TO ELECTRICAL DRAWINGS FOR ADDITIONAL LIGHT FIXTURE SPECIFIC INFORMATION.
5. REFER TO MECHANICAL DRAWINGS FOR ADDITIONAL DIFFUSER SPECIFIC INFORMATION.

RCP KEY NOTES

1. REPLACE ACOUSTICAL TILE CEILING SYSTEM DAMAGED BY THE REMOVAL OF EXISTING DEVICES OR WALLS AS REQUIRED. REINSTALL ANY EXISTING DEVICES THAT WERE TEMPORARILY REMOVED AS PART OF THE DEMOLITION.
2. REPLACE GPDW CEILING SYSTEM DAMAGED BY THE REMOVAL OF EXISTING DEVICES OR WALLS AS REQUIRED. REINSTALL ANY EXISTING DEVICES THAT WERE TEMPORARILY REMOVED AS PART OF THE DEMOLITION.
3. MAPLE VENEERED PLYWOOD SOFFIT ABOVE CASEWORK. ALIGN FACE OF SOFFIT WITH FACE OF CASEWORK.
4. REPLACE EXISTING DEVICES THAT WERE REMOVED AS PART OF THE DEMOLITION.

RCP SYMBOL LEGEND

- EXISTING ACOUSTICAL TILE CEILING (24X48)
- NEW ACOUSTICAL TILE CEILING (24X48)
- EXISTING GPDW CEILING
- NEW GPDW CEILING
- EXISTING/REINSTALLED RECESSED LIGHT FIXTURE
- NEW RECESSED LIGHT FIXTURE
- EXISTING/REINSTALLED PHOTOELECTRIC SMOKE DETECTOR
- EXISTING/REINSTALLED HVAC SUPPLY DIFFUSER
- EXISTING/REINSTALLED HVAC RETURN DIFFUSER
- EXISTING/REINSTALLEDCEILING MOUNTED SPEAKER
- NEW FIRE ALARM HORN/STROBE COMBINATION

DAO ARCHITECTURE

7230 Meade St.
Westminster, CO 80030

Phone: 720.273.0431
Email: dan@daoarch.com
Web: www.daoarch.com

Westminster Public Schools

Hodgkins Leadership Academy Classroom Conversion Project

3475 W 67th Ave,
Denver, CO 80221


DAO No.:2021-033

September 25, 2026

Main Level RCP


A1.4

Autodesk Docs://WPS 2026 Bond Projects - Hodgkins Classroom Conversion/Hodgkins ES Classroom Conversion (Revit 2026).rvt
9/25/2026 9:14:19 AM

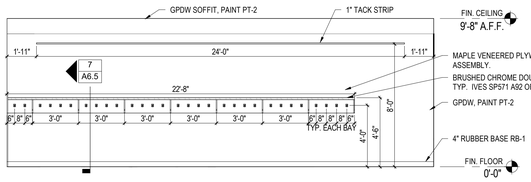


1 Classroom B020 - North

1 | A1.0 SCALE: 1/4" = 1'-0"

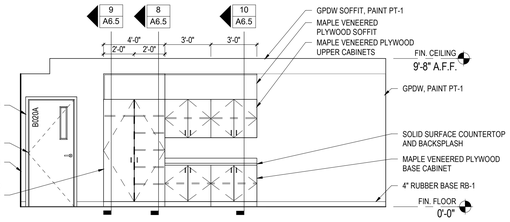


2 Classroom B020 - East

1 | A1.0 SCALE: 1/4" = 1'-0"

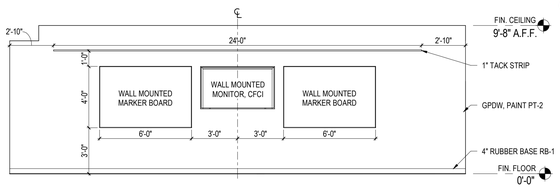


3 Classroom B020 - South

1 | A1.0 SCALE: 1/4" = 1'-0"

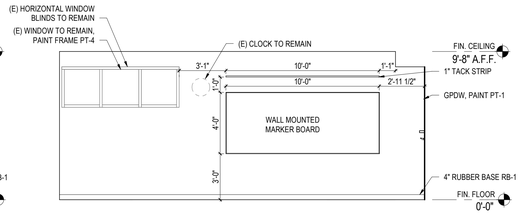


4 Classroom B020 - West

1 | A1.0 SCALE: 1/4" = 1'-0"

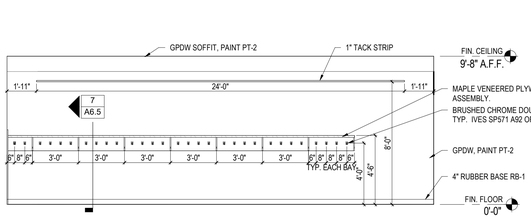


5 Classroom B030 - North

1 | A1.0 SCALE: 1/4" = 1'-0"

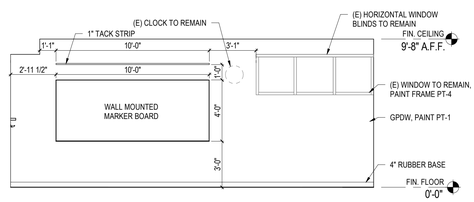


6 Classroom B030 - East

1 | A1.0 SCALE: 1/4" = 1'-0"

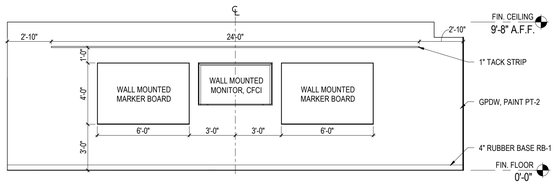

7 Classroom B030 - South

1 | A1.0 SCALE: 1/4" = 1'-0"

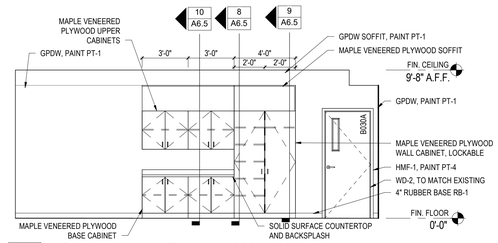


8 Classroom B030 - West

1 | A1.0 SCALE: 1/4" = 1'-0"


9 Classroom B135 - North

1 | A1.1 SCALE: 1/4" = 1'-0"

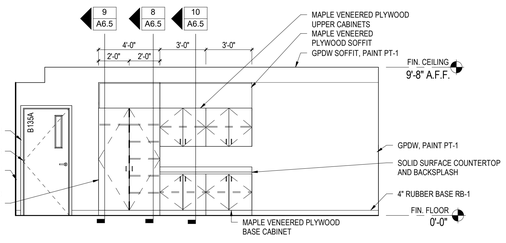


10 Classroom B135 - East

1 | A1.1 SCALE: 1/4" = 1'-0"

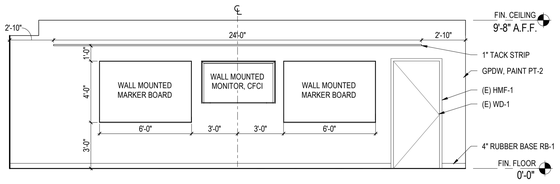


11 Classroom B135 - South

1 | A1.1 SCALE: 1/4" = 1'-0"

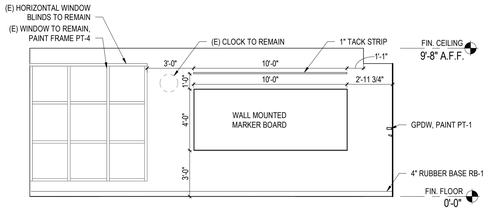


12 Classroom B135 - West

1 | A1.1 SCALE: 1/4" = 1'-0"

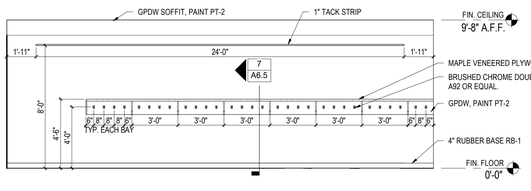


13 Classroom B145 - North

1 | A1.1 SCALE: 1/4" = 1'-0"

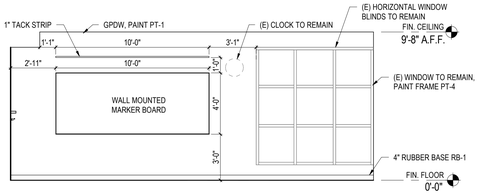


14 Classroom B145 - East

1 | A1.1 SCALE: 1/4" = 1'-0"

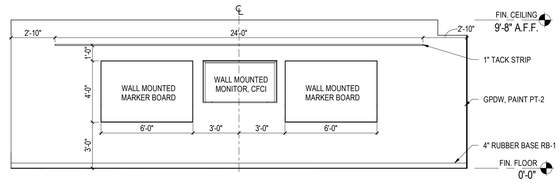

15 Classroom B145 - South

1 | A1.1 SCALE: 1/4" = 1'-0"

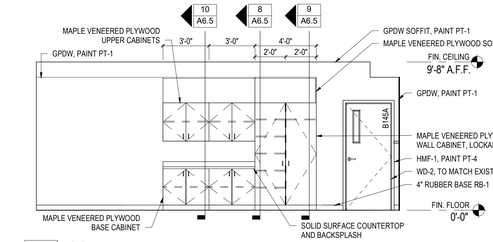

16 Classroom B145 - West

1 | A1.1 SCALE: 1/4" = 1'-0"

DAO ARCHITECTURE

7230 Meade St.
Westminster, CO 80030

Phone: 720.273.0431
Email: dan@daoarch.com
Web: www.daoarch.com

Westminster Public Schools

Hodgkins Leadership Academy Classroom Conversion Project

3475 W 67th Ave,
Denver, CO 80221


DAO No.:2021-033

September 25, 2026

Interior Elevations

A6.0


Autodesk Docs://WPS 2026 Bond Projects - Hodgkins Classroom Conversion/Hodgkins ES Classroom Conversion (Revit 2026).rvt
9/25/2026 9:14:20 AM

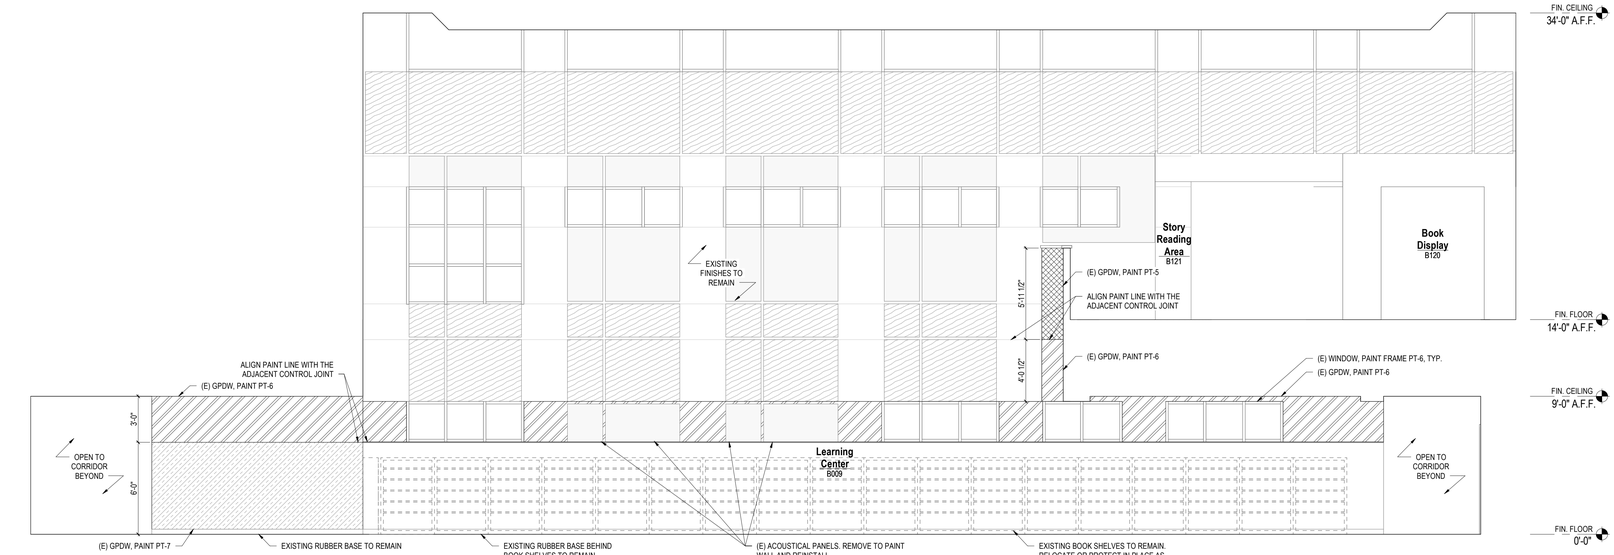

1 Learning Center B009 - East

SCALE: 1/4" = 1'-0"

1 | A1.0

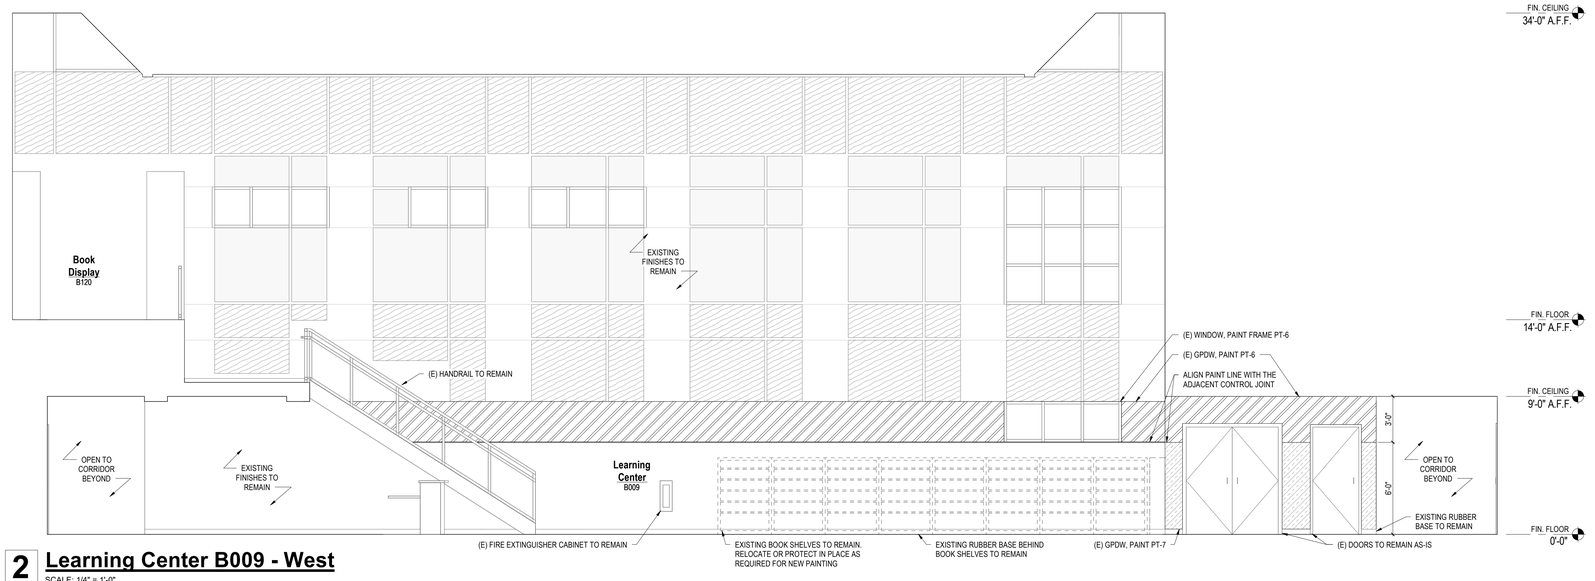

2 Learning Center B009 - West

SCALE: 1/4" = 1'-0"

1 | A1.0

DAO ARCHITECTURE

7230 Meade St.
Westminster, CO 80030

Phone: 720.273.0431
Email: dan@daoarch.com
Web: www.daoarch.com

Westminster Public Schools

Hodgkins Leadership Academy Classroom Conversion Project

3475 W 67th Ave,
Denver, CO 80221

DAO No.:2021-033

September 25, 2026


Interior Elevations

A6.1


Autodesk Docs://WPS 2026 Bond Projects - Hodgkins Classroom Conversion/Hodgkins ES Classroom Conversion (Revit 2026).rvt
9/25/2026 9:14:21 AM




1 B013 - EAST
SCALE: 1/4" = 1'-0"
1 A1.0

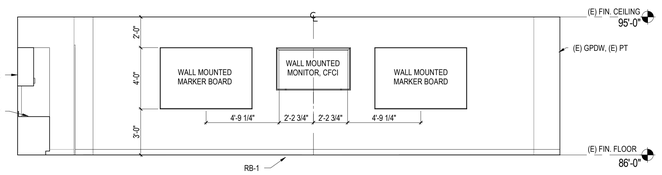


2 B013 - NORTH
SCALE: 1/4" = 1'-0"
1 A1.0

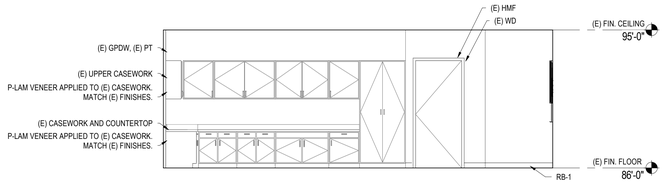


3 B013 - WEST
SCALE: 1/4" = 1'-0"
1 A1.0

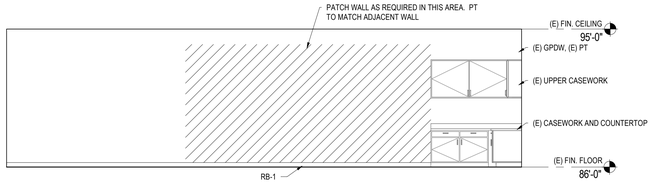


4 B013 - SOUTH
SCALE: 1/4" = 1'-0"
1 A1.0

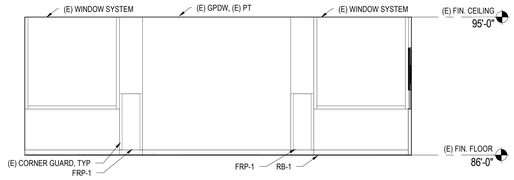


5 B015 - EAST
SCALE: 1/4" = 1'-0"
1 A1.0

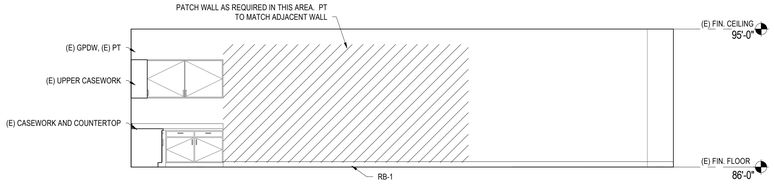


6 B015 - NORTH
SCALE: 1/4" = 1'-0"
1 A1.0

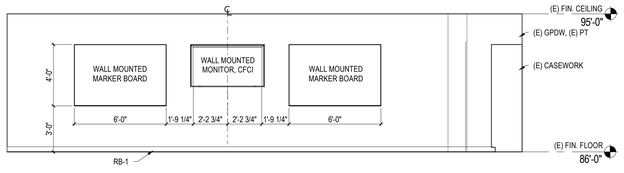


7 B015 - SOUTH
SCALE: 1/4" = 1'-0"
1 A1.0

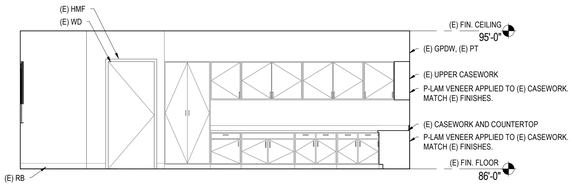


8 B015 - WEST
SCALE: 1/4" = 1'-0"
1 A1.0

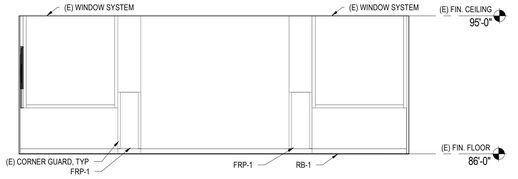


9 B021 - EAST
SCALE: 1/4" = 1'-0"
1 A1.0

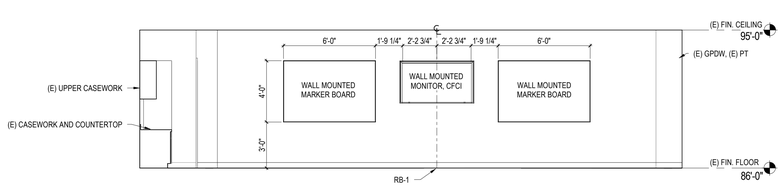

10 B021 - NORTH
SCALE: 1/4" = 1'-0"
1 A1.0

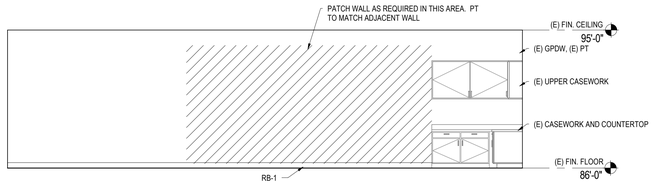

11 B021 - SOUTH
SCALE: 1/4" = 1'-0"
1 A1.0

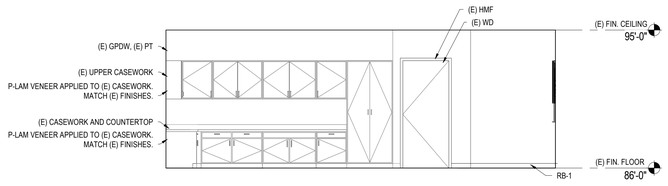

12 B021 - WEST
SCALE: 1/4" = 1'-0"
1 A1.0

DAO ARCHITECTURE
7230 Meade St.
Westminster, CO 80030
Phone: 720.273.0431
Email: dan@daoarch.com
Web: www.daoarch.com

Westminster Public Schools

Hodgkins Leadership Academy Classroom Conversion Project

3475 W 67th Ave,
Denver, CO 80221


DAO No.:2021-033

September 25, 2026

Interior Elevations

A6.2


Autodesk Docs://WPS 2026 Bond Projects - Hodgkins Classroom Conversion/Hodgkins ES Classroom Conversion (Revit 2026).rvt
9/25/2026 9:14:22 AM

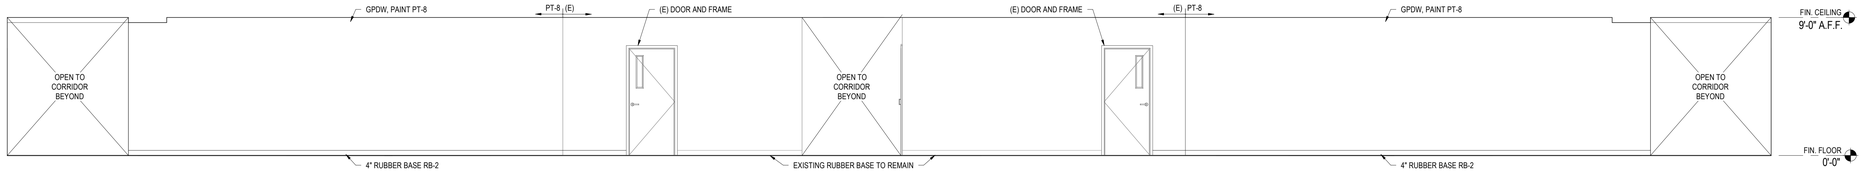

1 Corridor B023 - South

1 | A1.0


SCALE: 1/4" = 1'-0"

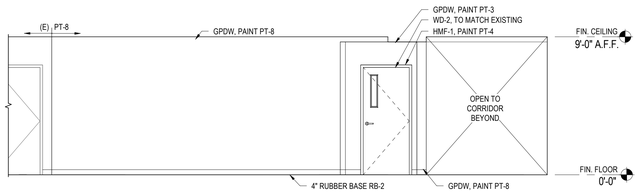

2 Corridor B012 - West

1 | A1.0


SCALE: 1/4" = 1'-0"

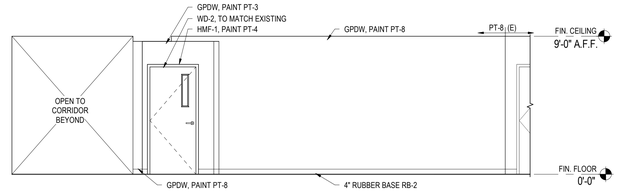

3 Corridor B032 - East

1 | A1.0


SCALE: 1/4" = 1'-0"

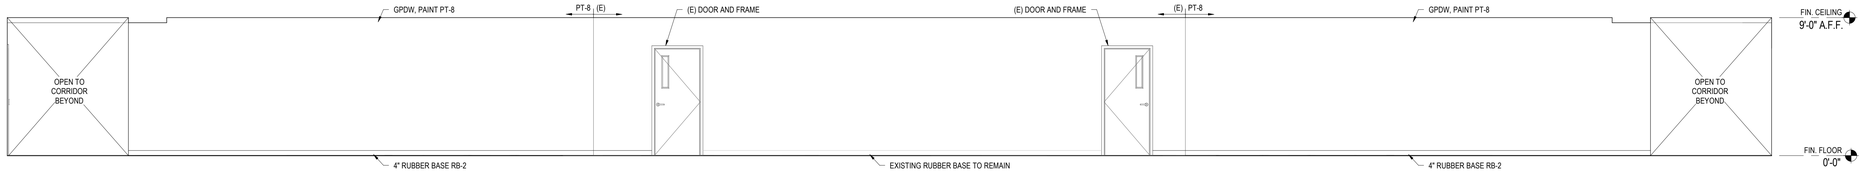

4 Corridor B138 - South

1 | A1.1


SCALE: 1/4" = 1'-0"

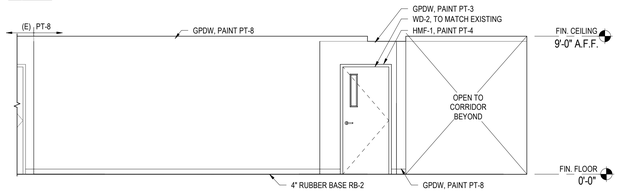

5 Corridor B128 - West

1 | A1.1


SCALE: 1/4" = 1'-0"

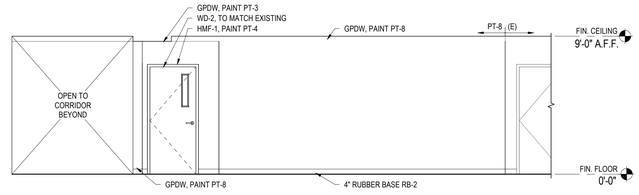

6 Corridor B147 - East

1 | A1.1


SCALE: 1/4" = 1'-0"

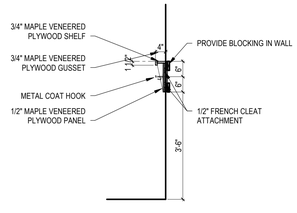

7 Backpack Storage Section

1 | A6.0


SCALE: 1/2" = 1'-0"

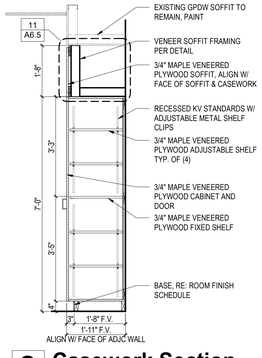

8 Casework Section

2 | A6.0


SCALE: 1/2" = 1'-0"

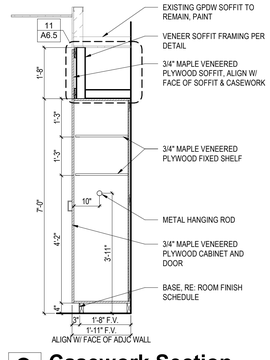

9 Casework Section

2 | A6.0


SCALE: 1/2" = 1'-0"

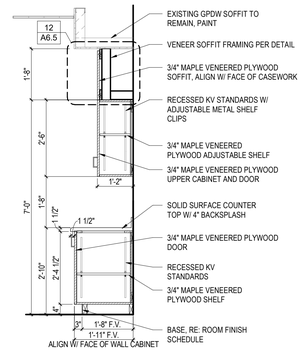

10 Casework Section

2 | A6.0

SCALE: 1/2" = 1'-0"

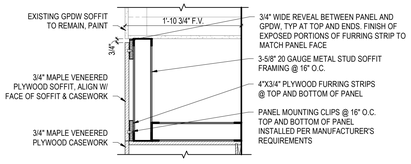


11 Veneer Soffit Detail

8 | A6.5

SCALE: 1" = 1'-0"

CASEWORK GENERAL NOTES


1. ALL CASEWORK SHALL BE CONSTRUCTED TO MEET THE FOLLOWING AWI CONSTRUCTION GRADES:
   WOOD VENEERED PLYWOOD CASEWORK
   -GRADE = CUSTOM
   -SOLID SURFACE COUNTERTOPS AND BACKSPLASH
2. TYPICAL MATERIALS:
   -HEAVY DUTY DRAWER SLIDES
   -FIVE KNUCKLE HINGES
   -WIRE PULLS
   -METAL SHELF CLIPS ON RECESSED K.V. STANDARDS
3. SEE SHEET A9.0 FOR FINISHES.
4. RECESS ALL KV STANDARDS PER DETAIL 13 ON SHEET A6.3 (THIS SHEET).
5. FACE OF WALL CABINETS (DETAILS 8 & 9, THIS SHEET) AND BASE CABINETS (DETAIL 10, THIS SHEET) TO ALIGN WITH FACE OF ADJACENT WALL.

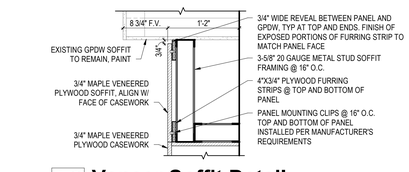

12 Veneer Soffit Detail


10 | A6.5

SCALE: 1" = 1'-0"

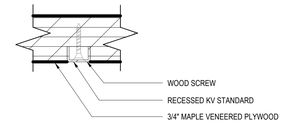

13 Typ. Recessed KV Standard


SCALE: 12" = 1'-0"

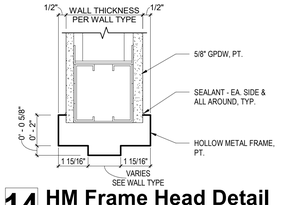

14 HM Frame Head Detail

16 | A6.5


SCALE: 3" = 1'-0"

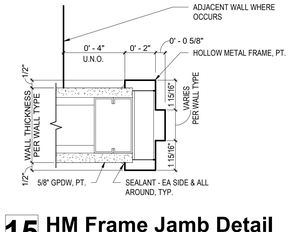

15 HM Frame Jamb Detail


16 | A6.5

SCALE: 3" = 1'-0"

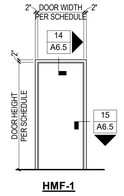


HMF-1

HM FRAME

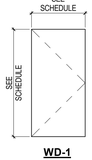

WD-1

FLUSH WOOD DOOR

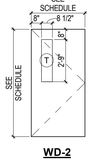

WD-2

FLUSH WOOD DOOR W/ LITE TO MATCH EXISTING CONDITIONS

16 Door and Frame Types

SCALE: 1/4" = 1'-0"

(T) INDICATES TEMPERED GLAZING AT THESE LOCATIONS

DOOR AND FRAME SCHEDULE

IDENTIFICATION			DOOR						
			DIMENSIONS						
DOOR NO.	ROOM NO.	ROOM NAME	WIDTH WI	H	TYPE	FRAME TYPE	DOOR/FRAME FIRE RATING	HARDWARE	REMARKS
B020A	B020	Classroom	3' - 0"	7' - 0"	WD-2	HMF-1	N/A	01	Mag Hold, Narrow Lite, Door Finish to Match Existing, Paint Frame
B030A	B030	Classroom	3' - 0"	7' - 0"	WD-2	HMF-1	N/A	01	Mag Hold, Narrow Lite, Door Finish to Match Existing, Paint Frame
B135A	B135	Classroom	3' - 0"	7' - 0"	WD-2	HMF-1	N/A	01	Mag Hold, Narrow Lite, Door Finish to Match Existing, Paint Frame
B136a	B136	Small Group	3' - 0"	7' - 0"	WD-1 (E)	HMF-1 (E)	N/A	EX-01	Existing Door, Frame, and Hardware to Remain
B136d	A109	Mech	3' - 0"	7' - 0"	WD-1	HM-1			
B136e	A111	Kitchen	3' - 0"	7' - 0"	WD-1	HM-1			
B136f	B128	Corridor	3' - 0"	7' - 0"	WD-1	HM-1			
B145A	B145	Classroom	3' - 0"	7' - 0"	WD-2	HMF-1	N/A	01	Mag Hold, Narrow Lite, Door Finish to Match Existing, Paint Frame

NOTE:
(E) = EXISTING DOOR AND FRAME
1. NEW WOOD DOORS TO MATCH EXISTING CONDITIONS.
2. GENERAL CONTRACTOR TO VERIFY EXISTING DOORS AND/OR FRAMES AND COORDINATE REQUIRED PREPARATION.
3. DOOR LITE KITS TO BE ANEMOSTAT LO-PRO LITE KITS.

DAO ARCHITECTURE
7230 Meade St.
Westminster, CO 80030
Phone: 720.273.0431
Email: dan@daoarch.com
Web: www.daoarch.com

Westminster Public Schools

Hodgkins Leadership Academy Classroom Conversion Project

3475 W 67th Ave,
Denver, CO 80221

DAO No.:2021-033

September 25, 2026

Corridor Elevations & Casework Sections & Door Details

A6.5

Autodesk Docs://WPS 2026 Bond Projects - Hodgkins Classroom Conversion/Hodgkins ES Classroom Conversion (Revit 2026).rvt
9/25/2026 9:14:24 AM



2 Lower Level Finish Plan

SCALE: 1/8" = 1'-0"

ROOM FINISH SCHEDULE

IDENTIFICATION		FLOOR			WALLS								CEILING	
					NORTH		EAST		SOUTH		WEST			
NO.	NAME	MATERIAL	FINISH	BASE	MATERIAL	FINISH	MATERIAL	FINISH	MATERIAL	FINISH	MATERIAL	FINISH	MATERIAL	REMARKS
103B	PE Office	(E) CONC.	LVT-1	RB-1	(E) GPDW	(E)	(E) GPDW	(E)	(E) GPDW	(E)	(E) GPDW	(E)	(E) ACT	
A102	Corridor	(E) CONC.	LVT-1, LVT-2	RB-1	(E) GPDW	(E)	(E) GPDW	(E)	(E) GPDW	-	(E) GPDW	(E)	(E) ACT	
A102B	Kitchenette	(E) CONC.	LVT-1	RB-1	(E) GPDW	(E)	(E) GPDW	(E)	-	-	(E) GPDW	(E)	(E) ACT	
A105A	General Music Storage	(E) CONC.	LVT-1	RB-1	(E) GPDW	(E)	(E) GPDW	(E)	(E) GPDW	(E)	(E) GPDW	(E)	(E) ACT	
A110	B&A School Care	(E) CONC.	LVT-1	RB-1	(E) GPDW	(E)	(E) GPDW	(E)	(E) GPDW	(E)	(E) GPDW	(E)	(E) ACT	
A112	Multi-Purpose Room	(E) CONC.	LVT-1, LVT-2	RB-1	(E) GPDW	(E)	(E) GPDW	(E)	(E) GPDW	(E)	(E) GPDW	(E)	(E) ACT	
A112A	Multipurpose Room Storage	(E) CONC.	LVT-1	RB-1	(E) GPDW	(E)	(E) GPDW	(E)	(E) GPDW	(E)	(E) GPDW	(E)	(E) ACT	
A130	Storage	(E) CONC.	LVT-1	RB-1	(E) GPDW	(E)	(E) GPDW	(E)	(E) GPDW	(E)	(E) GPDW	(E)	(E) ACT	
B008	Classroom	(E) CONC.	CPT-1	RB-1	GPDW	PT-2	(E) GPDW	PT-1	(E) GPDW	PT-2	GPDW	PT-1	(E) ACT	Paint (E) Soffit to Match the Wall Below
B009	Learning Center	(E) CONC.	(E)	RB-2	(E) GPDW	PT-6	(E) GPDW	PT-6	(E) GPDW	PT-5 & PT-6	(E) GPDW	PT-6	(E)	Refer to Sheets A6.1 & A6.2 for Paint Layout
B012	Corridor	(E) CONC.	(E)	RB-2	(E) GPDW	(E)	(E) GPDW	(E)	(E) GPDW	(E)	GPDW	PT-8	(E) ACT	Paint Classroom Alcove Walls and Ceiling PT-3
B013	Classroom	(E) CONC.	CPT-1	RB-1	(E) GPDW	(E)	(E) GPDW	(E)	(E) GPDW	(E)	(E) GPDW	(E)	(E) ACT	
B015	Classroom	(E) CONC.	CPT-1	RB-1	(E) GPDW	(E)	(E) GPDW	(E)	(E) GPDW	(E)	(E) GPDW	(E)	(E) ACT	
B020	Classroom	(E) CONC.	CPT-1	RB-1	GPDW	PT-2	GPDW	PT-1	(E) GPDW	PT-2	(E) GPDW	PT-1	(E) ACT	Paint (E) Soffit to Match the Wall Below
B021	Classroom	(E) CONC.	CPT-1	RB-1	(E) GPDW	(E)	(E) GPDW	(E)	(E) GPDW	(E)	(E) GPDW	(E)	(E) ACT	
B023	Corridor	(E) CONC.	(E)	RB-2	(E) GPDW	(E)	-	-	GPDW	PT-8	-	-	(E) ACT	
B030	Classroom	(E) CONC.	CPT-1	RB-1	GPDW	PT-2	(E) GPDW	PT-1	(E) GPDW	PT-2	GPDW	PT-1	(E) ACT	Paint (E) Soffit to Match the Wall Below
B032	Corridor	(E) CONC.	(E)	RB-2	(E) GPDW	(E)	GPDW	PT-8	(E) GPDW	PT-8	(E) GPDW	(E)	(E) ACT	Paint Classroom Alcove Walls and Ceiling PT-3
B102	Nurse	(E) CONC.	LVT-1	RB-1	(E) GPDW	(E)	(E) GPDW	(E)	(E) GPDW	(E)	(E) GPDW	(E)	(E) ACT	
B108	Record Room	(E) CONC.	LVT-1	RB-1	(E) GPDW	(E)	(E) GPDW	(E)	(E) GPDW	(E)	(E) GPDW	(E)	(E) ACT	
B109	Staff Lounge	(E) CONC.	(E) CPT, LVT-1	RB-1	(E) GPDW	(E)	(E) GPDW	(E)	(E) GPDW	(E)	(E) GPDW	(E)	(E) ACT	
B111	Corridor	(E) CONC.	(E) CPT, LVT-1	(E) RB, RB-1	(E) GPDW	(E)	-	-	(E) GPDW	(E)	-	-	(E) ACT	
B112	Exec. Closeout	(E) CONC.	LVT-1	RB-1	(E) GPDW	(E)	(E) GPDW	(E)	(E) GPDW	(E)	(E) GPDW	(E)	(E) ACT	
B119	Special Ed. Classroom	(E) CONC.	(E) CPT, LVT-1	RB-1	(E) GPDW	(E)	(E) GPDW	(E)	(E) GPDW	(E)	(E) GPDW	(E)	(E) ACT	
B123	Classroom	(E) CONC.	(E) CPT, LVT-1	RB-1	(E) GPDW	(E)	(E) GPDW	(E)	(E) GPDW	(E)	(E) GPDW	(E)	(E) ACT	
B123A	Storage	(E) CONC.	LVT-1	RB-1	(E) GPDW	(E)	(E) GPDW	(E)	(E) GPDW	(E)	(E) GPDW	(E)	(E) ACT	
B124	Classroom	(E) CONC.	(E) CPT, LVT-1	RB-1	(E) GPDW	(E)	(E) GPDW	(E)	(E) GPDW	(E)	(E) GPDW	(E)	(E) ACT	
B124B	Storage	(E) CONC.	LVT-1	RB-1	(E) GPDW	(E)	(E) GPDW	(E)	(E) GPDW	(E)	(E) GPDW	(E)	(E) ACT	
B126	Classroom	(E) CONC.	(E) CPT, LVT-1	RB-1	(E) GPDW	(E)	(E) GPDW	(E)	(E) GPDW	(E)	(E) GPDW	(E)	(E) ACT	
B126B	Storage	(E) CONC.	LVT-1	RB-1	(E) GPDW	(E)	(E) GPDW	(E)	(E) GPDW	(E)	(E) GPDW	(E)	(E)	
B128	Corridor	(E) CONC.	(E)	RB-2	(E) GPDW	(E)	(E) GPDW	(E)	(E) GPDW	(E)	GPDW	PT-8	(E) ACT	Paint Classroom Alcove Walls and Ceiling PT-3
B129	Storage	(E) CONC.	LVT-1	RB-1	(E) GPDW	(E)	(E) GPDW	(E)	(E) GPDW	(E)	(E) GPDW	(E)	(E) ACT	
B130	Classroom	(E) CONC.	(E) CPT, LVT-1	RB-1	(E) GPDW	(E)	(E) GPDW	(E)	(E) GPDW	(E)	(E) GPDW	(E)	(E) ACT	
B130A	Storage	(E) CONC.	LVT-1	RB-1	(E) GPDW	(E)	(E) GPDW	(E)	(E) GPDW	(E)	(E) GPDW	(E)	(E) ACT	
B132	Classroom	(E) CONC.	(E) CPT, LVT-1	RB-1	(E) GPDW	(E)	(E) GPDW	(E)	(E) GPDW	(E)	(E) GPDW	(E)	(E) ACT	
B132B	Storage	(E) CONC.	LVT-1	RB-1	(E) GPDW	(E)	(E) GPDW	(E)	(E) GPDW	(E)	(E) GPDW	(E)	(E) ACT	
B135	Classroom	(E) CONC.	CPT-1	RB-1	GPDW	PT-2	GPDW	PT-1	(E) GPDW	PT-2	(E) GPDW	PT-1	(E) ACT	Paint (E) Soffit to Match the Wall Below
B137	Classroom	(E) CONC.	(E) CPT, LVT-1	RB-1	(E) GPDW	(E)	(E) GPDW	(E)	(E) GPDW	(E)	(E) GPDW	(E)	(E) ACT	
B137B	Storage	(E) CONC.	LVT-1	RB-1	(E) GPDW	(E)	(E) GPDW	(E)	(E) GPDW	(E)	(E) GPDW	(E)	(E)	
B138	Corridor	(E) CONC.	(E)	RB-2	(E) GPDW	(E)	-	-	GPDW	PT-8	-	-	(E) ACT	
B145	Classroom	(E) CONC.	CPT-1	RB-1	GPDW	PT-2	(E) GPDW	PT-1	(E) GPDW	PT-2	GPDW	PT-1	(E) ACT	Paint (E) Soffit to Match the Wall Below
B147	Corridor	(E) CONC.	(E)	RB-2	(E) GPDW	(E)	GPDW	PT-8	(E) GPDW	(E)	(E) GPDW	(E)	(E) ACT	Paint Classroom Alcove Walls and Ceiling PT-3
S001	Stair	(E) CONC.	LVT-1	RB-1	(E) GPDW	(E)	(E) GPDW	(E)	(E) GPDW	(E)	(E) GPDW	(E)	(E) ACT	
S003	Stair	(E) CONC.	LVT-1	RB-1	(E) GPDW	(E)	(E) GPDW	(E)	(E) GPDW	(E)	(E) GPDW	(E)	(E) ACT	
S004	Stair	(E) CONC.	LVT-1	RB-1	(E) GPDW	(E)	(E) GPDW	(E)	(E) GPDW	(E)	(E) GPDW	(E)	(E) ACT	

FINISH PLAN LEGEND

L CORNER GUARD - STAINLESS STEEL

CARPET

LVT1

LVT2

FINISH LEGEND

FLOORING AND WALL BASE

CARPET

CPT1 TARKETT POWERBOND 6' - 11877 THREADCRAFT
COLOR: 60801 NIGHT VALE

LUXURY VINYL TILE

LVT1 ARMSTRONG DIAMOND 10 TECHNOLOGY ARBORART
COLOR: GALENA OAK RYE NA180 6" X 48" AT 1/3 OFFSET

LVT2 ARMSTRONG DIAMOND 10 TECHNOLOGY COALESCE
COLOR: OXIDIZE PLATINUM ST883 18" X 36" AT 1/3 OFFSET

RUBBER BASE/RESILIENT BASE

RB1 ROPPE 4" BASE BLACK

RB2 MANNINGTON COMMERCIAL 4" LIGHT TEAL #254

RUBBER/RESILIENT FLOOR TRANSITIONS

TE-1 JOHNSONITE BY TARKETT SLT OR EQUAL. COLOR: BLACK

WALLS

PAINT/EPOXY PAINT

PT1 - FIELD PAINT	BENJAMIN MOORE OLYMPIC MOUNTAINS #971
PT2 - ACCENT PAINT	BENJAMIN MOORE OLD BLUE JEANS #839
PT3 - ALCOVE PAINT	BLUE TO MATCH EXISTING ALCOVE PAINT
PT4 - FRAME PAINT	TEAL TO MATCH EXISTING FRAME PAINT
PT5 - ACCENT PAINT	LIGHT BLUE TO MATCH EXISTING LEARNING CENTER PAINT
PT6 - ACCENT PAINT	PURPLE TO MATCH EXISTING LEARNING CENTER PAINT
PT7 - ACCENT PAINT	BEIGE TO MATCH EXISTING LEARNING CENTER PAINT
PT8 - FIELD PAINT	BENJAMIN MOORE STERLING SILVER #1461

CASEWORK

WOOD VENEERED PLYWOOD

WVP PLAIN SLICED WHITE MAPLE WITH CLEAR FINISH

SOLID SURFACE

SS1 FORMICA CLASSICS RIVER ROCK MOSAIC 656
MATTE FINISH

DAO ARCHITECTURE

7230 Meade St.
Westminster, CO 80030

Phone: 720.273.0431
Email: dan@daoarch.com
Web: www.daoarch.com

Westminster Public Schools

Hodgkins Leadership Academy Classroom Conversion Project

3475 W 67th Ave,
Denver, CO 80221

DAO No.:2021-033

September 25, 2026

Lower Level Finish Plan

A9.0


Autodesk Docs://WPS 2026 Bond Projects - Hodgkins Classroom Conversion/Hodgkins ES Classroom Conversion (Revit 2026).rvt
9/25/2026 9:14:25 AM

ROOM FINISH SCHEDULE

IDENTIFICATION		FLOOR			WALLS								CEILING	
					NORTH		EAST		SOUTH		WEST			
NO.	NAME	MATERIAL	FINISH	BASE	MATERIAL	FINISH	MATERIAL	FINISH	MATERIAL	FINISH	MATERIAL	FINISH	MATERIAL	REMARKS
103B	PE Office	(E) CONC.	LVT-1	RB-1	(E) GPDW	(E)	(E) GPDW	(E)	(E) GPDW	(E)	(E) GPDW	(E)	(E) ACT	
A102	Corridor	(E) CONC.	LVT-1, LVT-2	RB-1	(E) GPDW	(E)	(E) GPDW	(E)	(E) GPDW	-	(E) GPDW	(E)	(E) ACT	
A102B	Kitchenette	(E) CONC.	LVT-1	RB-1	(E) GPDW	(E)	(E) GPDW	(E)	-	-	(E) GPDW	(E)	(E) ACT	
A105A	General Music Storage	(E) CONC.	LVT-1	RB-1	(E) GPDW	(E)	(E) GPDW	(E)	(E) GPDW	(E)	(E) GPDW	(E)	(E) ACT	
A110	B&A School Care	(E) CONC.	LVT-1	RB-1	(E) GPDW	(E)	(E) GPDW	(E)	(E) GPDW	(E)	(E) GPDW	(E)	(E) ACT	
A112	Multi-Purpose Room	(E) CONC.	LVT-1, LVT-2	RB-1	(E) GPDW	(E)	(E) GPDW	(E)	(E) GPDW	(E)	(E) GPDW	(E)	(E) ACT	
A112A	Multipurpose Room Storage	(E) CONC.	LVT-1	RB-1	(E) GPDW	(E)	(E) GPDW	(E)	(E) GPDW	(E)	(E) GPDW	(E)	(E) ACT	
A130	Storage	(E) CONC.	LVT-1	RB-1	(E) GPDW	(E)	(E) GPDW	(E)	(E) GPDW	(E)	(E) GPDW	(E)	(E) ACT	
B008	Classroom	(E) CONC.	CPT-1	RB-1	GPDW	PT-2	(E) GPDW	PT-1	(E) GPDW	PT-2	GPDW	PT-1	(E) ACT	Paint (E) Soffit to Match the Wall Below
B009	Learning Center	(E) CONC.	(E)	RB-2	(E) GPDW	PT-6	(E) GPDW	PT-6	(E) GPDW	PT-5 & PT-6	(E) GPDW	PT-6	(E)	Refer to Sheets A6.1 & A6.2 for Paint Layout
B012	Corridor	(E) CONC.	(E)	RB-2	(E) GPDW	(E)	(E) GPDW	(E)	(E) GPDW	(E)	GPDW	PT-8	(E) ACT	Paint Classroom Alcove Walls and Ceiling PT-3
B013	Classroom	(E) CONC.	CPT-1	RB-1	(E) GPDW	(E)	(E) GPDW	(E)	(E) GPDW	(E)	(E) GPDW	(E)	(E) ACT	
B015	Classroom	(E) CONC.	CPT-1	RB-1	(E) GPDW	(E)	(E) GPDW	(E)	(E) GPDW	(E)	(E) GPDW	(E)	(E) ACT	
B020	Classroom	(E) CONC.	CPT-1	RB-1	GPDW	PT-2	GPDW	PT-1	(E) GPDW	PT-2	(E) GPDW	PT-1	(E) ACT	Paint (E) Soffit to Match the Wall Below

ROOM FINISH SCHEDULE

IDENTIFICATION		FLOOR			WALLS								CEILING	
					NORTH		EAST		SOUTH		WEST			
NO.	NAME	MATERIAL	FINISH	BASE	MATERIAL	FINISH	MATERIAL	FINISH	MATERIAL	FINISH	MATERIAL	FINISH	MATERIAL	REMARKS
B021	Classroom	(E) CONC.	CPT-1	RB-1	(E) GPDW	(E)	(E) GPDW	(E)	(E) GPDW	(E)	(E) GPDW	(E)	(E) ACT	
B023	Corridor	(E) CONC.	(E)	RB-2	(E) GPDW	(E)	-	-	GPDW	PT-8	-	-	(E) ACT	
B030	Classroom	(E) CONC.	CPT-1	RB-1	GPDW	PT-2	(E) GPDW	PT-1	(E) GPDW	PT-2	GPDW	PT-1	(E) ACT	Paint (E) Soffit to Match the Wall Below
B032	Corridor	(E) CONC.	(E)	RB-2	(E) GPDW	(E)	GPDW	PT-8	(E) GPDW	(E)	(E) GPDW	(E)	(E) ACT	Paint Classroom Alcove Walls and Ceiling PT-3
B102	Nurse	(E) CONC.	LVT-1	RB-1	(E) GPDW	(E)	(E) GPDW	(E)	(E) GPDW	(E)	(E) GPDW	(E)	(E) ACT	
B108	Record Room	(E) CONC.	LVT-1	RB-1	(E) GPDW	(E)	(E) GPDW	(E)	(E) GPDW	(E)	(E) GPDW	(E)	(E) ACT	
B109	Staff Lounge	(E) CONC.	(E) CPT, LVT-1	RB-1	(E) GPDW	(E)	(E) GPDW	(E)	(E) GPDW	(E)	(E) GPDW	(E)	(E) ACT	
B111	Corridor	(E) CONC.	(E) CPT, LVT-1	(E) RB, RB-1	(E) GPDW	(E)	-	-	-	-	(E) GPDW	(E)	(E) ACT	
B112	Elec. Closeout	(E) CONC.	LVT-1	RB-1	(E) GPDW	(E)	(E) GPDW	(E)	(E) GPDW	(E)	(E) GPDW	(E)	(E) ACT	
B119	Special Ed. Classroom	(E) CONC.	(E) CPT, LVT-1	RB-1	(E) GPDW	(E)	(E) GPDW	(E)	(E) GPDW	(E)	(E) GPDW	(E)	(E) ACT	
B123	Classroom	(E) CONC.	(E) CPT, LVT-1	RB-1	(E) GPDW	(E)	(E) GPDW	(E)	(E) GPDW	(E)	(E) GPDW	(E)	(E) ACT	
B123A	Storage	(E) CONC.	LVT-1	RB-1	(E) GPDW	(E)	(E) GPDW	(E)	(E) GPDW	(E)	(E) GPDW	(E)	(E) ACT	
B124	Classroom	(E) CONC.	(E) CPT, LVT-1	RB-1	(E) GPDW	(E)	(E) GPDW	(E)	(E) GPDW	(E)	(E) GPDW	(E)	(E) ACT	
B124B	Storage	(E) CONC.	LVT-1	RB-1	(E) GPDW	(E)	(E) GPDW	(E)	(E) GPDW	(E)	(E) GPDW	(E)	(E) ACT	
B126	Classroom	(E) CONC.	(E) CPT, LVT-1	RB-1	(E) GPDW	(E)	(E) GPDW	(E)	(E) GPDW	(E)	(E) GPDW	(E)	(E) ACT	
B126B	Storage	(E) CONC.	LVT-1	RB-1	(E) GPDW	(E)	(E) GPDW	(E)	(E) GPDW	(E)	(E) GPDW	(E)	(E)	
B128	Corridor	(E) CONC.	(E)	RB-2	(E) GPDW	(E)	(E) GPDW	(E)	(E) GPDW	(E)	GPDW	PT-8	(E) ACT	Paint Classroom Alcove Walls and Ceiling PT-3
B129	Storage	(E) CONC.	LVT-1	RB-1	(E) GPDW	(E)	(E) GPDW	(E)	(E) GPDW	(E)	(E) GPDW	(E)	(E) ACT	
B130	Classroom	(E) CONC.	(E) CPT, LVT-1	RB-1	(E) GPDW	(E)	(E) GPDW	(E)	(E) GPDW	(E)	(E) GPDW	(E)	(E) ACT	
B130A	Storage	(E) CONC.	LVT-1	RB-1	(E) GPDW	(E)	(E) GPDW	(E)	(E) GPDW	(E)	(E) GPDW	(E)	(E) ACT	
B132	Classroom	(E) CONC.	(E) CPT, LVT-1	RB-1	(E) GPDW	(E)	(E) GPDW	(E)	(E) GPDW	(E)	(E) GPDW	(E)	(E) ACT	
B132B	Storage	(E) CONC.	LVT-1	RB-1	(E) GPDW	(E)	(E) GPDW	(E)	(E) GPDW	(E)	(E) GPDW	(E)	(E) ACT	
B135	Classroom	(E) CONC.	CPT-1	RB-1	GPDW	PT-2	GPDW	PT-1	(E) GPDW	PT-2	(E) GPDW	PT-1	(E) ACT	Paint (E) Soffit to Match the Wall Below
B137	Classroom	(E) CONC.	(E) CPT, LVT-1	RB-1	(E) GPDW	(E)	(E) GPDW	(E)	(E) GPDW	(E)	(E) GPDW	(E)	(E) ACT	
B137B	Storage	(E) CONC.	LVT-1	RB-1	(E) GPDW	(E)	(E) GPDW	(E)	(E) GPDW	(E)	(E) GPDW	(E)	(E)	
B138	Corridor	(E) CONC.	(E)	RB-2	(E) GPDW	(E)	-	-	GPDW	PT-8	-	-	(E) ACT	
B145	Classroom	(E) CONC.	CPT-1	RB-1	GPDW	PT-2	(E) GPDW	PT-1	(E) GPDW	PT-2	GPDW	PT-1	(E) ACT	Paint (E) Soffit to Match the Wall Below
B147	Corridor	(E) CONC.	(E)	RB-2	(E) GPDW	(E)	GPDW	PT-8	(E) GPDW	(E)	(E) GPDW	(E)	(E) ACT	Paint Classroom Alcove Walls and Ceiling PT-3
S001	Stair	(E) CONC.	LVT-1	RB-1	(E) GPDW	(E)	(E) GPDW	(E)	(E) GPDW	(E)	(E) GPDW	(E)	(E) ACT	
S003	Stair	(E) CONC.	LVT-1	RB-1	(E) GPDW	(E)	(E) GPDW	(E)	(E) GPDW	(E)	(E) GPDW	(E)	(E) ACT	
S004	Stair	(E) CONC.	LVT-1	RB-1	(E) GPDW	(E)	(E) GPDW	(E)	(E) GPDW	(E)	(E) GPDW	(E)	(E) ACT	

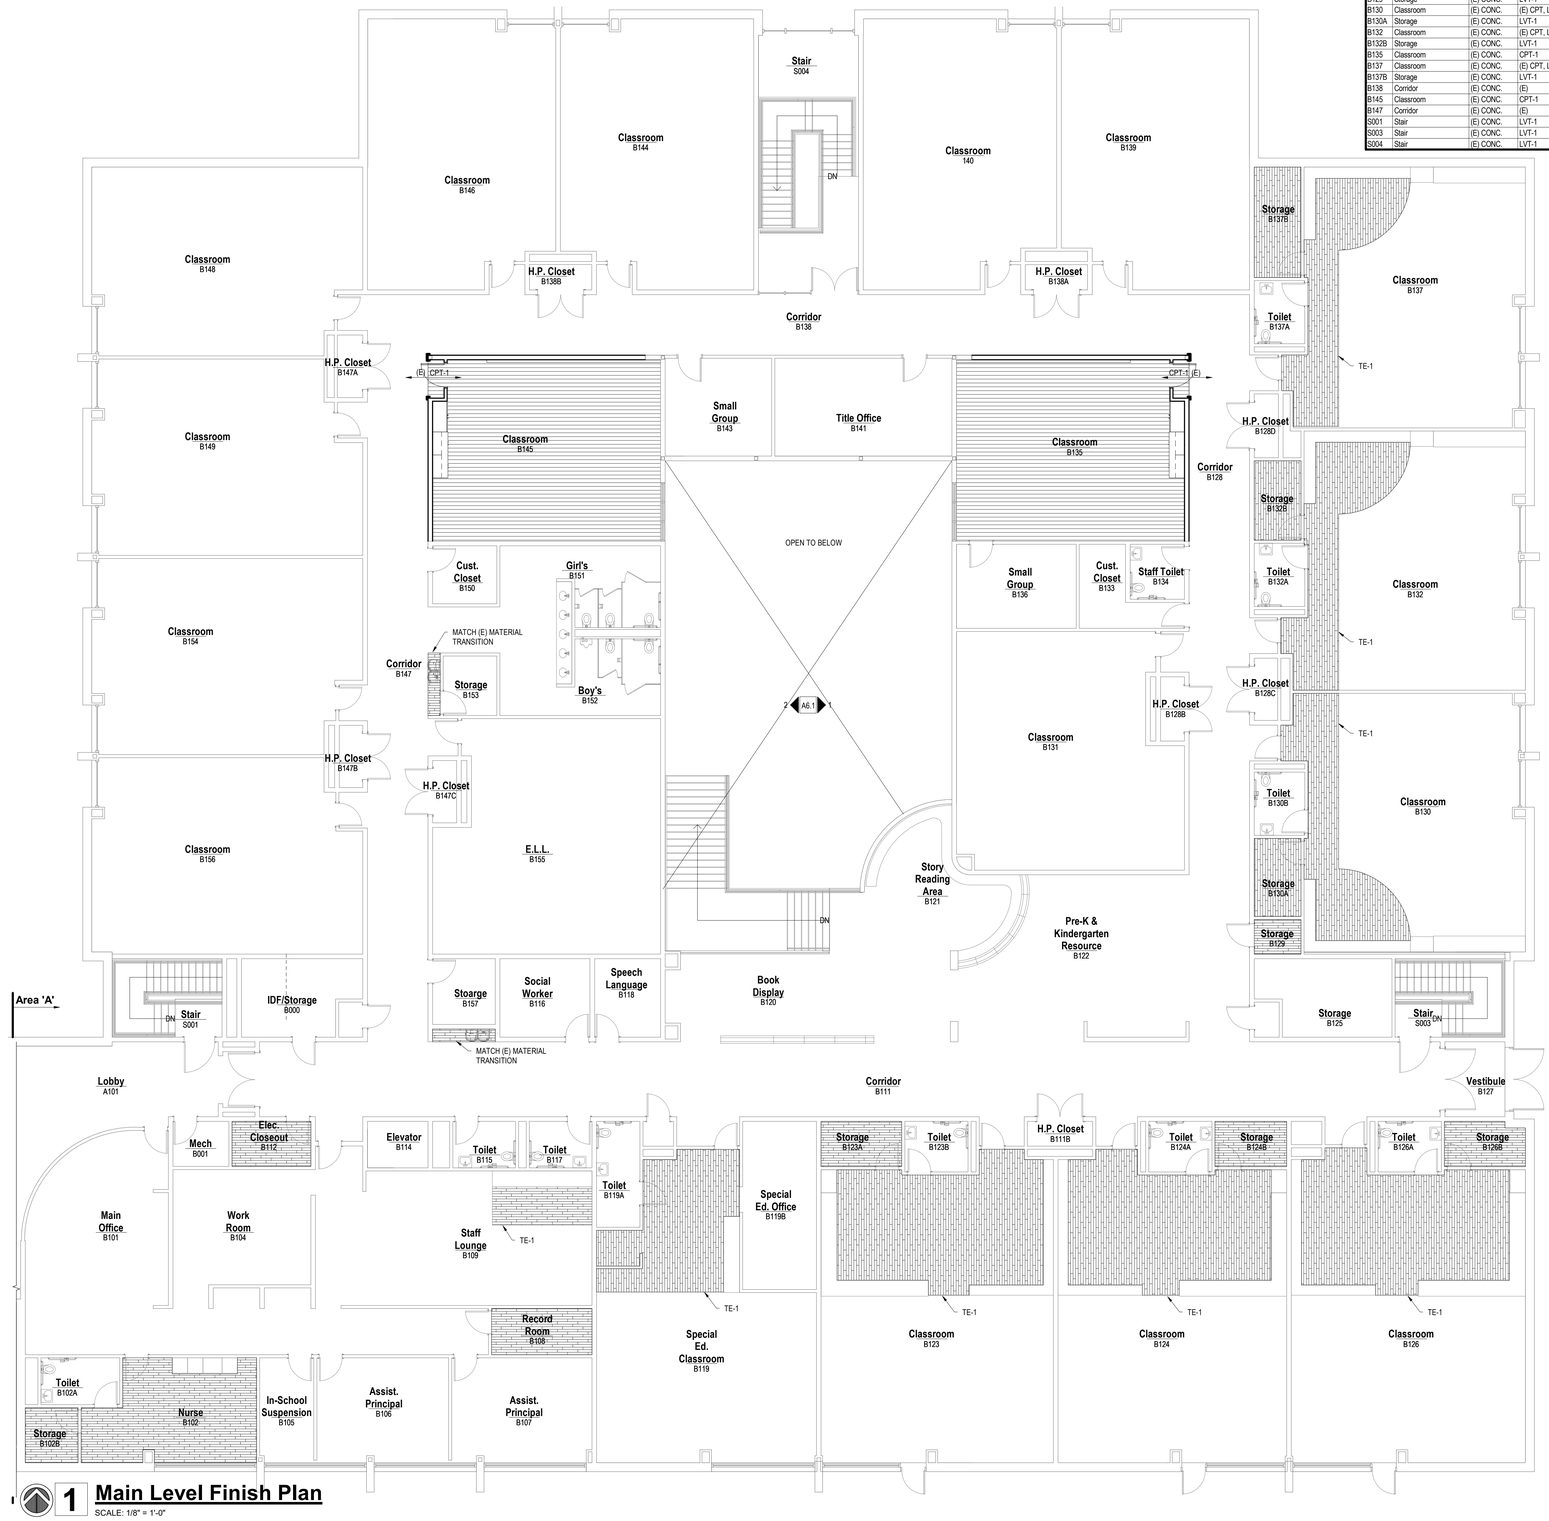

1 **Main Level Finish Plan**
SCALE: 1/8" = 1'-0"

FINISH PLAN LEGEND

- L CORNER GUARD - STAINLESS STEEL
- CARPET
- LVT1
- LVT2

FINISH LEGEND

FLOORING AND WALL BASE

CARPET
CPT1 TARKETT POWERBOND 6' - 11877 THREADCRAFT
COLOR: 60801 NIGHT VALE

LUXURY VINYL TILE
LVT1 ARMSTRONG DIAMOND 10 TECHNOLOGY ARBORART
COLOR: GALENA OAK RYE NA180 6" X 48" AT 1/3 OFFSET
LVT2 ARMSTRONG DIAMOND 10 TECHNOLOGY COALESCE
COLOR: OXIDIZE PLATINUM ST883 18" X 36" AT 1/3 OFFSET

RUBBER BASE/RESILIENT BASE
RB1 ROPPE 4" BASE BLACK
RB2 MANNINGTON COMMERCIAL 4" LIGHT TEAL #254

RUBBER/RESILIENT FLOOR TRANSITIONS
TE-1 JOHNSONITE BY TARKETT SLT OR EQUAL. COLOR: BLACK

WALLS


PAINT/EPOXY PAINT

PT1 - FIELD PAINT	BENJAMIN MOORE OLYMPIC MOUNTAINS #971
PT2 - ACCENT PAINT	BENJAMIN MOORE OLD BLUE JEANS #839
PT3 - ALCOVE PAINT	BLUE TO MATCH EXISTING ALCOVE PAINT
PT4 - FRAME PAINT	TEAL TO MATCH EXISTING FRAME PAINT
PT5 - ACCENT PAINT	LIGHT BLUE TO MATCH EXISTING LEARNING CENTER PAINT
PT6 - ACCENT PAINT	PURPLE TO MATCH EXISTING LEARNING CENTER PAINT
PT7 - ACCENT PAINT	BEIGE TO MATCH EXISTING LEARNING CENTER PAINT
PT8 - FIELD PAINT	BENJAMIN MOORE STERLING SILVER # 1461

CASEWORK

WOOD VENEERED PLYWOOD
WVP PLAIN SLICED WHITE MAPLE WITH CLEAR FINISH

SOLID SURFACE
SS1 FORMICA CLASSICS RIVER ROCK MOSAIC 656
MATTE FINISH

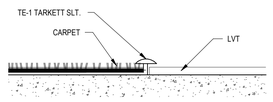

2 **CPT TO LVT**
SCALE: 12" = 1'-0"

DAO ARCHITECTURE
7230 Meade St.
Westminster, CO 80030
Phone: 720.273.0431
E-mail: dan@daoarch.com
Web: www.daoarch.com

Westminster Public Schools

Hodgkins Leadership Academy Classroom Conversion Project

3475 W 67th Ave,
Denver, CO 80221

DAO No.:2021-033

September 25, 2026

Main Level Finish Plan Area 'A'

A9.1

Autodesk Docs://WPS 2026 Bond Projects - Hodgkins Classroom Conversion/Hodgkins ES Classroom Conversion (Revit 2026).rvt
9/25/2026 9:29:04 AM

ROOM FINISH SCHEDULE

IDENTIFICATION		FLOOR			WALLS								CEILING	
					NORTH		EAST		SOUTH		WEST			
NO.	NAME	MATERIAL	FINISH	BASE	MATERIAL	FINISH	MATERIAL	FINISH	MATERIAL	FINISH	MATERIAL	FINISH	MATERIAL	REMARKS
103B	PE Office	(E) CONC.	LVT-1	RB-1	(E) GPDW	(E)	(E) GPDW	(E)	(E) GPDW	(E)	(E) GPDW	(E)	(E) ACT	
A102	Corridor	(E) CONC.	LVT-1, LVT-2	RB-1	(E) GPDW	(E)	(E) GPDW	(E)	(E) GPDW	-	(E) GPDW	(E)	(E) ACT	
A102B	Kitchenette	(E) CONC.	LVT-1	RB-1	(E) GPDW	(E)	(E) GPDW	(E)	-	-	(E) GPDW	(E)	(E) ACT	
A105A	General Music Storage	(E) CONC.	LVT-1	RB-1	(E) GPDW	(E)	(E) GPDW	(E)	(E) GPDW	(E)	(E) GPDW	(E)	(E) ACT	
A110	B&A School Care	(E) CONC.	LVT-1	RB-1	(E) GPDW	(E)	(E) GPDW	(E)	(E) GPDW	(E)	(E) GPDW	(E)	(E) ACT	
A112	Multi-Purpose Room	(E) CONC.	LVT-1, LVT-2	RB-1	(E) GPDW	(E)	(E) GPDW	(E)	(E) GPDW	(E)	(E) GPDW	(E)	(E) ACT	
A112A	Multipurpose Room Storage	(E) CONC.	LVT-1	RB-1	(E) GPDW	(E)	(E) GPDW	(E)	(E) GPDW	(E)	(E) GPDW	(E)	(E) ACT	
A130	Storage	(E) CONC.	LVT-1	RB-1	(E) GPDW	(E)	(E) GPDW	(E)	(E) GPDW	(E)	(E) GPDW	(E)	(E) ACT	
B008	Classroom	(E) CONC.	CPT-1	RB-1	GPDW	PT-2	(E) GPDW	PT-1	(E) GPDW	PT-2	GPDW	PT-1	(E) ACT	Paint (E) Soffit to Match the Wall Below
B009	Learning Center	(E) CONC.	(E)	RB-2	(E) GPDW	PT-6	(E) GPDW	PT-6	(E) GPDW	PT-5 & PT-6	(E) GPDW	PT-6	(E)	Refer to Sheets A6.1 & A6.2 for Paint Layout
B012	Corridor	(E) CONC.	(E)	RB-2	(E) GPDW	(E)	(E) GPDW	(E)	(E) GPDW	(E)	GPDW	PT-8	(E) ACT	Paint Classroom Alcove Walls and Ceiling PT-3
B013	Classroom	(E) CONC.	CPT-1	RB-1	(E) GPDW	(E)	(E) GPDW	(E)	(E) GPDW	(E)	(E) GPDW	(E)	(E) ACT	
B015	Classroom	(E) CONC.	CPT-1	RB-1	(E) GPDW	(E)	(E) GPDW	(E)	(E) GPDW	(E)	(E) GPDW	(E)	(E) ACT	
B020	Classroom	(E) CONC.	CPT-1	RB-1	GPDW	PT-2	GPDW	PT-1	(E) GPDW	PT-2	(E) GPDW	PT-1	(E) ACT	Paint (E) Soffit to Match the Wall Below
B021	Classroom	(E) CONC.	CPT-1	RB-1	(E) GPDW	(E)	(E) GPDW	(E)	(E) GPDW	(E)	(E) GPDW	(E)	(E) ACT	
B023	Corridor	(E) CONC.	(E)	RB-2	(E) GPDW	(E)	-	-	GPDW	PT-8	-	-	(E) ACT	
B030	Classroom	(E) CONC.	CPT-1	RB-1	GPDW	PT-2	(E) GPDW	PT-1	(E) GPDW	PT-2	GPDW	PT-1	(E) ACT	Paint (E) Soffit to Match the Wall Below
B032	Corridor	(E) CONC.	(E)	RB-2	(E) GPDW	(E)	GPDW	PT-8	(E) GPDW	(E)	(E) GPDW	(E)	(E) ACT	Paint Classroom Alcove Walls and Ceiling PT-3
B102	Nurse	(E) CONC.	LVT-1	RB-1	(E) GPDW	(E)	(E) GPDW	(E)	(E) GPDW	(E)	(E) GPDW	(E)	(E) ACT	
B108	Record Room	(E) CONC.	LVT-1	RB-1	(E) GPDW	(E)	(E) GPDW	(E)	(E) GPDW	(E)	(E) GPDW	(E)	(E) ACT	
B109	Staff Lounge	(E) CONC.	(E) CPT, LVT-1	RB-1	(E) GPDW	(E)	(E) GPDW	(E)	(E) GPDW	(E)	(E) GPDW	(E)	(E) ACT	
B111	Corridor	(E) CONC.	(E) CPT, LVT-1	(E) RB, RB-1	(E) GPDW	(E)	-	-	(E) GPDW	(E)	-	-	(E) ACT	
B112	Exec. Closeout	(E) CONC.	LVT-1	RB-1	(E) GPDW	(E)	(E) GPDW	(E)	(E) GPDW	(E)	(E) GPDW	(E)	(E) ACT	
B119	Special Ed. Classroom	(E) CONC.	(E) CPT, LVT-1	RB-1	(E) GPDW	(E)	(E) GPDW	(E)	(E) GPDW	(E)	(E) GPDW	(E)	(E) ACT	
B123	Classroom	(E) CONC.	(E) CPT, LVT-1	RB-1	(E) GPDW	(E)	(E) GPDW	(E)	(E) GPDW	(E)	(E) GPDW	(E)	(E) ACT	
B123A	Storage	(E) CONC.	LVT-1	RB-1	(E) GPDW	(E)	(E) GPDW	(E)	(E) GPDW	(E)	(E) GPDW	(E)	(E) ACT	
B124	Classroom	(E) CONC.	(E) CPT, LVT-1	RB-1	(E) GPDW	(E)	(E) GPDW	(E)	(E) GPDW	(E)	(E) GPDW	(E)	(E) ACT	
B124B	Storage	(E) CONC.	LVT-1	RB-1	(E) GPDW	(E)	(E) GPDW	(E)	(E) GPDW	(E)	(E) GPDW	(E)	(E) ACT	
B126	Classroom	(E) CONC.	(E) CPT, LVT-1	RB-1	(E) GPDW	(E)	(E) GPDW	(E)	(E) GPDW	(E)	(E) GPDW	(E)	(E) ACT	
B126B	Storage	(E) CONC.	LVT-1	RB-1	(E) GPDW	(E)	(E) GPDW	(E)	(E) GPDW	(E)	(E) GPDW	(E)	(E)	
B128	Corridor	(E) CONC.	(E)	RB-2	(E) GPDW	(E)	(E) GPDW	(E)	(E) GPDW	(E)	GPDW	PT-8	(E) ACT	Paint Classroom Alcove Walls and Ceiling PT-3
B129	Storage	(E) CONC.	LVT-1	RB-1	(E) GPDW	(E)	(E) GPDW	(E)	(E) GPDW	(E)	(E) GPDW	(E)	(E) ACT	
B130	Classroom	(E) CONC.	(E) CPT, LVT-1	RB-1	(E) GPDW	(E)	(E) GPDW	(E)	(E) GPDW	(E)	(E) GPDW	(E)	(E) ACT	
B130A	Storage	(E) CONC.	LVT-1	RB-1	(E) GPDW	(E)	(E) GPDW	(E)	(E) GPDW	(E)	(E) GPDW	(E)	(E) ACT	
B132	Classroom	(E) CONC.	(E) CPT, LVT-1	RB-1	(E) GPDW	(E)	(E) GPDW	(E)	(E) GPDW	(E)	(E) GPDW	(E)	(E) ACT	
B132B	Storage	(E) CONC.	LVT-1	RB-1	(E) GPDW	(E)	(E) GPDW	(E)	(E) GPDW	(E)	(E) GPDW	(E)	(E) ACT	
B135	Classroom	(E) CONC.	CPT-1	RB-1	GPDW	PT-2	GPDW	PT-1	(E) GPDW	PT-2	(E) GPDW	PT-1	(E) ACT	Paint (E) Soffit to Match the Wall Below
B137	Classroom	(E) CONC.	(E) CPT, LVT-1	RB-1	(E) GPDW	(E)	(E) GPDW	(E)	(E) GPDW	(E)	(E) GPDW	(E)	(E) ACT	
B137B	Storage	(E) CONC.	LVT-1	RB-1	(E) GPDW	(E)	(E) GPDW	(E)	(E) GPDW	(E)	(E) GPDW	(E)	(E)	
B138	Corridor	(E) CONC.	(E)	RB-2	(E) GPDW	(E)	-	-	GPDW	PT-8	-	-	(E) ACT	
B145	Classroom	(E) CONC.	CPT-1	RB-1	GPDW	PT-2	(E) GPDW	PT-1	(E) GPDW	PT-2	GPDW	PT-1	(E) ACT	Paint (E) Soffit to Match the Wall Below
B147	Corridor	(E) CONC.	(E)	RB-2	(E) GPDW	(E)	GPDW	PT-8	(E) GPDW	(E)	(E) GPDW	(E)	(E) ACT	Paint Classroom Alcove Walls and Ceiling PT-3
S001	Stair	(E) CONC.	LVT-1	RB-1	(E) GPDW	(E)	(E) GPDW	(E)	(E) GPDW	(E)	(E) GPDW	(E)	(E) ACT	
S003	Stair	(E) CONC.	LVT-1	RB-1	(E) GPDW	(E)	(E) GPDW	(E)	(E) GPDW	(E)	(E) GPDW	(E)	(E) ACT	
S004	Stair	(E) CONC.	LVT-1	RB-1	(E) GPDW	(E)	(E) GPDW	(E)	(E) GPDW	(E)	(E) GPDW	(E)	(E) ACT	



1 **Main Level Finish Plan Copy 1**

SCALE: 1/8" = 1'-0"

Autodesk Docs://WPS 2026 Bond Projects - Hodgkins Classroom Conversion/Hodgkins ES Classroom Conversion (Revit 2026).rvt
9/25/2026 9:29:04 AM

FINISH PLAN LEGEND

- CORNER GUARD - STAINLESS STEEL
- CARPET
- LVT1
- LVT2

FINISH LEGEND

FLOORING AND WALL BASE

CARPET

CPT1 TARKETT POWERBOND 6' - 11877 THREADCRAFT
COLOR: 60801 NIGHT VALE

LUXURY VINYL TILE

LVT1 ARMSTRONG DIAMOND 10 TECHNOLOGY ARBORART
COLOR: GALENA OAK RYE NA180 6" X 48" AT 1/3 OFFSET

LVT2 ARMSTRONG DIAMOND 10 TECHNOLOGY COALESCE
COLOR: OXIDIZE PLATINUM ST883 18" X 36" AT 1/3 OFFSET

RUBBER BASE/RESILIENT BASE

RB1 ROPPE 4" BASE BLACK

RB2 MANNINGTON COMMERCIAL 4" LIGHT TEAL #254

RUBBER/RESILIENT FLOOR TRANSITIONS

TE-1 JOHNSONITE BY TARKETT SLT OR EQUAL. COLOR: BLACK

WALLS

PAINT/EPOXY PAINT

PT1 - FIELD PAINT	BENJAMIN MOORE OLYMPIC MOUNTAINS #971
PT2 - ACCENT PAINT	BENJAMIN MOORE OLD BLUE JEANS #839
PT3 - ALCOVE PAINT	BLUE TO MATCH EXISTING ALCOVE PAINT
PT4 - FRAME PAINT	TEAL TO MATCH EXISTING FRAME PAINT
PT5 - ACCENT PAINT	LIGHT BLUE TO MATCH EXISTING LEARNING CENTER PAINT
PT6 - ACCENT PAINT	PURPLE TO MATCH EXISTING LEARNING CENTER PAINT
PT7 - ACCENT PAINT	BEIGE TO MATCH EXISTING LEARNING CENTER PAINT
PT8 - FIELD PAINT	BENJAMIN MOORE STERLING SILVER #1461

CASEWORK

WOOD VENEERED PLYWOOD

WVP PLAIN SLICED WHITE MAPLE WITH CLEAR FINISH

SOLID SURFACE

SS1 FORMICA CLASSICS RIVER ROCK MOSAIC 656
MATTE FINISH

DAO ARCHITECTURE

7230 Meade St.
Westminster, CO 80030

Phone: 720.273.0431
Email: dan@daoarch.com
Web: www.daoarch.com

Westminster Public Schools

Hodgkins Leadership Academy Classroom Conversion Project

3475 W 67th Ave,
Denver, CO 80221

DAO No.:2021-033

September 25, 2026

Main Level Finish Plan Area 'B'

A9.2

GENERAL LEGEND

ABBV.	SYMBOL	DESCRIPTION
HP		HEAT PUMP
SF		SUPPLY FAN
EF		EXHAUST FAN
RG		RETURN GRILLE
EG		EXHAUST GRILLE
TG		TRANSFER GRILLE
SA		SUPPLY AIR
RA		RETURN AIR
EA		EXHAUST AIR
OA		OUTSIDE AIR
TA		TRANSFER AIR
G.C.		GENERAL CONTRACTOR
M.C.		MECHANICAL CONTRACTOR
E.C.		ELECTRICAL CONTRACTOR
T.C.C.		TEMPERATURE CONTROL CONTRACTOR
F.P.C.		FIRE PROTECTION CONTRACTOR
A.F.F.		ABOVE FINISHED FLOOR
(N)		NEW
(E)		EXISTING
		EXISTING (DEMOLITION OR REMOVED)
		CONTROL WIRING
AD/AP		ACCESS DOOR/ACCESS PANEL
		POINT OF CONNECTION - NEW TO EXISTING
MVD		MANUAL VOLUME DAMPER
FD		FIRE DAMPER
FSD		COMBINATION MOTORIZED FIRE/SMOKE DAMPER
		EXISTING FIRE DAMPER
		EXISTING COMBINATION MOTORIZED FIRE/SMOKE DAMPER
	T H CO2	TEMPERATURE / HUMIDITY / CARBON DIOXIDE SENSOR
		SUPPLY DUCT UP & DOWN
		RETURN/EXHAUST DUCT UP & DOWN
		ROUND SUPPLY DUCT UP & DOWN
		DUCT ELBOW WITH TURNING VANES
		SQUARE TO ROUND TRANSITION
	12x8 / 12x8	OFFSET DUCT UP / DOWN IN DIRECTION OF ARROW
		CONICAL SPIN-IN FITTING WITH MANUAL VOLUME DAMPER
		CONICAL SPIN-IN FITTING WITHOUT MANUAL VOLUME DAMPER
		45° TAKEOFF
		STANDARD RADIUS ELBOW
	10x8	NEW RECTANGULAR DUCTWORK - WIDTH x DEPTH
	10"ø	NEW ROUND DUCTWORK - DIAMETER
	10x8ø	NEW OVAL DUCTWORK - WIDTH / DEPTH
	(E)10x8	EXISTING DUCTWORK TO REMAIN
	10x8	EXISTING DUCTWORK TO BE REMOVED
CD		CEILING DIFFUSER (FOUR WAY THROW PATTERN)
RG/EG		RETURN OR EXHAUST REGISTER OR GRILLE
		FLEXIBLE DUCTWORK

GRILLES, REGISTERS & DIFFUSERS SCHEDULE

PLAN CODE	MANUFACTURER & MODEL NO.	TYPE & SERVICE	NECK SIZE	FACE SIZE	VOLUME DAMPER (OBD)	MATERIAL	MOUNTING TYPE	FINISH	REMARKS
EG-1	PRICE PDDR	EXHAUST	AS NOTED	24"x24"	NONE	STEEL	LAY-IN	WHITE	NOTE: 1

NOTES:
1. ACCEPTABLE ALTERNATES: KRUEGER, TITUS.

SHEET INDEX

SHEET NUMBER	MECHANICAL, PLUMBING & FIRE PROTECTION SHEET TITLE	SHEET SCALE
M0.0	Mechanical Cover Sheet	NONE
M1.0	Lower Level HVAC Floor Plan	1/8" = 1'-0"
M1.1	Main Level HVAC Floor Plan	1/8" = 1'-0"
MD1.0	Lower Level HVAC Demolition Plan	1/8" = 1'-0"
MD1.1	Main Level HVAC Demolition Plan	1/8" = 1'-0"

MECHANICAL DEMOLITION GENERAL NOTES AND SPECIFICATIONS

1. THE MECHANICAL CONTRACTOR SHALL INSPECT SITE TO BECOME FAMILIAR WITH THE SCOPE OF THE WORK. THESE DOCUMENTS DO NOT REFLECT AS-BUILT CONDITIONS. ANY DISCREPANCIES BETWEEN THESE DOCUMENTS AND THE ACTUAL CONDITIONS SHALL BE REPORTED TO THE ARCHITECT/ENGINEER FOR RESOLUTION PRIOR TO BID PRICING. NO EXTRAS WILL BE ALLOWED DUE TO LACK OF KNOWLEDGE OF THE EXISTING CONDITIONS.
2. THE MECHANICAL CONTRACTOR SHALL COORDINATE THE LOCATION OF ALL ABOVE CEILING EQUIPMENT, DUCTWORK, AND CEILING MOUNTED AIR DEVICES WITH EXISTING ARCHITECTURAL, STRUCTURAL, ELECTRICAL, AND MECHANICAL CONDITIONS. APPROXIMATE LOCATIONS OF NEW WORK ARE SHOWN AND SHOULD BE FOLLOWED AS CLOSELY AS EXISTING CONDITIONS WILL ALLOW.
3. COORDINATE DEMOLITION REQUIREMENTS WITH THE GENERAL CONTRACTOR.
4. COORDINATE EXTENT OF DEMOLITION WITH THE NEW CONSTRUCTION AS SHOWN IN THESE DOCUMENTS.
5. EXISTING MECHANICAL WORK IS SHOWN LIGHT.
6. ALL MECHANICAL ITEMS INDICATED TO BE DEMOLISHED SHALL BE INSPECTED FOR SALVAGE BY THE OWNER. ALL NON-SALVAGEABLE ITEMS SHALL THEN BE IMMEDIATELY REMOVED FROM THE SITE BY THE MECHANICAL CONTRACTOR.
7. ALL UNUSED TEMPERATURE CONTROL WIRING, WIRE MOLD, PNEUMATIC TUBING AND CONTROL COMPONENTS SHALL BE REMOVED.
8. ALL UNUSED HANGERS AND SUPPORTS SHALL BE REMOVED.
9. THE REMOVAL OR INSTALLATION OF CONTROLS, PIPES, DUCTS, AND EQUIPMENT MAY REQUIRE THE REMOVAL OF EXISTING WALLS AND CEILINGS. THE GENERAL CONTRACTOR SHALL BE RESPONSIBLE FOR REPAIRING AND PAINTING THESE WALLS AND/OR CEILINGS SO THEY MATCH THE EXISTING WHERE NOT REPLACED UNDER THE ARCHITECTURAL DOCUMENTS. THE GENERAL CONTRACTOR SHALL REVIEW THE MECHANICAL DRAWINGS TO IDENTIFY THESE LOCATIONS PRIOR TO BID PRICING.
10. THE GENERAL CONTRACTOR SHALL PATCH AND PAINT WALLS TO MATCH EXISTING AT THE DEMOLISHED CONTROLS.
11. THE GENERAL CONTRACTOR SHALL PATCH THE CEILING, ROOF, AND WALLS TO MATCH EXISTING AT DEMOLISHED HANGERS AND SUPPORTS.
12. THE GENERAL CONTRACTOR SHALL MAKE REPAIRS TO ALL EXISTING BUILDING COMPONENTS THAT HAVE BEEN AFFECTED BY THE DEMOLITION OF MECHANICAL SYSTEMS.
13. PORTIONS OF THIS BUILDING WILL BE OCCUPIED DURING THIS CONSTRUCTION PROJECT. THE MECHANICAL CONTRACTOR SHALL COORDINATE THE SCHEDULING OF THEIR WORK WITH THE GENERAL CONTRACTOR. CLEAN UP AT THE END OF EACH DAY.

MECHANICAL GENERAL NOTES AND SPECIFICATIONS

1. THESE DOCUMENTS ARE DIAGRAMMATIC IN NATURE AND ARE NOT INTENDED TO BE UTILIZED AS SHOP DRAWINGS NOR NECESSARILY SCALED FOR EXACT MEASUREMENTS. ANY DISCREPANCIES BETWEEN THESE DOCUMENTS AND THE ACTUAL CONDITIONS SHALL BE REPORTED TO THE ARCHITECT/ENGINEER FOR RESOLUTION PRIOR TO INSTALLATION.
2. MECHANICAL WORK SHALL COMPLY WITH ALL APPLICABLE CODES. VERIFY ALL REQUIREMENTS PRIOR TO SUBMITTING BID OR COMMENCING WORK.
3. MECHANICAL CONTRACTOR SHALL BE RESPONSIBLE FOR ANY ADDITIONAL COORDINATION OR MODIFICATIONS THAT MAY BE REQUIRED DUE TO THE USE OR INSTALLATION OF EQUIPMENT OTHER THAN THAT OF THE BASIS OF DESIGN MANUFACTURERS LISTED ON THE DRAWINGS.
4. THE MECHANICAL CONTRACTOR SHALL COORDINATE WORK WITH OTHER TRADES PRIOR TO AND DURING CONSTRUCTION. THE MECHANICAL SYSTEMS SHOWN SHALL BE RUN AS HIGH AS POSSIBLE UNLESS NOTED OTHERWISE.
5. REFER TO THE ARCHITECTURAL REFLECTED CEILING PLANS FOR EXACT LOCATION OF ALL CEILING AIR DEVICES AND ACCESS PANELS. OBTAIN CLARIFICATION FROM THE ARCHITECT, IF EXACT LOCATIONS ARE NOT SHOWN.
6. REFER TO THE ARCHITECTURAL DRAWINGS FOR ROOFING DETAILS SPECIFIC TO THIS PROJECT.
7. THE MECHANICAL CONTRACTOR SHALL COORDINATE THERMOSTAT, SENSOR, AND SWITCH LOCATIONS WITH ARCHITECT/ENGINEER PRIOR TO INSTALLATION. ALL THERMOSTATS, SENSORS, AND SWITCHES SHALL BE LOCATED 48" AFF UNLESS INDICATED OTHERWISE. WHERE EXISTING CONDITIONS REQUIRE EXPOSED CONTROL WIRING, SUCH WIRING SHALL BE CONCEALED WITH WIRE MOLD. WIRE MOLD COLOR SHALL BE SELECTED BY THE ARCHITECT.
8. BALANCE AIR SYSTEMS TO THE QUANTITIES SHOWN AND SUBMIT BALANCE REPORT TO THE ARCHITECT/ENGINEER FOR REVIEW. FAN SYSTEMS TO BE BALANCED WITHIN PLUS 10 PERCENT OR MINUS 5 PERCENT OF LISTED VALUES. AIR INLETS AND OUTLETS TO BE BALANCED WITH PLUS 10 PERCENT TO MINUS 5 PERCENT OF LISTED VALUES.
9. SUBMIT TO THE ARCHITECT/ENGINEER ELECTRONIC PDF FILES OF MECHANICAL SUBMITTALS FOR REVIEW OF ALL DUCTWORK ACCESSORIES. ENGINEER ASSUMES NO RESPONSIBILITY FOR EQUIPMENT OR INSTALLATION COORDINATION THAT HAS NOT BEEN SUBMITTED FOR REVIEW.
10. CONTRACTOR SHALL WARRANTY WORK, EQUIPMENT, MATERIALS, AND PROPER OPERATION FOR A PERIOD OF ONE YEAR FROM THE DATE OF ACCEPTANCE OF BUILDING BY OWNER. THIS GUARANTEE SHALL NOT INCLUDE NORMAL MAINTENANCE REQUIRED BY THE OWNER AS DESCRIBED IN O&M MANUALS.
11. PROVIDE TWO SETS OF OPERATION AND MAINTENANCE (O&M) MANUALS FOR OWNER AT COMPLETION OF PROJECT TO THE ARCHITECT/ENGINEER FOR REVIEW. DOCUMENTATION SHALL CONSIST OF MANUFACTURER'S INFORMATION, SPECIFICATIONS AND RECOMMENDATIONS, PROGRAMMING PROCEDURES AND DATA POINTS, NARRATIVES, AND OTHER MEANS OF ILLUSTRATING TO THE OWNER HOW THE BUILDING, EQUIPMENT, AND SYSTEMS ARE INTENDED TO BE INSTALLED, MAINTAINED, AND OPERATED. REQUIRED REGULAR MAINTENANCE ACTIONS FOR EQUIPMENT AND SYSTEMS SHALL BE CLEARLY STATED ON A READILY VISIBLE LABEL. THE LABEL SHALL INCLUDE THE TITLE OR PUBLICATION NUMBER FOR THE OPERATION AND MAINTENANCE MANUAL FOR THAT PERTICULAR MODEL AND TYPE OF PRODUCT.
12. CONTRACTOR SHALL MAINTAIN A COMPLETE AND ACCURATE SET OF RECORD DRAWINGS SHOWING ACTUAL INSTALLED LOCATIONS OF WORK. SUBMIT THESE DRAWINGS AS PART OF THE OPERATION AND MAINTENANCE MANUALS AT COMPLETION OF PROJECT.

MECHANICAL HVAC INSULATION NOTES AND SPECIFICATIONS

1. ALL RECTANGULAR SUPPLY, RETURN, AND TRANSFER DUCTWORK SHALL BE LINED WITH 1" DUCT LINER, UNLESS NOTED OTHERWISE.
2. ALL CONCEALED ROUND DUCTWORK SHALL BE WRAPPED WITH 1-½" DUCT WRAP WITH VAPOR BARRIER JACKET, MINIMUM R-6.
3. OUTSIDE AIR DUCTWORK SHALL BE WRAPPED WITH 2" DUCT WRAP WITH VAPOR BARRIER JACKET, MINIMUM R-8. NO DUCT LINER ALLOWED.
4. FLEXIBLE DUCTWORK SHALL BE WRAPPED WITH FIBERGLASS INSULATION WITH VAPOR BARRIER JACKET, MINIMUM R-6.
5. ALL EXHAUST DUCTWORK SHALL NOT BE REQUIRED TO BE INSULATED, UNLESS NOTED OTHERWISE.

MECHANICAL HVAC NOTES AND SPECIFICATIONS

1. DUCTWORK DIMENSIONS LISTED ON THE DRAWINGS ARE CLEAR, INSIDE DIMENSIONS. WHEN DUCT LINER IS REQUIRED, INCREASE SHEET METAL DIMENSIONS ACCORDINGLY.
2. FLEXIBLE DUCTWORK SHALL BE THE SAME SIZE AS THE NECK OF THE AIR DEVICE. FLEXIBLE DUCTWORK SHALL NOT EXCEED 8'-0" IN LENGTH. PROVIDE RIGID ROUND DUCTWORK FOR TAKEOFFS IN EXCESS OF 8'-0".
3. UNLESS INDICATED OTHERWISE, BRANCH TAKEOFFS ARE TO BE THE SAME SIZE AS THE DIFFUSER NECK SIZE INDICATED.
4. PROVIDE DUCT TRANSITIONS FROM EQUIPMENT CONNECTIONS TO DUCT SIZES INDICATED AS REQUIRED.
5. PROVIDE A FLEXIBLE CONNECTION TO THE INTAKE AND DISCHARGE OF ALL MECHANICAL EQUIPMENT HAVING ROTATING PARTS. FLEXIBLE CONNECTION SHALL COMPLY WITH ALL APPLICABLE CODES.
6. ALL DUCTWORK SHALL BE A MINIMUM 26 GAUGE SHEETMETAL, OR AS REQUIRED BY ALL APPLICABLE CODES. ALL DUCTWORK CROSSING RATED CORRIDORS SHALL BE A MINIMUM 24 GAUGE SHEETMETAL. DUCT GAUGES SHALL MEET OR EXCEED SMACNA STANDARDS.
7. ALL SUPPLY, RETURN AND EXHAUST DUCTWORK SHALL BE SEALED AIRTIGHT WITH DUCT SEALANT (SMACNA SEAL CLASS "A") ALONG ALL SEAMS AND JOINTS.
8. ALL UNLINED DUCTWORK THAT IS VISIBLE THROUGH THE AIR DEVICE SHALL BE PAINTED FLAT BLACK.
9. ALL ELBOWS, BOTH HORIZONTAL AND VERTICAL, SHALL BE LONG RADIUS ELBOWS WHEREVER POSSIBLE, OR SHALL HAVE TURNING VANES WHERE SHOWN.
10. BRANCH FITTINGS SERVING GRILLES AND DIFFUSERS SHALL BE CONICAL (OR 45° TAKEOFFS AS SHOWN ON DRAWINGS). PROVIDE WITH MANUAL VOLUME DAMPERS UNLESS THE AIR TERMINAL IS PROVIDED WITH AN OBD.
11. RECTANGULAR BRANCH DUCT TAKEOFFS SHALL HAVE 45° TAKEOFFS AND ROUND DUCT TAKEOFFS SHALL BE CONICAL.

DAO ARCHITECTURE
7230 Meade St.
Westminster, CO 80030
Phone: 720.273.0431
Email: dan@daoarch.com
Web: www.daoarch.com

The Ballard Group, Inc.
Mechanical Consulting Engineers
2525 S. Wadsworth Blvd, Suite 200
Lakewood, CO 80227
(303) 988-4514

Westminster Public Schools

Hodgkins ES Classroom Conversion
3475 W 67th Ave,
Denver, CO 80221


DAO No.:2021-033

November 12, 2021

Mechanical Cover Sheet

M0.0

N:\21127\21127-HVAC-R19.rvt
11/10/2021 3:58:16 PM

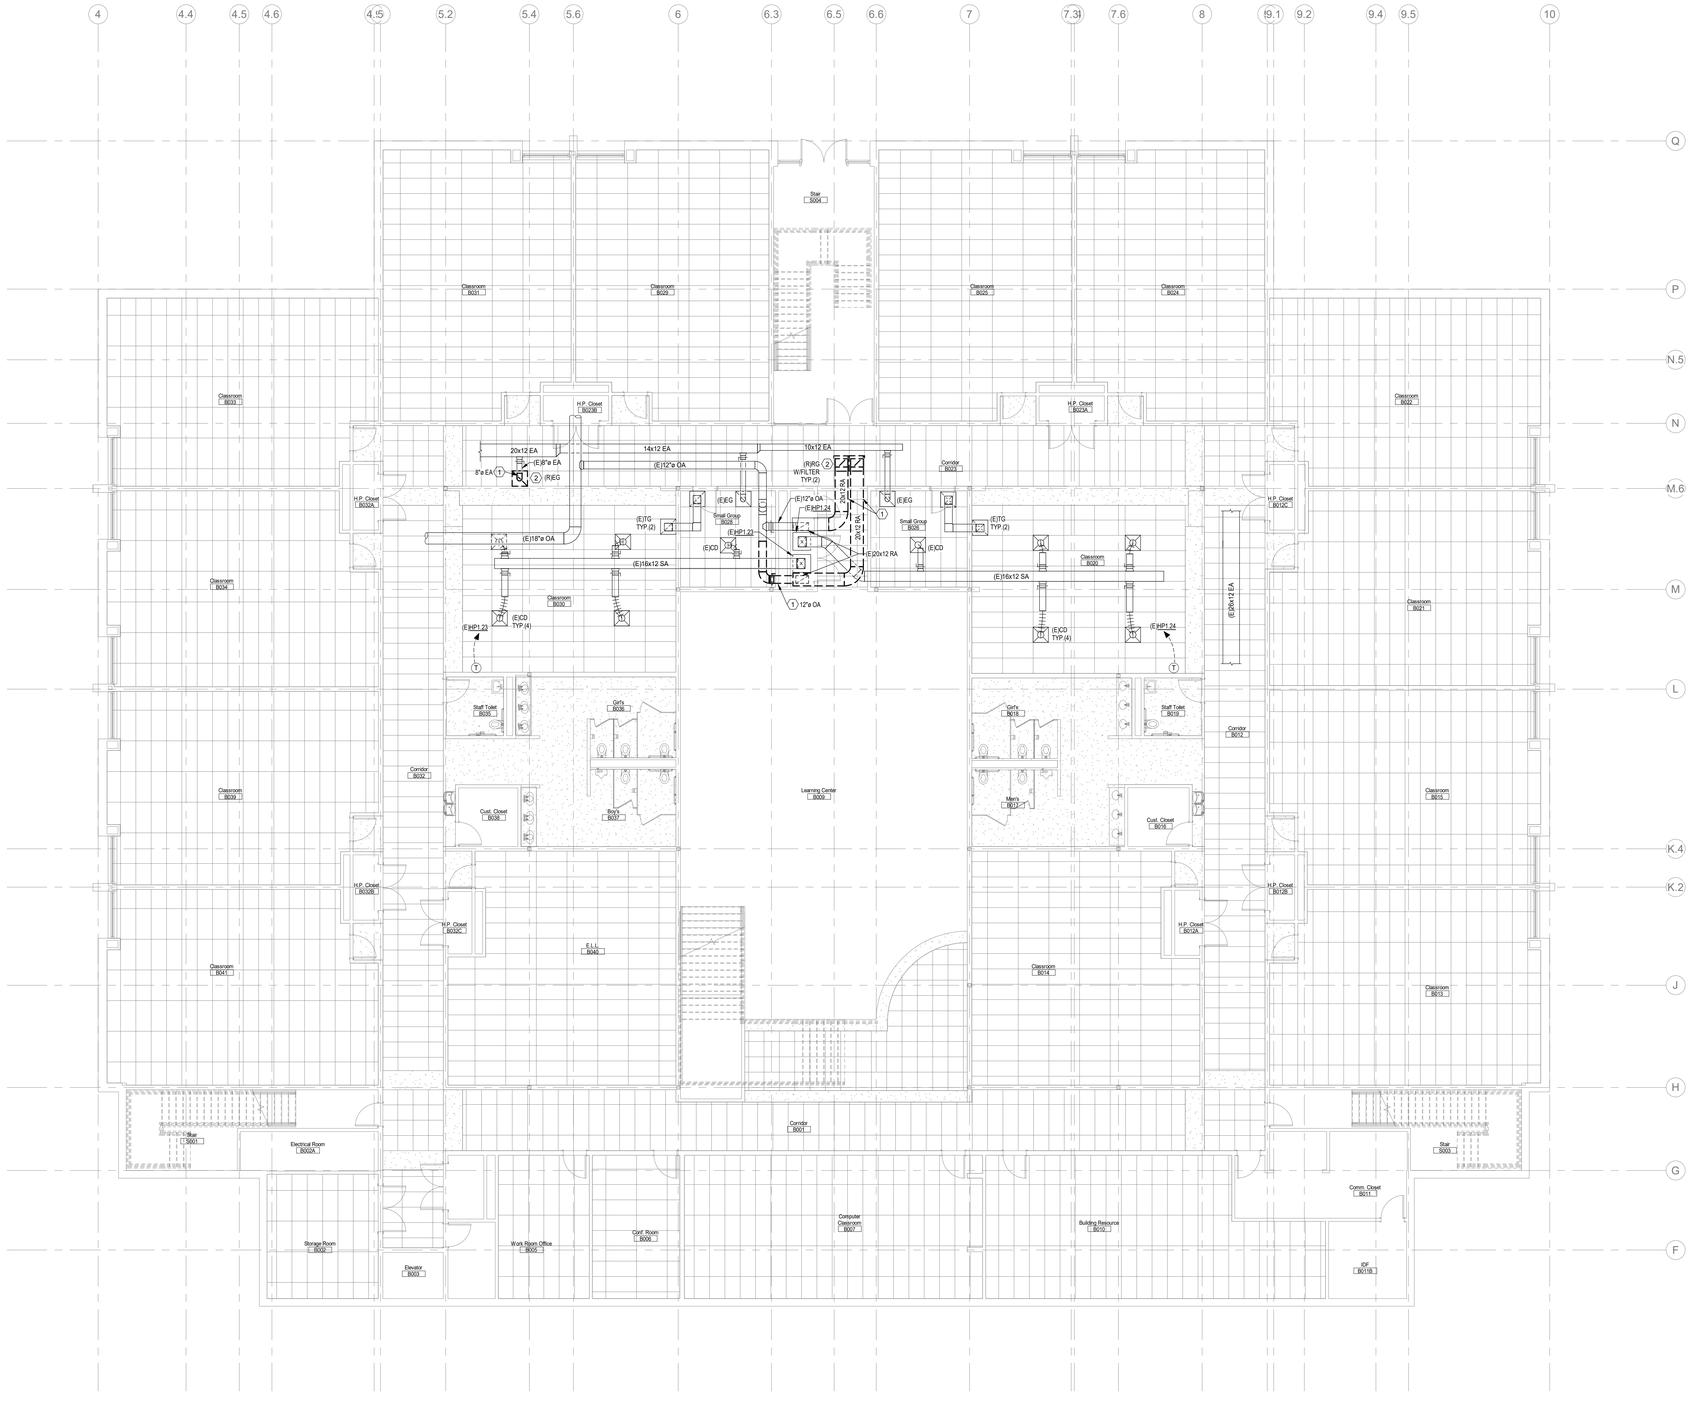

Lower Level HVAC Demolition Plan

SCALE: 1/8" = 1'-0"

HVAC DEMOLITION KEYNOTES:

1. REMOVE EXISTING DUCTWORK OF SIZE INDICATED ALONG WITH ALL HANGERS, SUPPORTS, INSULATION AND ACCESSORIES.
2. EXISTING AIR DEVICE TO BE REUSED AND RELOCATED. REFER TO NEW FLOOR PLAN FOR LOCATION.

DAO ARCHITECTURE

7230 Meade St.
Westminster, CO 80030

Phone: 720.273.0431
Email: dan@daoarch.com
Web: www.daoarch.com

The Ballard Group, Inc.
Mechanical Consulting Engineers
2525 S. Wadsworth Blvd, Suite 200
Lakewood, CO 80227
(303) 988-4514

Westminster Public Schools

Hodgkins ES Classroom Conversion
3475 W 67th Ave,
Denver, CO 80221


DAO No.:2021-033

November 12, 2021

Lower Level HVAC Demolition Plan

MD1.0

N:\21\2702127-HVAC-R19.rvt
11/10/2021 3:58:21 PM

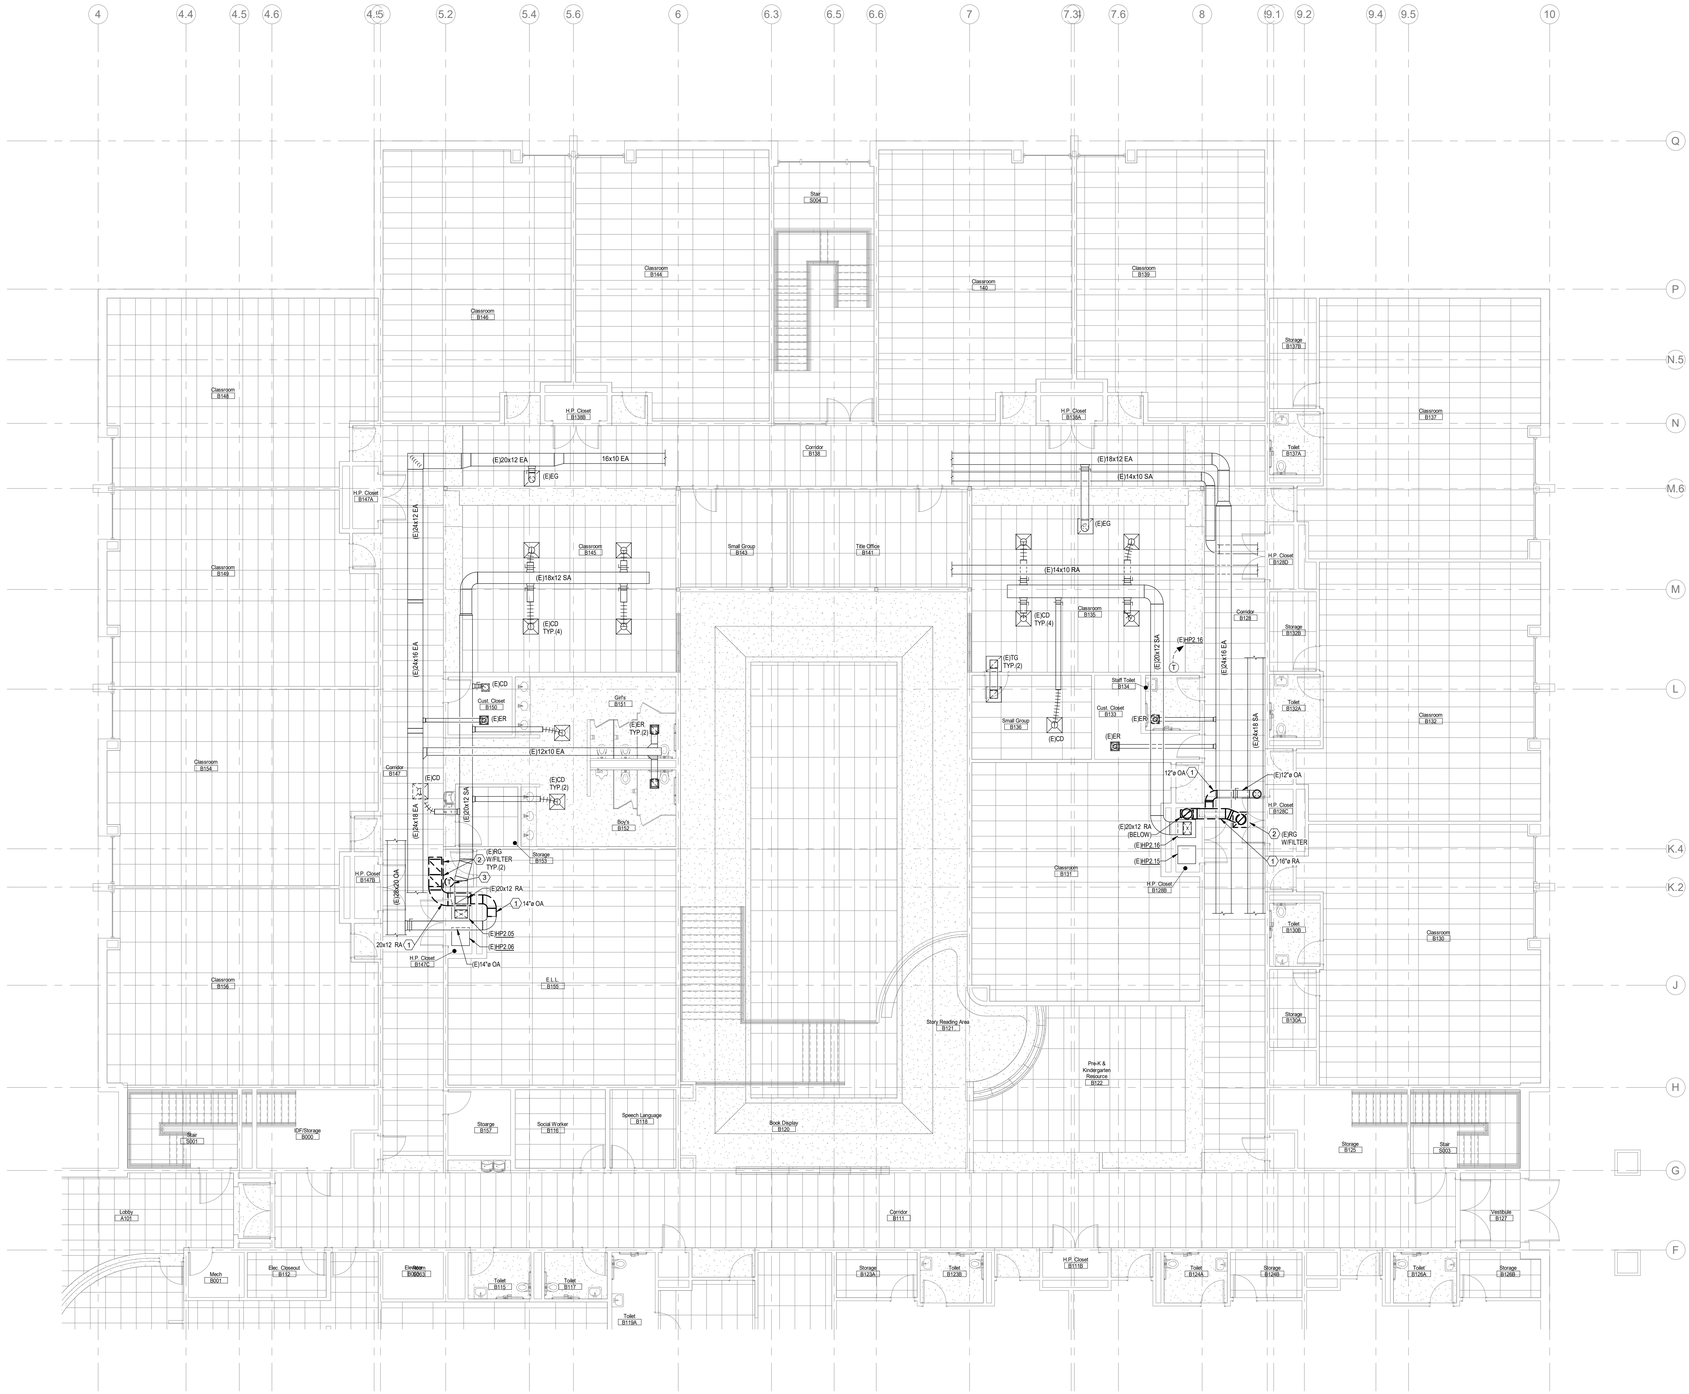

Main Level HVAC Demolition Plan

SCALE: 1/8" = 1'-0"

HVAC DEMOLITION KEYNOTES:

1. REMOVE EXISTING DUCTWORK OF SIZE INDICATED ALONG WITH ALL HANGERS, SUPPORTS, INSULATION AND ACCESSORIES.
2. EXISTING AIR DEVICE TO BE REUSED AND RELOCATED. REFER TO NEW FLOOR PLAN FOR LOCATION.
3. EXISTING THERMOSTAT TO BE REUSED AND RELOCATED. REFER TO NEW FLOOR PLAN FOR LOCATION. REMOVE ALL EXISTING CONTROL WIRING.

DAO ARCHITECTURE

7230 Meade St.
Westminster, CO 80030

Phone: 720.273.0431
Email: dan@daoarch.com
Web: www.daoarch.com

The Ballard Group, Inc.
Mechanical Consulting Engineers
2525 S. Wadsworth Blvd, Suite 200
Lakewood, CO 80227
(303) 988-4514

Westminster Public Schools

Hodgkins ES Classroom Conversion
3475 W 67th Ave,
Denver, CO 80221


DAO No.:2021-033

November 12, 2021

Main Level HVAC Demolition Plan

MD1.1

N:\21\272\127-HVAC-R19.rvt
11/10/2021 3:58:23 PM

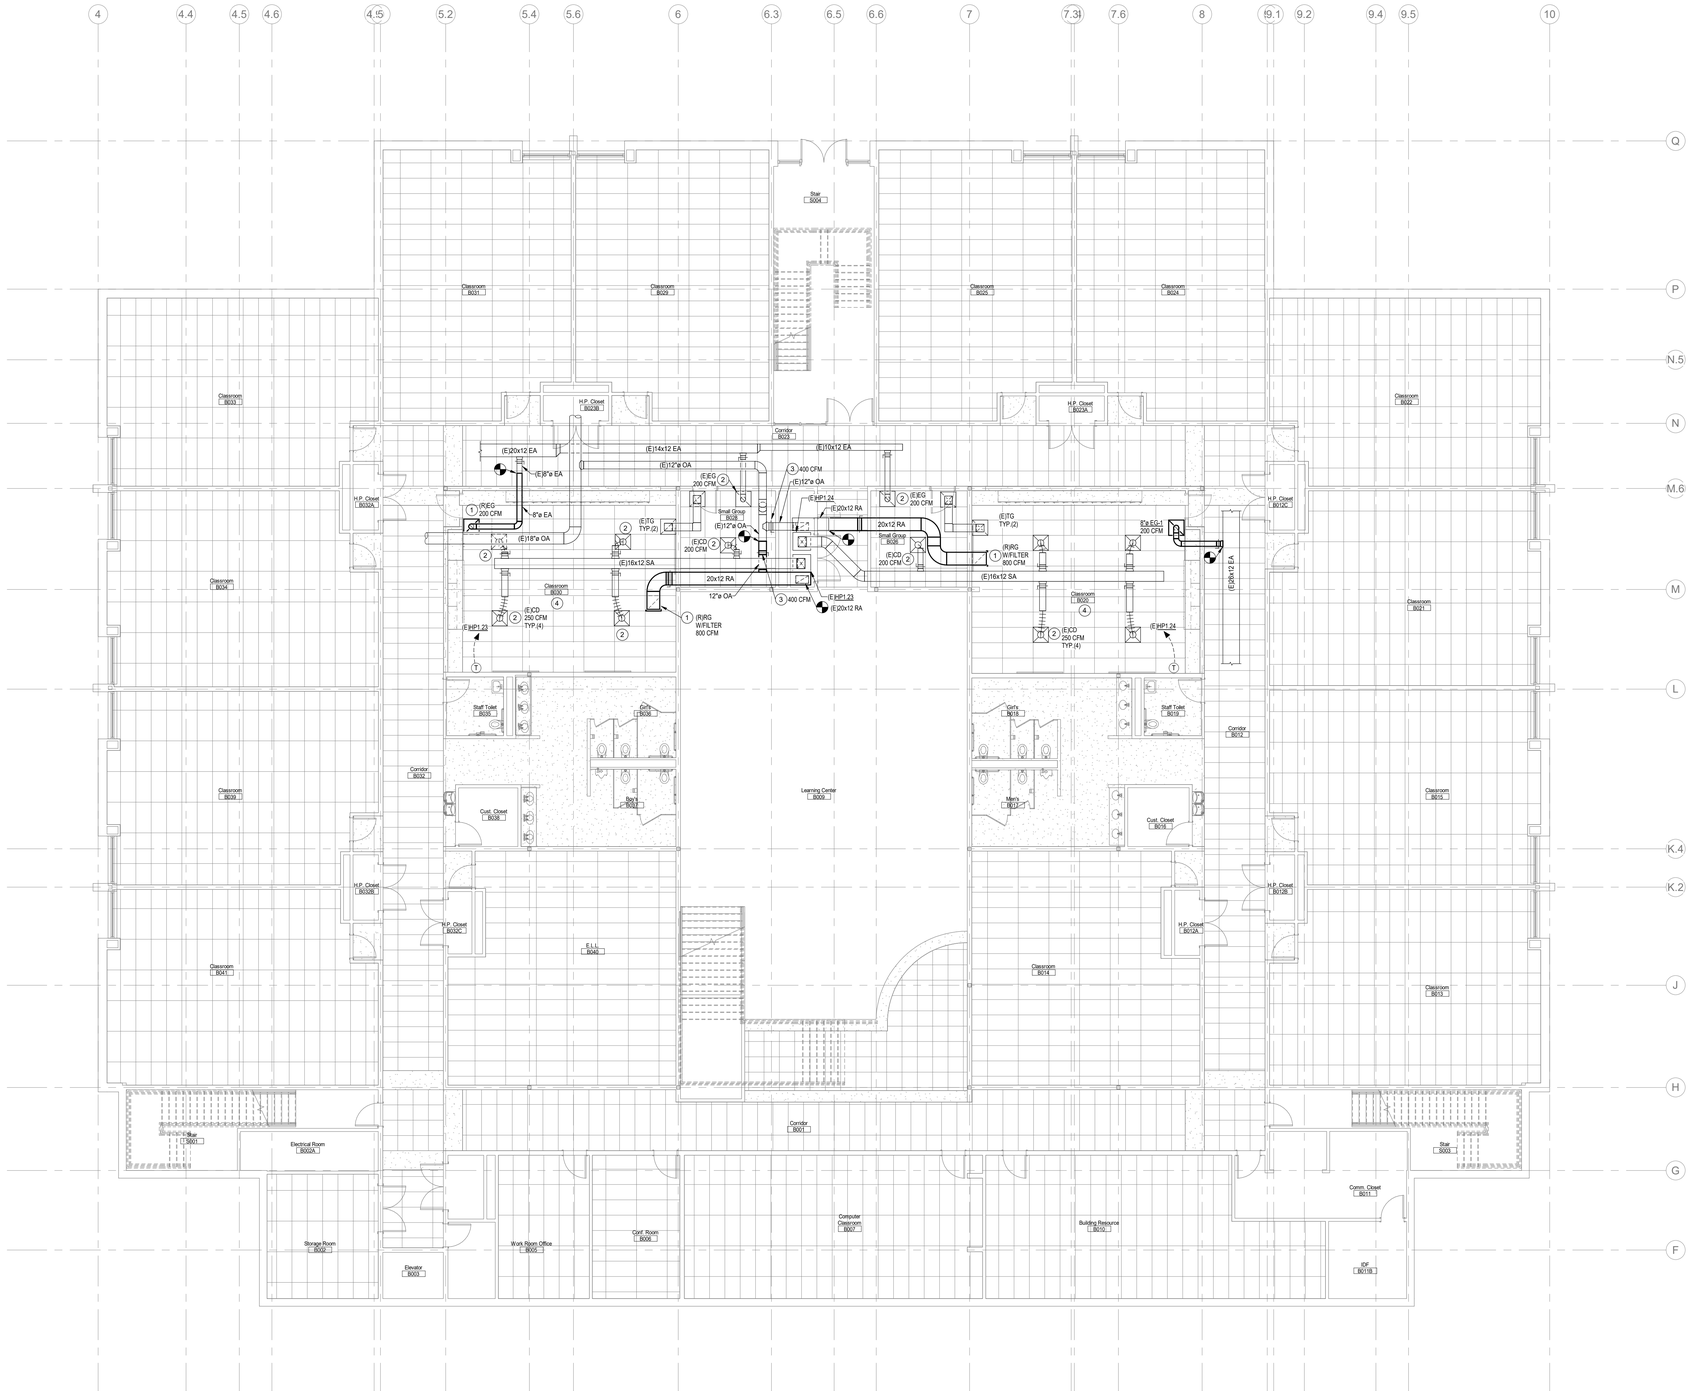

Lower Level HVAC Floor Plan

SCALE: 1/8" = 1'-0"

HVAC KEYNOTES:

1. RELOCATED AIR DEVICE OF TYPE INDICATED. REBALANCE TO AIRFLOW INDICATED.
2. EXISTING AIR DEVICE TO BE REINSTALLED INTO CEILING. REBALANCE TO AIRFLOW INDICATED.
3. BALANCE MANUAL VOLUME DAMPER TO AIRFLOW INDICATED.
4. OUTSIDE AIR REQUIRED: (700 SQFT x 0.12 + 18 PEOPLE x 10 CFM/PER / 0.8) = 330 CFM REQUIRED, 1,000 CFM SA x 0.40 OA FRAC = 400 CFM PROVIDED

DAO ARCHITECTURE

7230 Meade St.
Westminster, CO 80030

Phone: 720.273.0431
Email: dan@daoarch.com
Web: www.daoarch.com

The Ballard Group, Inc.
Mechanical Consulting Engineers
2525 S. Wadsworth Blvd, Suite 200
Lakewood, CO 80227
(303) 988-4514

Westminster Public Schools

Hodgkins ES Classroom Conversion
3475 W 67th Ave,
Denver, CO 80221


DAO No.:2021-033

November 12, 2021

Lower Level HVAC Floor Plan

M1.0

N:\21\272\127-HVAC-R19.rvt
11/10/2021 3:58:17 PM

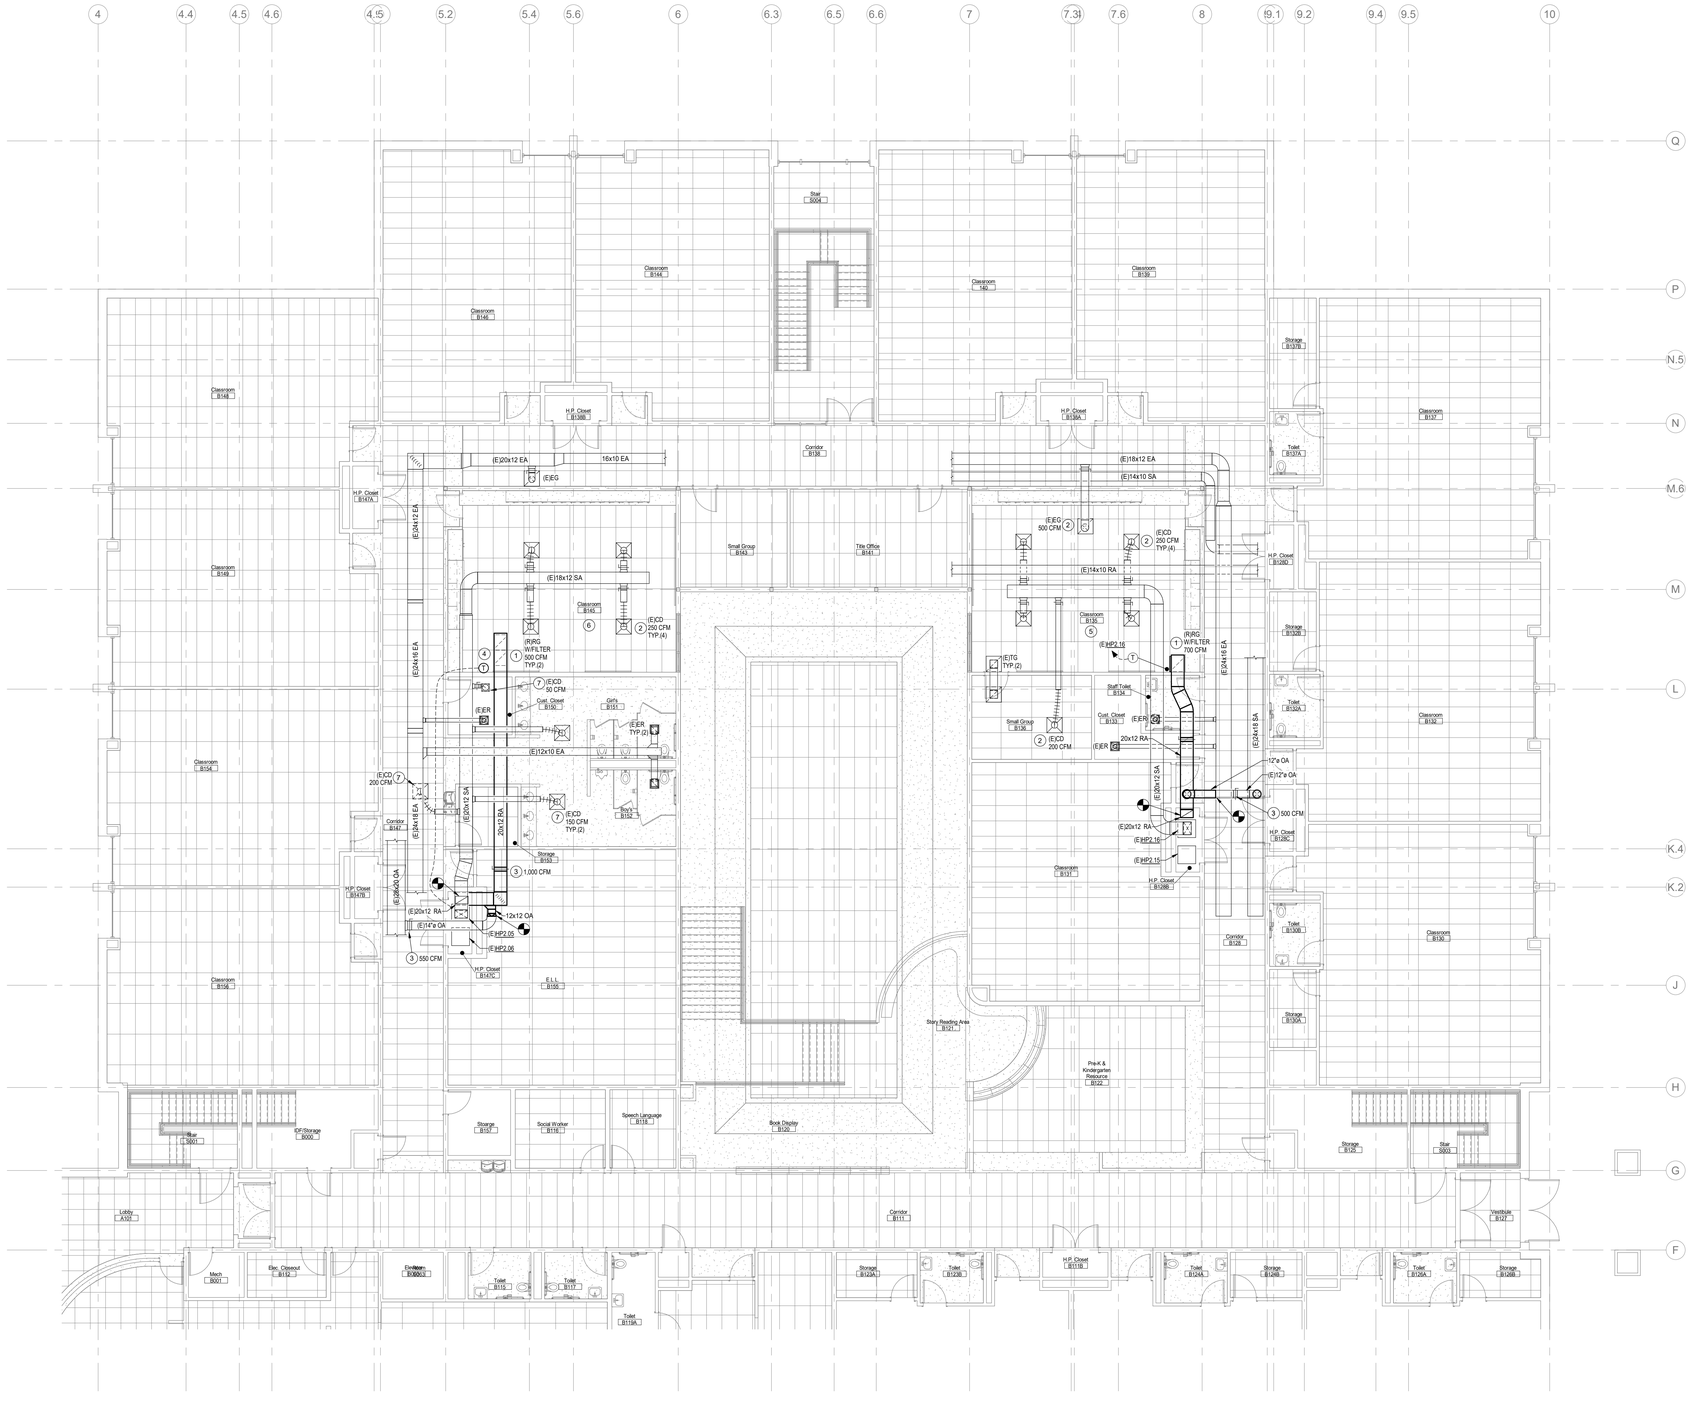

Main Level HVAC Floor Plan

SCALE: 1/8" = 1'-0"

HVAC KEYNOTES:

1. RELOCATED AIR DEVICE OF TYPE INDICATED. REBALANCE TO AIRFLOW INDICATED.
2. EXISTING AIR DEVICE TO BE REINSTALLED INTO CEILING. REBALANCE TO AIRFLOW INDICATED.
3. BALANCE MANUAL VOLUME DAMPER TO AIRFLOW INDICATED.
4. EXISTING THERMOSTAT RELOCATED TO LOCATION INDICATED. PROVIDE NEW CONTROL WIRING ROUTED TO EXISTING HEAT PUMP.
5. OUTSIDE AIR REQUIRED: (700 SQFT x 0.12 + 18 PEOPLE x 10 CFM/PER / 0.8) = 330 CFM REQUIRED, 1,000 CFM SA x 0.48 OA FRAC = 480 CFM PROVIDED
6. OUTSIDE AIR REQUIRED: (700 SQFT x 0.12 + 18 PEOPLE x 10 CFM/PER / 0.8) = 330 CFM REQUIRED, 1,000 CFM SA x 0.55 OA FRAC = 550 CFM PROVIDED
7. REBALANCE EXISTING AIR DEVICE.

DAO ARCHITECTURE

7230 Meade St.
Westminster, CO 80030

Phone: 720.273.0431
Email: dan@daoarch.com
Web: www.daoarch.com

The Ballard Group, Inc.
Mechanical Consulting Engineers
2525 S. Wadsworth Blvd, Suite 200
Lakewood, CO 80227
(303) 988-4514

Westminster Public Schools

Hodgkins ES Classroom Conversion
3475 W 67th Ave,
Denver, CO 80221

DAO No.:2021-033

November 12, 2021

Main Level HVAC Floor Plan

M1.1

N:\21127\21127-HVAC-R19.rvt
11/10/2021 3:58:20 PM

ABBREVIATIONS LEGEND
(Not all symbols listed below are used on these drawings)

SYMBOL	DESCRIPTION	SYMBOL	DESCRIPTION
A	AMPERES	MCP	MOTOR CIRCUIT PROTECTOR
AC	ABOVE COUNTER; MOUNT HORIZONTALLY TO CENTERLINE OF DEVICE, +6" ABOVE COUNTER OR BACK SPLASH	MEC	SEE MECHANICAL EQUIPMENT SCHEDULE
AFF	ABOVE FINISHED FLOOR	MIN	MINIMUM
AFG	ABOVE FINISHED GRADE	MLO	MAIN LUGS ONLY
ANN	ANNUNCIATOR	MTS	MANUAL TRANSFER SWITCH
ARF	ABOVE RAISED FLOOR	NC	NORMALLY CLOSED
ASSD	AIR SAMPLING SMOKE DETECTION	NIC	NOT IN CONTRACT
ATS	AUTOMATIC TRANSFER SWITCH	NL	NIGHT LIGHT
BFG	BELOW FINISHED GRADE	NO	NORMALLY OPEN
C	CONDUIT	NTS	NOT TO SCALE
CATV	CABLE TELEVISION	OC	ON CENTER
CB	CIRCUIT BREAKER	OFCI	OWNER FURNISHED, CONTRACTOR INSTALLED
CCTV	CLOSED CIRCUIT TELEVISION	OFOI	OWNER FURNISHED, OWNER INSTALLED
(E)	EXISTING	OSWF	ON SITE WORK FORCE
EM	EMERGENCY	PB	PULL BOX
EMDC	EMERGENCY MAIN DISTRIBUTION CENTER	SB	STAND-BY
EP	EXPLOSION PROOF	SDC	SUB-DISTRIBUTION CENTER
EPO	EMERGENCY POWER OFF	TP	TAMPER PROOF
EVO	EMERGENCY VENTILATION ON/OFF	TVSS	TRANSIENT VOLTAGE SURGE SUPPRESSER
EWC	ELECTRIC WATER COOLER	TYP	TYPICAL
FA	FIRE ALARM	UF	UNDER FLOOR
G	GROUND	UG	UNDER GROUND
GCP	GENERATOR CONTROL PANEL	UON	UNLESS OTHERWISE NOTED
GFCI	GROUND FAULT CIRCUIT INTERRUPTER	UPS	UNINTERRUPTIBLE POWER SUPPLY
HOA	HAND OFF AUTOMATIC	V	VOLTS
IG	ISOLATED GROUND	VFD	VARIABLE FREQUENCY DRIVE
MAX	MAXIMUM	W/	WITH
MCB	MAIN CIRCUIT BREAKER	W/O	WITHOUT
MCC	MOTOR CONTROL CENTER	WP	WEATHER PROOF
MDC	MAIN DISTRIBUTION CENTER	XFMR	TRANSFORMER

CONTROLS LEGEND
(Not all symbols listed below are used on these drawings)

SYMBOL	DESCRIPTION	SYMBOL	DESCRIPTION
S_a	SINGLE POLE SWITCH (SUBSCRIPT DENOTES SWITCHING)	S_{VS}	VARIABLE SPEED/SPEED CONTROLLER SWITCH
S_2	TWO POLE SWITCH	S_{EP}	EXPLOSION PROOF SWITCH
S_3	THREE-WAY SWITCH	S_{TO}	THERMAL OVERLOAD SWITCH
S_4	FOUR-WAY SWITCH	S_{MC}	MOMENTARY CONTACT SWITCH
S_K	KEY OPERATED SWITCH	S	COMBINATION SWITCH AND DUPLEX RECEPTACLE
S_M	MANUAL SWITCH, HORSEPOWER RATE	P	PHOTOCELL
S_D	DIMMER SWITCH		PUSH BUTTON
S_{PI}	SWITCH WITH PILOT LIGHT (PILOT LIGHT IS 'ON' WHEN SWITCH IS 'ON')	TC	TIME CLOCK
S_P	SWITCH WITH PILOT LIGHT LOCATOR (CONTINUOUSLY LIGHTED HANDLE)		OCCUPANCY SENSOR - WALL MOUNTED IR=INFRARED, US=ULTRASONIC, DT=DUAL TECHNOLOGY
S_{LV}	LOW VOLTAGE SWITCH		

TECHNOLOGY LEGEND
(Not all symbols listed below are used on these drawings)

SYMBOL	DESCRIPTION		SYMBOL	DESCRIPTION	
	WALL FIELD		# XXX	CEILING MOUNTED OUTLET (# = QTY OF CABLES; XXX= SEE BELOW)	
	TELECOM GROUND BAR			AV = AUDIO VISUAL	SEC = SECURITY
	WIRE BASKET TRAY			WAP=WIRELESS ACCESS POINT	PRJ = PROJECTOR
	CABLE TRAY				
	J-HOOK PATHWAY		T XXX	DATA POWER POLE (XXX = SEE BELOW)	
#	FLOOR SPACE BOX DATA OUTLET(# = QTY OF CABLES)			SEC = SECURITY	SR = SURFACE RACEWAY
#	POKE-THRU (# = QTY OF CABLES)		ZZ	TELEVISION COAXIAL CABLE (ZZ = ELEVATION)	
# XXX ZZ	DATA OUTLET (# = QTY OF CABLES; XXX = SEE BELOW ZZ = ELEVATION)			CEILING MOUNTED TELEVISION COAXIAL OUTLET	
	D = MEDICAL/SUPPLY DISPENSER	RED = RED PHONE	J	FLOOR JBOX	
	EEG = EEG NETWORK	T = TRANSLATION PHONE	J XXX	POKE THRU; (XXX = SEE BELOW)	
	EP = EMERGENCY PHONE	TC = TIME CLOCK		FF = FURNITURE FEED	AV = AUDIO VISUAL
	F = FACP	W = WALL PHONE	J XXX ZZ	WALL MOUNTED JBOX (XXX = SEE BELOW; ZZ = ELEVATION)	
	POS = POINT OF SALE	AV = AUDIO VISUAL		CLG = CEILING	AV = AUDIO VISUAL
	RAD = RADIOLOGY NETWORK	PRT = PRINTER	PB YY	PULLBOX (YY = SIZE)	
	SR = SURFACE RUNWAY	MFP = MULTI FUNCTIONS PRINTER	C XXX	CLOCK OUTLET (XXX = SEE BELOW)	
	BAS = BUILDING AUTOMATION SYSTEM	WP = WEATHER PROOF		DS = DOUBLE SIDED	DIGITAL (PROVIDE 1 CAT 6 CONNECTION)
	SCH = SCHEDULER	SEC = SECURITY		A = ANALOG	
	CP = CONTROL PANEL	CLK = CLOCK	XXX	COMBINATION CLOCK/SPEAKER OUTLET (XXX = SEE BELOW)	
	RIO = ROUGH IN ONLY			A = ANALOG	D = DIGITAL
			C	CEILING MOUNTED CLOCK	
			DAS	DISTRIBUTED ANTENNA SYSTEM	
			WAP	WIRELESS ACCESS POINT ENCLOSURE	
				EQUIPMENT RACK	
				WIRE MANAGER	
				CABINET	

AUDIO VISUAL LEGEND
(Not all symbols listed below are used on these drawings)

SYMBOL	DESCRIPTION	SYMBOL	DESCRIPTION	
##	CEILING MOUNTED SPEAKER (## = TYPE #)	J XXX	FLOOR POKE THRU (XXX = SEE BELOW)	
	WALL MOUNTED SPEAKER		CTRL = CONTROL UNIT	I/O = INPUT/OUTPUT PLATE
(XX)	DISPLAY (XX = SIZE OF SCREEN * = ELEVATION)	SSS	SOUND SHOWER SPEAKER	
*	SCHEDULER : (* = ELEVATION)	PS ZZ	PARTITION SENSOR (ZZ = ELEVATION)	
*	CONTROL UNIT : (* = ELEVATION)	ZZ	TELEVISION COAXIAL CABLE (ZZ = ELEVATION)	
*	INPUT/OUTPUT PLATE : (* = ELEVATION)		CEILING MOUNTED TELEVISION COAXIAL OUTLET	
*	MICROPHONE OUTLET : (* = ELEVATION)	VC	VOLUME CONTROL	
	PROJECTOR	HDMI	HIGH DEFINITION MULTIMEDIA INTERFACE	
		##	CEILING MOUNTED MICROPHONE (## = TYPE #)	

ONE-LINE DIAGRAM LEGEND
(Not all symbols listed below are used on these drawings)

SYMBOL	DESCRIPTION	SYMBOL	DESCRIPTION
	DISCONNECT SWITCH	A	PANELBOARD "A"
	DISCONNECT SWITCH, FUSED	PM	EM=ENERGY METER, PM=POWER METER, CM=CIRCUIT MONITOR
	CIRCUIT BREAKER	VS	VOLTMETER TEST SWITCH
	FUSE	AS	AMMETER TEST SWITCH
	GROUND	V	VOLTMETER
T ##	STEP DOWN TRANSFORMER, ## INDICATES KVA	A	AMMETER
TK ##	K-RATED STEP DOWN TRANSFORMER ## INDICATES KVA, # INDICATES K RATING	XXX	SEE FEEDER/MEC/TRANSFORMER SCHEDULES FOR FEEDER SIZE
	CURRENT TRANSFORMER	G	ENGINE GENERATOR
	POTENTIAL TRANSFORMER		CONTACTOR/RELAY/CAPACITOR (AS NOTED)
OR	SERVICE ENTRANCE TRANSFORMER		TRANSFER SWITCH - ATS=AUTOMATIC, MTS=MANUAL
	METER	GFI	GROUND FAULT INTERRUPTER
	EQUIPMENT ENCLOSURE	SPD	SURGE PROTECTIVE DEVICE
	SERVICE WEATHERHEAD	ST	SHUNT TRIP
SCA	SHORT CIRCUIT CURRENT AVAILABLE		TERMINATIONS LB=LOAD BREAK, NLB=NO LOAD BREAK
x	KIRK KEY INTERLOCK, SUBSCRIPT INDICATES INTERLOCKED GROUP		DRAW-OUT DEVICE
x	ELECTRICAL INTERLOCK, SUBSCRIPT INDICATES INTERLOCKED GROUP		PLUG-IN DEVICE
	MECHANICAL INTERLOCK	EO	ELECTRICALLY OPERATED

POWER LEGEND
(Not all symbols listed below are used on these drawings)

SYMBOL	DESCRIPTION	SYMBOL	DESCRIPTION
	SINGLE RECEPTACLE	PM	PLUG MOLD (MULTI-OUTLET ASSEMBLY)
	DUPLEX RECEPTACLE	WM	WIREMOLD (SURFACE RACEWAY)
	DOUBLE DUPLEX RECEPTACLE		CONDUIT CONCEALED
	DUPLEX RECEPTACLE, HALF SWITCHED		CONDUIT EXPOSED
GLC	DUPLEX RECEPTACLE, CEILING MOUNTED		CONDUIT, UNDERGROUND OR CONCEALED IN FLOOR AS ALLOWED PER SPECIFICATIONS
	DUPLEX RECEPTACLE, FLOOR MOUNTED		CONDUIT TURNING DOWN
	DOUBLE DUPLEX RECEPTACLE, FLOOR MOUNTED		CONDUIT TURNING UP
	SPECIAL RECEPTACLE		CONDUIT CAPPED
	SPECIAL RECEPTACLE, FLOOR MOUNTED	A-1,3,5	BRANCH CIRCUIT HOME RUN, NUMBER OF ARROWS INDICATES NUMBER OF CIRCUITS, SUBSCRIPTS INDICATE PANEL & CIRCUITS
	JUNCTION BOX, FLOOR OR CEILING MOUNTED		GROUND BAR
	JUNCTION BOX, WALL MOUNTED		MAIN SWITCHBOARD/DISTRIBUTION CENTER
M	MOTOR	T	TRANSFORMER
	DISCONNECT SWITCH (NON-FUSED)	CT	CURRENT TRANSFORMER
	DISCONNECT SWITCH (FUSED)	T	THERMOSTAT
	VARIABLE SPEED DRIVE WITH DISCONNECT	GANN	GENERATOR ANNUNCIATOR PANEL
	ENCLOSED CIRCUIT BREAKER	A-1	SHADING INDICATES EMERGENCY SYSTEM TEXT INDICATES PANEL AND CIRCUIT DESIGNATION
S	TOGGLE SWITCH	M	UTILITY METER
	ELECTRICAL PANELBOARD, CONTROL PANEL, OR OTHER CABINET AS NOTED		

REFERENCE SYMBOLS LEGEND
(Not all symbols listed below are used on these drawings)

SYMBOL	DESCRIPTION	SYMBOL	DESCRIPTION
	KEY NOTE REFERENCE		KITCHEN/OWNER/MEDICAL EQUIPMENT REFERENCE
UPA-#	TYPICAL CIRCUIT NUMBER		EXISTING TO REMAIN
TGM	TYPICAL LUMINAIRE TYPE		EXISTING TO BE REMOVED
	TYPICAL ROOM REFERENCE (TOP = RM #, BOTTOM = FLR)		EXISTING TO BE RELOCATED
MR	MECHANICAL EQUIPMENT REFERENCE		EXISTING TO REMAIN - REPLACE DEVICE
LC1	LIGHTING CONTROL / EQUIPMENT REFERENCE		EXISTING TO BE REMOVED AND REPLACED

ONE-LINE DIAGRAM LEGEND
(Not all symbols listed below are used on these drawings)

SYMBOL	DESCRIPTION	SYMBOL	DESCRIPTION
	DISCONNECT SWITCH	A	PANELBOARD "A"
	DISCONNECT SWITCH, FUSED	PM	EM=ENERGY METER, PM=POWER METER, CM=CIRCUIT MONITOR
	CIRCUIT BREAKER	VS	VOLTMETER TEST SWITCH
	FUSE	AS	AMMETER TEST SWITCH
	GROUND	V	VOLTMETER
T ##	STEP DOWN TRANSFORMER, ## INDICATES KVA	A	AMMETER
TK ##	K-RATED STEP DOWN TRANSFORMER ## INDICATES KVA, # INDICATES K RATING	XXX	SEE FEEDER/MEC/TRANSFORMER SCHEDULES FOR FEEDER SIZE
	CURRENT TRANSFORMER	G	ENGINE GENERATOR
	POTENTIAL TRANSFORMER		CONTACTOR/RELAY/CAPACITOR (AS NOTED)
OR	SERVICE ENTRANCE TRANSFORMER		TRANSFER SWITCH - ATS=AUTOMATIC, MTS=MANUAL
	METER	GFI	GROUND FAULT INTERRUPTER
	EQUIPMENT ENCLOSURE	TVSS SPD	TRANSIENT VOLTAGE SURGE SUPPRESSER
	SERVICE WEATHERHEAD	ST	SHUNT TRIP
SCA	SHORT CIRCUIT CURRENT AVAILABLE		TERMINATIONS LB=LOAD BREAK, NLB=NO LOAD BREAK
x	KIRK KEY INTERLOCK, SUBSCRIPT INDICATES INTERLOCKED GROUP		DRAW-OUT DEVICE
x	ELECTRICAL INTERLOCK, SUBSCRIPT INDICATES INTERLOCKED GROUP		PLUG-IN DEVICE
	MECHANICAL INTERLOCK	EO	ELECTRICALLY OPERATED

POWER PLAN NOTES:

1. MAKE ALL FINAL ELECTRICAL CONNECTIONS TO EQUIPMENT REQUIRING ELECTRICAL CONNECTION. THIS SHALL INCLUDE BUT NOT BE LIMITED TO ALL MECHANICAL AND OTHER EQUIPMENT INCLUDED IN THIS PROJECT.
2. CIRCUITS MAY BE COMBINED INTO HOMERUNS OF UP TO SIX (6) CURRENT CARRYING CONDUCTORS, INCLUDING NEUTRALS, UNLESS OTHERWISE INDICATED. WHERE CIRCUITS ARE COMBINED WITHIN A SINGLE CONDUIT, PROVIDE STRIPING FOR FULL LENGTH OF NEUTRAL CONDUCTOR INSULATION TO MATCH THE COLOR CODE OF THE ASSOCIATED PHASE CONDUCTOR. SEE SPECIFICATION FOR COLOR CODES.

ONE-LINE DIAGRAM NOTES:

1. PANELBOARDS INDICATED ON ONE LINE DIAGRAMS DO NOT SHOW ALL BRANCH CIRCUITS. REFER TO PANELBOARD SCHEDULE(S).
2. EXISTING ONE-LINE DIAGRAM TAKEN FROM OWNER FURNISHED DRAWINGS. EXISTING INFORMATION SHOWN OTHER THAN LOCATIONS IMPACTED BY NEW WORK HAS NOT BEEN VERIFIED.

DEMOLITION NOTES:

1. UNLESS NOTED OTHERWISE, BOLD ITEMS INDICATE EQUIPMENT, DEVICES, ETC. TO BE REMOVED. SEE SPECIFICATION SECTION 260500 FOR REMODEL/DEMOLITION DETAILED REQUIREMENTS.
2. DEMOLITION DRAWINGS MAY NOT SHOW EVERY ITEM TO BE DEMOLISHED. CONTRACTOR SHALL VISIT SITE TO DETERMINE AND COORDINATE THE EXACT EXTENT OF DEMOLITION TO FACILITATE ALL WORK INDICATED BY THE CONTRACT DOCUMENTS PRIOR TO QUOTATION. NO EXTRAS WILL BE ALLOWED FOR WORK REQUIRED TO ACHIEVE THE END RESULT AS INDICATED BY THE CONTRACT DOCUMENTS. REWORK EXISTING TERMINATIONS, CONNECTIONS, CONDUIT, WIRING, ETC. TO ACCEPT NEW WORK. MAINTAIN CIRCUIT CONTINUITY TO EXISTING CIRCUITS AND DEVICES TO REMAIN OR REMODEL/DEMOLITION DETAILED REQUIREMENTS TO BE RELOCATED. PRIOR TO COMMENCEMENT OF ANY DEMO WORK, CONFIRM EXISTING CONDITIONS AND NOTIFY ENGINEER OF ANY DISCREPANCIES FOR RESOLUTION.
3. ALL ITEMS IDENTIFIED TO BE REMOVED SHALL BE REMOVED IN THEIR ENTIRETY INCLUDING ALL WIRING AND EXPOSED CONDUIT AND CONDUIT SUPPORTS BACK TO POINT OF ORIGIN OR NEXT DEVICE TO REMAIN. REMOVED ITEMS SHALL BE TURNED OVER TO THE OWNER, UNLESS NOTED OTHERWISE, AND STORED IN THE AREA DESIGNATED BY THE OWNER. REMOVE FROM SITE AND LEGALLY DISPOSE OF ALL ITEMS THE OWNER CHOOSES NOT TO ACCEPT.
4. WHERE EXISTING CONDUITS ARE SHOWN TO BE REMOVED AND HAVE BEEN ROUTED IN CONCRETE FLOOR SLABS, CONCRETE WALLS OR CONCRETE CEILINGS, THEY SHALL BE CUT BACK FLUSH WITH CONCRETE. FILL WITH GROUT TO ACHIEVE A SMOOTH AND EVEN FINISH FLUSH WITH CONCRETE SURFACE AFTER CONDUCTORS HAVE BEEN REMOVED.
5. REUSE EXISTING CONDUIT WHERE CURRENT NEC AND LOCAL CODE REQUIREMENTS ARE MAINTAINED. PROVIDE NEW CONDUIT AND WIRE FOR NEW INSTALLATIONS AND EXTENSION OF EXISTING INSTALLATIONS. REUSE EXISTING CONDUIT IN PLACE, DO NOT REINSTALL EXISTING CONDUIT. PROVIDE LABELING PER SPECIFICATIONS FOR REUSED CONDUIT.
6. RELOCATED EQUIPMENT AND DEVICES ARE TO BE CLEANED OF ALL FOREIGN MATERIAL. REPLACE EQUIPMENT OR DEVICES WHICH ARE DEFECTIVE OR DAMAGED DURING RELOCATION.
7. WHERE EXISTING DEVICES, SWITCHES, MOTOR CONNECTIONS, ETC. ARE TO BE REMOVED FROM WALLS WHICH ARE REMAINING, WALLS SHALL BE PATCHED TO MATCH ORIGINAL FINISH. BLANK COVERPLATES OVER EXISTING BOXES ARE NOT ACCEPTABLE, UNLESS NOTED OTHERWISE.

GENERAL NOTES:

1. FOR REMODELING, WORK INCLUDED IS DENOTED IN BOLD. EXISTING CONDITIONS TO REMAIN ARE DENOTED LIGHTLY.
2. PROTECT STRUCTURE AND OWNER EQUIPMENT FROM DAMAGE. IMMEDIATELY REPLACE OR REPAIR, TO ORIGINAL CONDITION, DAMAGE CAUSED BY THE CONTRACTOR WHETHER EQUIPMENT APPEARS TO BE CURRENTLY IN USE OR NOT, UNLESS WRITTEN AUTHORIZATION FROM THE OWNER INDICATED OTHERWISE. PREPARE LISTING OF ALL EXISTING DAMAGED ITEMS AND SUBMIT TO OWNER PRIOR TO BEGINNING WORK.
3. INSTALL CONDUIT CONCEALED IN FINISHED AREAS UNLESS OTHERWISE NOTED. PAINT EXPOSED CONDUIT TO MATCH EXISTING FINISHES WITHIN THE SURROUNDING AREA.
4. FIRE SEAL ALL FIRE RATED WALL AND FLOOR PENETRATIONS. REFER TO ARCHITECTURAL DRAWINGS FOR FIRE RATED WALLS.
5. COORDINATE EXACT REQUIREMENTS AND LOCATIONS OF MECHANICAL EQUIPMENT WITH MECHANICAL DRAWINGS AND MECHANICAL CONTRACTOR PRIOR TO ROUGH-IN AND ORDERING MATERIALS OR EQUIPMENT.
6. A DETAILED WRITTEN METHOD OF PROCEDURE IS REQUIRED WHEN A CONSTRUCTION ACTIVITY OR AN OUTAGE AFFECTS THE SAFETY OF OCCUPANTS, TELEPHONE/DATA/FIRE ALARM EQUIPMENT OR COMPONENTS OF ANY SYSTEM WHICH SUPPORTS THIS EQUIPMENT OR ESSENTIALLY AFFECTS THE BUILDING MANAGEMENT, OPERATIONS OR SECURITY. SEE SPECIFICATIONS FOR ADDITIONAL INFORMATION.
7. EXISTING INFORMATION SHOWN ON THE DRAWINGS HAS BEEN TAKEN FROM OWNER FURNISHED DRAWINGS AND/OR LIMITED FIELD OBSERVATIONS. CATOR, RUMA & ASSOCIATES IS NOT RESPONSIBLE FOR THE ACCURACY OF ANY INFORMATION OR THE ADEQUACY, SAFETY AND CONFORMANCE TO CURRENT PREVAILING CODES OF ANY WORK SHOWN AS EXISTING ON THESE DRAWINGS.
8. PROVIDE SEPARATE INSULATED GROUNDING CONDUCTOR IN ALL FEEDER, HOMERUN AND BRANCH CIRCUITS.

TECHNOLOGY PLAN NOTES:

1. PROVIDE J-HOOK TYPE CABLE SUPPORTS EVERY 4'-0" TO 5'-0" IN OPEN OR ACCESSIBLE CEILING SPACE AS REQUIRED TO SUPPORT CABLES IN ROUTE TO CABLE TRAY OR CONDUIT PATHWAY TO TELECOMMUNICATIONS ROOM. ROUTE CABLE SUPPORTS SUCH THAT CABLE VISIBILITY WILL BE MINIMIZED IN ANY OPEN CEILING AREAS.

ROUGH-IN AND PATHWAY NOTES:

1. PROVIDE 4-11/16" x 4-11/16" x 2-7/8" OUTLET BOX AND SINGLE GANG MUD RING FOR ALL TELE/DATA OUTLETS. ROUTE 1" CONDUIT FROM EACH OUTLET TO ABOVE ACCESSIBLE CEILING UNLESS OTHERWISE NOTED. PROVIDE INSULATED THROAT CONNECTOR ON CONDUIT END. KEEP ALL EXPOSED CONDUITS TIGHT TO STRUCTURE.
2. PROVIDE 4-11/16" x 4-11/16" x 2-7/8" OUTLET BOX AND TWO-GANG MUD RING FOR ALL AV DEVICE AND DISPLAY BACKBOX LOCATIONS UNLESS OTHERWISE NOTED. ROUTE 1-1/4" CONDUIT TO ABOVE ACCESSIBLE CEILING UNLESS OTHERWISE NOTED. PROVIDE INSULATED THROAT CONNECTOR ON CONDUIT END. KEEP ALL EXPOSED CONDUITS TIGHT TO STRUCTURE.
3. COORDINATE AND VERIFY EXACT MOUNTING LOCATIONS OF WALL, CEILING, AND FLOOR DEVICES WITH ARCHITECTURAL ELEVATIONS AND ANY FURNITURE OR SPECIALTY EQUIPMENT SUPPLIER DRAWINGS PRIOR TO ROUGH-IN.
4. CONDUIT DEDICATED FOR TECHNOLOGY SYSTEMS SHALL BE INSTALLED IN EMT UNLESS OTHERWISE NOTED. FLEX CONDUIT SHALL NOT BE USED WITHOUT PRIOR APPROVAL FROM THE ENGINEER OR OWNER.
5. CONDUIT DEDICATED FOR TECHNOLOGY SYSTEMS SHALL NOT EXCEED 100' OR CONTAIN MORE THAN 180 DEGREES OF TOTAL BENDS WITHOUT UTILIZING APPROPRIATELY SIZED PULL BOXES.
6. MINIMUM BEND RADII FOR 2" CONDUIT OR SMALLER SHALL BE 6 TIMES THE OUTSIDE DIAMETER OF THE CONDUIT. BEND RADII FOR CONDUIT LARGER THAN 2" SHALL BE 10 TIMES THE OUTSIDE DIAMETER OF THE CONDUIT. L-BENDS SHALL NOT BE USED.
7. ALL BACKBONE PATHWAYS SHALL BE EQUIPPED WITH A PULL CORD THAT HAS A MINIMUM TEST RATING OF 200lbs.
8. ALLOW FOR A MINIMUM OF 3" VERTICAL CLEAR SPACE ABOVE CONDUITS AND 12"VERTICAL CLEAR SPACE ABOVE CABLE TRAY.

DAO ARCHITECTURE
7230 Meade St.
Westminster, CO 80030
Phone: 720.273.0431
Email: dan@daoarch.com
Web: www.daoarch.com

CATOR | RUMA & ASSOCIATES, CO.
896 Tabor Street, Lakewood, CO 80401
(303) 232-6200 ▪ www.catorruma.com

Rev. #	Description	Rev. Date
	Revision Schedule	

Westminster Public Schools

Hodgkins Leadership Academy Classroom Conversion Project

3475 W 67th Ave,
Denver, CO 80221


DAO No.: 2021-033

September 25, 2026

ELECTRICAL NOTES, LEGENDS & DETAILS

E0.1

P:\WPS\2026-0530-Hodgkins Leadership Academy 2026 Bond Project\Cad
9/22/2026 4:11:20 PM

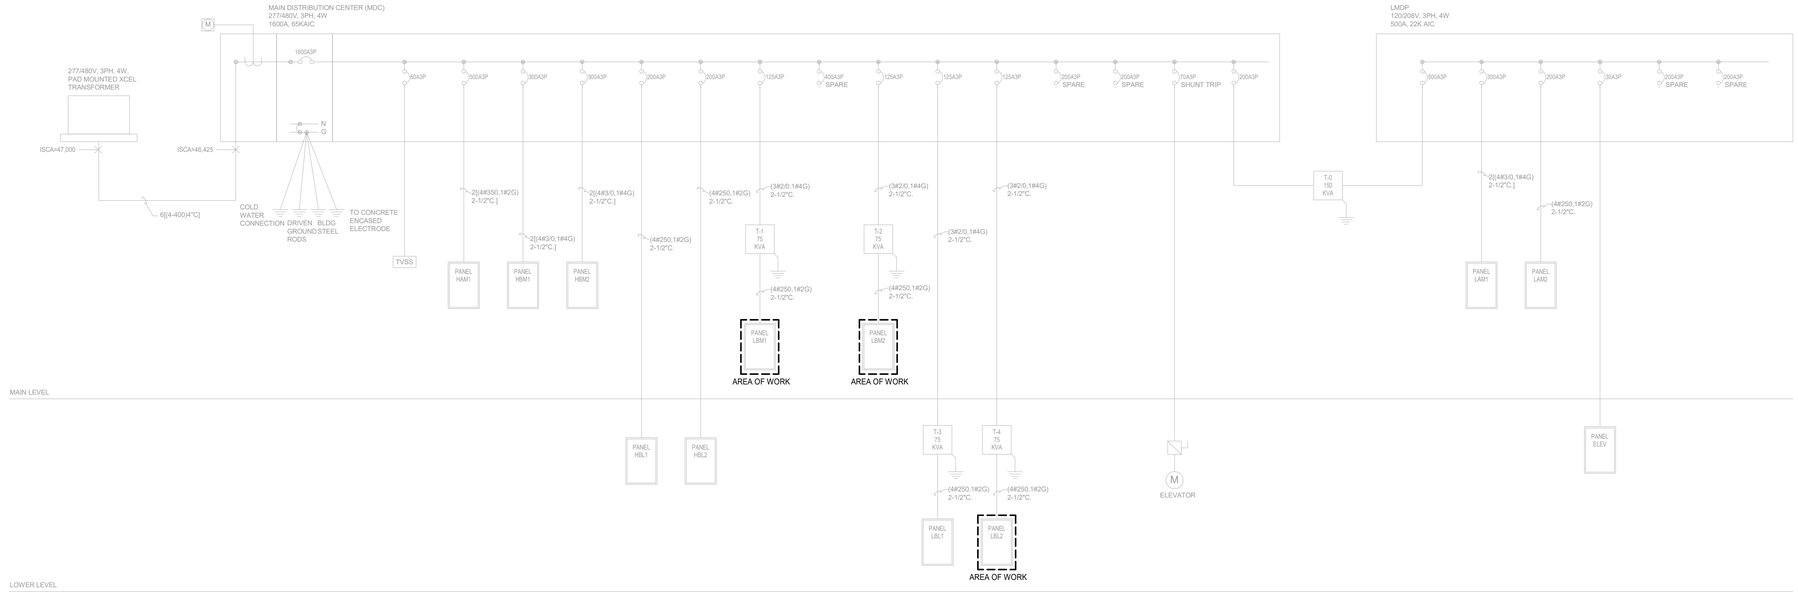

ELECTRICAL ONE-LINE DIAGRAM (FOR REFERENCE ONLY)

SCALE: NONE

P:\WPS\2026-0530-Hodgkins Leadership Academy 2026 Bond Project\Cad
9/22/2026 4:11:20 PM

DAO ARCHITECTURE

7230 Meade St.
Westminster, CO 80030

Phone: 720.273.0431
Email: dan@daoarch.com
Web: www.daoarch.com

CATOR | RUMA & ASSOCIATES, CO.
896 Tabor Street, Lakewood, CO 80401
(303) 232-6200 ▪ www.catorruma.com

Rev. #	Description	Rev. Date
	Revision Schedule	

Westminster Public Schools

Hodgkins Leadership Academy Classroom Conversion Project

3475 W 67th Ave,
Denver, CO 80221

DAO No.: 2021-033


September 25, 2026

ELECTRICAL ONE-LINE DIAGRAM

E0.3


KEYNOTES

E1	DISCONNECT AND REMOVE EXISTING DEVICES. PRESERVE EXISTING BRANCH CIRCUIT FOR RE-CONNECTION OF NEW DEVICES, THIS ROOM. CONTRACTOR SHALL FIELD VERIFY EXACT CIRCUITS TO DEVICES IN THIS ROOM. PROVIDE CIRCUIT TRACING AS REQUIRED.

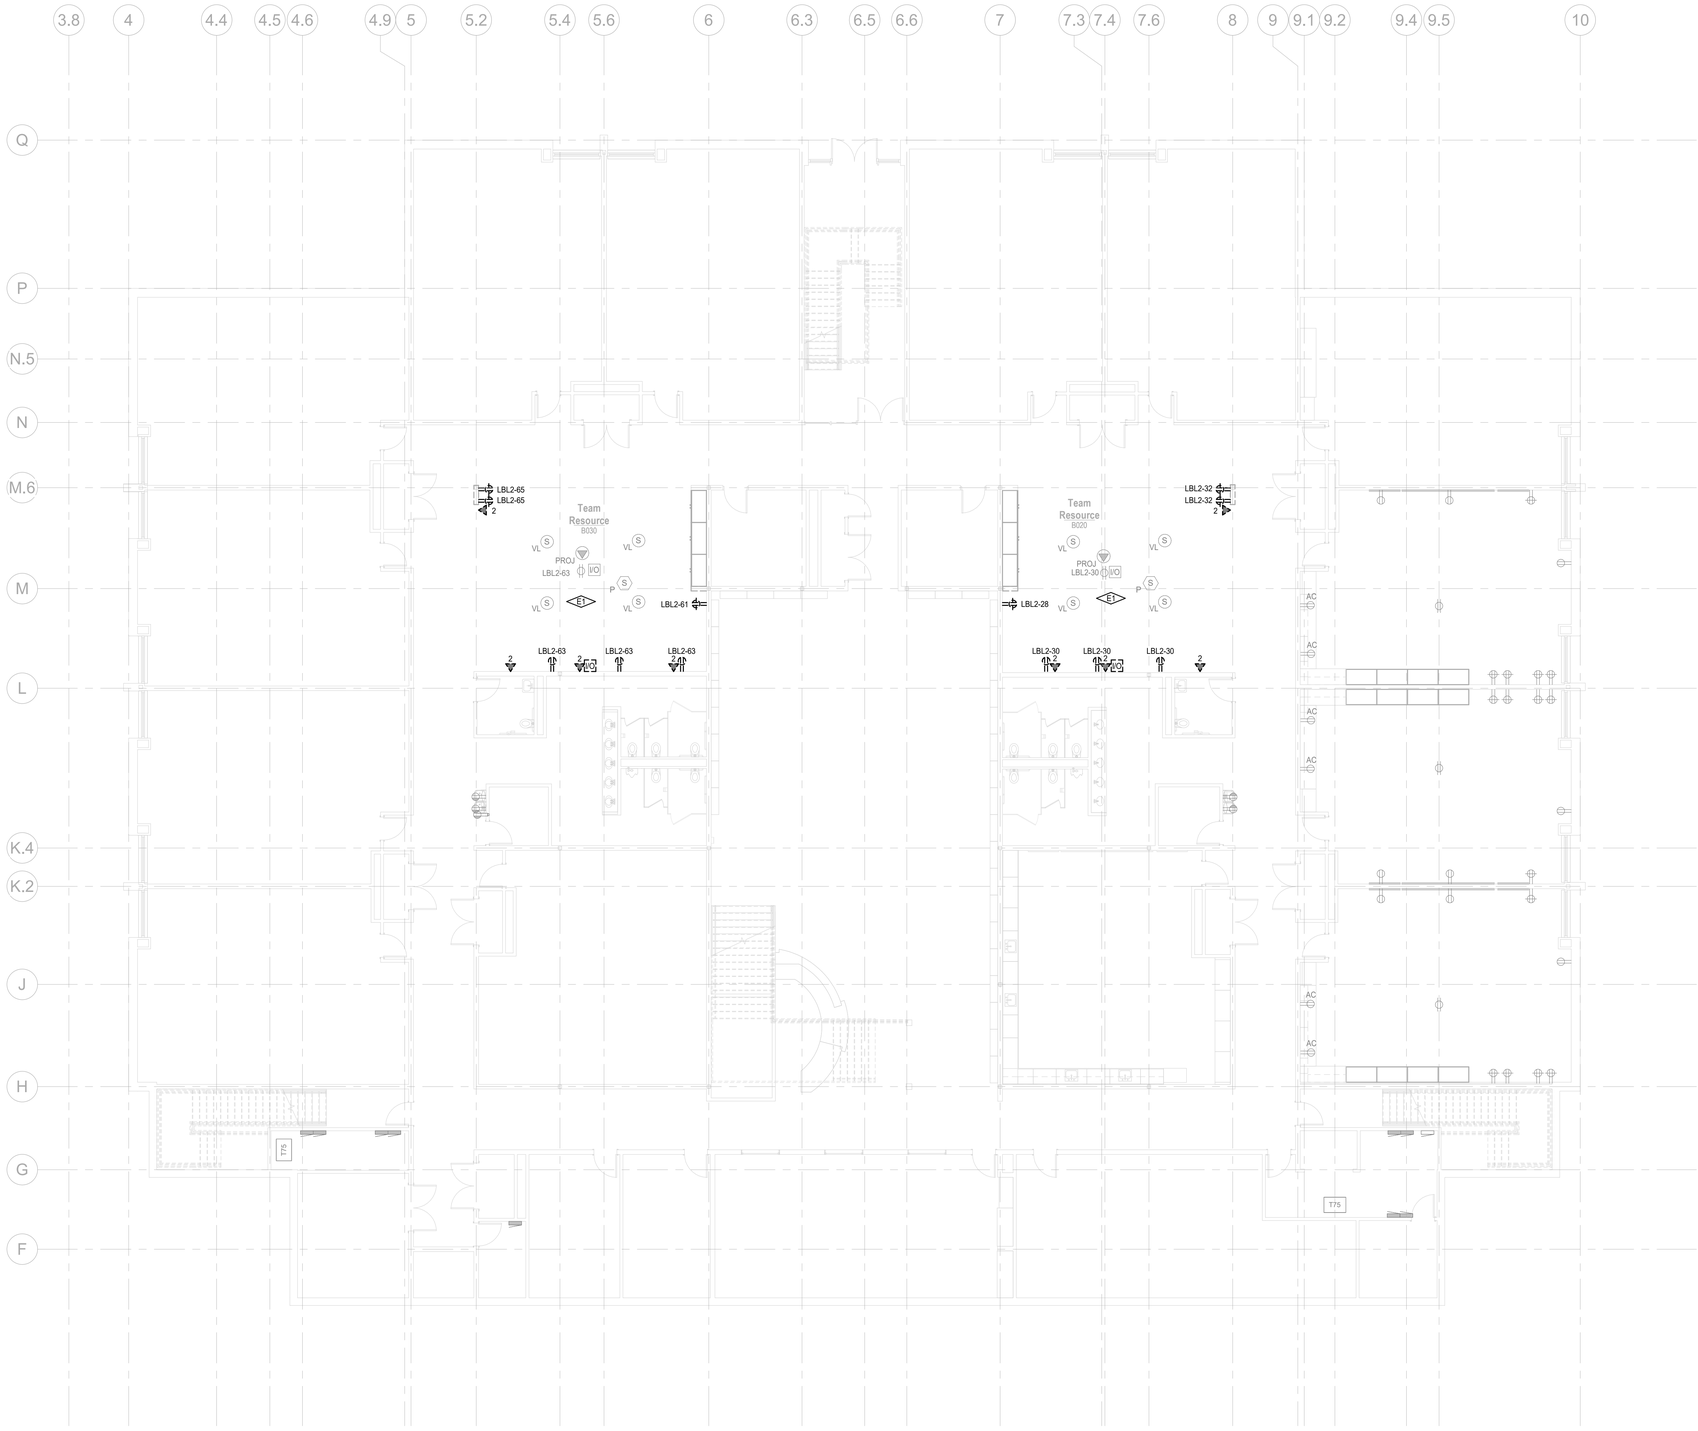

LOWER LEVEL POWER DEMOLITION PLAN

SCALE: 1/8" = 1'-0"

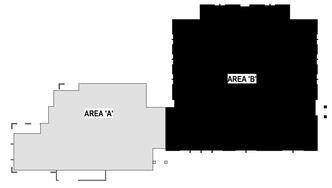

KeyPlan Area B

SCALE: NONE

DAO ARCHITECTURE

7230 Meade St.
Westminster, CO 80030

Phone: 720.273.0431
Email: dan@daoarch.com
Web: www.daoarch.com

CATOR | RUMA & ASSOCIATES, CO.
896 Tabor Street, Lakewood, CO 80401
(303) 232-6200 ▪ www.catorruma.com

Rev. #	Description	Rev. Date
	Revision Schedule	

Westminster Public Schools

Hodgkins Leadership Academy Classroom Conversion Project

3475 W 67th Ave,
Denver, CO 80221

DAO No.: 2021-033

September 25, 2026


LOWER LEVEL POWER DEMOLITION PLAN

ED1.2


P:\WPS\2026-0530-Hodgkins Leadership Academy 2026 Bond Project\Cad
9/22/2026 4:11:21 PM

KEYNOTES

E1	DISCONNECT AND REMOVE EXISTING DEVICES. PRESERVE EXISTING BRANCH CIRCUIT FOR RE-CONNECTION OF NEW DEVICES, THIS ROOM. CONTRACTOR SHALL FIELD VERIFY EXACT CIRCUITS TO DEVICES IN THIS ROOM. PROVIDE CIRCUIT TRACING AS REQUIRED.

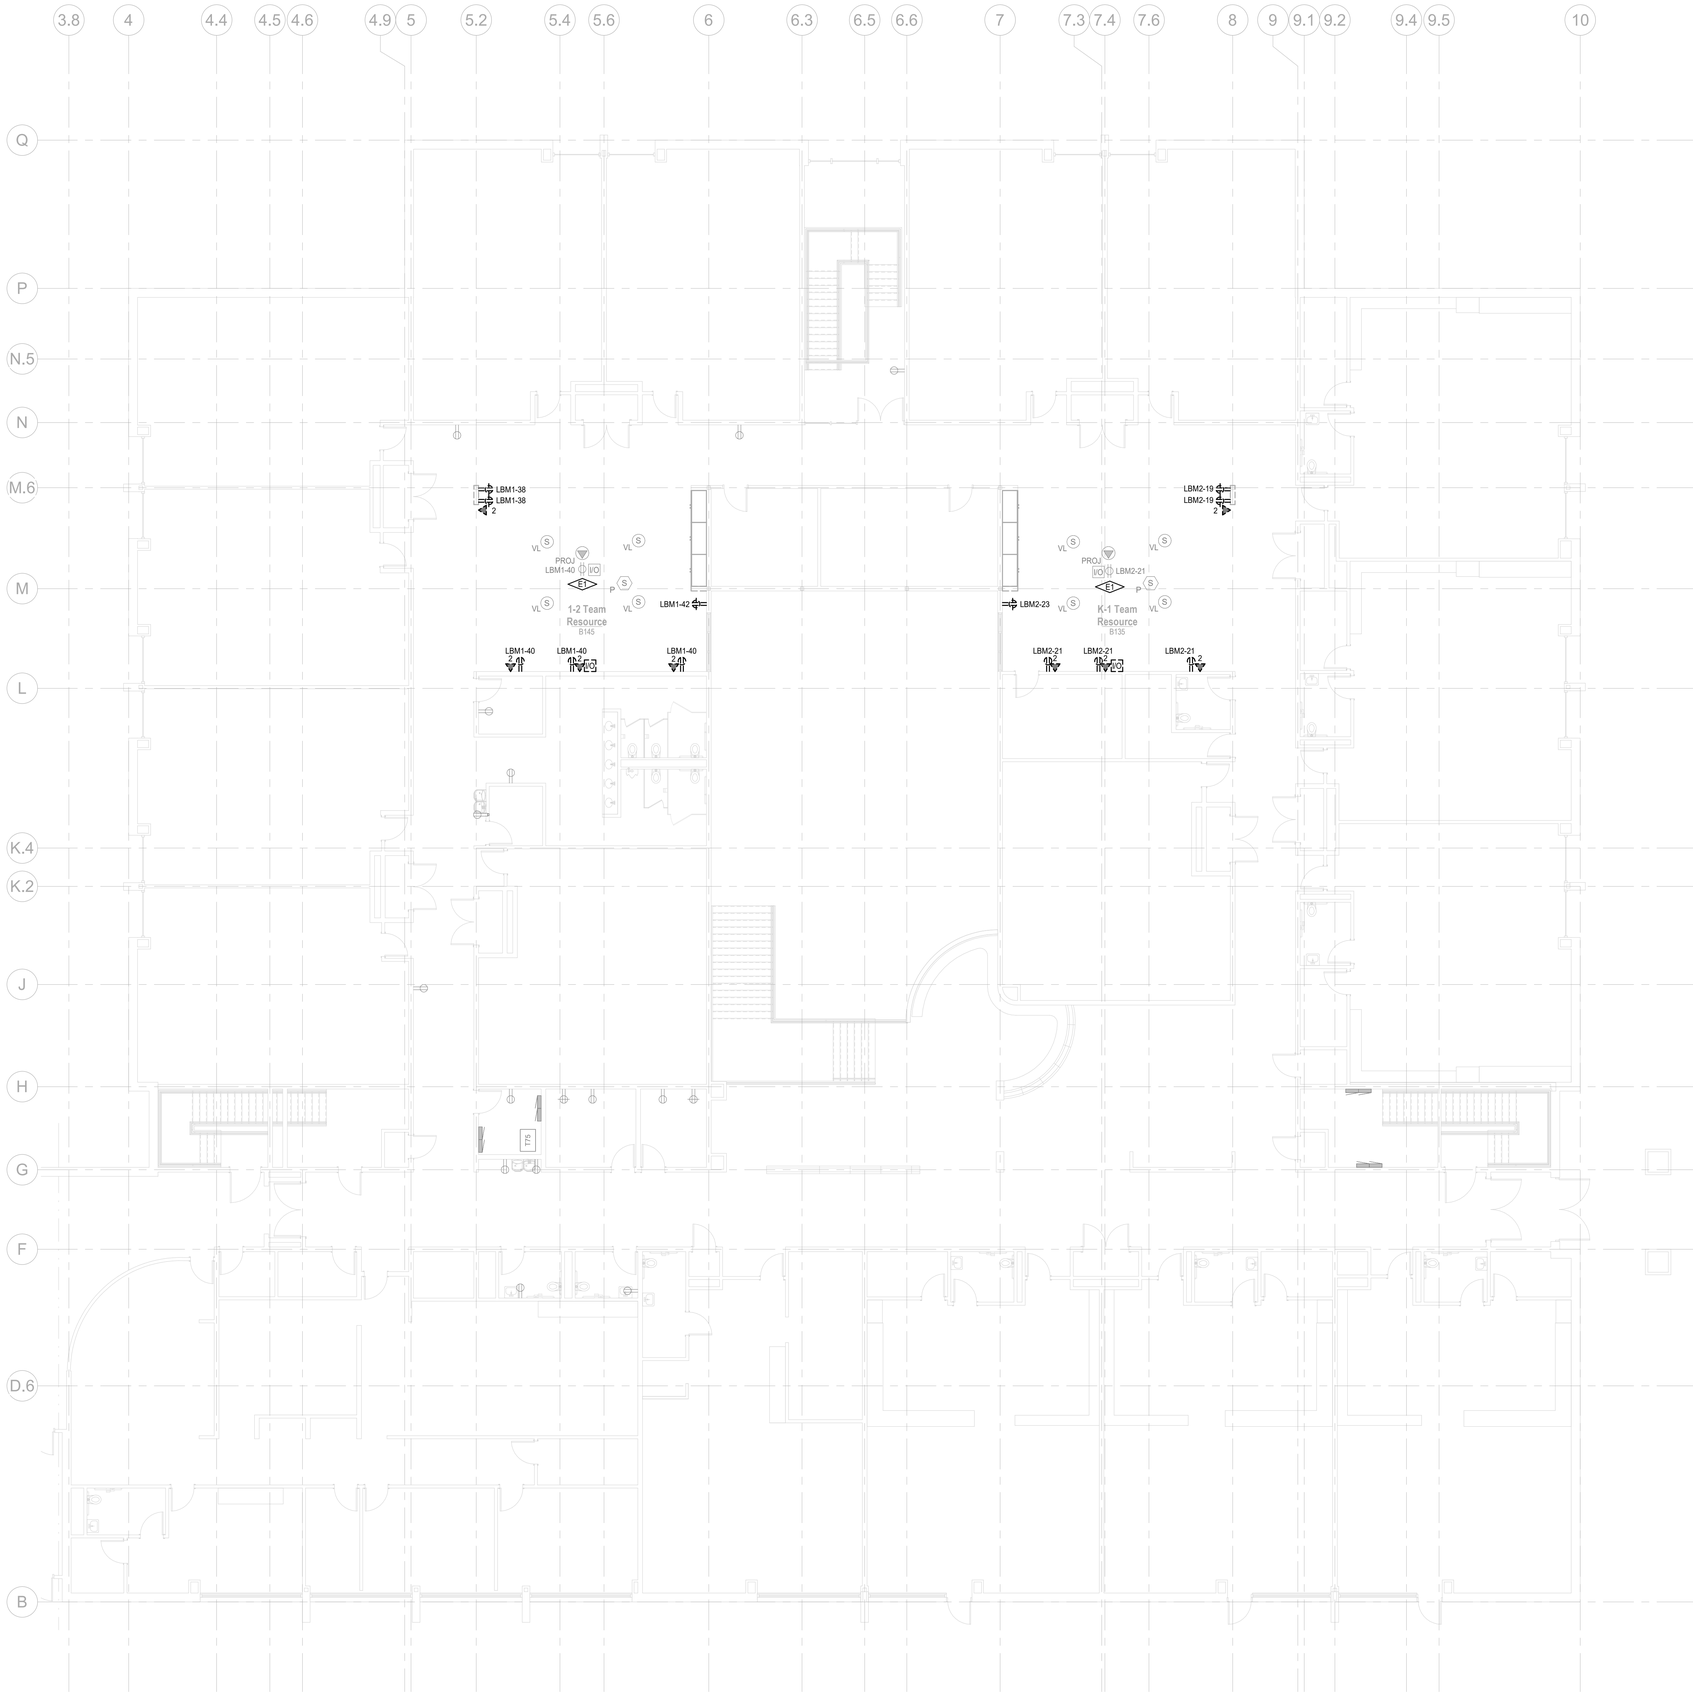

MAIN LEVEL POWER DEMOLITION PLAN
SCALE: 1/8" = 1'-0"

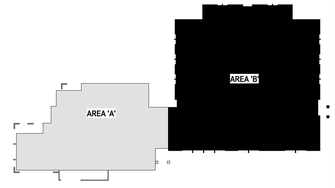

KeyPlan Area B
SCALE: NONE

DAO ARCHITECTURE
7230 Meade St.
Westminster, CO 80030
Phone: 720.273.0431
Email: dan@daoarch.com
Web: www.daoarch.com

CATOR | RUMA & ASSOCIATES, CO.
896 Tabor Street, Lakewood, CO 80401
(303) 232-6200 ▪ www.catorruma.com

Rev. #	Description	Rev. Date
	Revision Schedule	

Westminster Public Schools

Hodgkins Leadership Academy Classroom Conversion Project

3475 W 67th Ave,
Denver, CO 80221

DAO No.: 2021-033


September 25, 2026

MAIN LEVEL POWER DEMOLITION PLAN - AREA B

ED1.3B

P:\WPS\2026-1630-Hodgkins Leadership Academy 2026 Bond Project\Cad
9/22/2026 4:11:22 PM

KEYNOTES

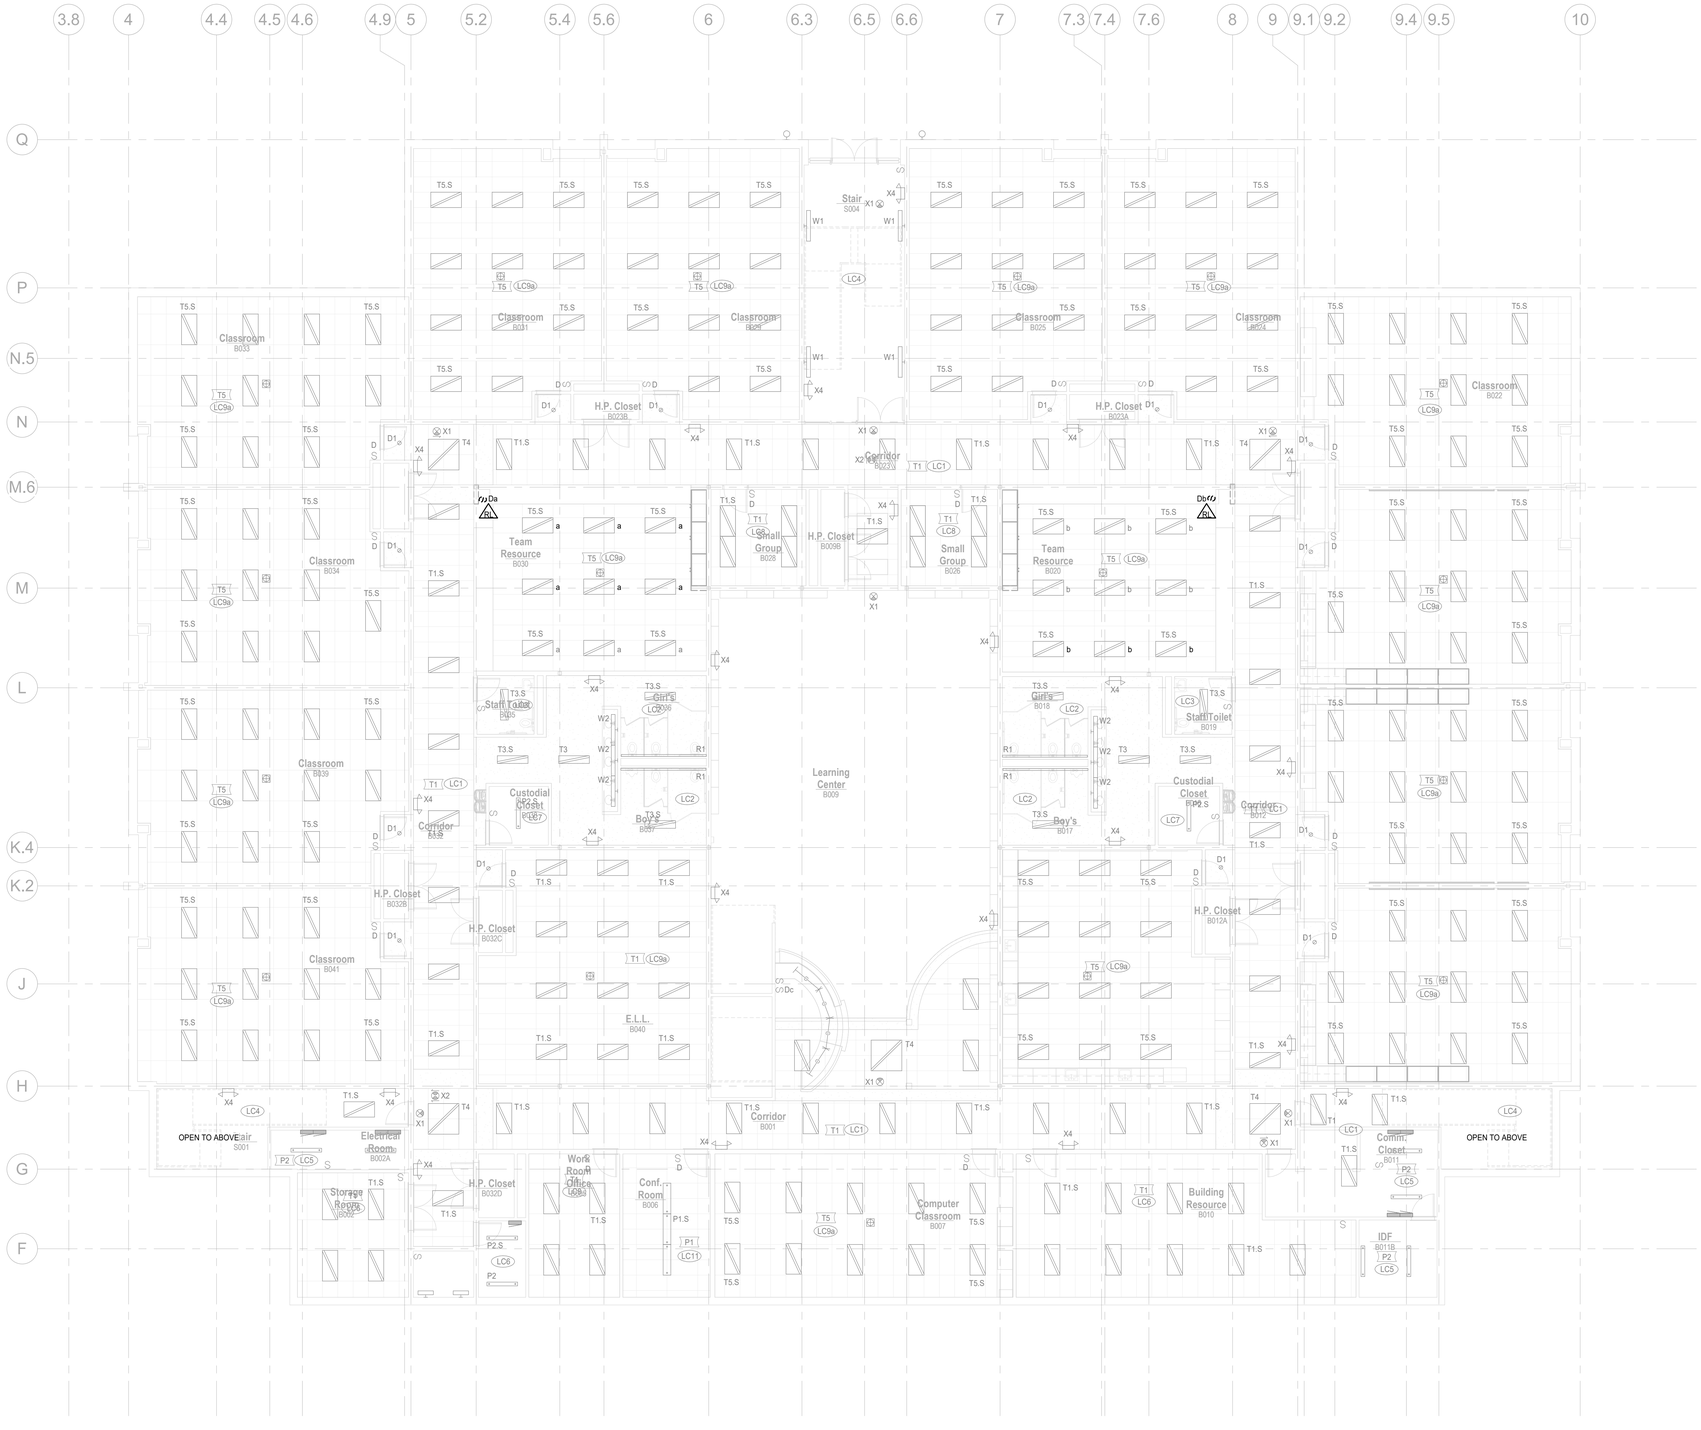

LOWER LEVEL LIGHTING DEMOLITION PLAN

SCALE: 1/8" = 1'-0"

P:\WPS\2026-0530 Hodgkins Leadership Academy 2026 Bond Project\Cad
9/22/2026 4:11:23 PM

DAO ARCHITECTURE

7230 Meade St.
Westminster, CO 80030

Phone: 720.273.0431
Email: dan@daoarch.com
Web: www.daoarch.com

CATOR | RUMA & ASSOCIATES, CO.
896 Tabor Street, Lakewood, CO 80401
(303) 232-6200 ▪ www.catorruma.com

Rev. #	Description	Rev. Date
	Revision Schedule	

Westminster Public Schools

Hodgkins Leadership Academy Classroom Conversion Project

3475 W 67th Ave,
Denver, CO 80221


DAO No.: 2021-033

September 25, 2026


LOWER LEVEL LIGHTING DEMOLITION PLAN

ED1.4

KEYNOTES

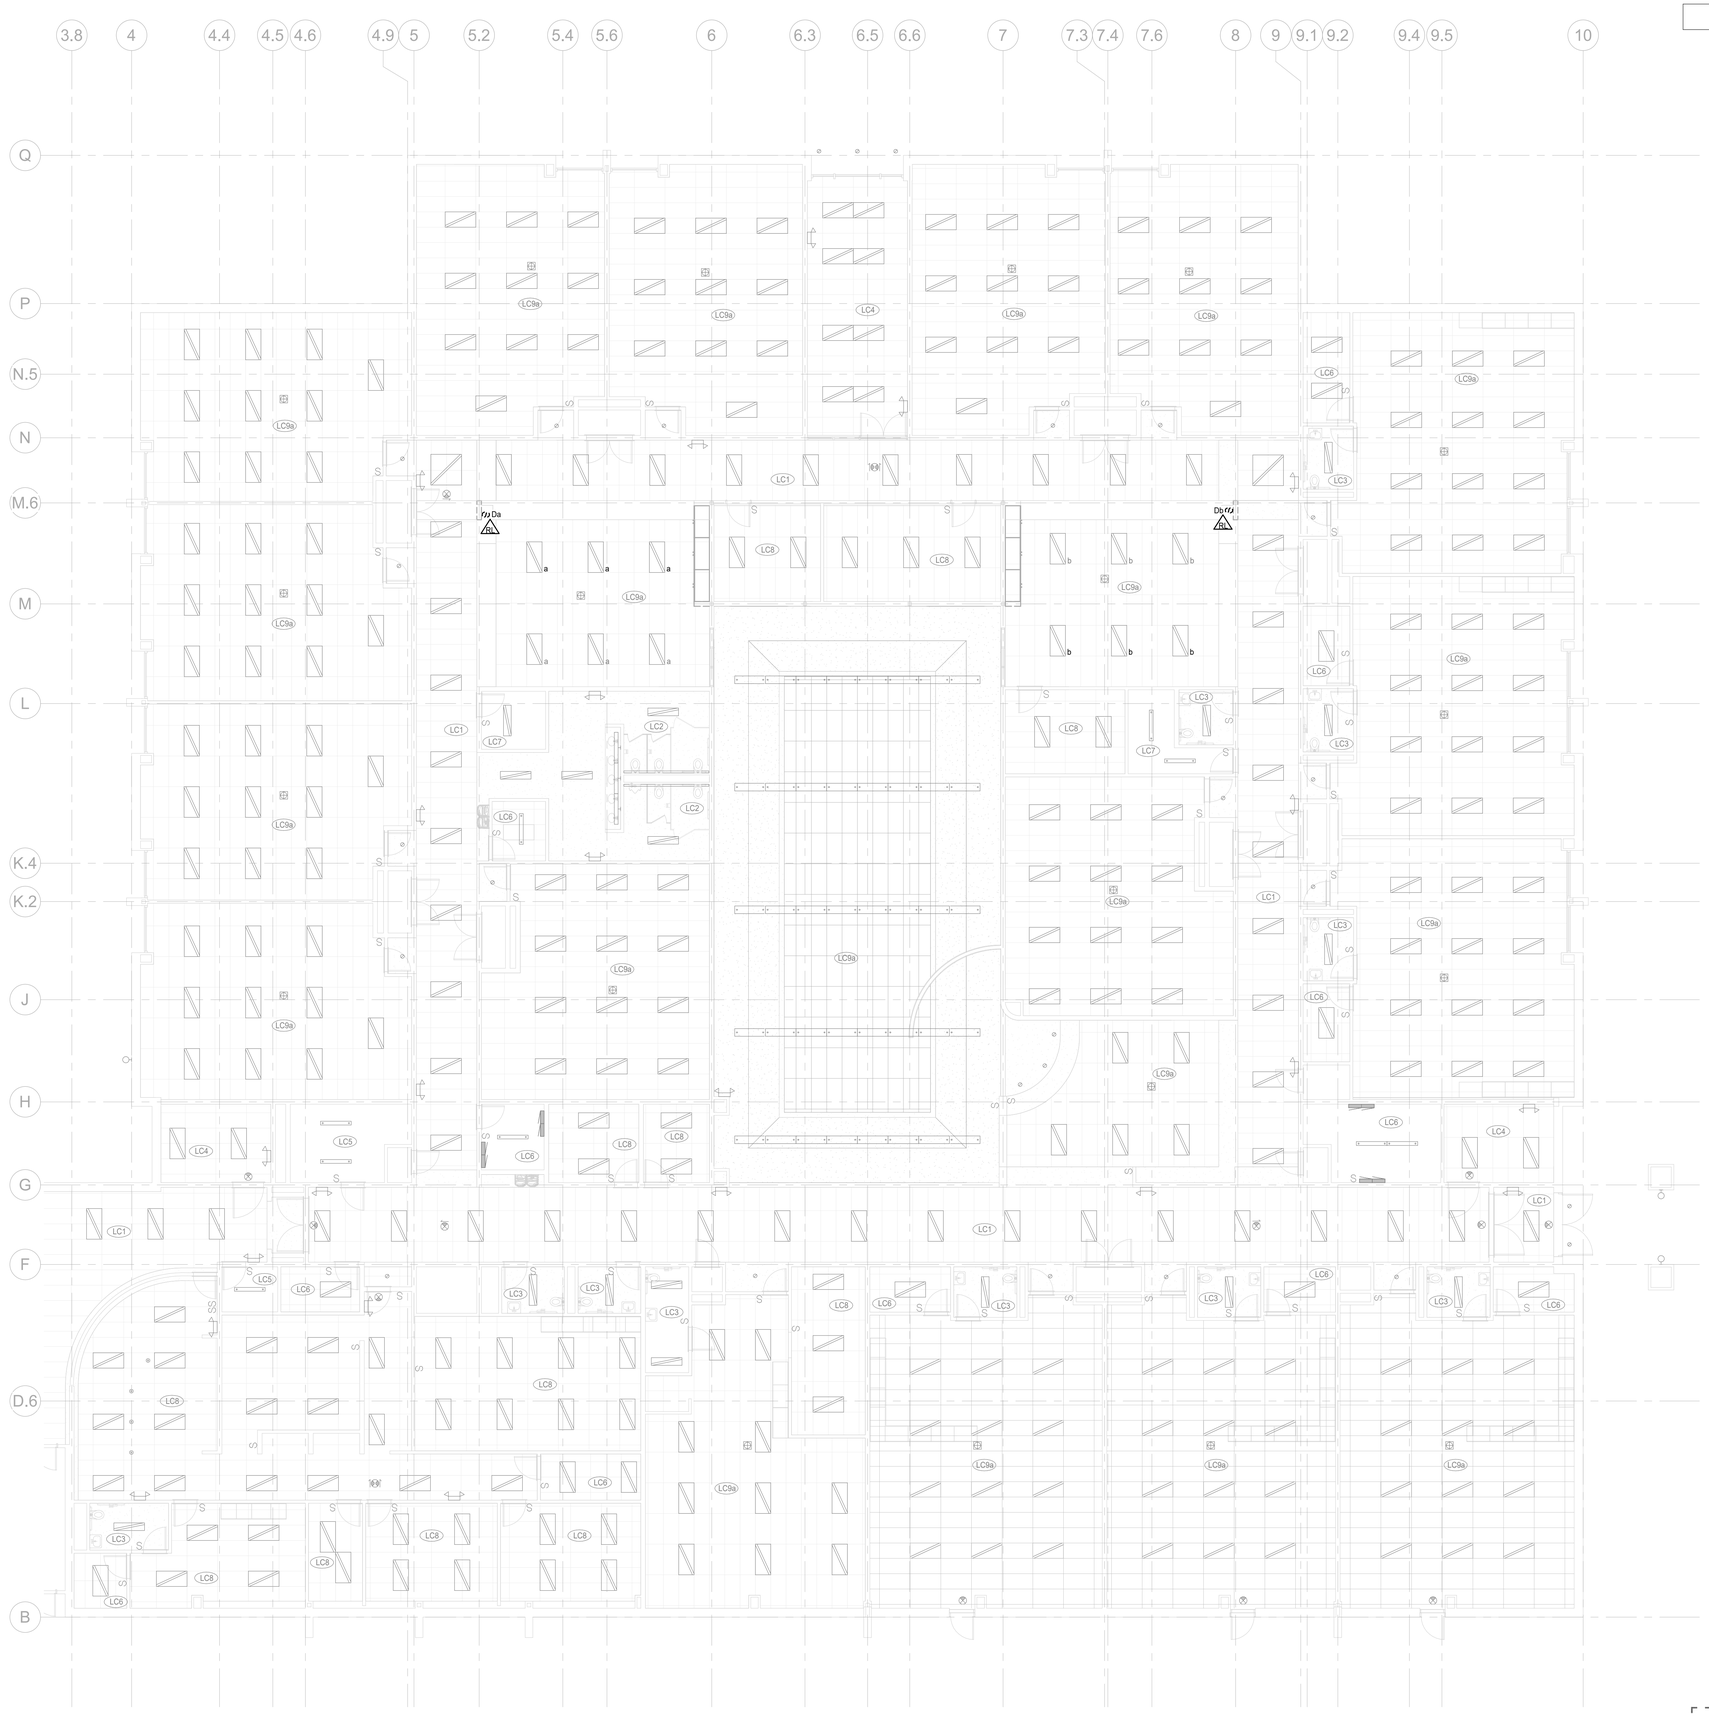

MAIN LEVEL LIGHTING DEMOLITION PLAN - AREA B
SCALE: 1/8" = 1'-0"

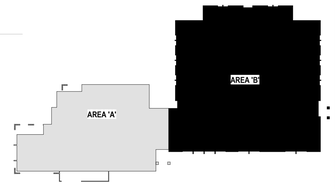

KeyPlan Area B
SCALE: NONE

DAO ARCHITECTURE
7230 Meade St.
Westminster, CO 80030
Phone: 720.273.0431
Email: dan@daoarch.com
Web: www.daoarch.com

CATOR | RUMA & ASSOCIATES, CO.
896 Tabor Street, Lakewood, CO 80401
(303) 232-6200 ▪ www.catorruma.com

Rev. #	Description	Rev. Date
Revision Schedule		

Westminster Public Schools

Hodgkins Leadership Academy Classroom Conversion Project

3475 W 67th Ave,
Denver, CO 80221

DAO No.: 2021-033

September 25, 2026


MAIN LEVEL LIGHTING DEMOLITION PLAN - AREA B

ED1.5B

P:\WPS\2026-0530-Hodgkins Leadership Academy 2026 Bond Project\Cad
9/22/2026 4:11:24 PM


KEYNOTES

E3	PROVIDE POWER PACK FOR CONTROL OF CONTROLLED RECEPTACLES. CONNECT TO EXISTING OCCUPANCY SENSOR FOR AUTOMATIC CONTROL.

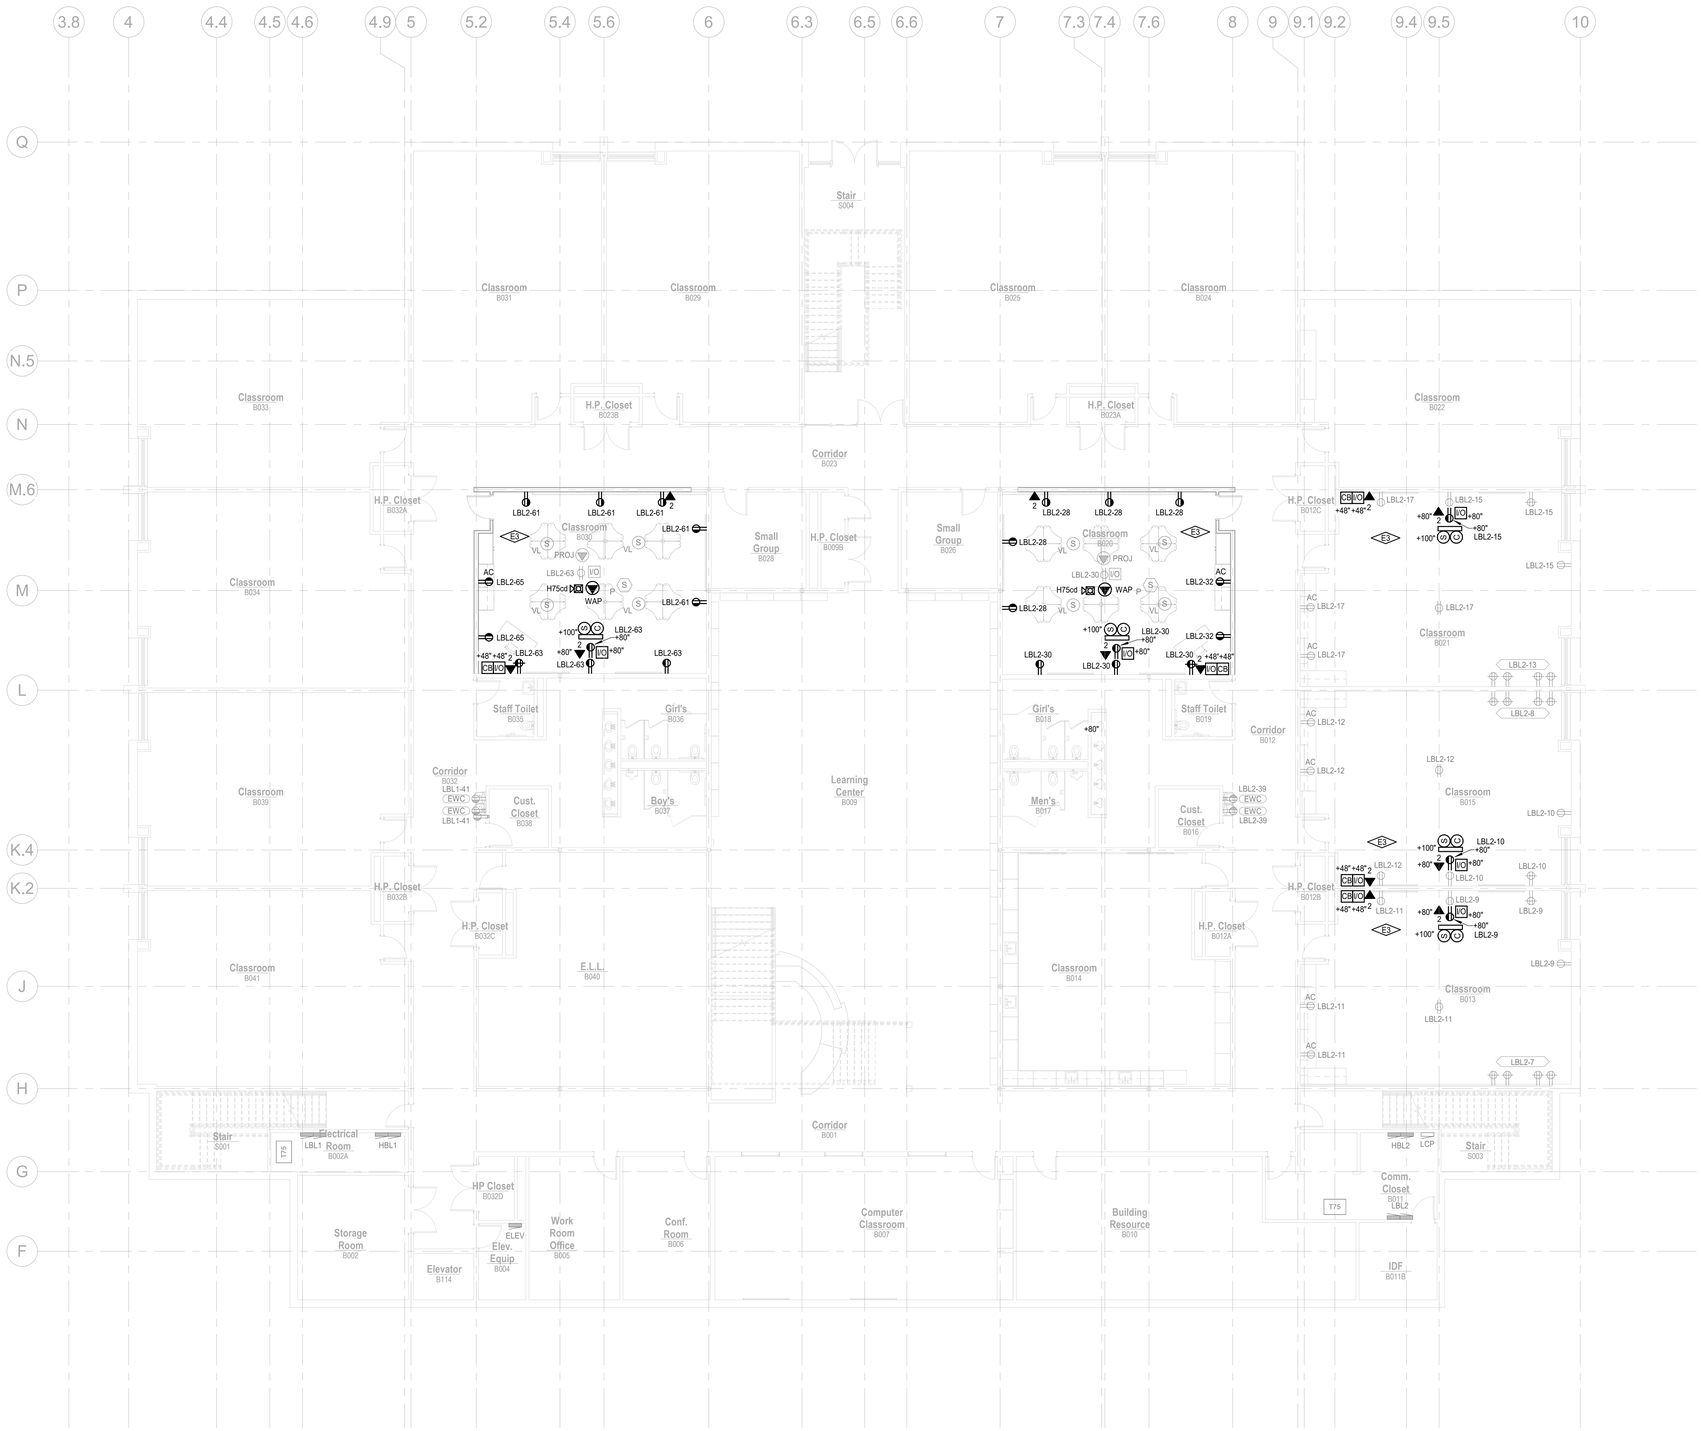

LOWER LEVEL POWER PLAN

SCALE: 1/8" = 1'-0"

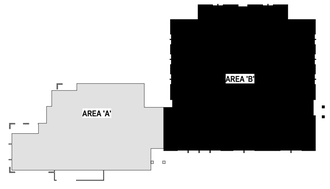

KeyPlan Area B

SCALE: NONE

DAO ARCHITECTURE

7230 Meade St.
Westminster, CO 80030

Phone: 720.273.0431
Email: dan@daoarch.com
Web: www.daoarch.com

CATOR | RUMA & ASSOCIATES, CO.
896 Tabor Street, Lakewood, CO 80401
(303) 232-6200 ▪ www.catorruma.com

Rev. #	Description	Rev. Date
	Revision Schedule	

Westminster Public Schools

Hodgkins Leadership Academy Classroom Conversion Project

3475 W 67th Ave,
Denver, CO 80221

DAO No.: 2021-033

September 25, 2026


LOWER LEVEL POWER PLAN

E1.2


P:\WPS\2025-5530 Hodgkins Leadership Academy 2026 Bond Project\Cad
9/22/2026 4:11:25 PM

KEYNOTES

E3	PROVIDE POWER PACK FOR CONTROL OF CONTROLLED RECEPTACLES. CONNECT TO EXISTING OCCUPANCY SENSOR FOR AUTOMATIC CONTROL.

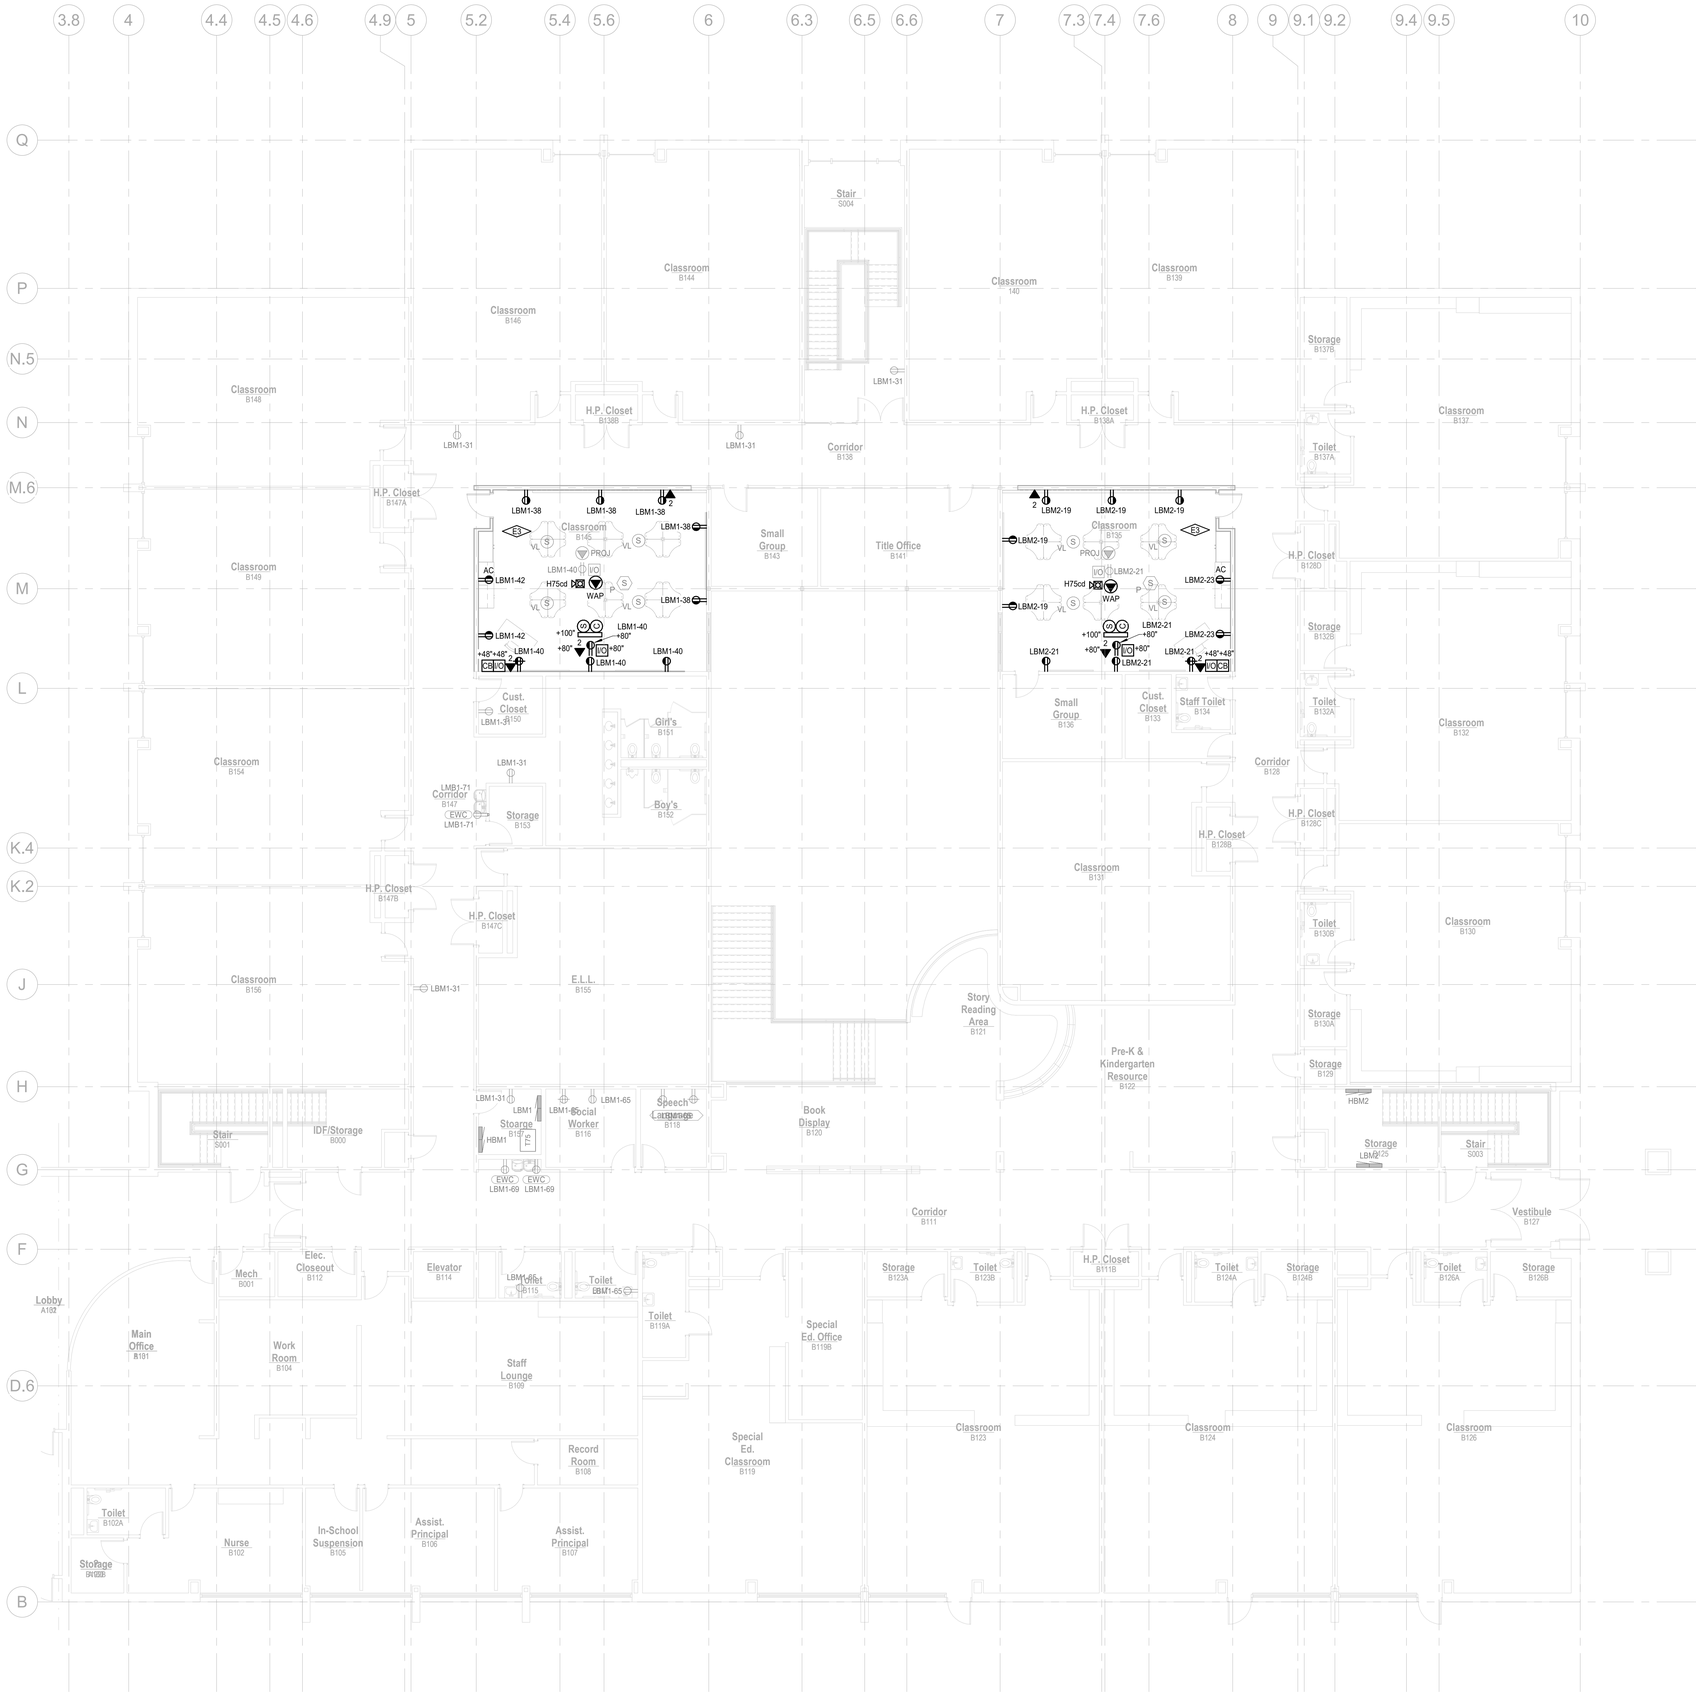

MAIN LEVEL POWER PLAN - AREA B
SCALE: 1/8" = 1'-0"

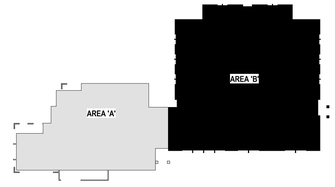

KeyPlan Area B
SCALE: NONE

DAO ARCHITECTURE
7230 Meade St.
Westminster, CO 80030
Phone: 720.273.0431
Email: dan@daoarch.com
Web: www.daoarch.com

CATOR | RUMA & ASSOCIATES, CO.
896 Tabor Street, Lakewood, CO 80401
(303) 232-6200 ▪ www.catorruma.com

Rev. #	Description	Rev. Date
	Revision Schedule	

Westminster Public Schools

Hodgkins Leadership Academy Classroom Conversion Project

3475 W 67th Ave,
Denver, CO 80221

DAO No.: 2021-033

September 25, 2026


MAIN LEVEL POWER PLAN - AREA B

E1.3B

P:\WPS\2026-0530-Hodgkins Leadership Academy 2026 Bond Project\Cad
9/22/2026 4:11:26 PM

KEYNOTES

E2	PROVIDE NLIGHT AIR RELAY PACK FOR CONTROLLED RECEPTACLE(S) INDICATED. PROGRAM FOR TIME-OF-DAY CONTROL AND COORDINATE SCHEDULE WITH OWNER.

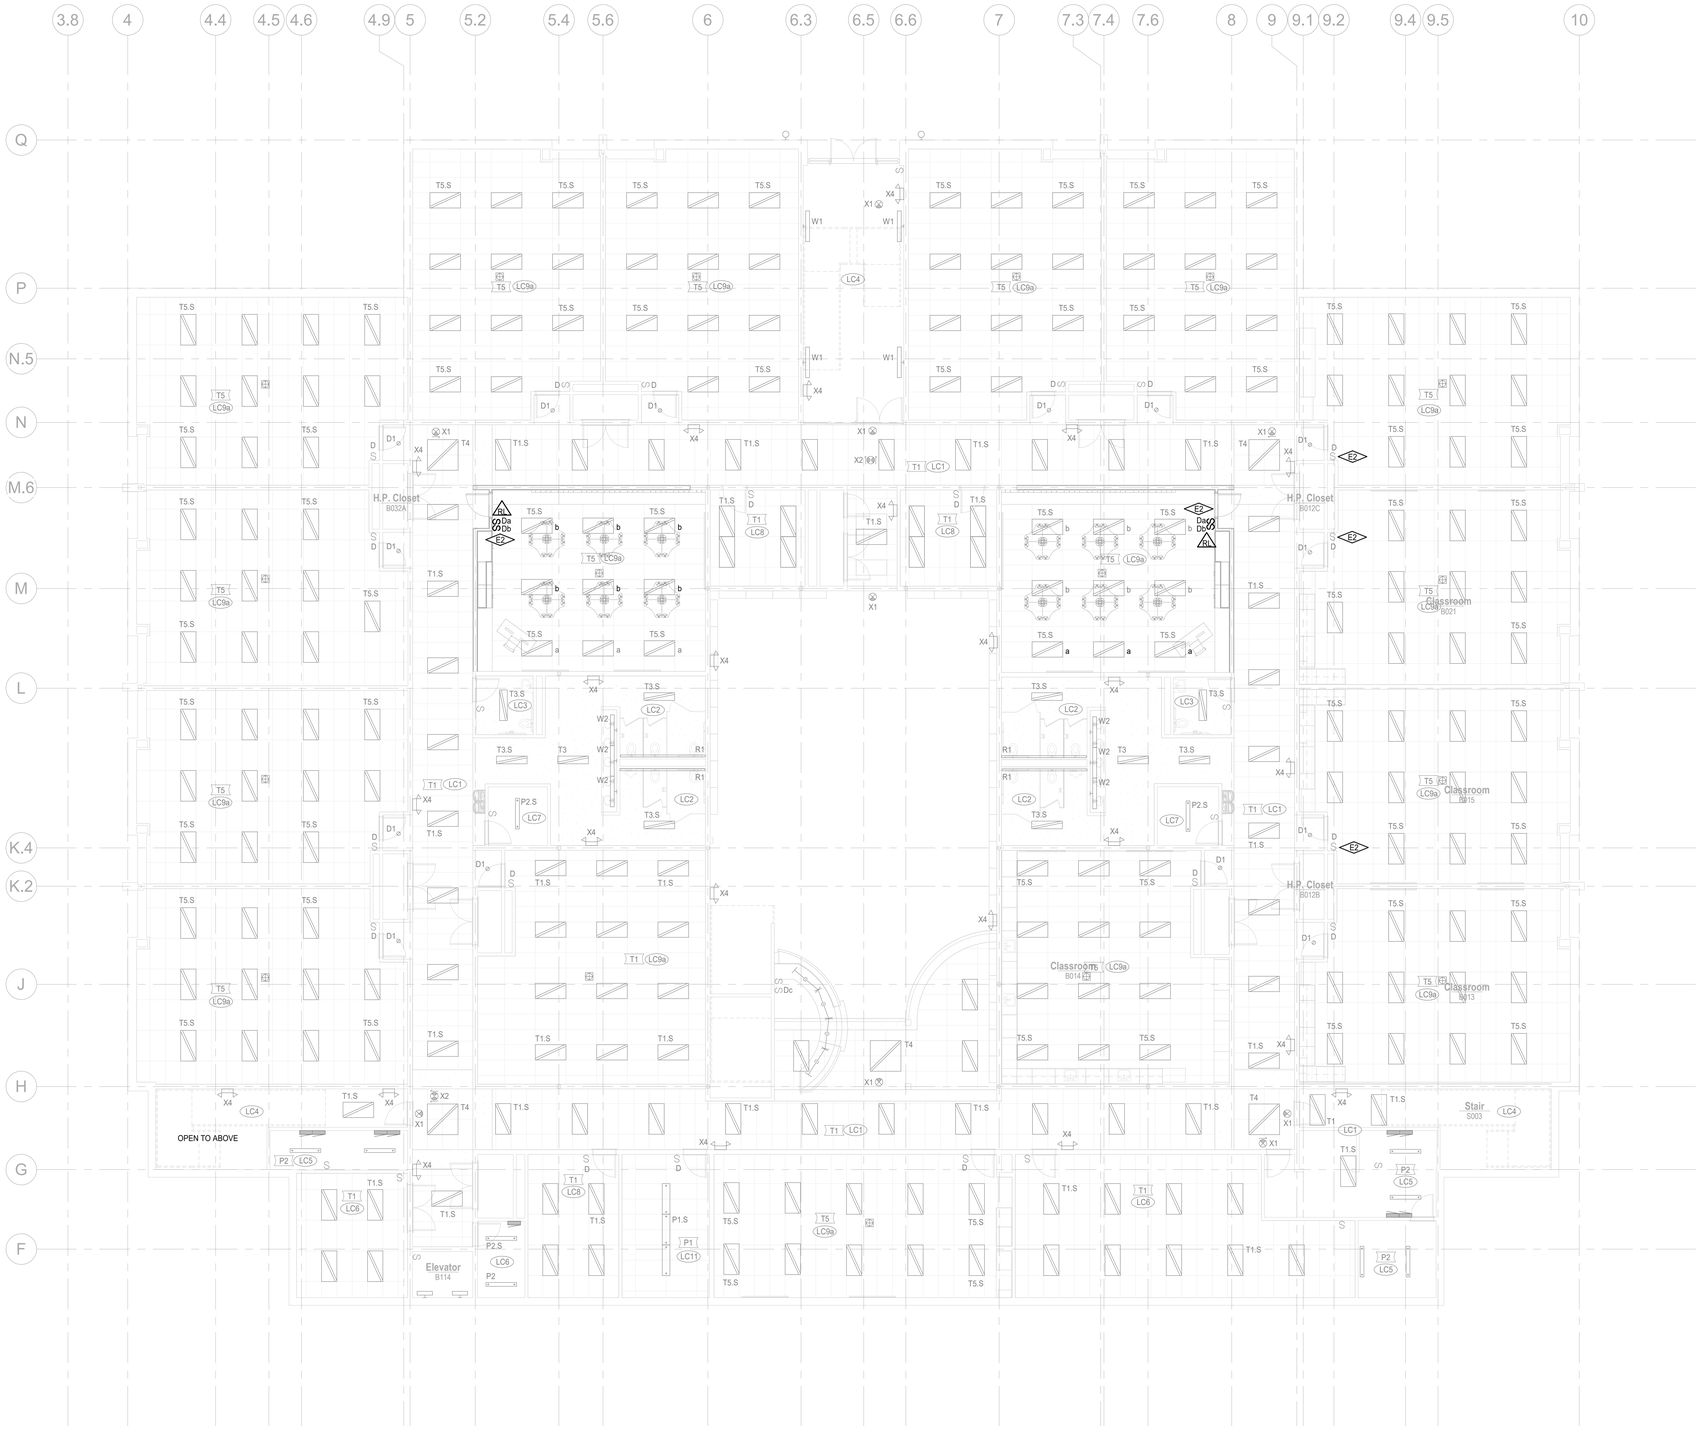

LOWER LEVEL LIGHTING PLAN
SCALE: 1/8" = 1'-0"

DAO ARCHITECTURE

7230 Meade St.
Westminster, CO 80030

Phone: 720.273.0431
Email: dan@daoarch.com
Web: www.daoarch.com

CATOR | RUMA & ASSOCIATES, CO.
896 Tabor Street, Lakewood, CO 80401
(303) 232-6200 ▪ www.catorruma.com

Rev. #	Description	Rev. Date
	Revision Schedule	

Westminster Public Schools

Hodgkins Leadership Academy Classroom Conversion Project

3475 W 67th Ave,
Denver, CO 80221

DAO No.: 2021-033

September 25, 2026


LOWER LEVEL LIGHTING PLAN

E1.4

P:\WFS\2026-0530 Hodgkins Leadership Academy 2026 Bond Project\Cad
9/22/2026 4:11:28 PM


KEYNOTES

E2	PROVIDE NLIGHT AIR RELAY PACK FOR CONTROLLED RECEPTACLE(S) INDICATED. PROGRAM FOR TIME-OF-DAY CONTROL AND COORDINATE SCHEDULE WITH OWNER.

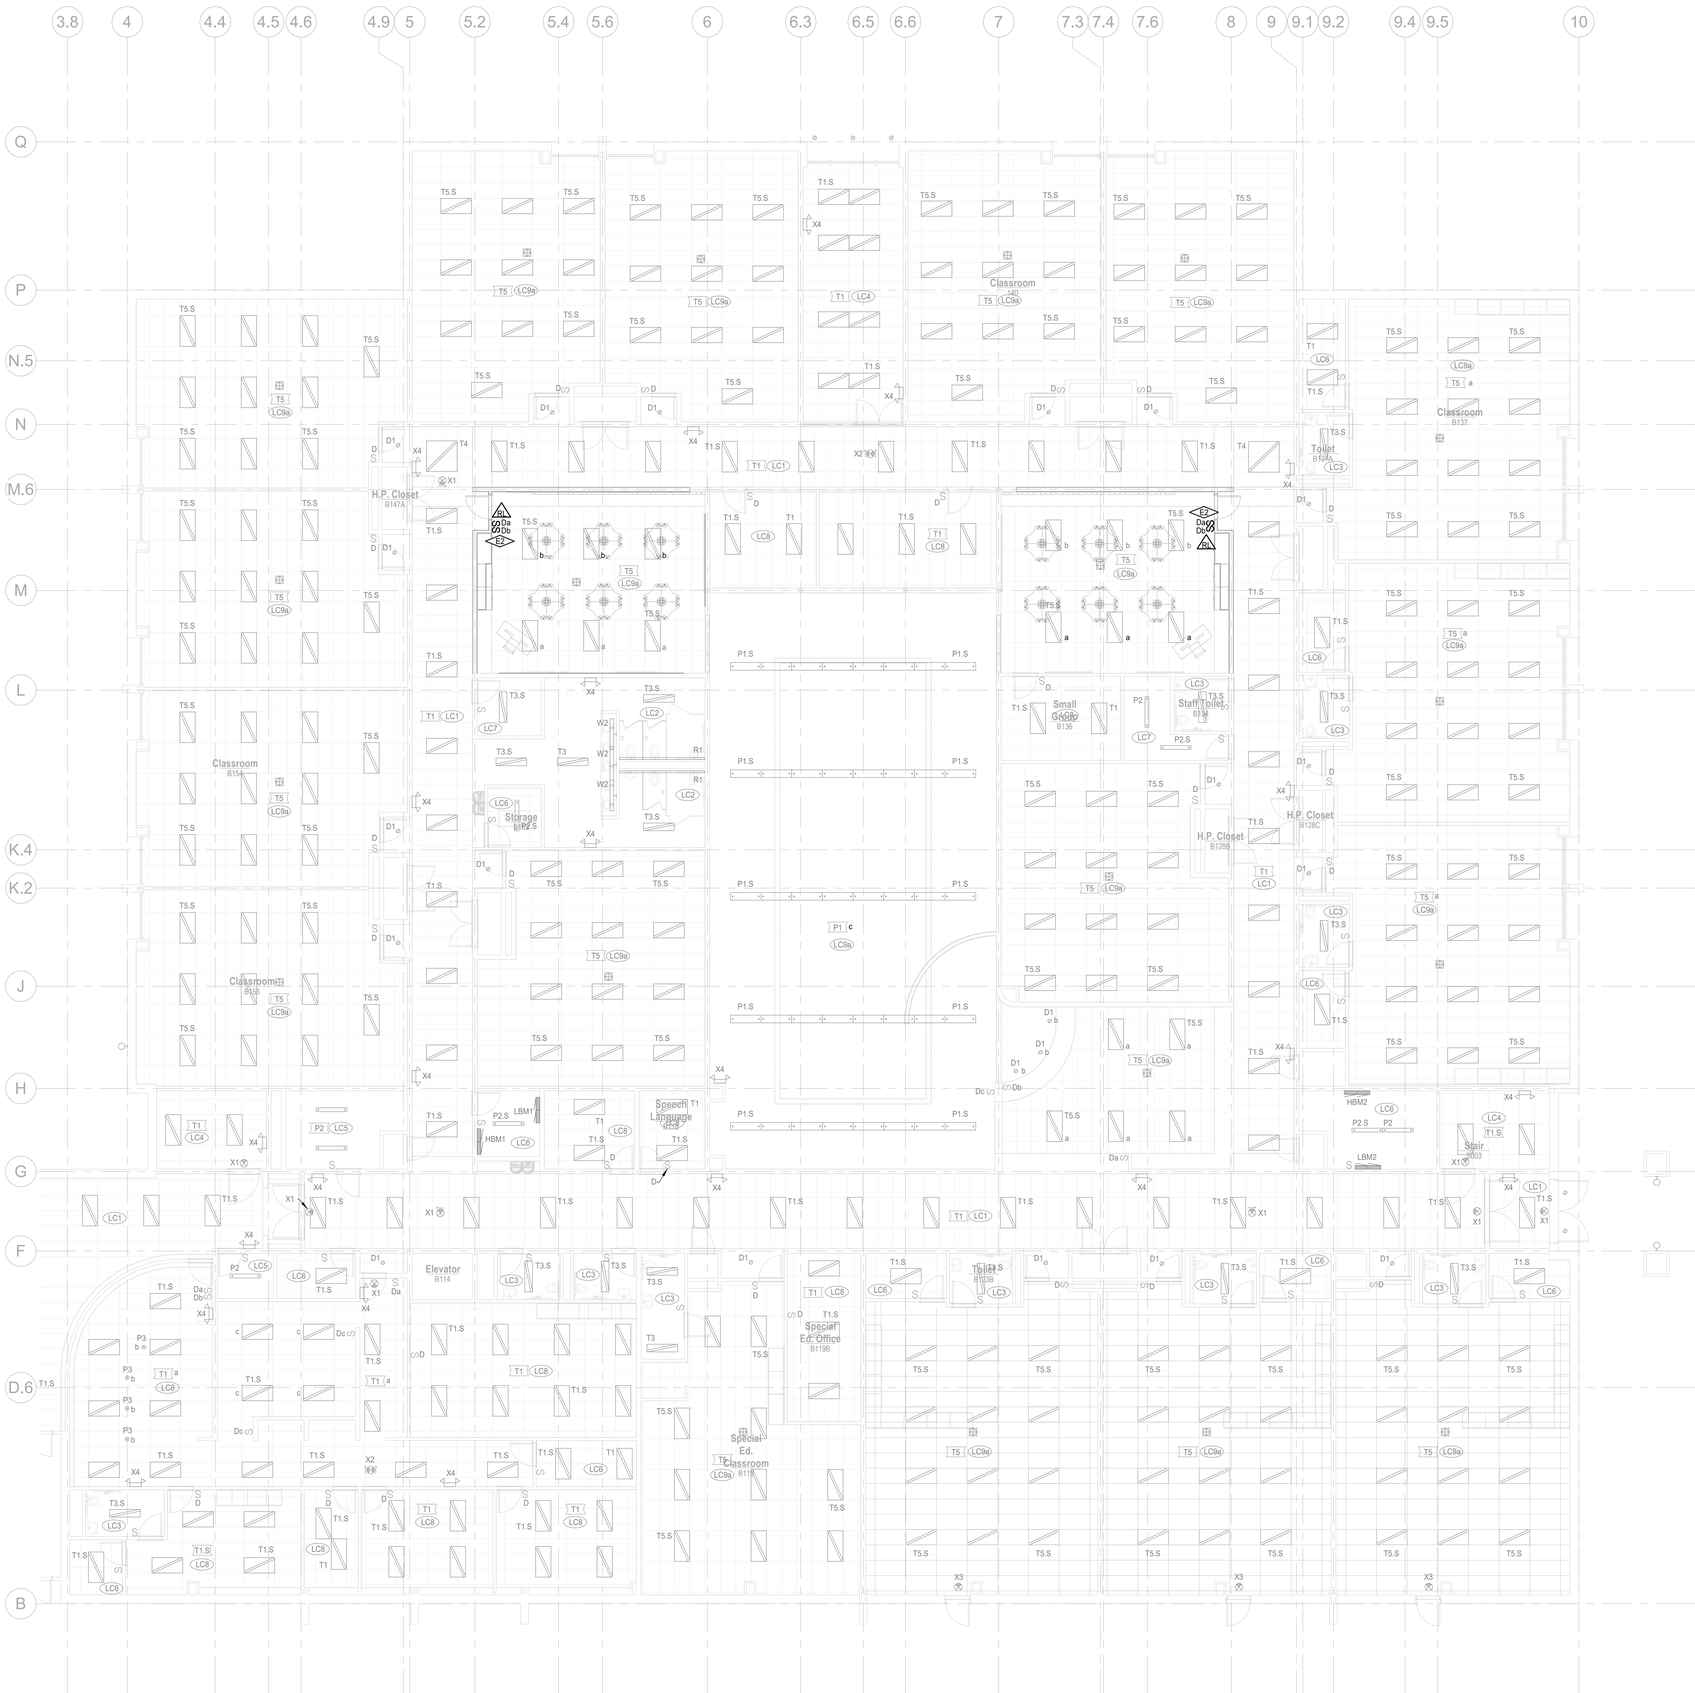

MAIN LEVEL LIGHTING PLAN - AREA B

SCALE: 1/8" = 1'-0"

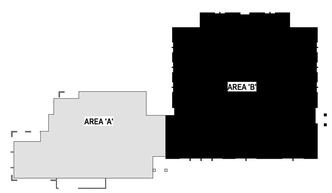

KeyPlan Area B

SCALE: NONE

DAO ARCHITECTURE

7230 Meade St.
Westminster, CO 80030

Phone: 720.273.0431
Email: dan@daoarch.com
Web: www.daoarch.com

CATOR | RUMA & ASSOCIATES, CO.
896 Tabor Street, Lakewood, CO 80401
(303) 232-6200 ▪ www.catorruma.com

Rev. #	Description	Rev. Date
	Revision Schedule	

Westminster Public Schools

Hodgkins Leadership Academy Classroom Conversion Project

3475 W 67th Ave,
Denver, CO 80221

DAO No.: 2021-033

September 25, 2026

MAIN LEVEL LIGHTING PLAN - AREA B

E1.5B

P:\WPS\2026-5530 Hodgkins Leadership Academy 2026 Bond Project\Cad
9/22/2026 4:11:29 PM

EXISTING PANEL LBM1

Panel Notes:
1. NEW LOAD ON EXISTING CIRCUIT BREAKER.

200 A MAIN CIRCUIT BREAKER — VOLTAGE 120 / 208 V
250 A BUS — PHASE 3 PH
WIRE 4 W

MFR : SIEMENS
MTG. : SURFACE

10000 AMPERE SHORT CIRCUIT RATING (FULLY RATED)

NOTE	DESCRIPTION	LTG	RECEPT	MOTORS	OTHER	GENERAL	TOTAL	BREAKER AMP / P	CCT	PH	CCT	BREAKER AMP / P	TOTAL	GENERAL	OTHER	MOTORS	RECEPT	LTG	DESCRIPTION	NOTE
	HP2.08A			1,789			1789	25 /	1	A	2	25 /	1789				1,789		HP2.08B	
	/			1,789			1789	/ 2	3	B	4	/ 2	1789				1,789		/	
	HP2.09A			1,789			1789	25 /	5	C	6	25 /	1789				1,789		HP2.09B	
	/			1,789			1789	/ 2	7	A	8	/ 2	1789				1,789		/	
	TELECOM RACK B158		1,800				1800	20 / 1	9	B	10	20 / 1	1800				1,800		PA RACK B113	
	TELECOM RACK B158		1,800				1800	20 / 1	11	C	12	20 / 1	1080				1,080		RECEPTACLES B113	
	TELECOM RACK B158		1,800				1800	20 / 1	13	A	14	20 / 1	1080				1,080		RECEPTACLES B155	
	ROOF RECEPT						0	20 / 1	15	B	16	20 / 1	1080				1,080		RECEPTACLES B155	
	EXIST. LOAD						0	20 / 1	17	C	18	20 / 1	1080				1,080		RECEPTACLES B155	
	RECEPTACLES B158		1,080				1080	20 / 1	19	A	20	20 / 1	1080				1,080		RECEPTACLES B154	
	RECEPTACLES B156		1,080				1080	20 / 1	21	B	22	20 / 1	1080				1,080		RECEPTACLES B154	
	RECEPTACLES B156		1,080				1080	20 / 1	23	C	24	20 / 1	1080				1,080		RECEPTACLES B154	
	RECEPTACLES B149		1,080				1080	20 / 1	25	A	26	20 / 1	1080				1,080		RECEPTACLES B148	
	RECEPTACLES B149		1,080				1080	20 / 1	27	B	28	20 / 1	1080				1,080		RECEPTACLES B148	
	RECEPTACLES B149		1,080				1080	20 / 1	29	C	30	20 / 1	1080				1,080		RECEPTACLES B148	
	RECEPTACLES B146		1,080				1080	20 / 1	31	A	32	20 / 1	1080				1,080		RECEPTACLES B144	
	RECEPTACLES B148		1,080				1080	20 / 1	33	B	34	20 / 1	1080				1,080		RECEPTACLES B144	
	RECEPTACLES B148		1,080				1080	20 / 1	35	C	36	20 / 1	1080				1,080		RECEPTACLES B144	
	RECEPTACLES B143		1,080				1080	20 / 1	37	A	38	20 / 1	**900**				**900**		**RECEPTACLES B145**	1
	RECEPTACLES B141		180				180	20 / 1	39	B	40	20 / 1	**900**				**900**		**RECEPTACLES B145**	1
	RECEPTACLES B141		1,080				1080	20 / 1	41	C	42	20 / 1	**480**				**480**		**RECEPTACLES B145**	1
	MICROWAVE				1200		1200	20 / 1	43	A	44	20 / 1	1200				1200		VENDING MACH B109	
	MICROWAVE				1200		1200	20 / 1	45	B	46	20 / 1	1200				1200		VENDING MACH B109	
	MICROWAVE				1200		1200	20 / 1	47	C	48	20 / 1	1200				1200		VENDING MACH B109	
	RECEPTACLES B157	1080					1080	20 / 1	49	A	50	20 / 1	1200				1200		REFRIGERATORS B109	
	MULTIFUNCTION DEVICE				2400		2400	20 / 1	51	B	52	20 / 1	1440				1440		RECEPT B104,B112	
	RECEPTACLES B104	1080					1080	20 / 1	53	C	54	20 / 1	1440				1440		RECEPTACLES B112	
	MULTIFUNCTION DEVICE				2400		2400	20 / 1	55	A	56	20 / 1	1080				1080		RECEPTACLES B109	
	RECEPTACLE B150	180					180	20 / 1	57	B	58	20 / 1	1200		1200				EWC	
	REFRIGERATOR B102	1200					1200	20 / 1	59	B	60	20 / 1	1200		1200				HAND DRYERS	
	RECEPT B105,B106	1440					1440	20 / 1	61	A	62	20 / 1	1080				1080		RECEPTACLES B101	
	RECEPTACLES B107	1080					1080	20 / 1	63	B	64	20 / 1	1080				1080		RECEPT CORRIDOR	
	RCPT B118,B116,B117,B115	1440					1440	20 / 1	65	C	66	20 / 1	1080				1080		RECEPTACLES B102	
	IDF B113 UPS				2500		2500	30 /	67	A	68	20 / 1	1080				1080		RECEPT CORRIDORS	
	/				2500		2500	/ 2	69	B	70	20 / 1	200		200				F.A. PANEL	
	SPARE						0	20 / 1	71	C	72	/	840			840			FCU-2	
	SPACE						0		73	A	74	2	840			840			/	
							0	30 /	75	B	76		0						SPACE	
							0	/ 2	77	C	78		0						SPACE	
	SPACE						0		79	A	80		0						SPACE	
	SPACE						0		81	B	82		0						SPACE	
	SPACE						0		83	C	84		0						SPACE	

PHASE LOADING SUMMARY — PANEL LOADING SUMMARY

LOAD TYPE (VA)	PH A	PH B	PH C
LIGHTING	0.0	0.0	0.0
RECEPTACLES	19,500.0	17,220.0	19,440.0
MOTORS	7,996.0	3,578.0	4,418.0
OTHER	6,100.0	7,500.0	2,400.0
GENERAL	0.0	0.0	0.0
TOTAL (VA)	33,596.0	28,298.0	26,258.0
NEC CALCULATED			
PHASE AMPACITY	256.3	224.7	187.8
	#REF!		
PHASE BALANCE	A-B	B-C	C-A
	19%	8%	28%

LOAD TYPE	CONNECTED LOAD KVA		NEC CALCULATED DEMAND LOAD		POWER FACTOR	DEMAND LOAD KW	
LIGHTING	0.0	KVA	x 125% =	0.0 KVA	x 95% =	0.0 KW	
RECEPTACLES							
FIRST 10 KVA	10.0	KVA	x 100% =	10.0 KVA	x 100% =	10.0 KW	
REMAINDER	46.2	KVA	x 50% =	23.1 KVA	x 100% =	23.1 KW	
MOTORS							
LARGEST	3.6	KVA	x 125% =	4.5 KVA	x 90% =	4.0 KW	
REMAINDER	12.4	KVA	x 100% =	12.4 KVA	x 90% =	11.2 KW	
OTHER	16.0	KVA	x 125% =	20.0 KVA	x 100% =	20.0 KW	
GENERAL	0.0	KVA	x 100% =	0.0 KVA	x 100% =	0.0 KW	
TOTAL	88.2	KVA		70.0 KVA		68.3 KW	

PANEL CONNECTED PF= 98%
CONNECTED AMPACITY = 244.7
NEC DEMAND AMPACITY = 194.2

GENERAL NOTES:
1. PROVIDE NEW UPDATED PANEL DIRECTORIES FOR PANELS THAT ARE INCLUDED IN THIS PROJECT.
2. PROVIDE TYPED DESCRIPTIONS OF NEW CIRCUITS BEING INSTALLED. INDICATE NEW SPARES IN PENCIL.

MDC LOAD SUMMARY

MDC CAPACITY	1600 A
EXISTING PEAK DEMAND	1174 A
NEC DEMAND FACTOR	x 125%
NEC CORRECTED PEAK DEMAND LOAD	1468 A
2025 LED UPGRADE LOAD REMOVED	257 A
2025 LED UPGRADE LOAD ADDED	171 A
2025 LED UPGRADE TOTAL BUILDING LOAD	1382 A
NEW LOAD REMOVED	10 A
NEW LOAD ADDED	12 A
NEW TOTAL BUILDING LOAD	1384 A

EXISTING PANEL LBM2

Panel Notes:
1. NEW LOAD ON EXISTING CIRCUIT BREAKER.

200 A MAIN CIRCUIT BREAKER — VOLTAGE 120 / 208 V
250 A BUS — PHASE 3 PH
WIRE 4 W

MFR : SIEMENS
MTG. : SURFACE

10000 AMPERE SHORT CIRCUIT RATING (FULLY RATED)

NOTE	DESCRIPTION	LTG	RECEPT	MOTORS	OTHER	GENERAL	TOTAL	BREAKER AMP / P	CCT	PH	CCT	BREAKER AMP / P	TOTAL	GENERAL	OTHER	MOTORS	RECEPT	LTG	DESCRIPTION	NOTE
	HP2.19			1,789			1789	25 /	1	A	2	20 / 1	1440						RECEPTACLES B130	
	/			1,789			1789	/ 2	3	B	4	20 / 1	1440						RECEPTACLES B130	
	RECEPT CORRIDOR		1,440				1440	20 / 1	5	C	6	20 / 1	1440						RECEPTACLES B130	
	RECEPTACLES B132		1,440				1440	20 / 1	7	A	8	20 / 1	1440						RECEPTACLES B137	
	RECEPTACLES B132		1,440				1440	20 / 1	9	B	10	20 / 1	1440						RECEPTACLES B137	
	RECEPTACLES B132		1,440				1440	20 / 1	11	C	12	20 / 1	1440						RECEPTACLES B137	
	RECEPTACLES B139		1,440				1440	20 / 1	13	A	14	20 / 1	1440						RECEPTACLES B140	
	RECEPTACLES B139		1,440				1440	20 / 1	15	B	16	20 / 1	1440						RECEPTACLES B140	
	RECEPTACLES B139		1,440				1440	20 / 1	17	C	18	20 / 1	1440						RECEPTACLES B140	
1	**RECEPTACLES B135**		**900**				900	20 / 1	19	A	20	20 / 1	1440						RECEPTACLES B131	
1	**RECEPTACLES B135**		**900**				900	20 / 1	21	B	22	20 / 1	1440						RECEPTACLES B131	
1	**RECEPTACLES B135**		**480**				480	20 / 1	23	C	24	20 / 1	1440						RECEPTACLES B131	
	RECEPTACLES B133		1,440				1440	20 / 1	25	A	26	20 / 1	1440						RECEPTACLES B119B	
	RECEPTACLES B136		1,440				1440	20 / 1	27	B	28	20 / 1	1440						RECEPTACLES B119	
	IRRIGATION CNTRL		600				600	20 / 1	29	C	30	20 / 1	1440						RECEPTACLES B119	
	WP RECEPT		180				180	20 / 1	31	A	32	20 / 1	1440						RECEPTACLES B122	
	ROOF RECEPT		360				360	20 / 1	33	B	34	20 / 1	1440						RECEPTBCLES B122	
	RECEPTACLES B125		1,440				1440	20 / 1	35	C	36	20 / 1	1200				1,200		LRC MOTOR SHADES	
	RECEPTACLES B123		1,440				1440	20 / 1	37	A	38	20 / 1	1200				1,200		LRC MOTOR SHADES	
	RECEPTACLES B123		1,440				1440	20 / 1	39	B	40	20 / 1	0						SPARE	
	RECEPTACLES B123		1,440				1440	20 / 1	41	C	42	20 / 1	0						SPARE	
	RECEPTACLES B124		1,440				1440	20 / 1	43	A	44	20 / 1	1440				1,440		RECEPTACLES B126	
	RECEPTACLES B124		1,440				1440	20 / 1	45	B	46	20 / 1	1440				1,440		RECEPTACLES B126	
	RECEPTACLES B124		1,440				1440	20 / 1	47	C	48	20 / 1	1440				1,440		RECEPTACLES B126	
	SPACE						0		49	A	50		0						SPACE	
	SPACE						0		51	B	52		0						SPACE	
	SPACE						0		53	C	54		0						SPACE	
	SPACE						0		55	A	56		0						SPACE	
	SPACE						0		57	B	58		0						SPACE	
	SPACE						0		59	C	60		0						SPACE	
	SPACE						0		61	A	62		0						SPACE	
	SPACE						0		63	B	64		0						SPACE	
	SPACE						0		65	C	66		0						SPACE	
	SPACE						0		67	A	68		0						SPACE	
	SPACE						0		69	B	70		0						SPACE	
	SPACE						0		71	C	72		0						SPACE	
	SPACE						0		73	A	74		0						SPACE	
	SPACE						0		75	B	76		0						SPACE	
	SPACE						0		77	C	78		0						SPACE	
	SPACE						0		79	A	80		0						SPACE	
	SPACE						0		81	B	82		0						SPACE	
	SPACE						0		83	C	84		0						SPACE	

PHASE LOADING SUMMARY — PANEL LOADING SUMMARY

LOAD TYPE (VA)	PH A	PH B	PH C
LIGHTING	0.0	0.0	0.0
RECEPTACLES	18,360.0	18,540.0	18,360.0
MOTORS	2,989.0	1,789.0	1,200.0
OTHER	0.0	0.0	0.0
GENERAL	0.0	0.0	0.0
TOTAL (VA)	21,349.0	20,329.0	19,560.0
NEC CALCULATED			
PHASE AMPACITY	146.5	137.3	130.4
	#REF!		
PHASE BALANCE	A-B	B-C	C-A
	5%	4%	9%

LOAD TYPE	CONNECTED LOAD KVA		NEC CALCULATED DEMAND LOAD		POWER FACTOR	DEMAND LOAD KW	
LIGHTING	0.0	KVA	x 125% =	0.0 KVA	x 95% =	0.0 KW	
RECEPTACLES							
FIRST 10 KVA	10.0	KVA	x 100% =	10.0 KVA	x 100% =	10.0 KW	
REMAINDER	45.3	KVA	x 50% =	22.6 KVA	x 100% =	22.6 KW	
MOTORS							
LARGEST	3.6	KVA	x 125% =	4.5 KVA	x 90% =	4.0 KW	
REMAINDER	2.4	KVA	x 100% =	2.4 KVA	x 90% =	2.2 KW	
OTHER	0.0	KVA	x 125% =	0.0 KVA	x 100% =	0.0 KW	
GENERAL	0.0	KVA	x 100% =	0.0 KVA	x 100% =	0.0 KW	
TOTAL	61.2	KVA		39.5 KVA		38.8 KW	

PANEL CONNECTED PF= 98%
CONNECTED AMPACITY = 170.0
NEC DEMAND AMPACITY = 109.6

GENERAL NOTES:
1. PROVIDE NEW UPDATED PANEL DIRECTORIES FOR PANELS THAT ARE INCLUDED IN THIS PROJECT.
2. PROVIDE TYPED DESCRIPTIONS OF NEW CIRCUITS BEING INSTALLED. INDICATE NEW SPARES IN PENCIL.

EXISTING PANEL LBL2

Panel Notes:
1. NEW LOAD ON EXISTING CIRCUIT BREAKER.
2. PROVIDE CIRCUIT BREAKER IN SPACE TO MATCH EXISTING.

200 A MAIN CIRCUIT BREAKER — VOLTAGE 120 / 208 V
250 A BUS — PHASE 3 PH
WIRE 4 W

MFR : SIEMENS
MTG. : SURFACE

10000 AMPERE SHORT CIRCUIT RATING (FULLY RATED)

NOTE	DESCRIPTION	LTG	RECEPT	MOTORS	OTHER	GENERAL	TOTAL	BREAKER AMP / P	CCT	PH	CCT	BREAKER AMP / P	TOTAL	GENERAL	OTHER	MOTORS	RECEPT	LTG	DESCRIPTION	NOTE
	HP1.07			1,789			1789	25 /	1	A	2	20 / 1	2400		2,400				TELECOM B011A	
	/			1,789			1789	/ 2	3	B	4	20 / 1	2400		2,400				TELECOM B011A	
	RECEPTACLES B011		180				180	20 / 1	5	C	6	20 / 1	2400		2,400				TELECOM B011A	
	RECEPTACLES B013		1,440				1440	20 / 1	7	A	8	20 / 1	1440				1,440		RECEPTACLES B015	
1	RECEPTACLES B013		**900**				900	20 / 1	9	B	10	20 / 1	900				**900**		RECEPTACLES B015	1
	RECEPTACLES B013		720				720	20 / 1	11	C	12	20 / 1	720				720		RECEPTACLES B015	
	RECEPTACLES B021		1,440				1440	20 / 1	13	A	14	20 / 1	1440				1,440		RECEPT CORRIDOR	
1	RECEPTACLES B021		**900**				900	20 / 1	15	B	16	20 / 1	1440				1,440		RECEPTACLES B022	
	RECEPTACLES B021		720				720	20 / 1	17	C	18	20 / 1	1440				1,440		RECEPTACLES B022	
	RECEPTACLES B024		1,440				1440	20 / 1	19	A	20	20 / 1	1440				1,440		RECEPTACLES B022	
	RECEPTACLES B024		1,440				1440	20 / 1	21	B	22	20 / 1	1440				1,440		RECEPTACLES B025	
	RECEPTACLES B024		1,440				1440	20 / 1	23	C	24	20 / 1	1440				1,440		RECEPTACLES B025	
	RECEPTACLES B014		1,440				1440	20 / 1	25	A	26	20 / 1	1440				1,440		RECEPTACLES B025	
	RECEPTACLES B014		1,440				1440	20 / 1	27	B	28	20 / 1	900				**900**		**RECEPTACLES B020**	1
	RECEPTACLES B014		1,440				1440	20 / 1	29	C	30	20 / 1	900				**900**		**RECEPTACLES B020**	1
	IDF B11A UPS				2,500		2500	30 /	31	A	32	20 / 1	480				**480**		**RECEPTACLES B020**	1
	/				2,500		2500	/ 2	33	B	34	20 /	840			840			FCU-1	
	SPARE						0	20 / 1	35	C	36	/ 2	840			840			/	
	RECEPTACLES B018		1,440				1440	20 / 1	37	A	38	20 / 1	1440				1,440		RECEPTACLES B011A	
	CORRIDOR B012		1,440				1440	20 / 1	39	B	40	20 / 1	1440				1,440		RECEPTACLES B007	
	RECEPTACLES B026		1,440				1440	20 / 1	41	C	42	20 / 1	1440				1,440		RECEPTACLES B007	
	SPARE						0	20 / 1	43	A	44	20 / 1	1440				1,440		RECEPTACLES B007	
	RECEPTACLES B007		1440				1440	20 / 1	45	B	46	20 / 1	1440				1,440		RECEPTACLES B007	
	RECEPTACLES B007		1440				1440	20 / 1	47	C	48	20 / 1	1440				1,440		RECEPTACLES B007	
	RECEPTACLES B006		1440				1440	20 / 1	49	A	50	20 / 1	1440				1,440		RECEPTACLES B007	
	RECEPTACLES B010		1,440				1440	20 / 1	51	B	52	30 /	0						SPARE	
	STEAM RM		1200				1200	20 / 1	53	C	54	/ 2	0						/	
	HAND DRYER				1200		1200	20 / 1	55	A	56	20 / 1	0						SPARE	
	STEAM RM		1200				1200	20 / 1	57	B	58	20 / 1	0						SPARE	
	SPACE						0	20 / 1	59	C	60	20 / 1	0						SPARE	
1	**RECEPTACLES B030**		**900**				900	20 / 1	61	A	62	20 / 1	0						SPACE	
1	**RECEPTACLES B030**		**900**				900	20 / 1	63	B	64	20 / 1	0						SPACE	
1	**RECEPTACLES B030**		**480**				480	20 / 1	65	C	66	20 / 1	0						SPACE	
	SPACE						0	20 / 1	67	A	68	20 / 1	0						SPACE	
	SPACE						0	20 / 1	69	B	70	20 / 1	0						SPACE	
	SPACE						0	20 / 1	71	C	72	20 / 1	0						SPACE	
	SPACE						0	20 / 1	73	A	74	20 / 1	0						SPACE	
	SPACE						0	20 / 1	75	B	76	20 / 1	0						SPACE	
	SPACE						0	20 / 1	77	C	78	20 / 1	0						SPACE	
	SPACE						0	20 / 1	79	A	80	20 / 1	0						SPACE	
	SPACE						0	20 / 1	81	B	82	20 / 1	0						SPACE	
	SPACE						0	20 / 1	83	C	84	20 / 1	0						SPACE	

PHASE LOADING SUMMARY — PANEL LOADING SUMMARY

LOAD TYPE (VA)	PH A	PH B	PH C
LIGHTING	0.0	0.0	0.0
RECEPTACLES	20,100.0	18,660.0	16,440.0
MOTORS	1,789.0	2,629.0	840.0
OTHER	6,100.0	4,900.0	2,400.0
GENERAL	0.0	0.0	0.0
TOTAL (VA)	27,989.0	26,189.0	19,680.0
NEC CALCULATED			
PHASE AMPACITY	207.2	195.7	143.6
	#REF!		
PHASE BALANCE	A-B	B-C	C-A
	7%	33%	42%

LOAD TYPE	CONNECTED LOAD KVA		NEC CALCULATED DEMAND LOAD		POWER FACTOR	DEMAND LOAD KW	
LIGHTING	0.0	KVA	x 125% =	0.0 KVA	x 95% =	0.0 KW	
RECEPTACLES							
FIRST 10 KVA	10.0	KVA	x 100% =	10.0 KVA	x 100% =	10.0 KW	
REMAINDER	45.2	KVA	x 50% =	22.6 KVA	x 100% =	22.6 KW	
MOTORS							
LARGEST	3.6	KVA	x 125% =	4.5 KVA	x 90% =	4.0 KW	
REMAINDER	1.7	KVA	x 100% =	1.7 KVA	x 90% =	1.5 KW	
OTHER	13.4	KVA	x 125% =	16.8 KVA	x 100% =	16.8 KW	
GENERAL	0.0	KVA	x 100% =	0.0 KVA	x 100% =	0.0 KW	
TOTAL	73.9	KVA		55.5 KVA		54.9 KW	

PANEL CONNECTED PF= 99%
CONNECTED AMPACITY = 205.0
NEC DEMAND AMPACITY = 154.1

GENERAL NOTES:
1. PROVIDE NEW UPDATED PANEL DIRECTORIES FOR PANELS THAT ARE INCLUDED IN THIS PROJECT.
2. PROVIDE TYPED DESCRIPTIONS OF NEW CIRCUITS BEING INSTALLED. INDICATE NEW SPARES IN PENCIL.

DAO ARCHITECTURE
7230 Meade St.
Westminster, CO 80030
Phone: 720.273.0431
Email: dan@daoarch.com
Web: www.daoarch.com

CATOR | RUMA & ASSOCIATES, CO.
896 Tabor Street, Lakewood, CO 80401
(303) 232-6200 ▪ www.catorruma.com

Rev. #	Description	Rev. Date
	Revision Schedule	

Westminster Public Schools

Hodgkins Leadership Academy Classroom Conversion Project

3475 W 67th Ave,
Denver, CO 80221


DAO No.: 2021-033

September 25, 2026

ELECTRICAL PANEL SCHEDULES

E3.0

P:\WPS\2026-0530-Hodgkins Leadership Academy 2026 Bond Project\Cad
9/22/2026 4:11:29 PM

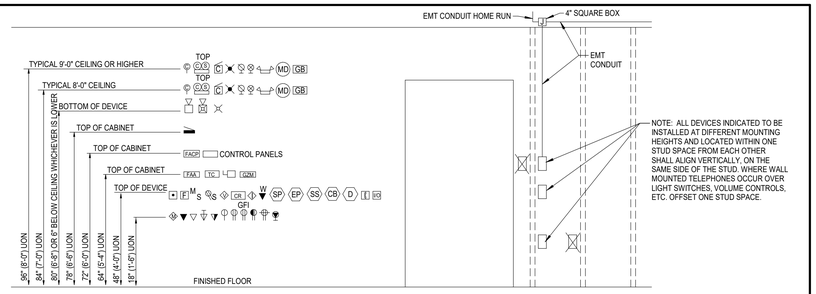


TYPICAL DEVICE MOUNTING HEIGHTS

NO SCALE

NOTES:

1. HEIGHTS SHOWN ARE TYPICAL TO CENTERLINE OF BOX UNLESS NOTED OTHERWISE.
2. WHERE EVER DEVICES ARE INDICATED TO BE ABOVE DOORS, DEVICE SHALL BE CENTERED BETWEEN TOP OF DOOR TRIM AND CEILING LINE.
3. MOUNTING HEIGHTS SHOWN ON ARCHITECTURAL ELEVATIONS SHALL GOVERN OVER THOSE SHOWN ABOVE.
4. DEVICE MOUNTING HEIGHTS SHALL BE PER MOST CURRENT VERSION OF GOVERNING CODES AND STANDARDS NEC, IBC, NFPA, ADA, ETC. WHERE DESCREPANCIES BECOME EVIDENT CONSULT THE ARCHITECT AND ENGINEER OF RECORD.

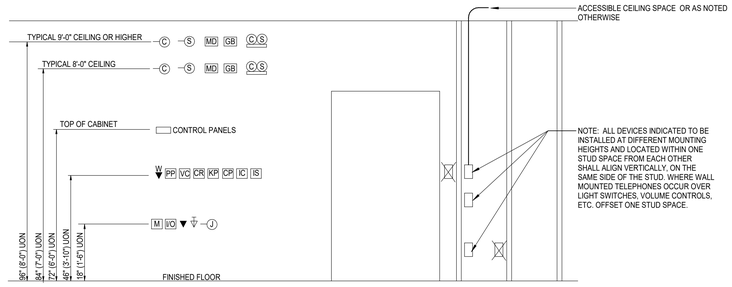


TYPICAL LOW VOLTAGE DEVICE MOUNTING HEIGHTS

NO SCALE

NOTES:

1. HEIGHTS SHOWN ARE TYPICAL TO CENTERLINE OF BOX UNLESS OTHERWISE NOTED.
2. WHERE EVER DEVICES ARE INDICATED TO BE ABOVE DOORS, DEVICE SHALL BE CENTERED BETWEEN TOP OF DOOR TRIM AND CEILING LINE.
3. MOUNTING HEIGHTS SHOWN ON ARCHITECTURAL ELEVATIONS SHALL GOVERN OVER THOSE SHOWN ABOVE. VERIFY MOUNTING HEIGHTS SHOWN ON ARCHITECTURAL ELEVATIONS. DEVICES AND COVER PLATES SHALL NOT COVER/OVERLAP EDGES OF WAINSCOTING, TILE OR OTHER SPECIALTY WALL FINISHES.
4. DEVICE MOUNTING HEIGHTS SHALL BE PER MOST CURRENT VERSION OF GOVERNING CODE AND STANDARDS NEC, IBC, NFPA, ADA, ETC. WHERE DISCREPANCIES BECOME EVIDENT, CONSULT THE ARCHITECT AND ENGINEER OF RECORD.
5. WHERE DEVICES ARE INSTALLED ABOVE COUNTER, THE DEVICES SHALL BE INSTALLED AT 46" MAXIMUM (COUNTERS/SHELVES 0-20 INCHES WIDE) AND 44" MAXIMUM (COUNTER/SHELVES 20-25 INCHES WIDE) ABOVE FINISHED FLOOR TO DEVICE CENTER.
6. LOW VOLTAGE DEVICES SHALL NOT BE INSTALLED BELOW 15" AFF PER ADA STANDARDS.

TTM-003

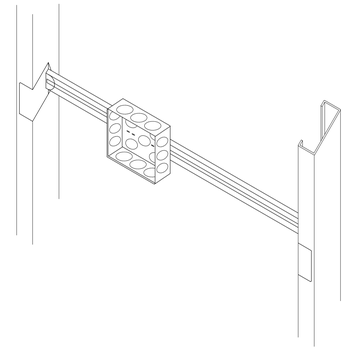

OUTLET BOX SUPPORT DETAIL

NO SCALE

DAO ARCHITECTURE
7230 Meade St.
Westminster, CO 80030
Phone: 720.273.0431
Email: dan@daoarch.com
Web: www.daoarch.com

CATOR | RUMA & ASSOCIATES, CO.
896 Tabor Street, Lakewood, CO 80401
(303) 232-6200 ▪ www.catorruma.com

Rev. #	Description	Rev. Date
Revision Schedule		

Westminster Public Schools

Hodgkins Leadership Academy Classroom Conversion Project

3475 W 67th Ave,
Denver, CO 80221

DAO No.: 2021-033

September 25, 2026

ELECTRICAL DETAILS

E5.0

P:\WPS\2025-0539 Hodgkins Leadership Academy_2026 Bond Project\Cad
9/22/2026 4:11:29 PM